



Fire - resistance time: 120 minutes

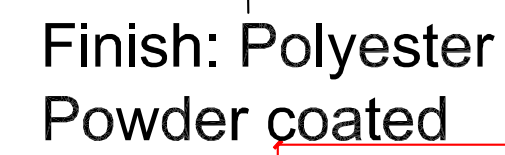

Outside elevation


Inside elevation

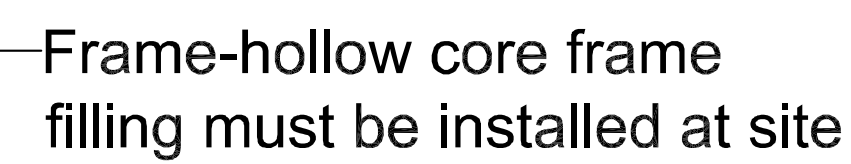

- Back plate 1.6mm

—Anchor 10*120mm

—Fire sealant
≥5mm

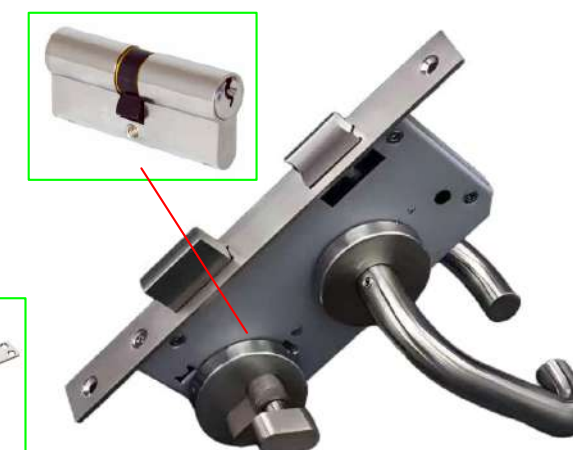

euro profile, cylinder with both side key+ solnoid lock (no thumbturn)



Door closer


Door Tag	Handling	Color	Floor	Qty.
AD1	LHRA + RHR	9010	GF	1
AD1	LHRA + RHR	9010	GF	1



Project name


By		Drawing title	
Design		Size	
Check		Qty	2
Review		Opening direction	
Approval		Date	2026.05.18
		Page No	1
Total Page	34	Diagram number	

Fire - resistance time: 120 minutes

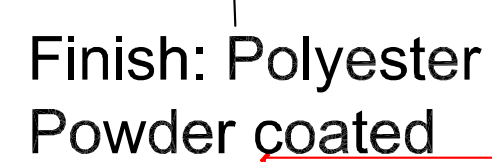

Outside elevation


Inside elevation

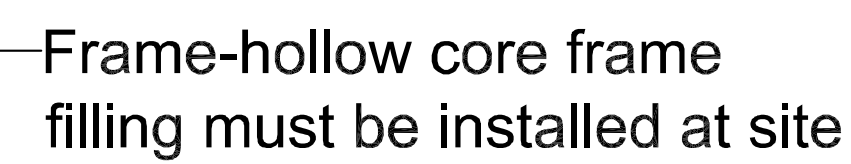

- Back plate 1.6mm

—Anchor 10*120mm

—Fire sealant
≥5mm

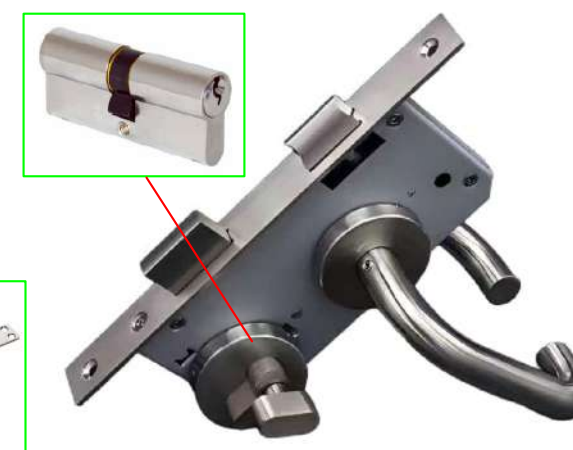

euro profile, cylinder with both side key+ solnoid lock (no thumbturn)



Door closer

Shanghai Xunzhong Industry Co., Ltd

Project name

By		Drawing title	
Design		Size	
Check		Qty	5
Review		Opening direction	
Approval		Date	2026.05.18
		Page No	2
Total Page	34	Diagram number	

FD1

Fire - resistance time: 120 minutes



sealing trip



Hinge



Flush bolt



Door coordinator



Auto bottom seal

Surface
Door Closer
with std arm

Door frame width 1988

Door leaf width 953

Door leaf width 953

2 Ball
Bearing
Hinge

Flush
bolt

Door Coordinator

Fireproof glass:
6mm thick

Handle lock
Deabolt lock

Fire sealant
≥5mm

Structure opening height 2800

Door leaf height 2750

Door frame height 2794

Undercut=6 mm

Finish: Polyester
Powder coated

Outside elevation

Inside elevation

Structure opening width 2000


Frame-hollow core frame
filling must be installed at site

Infill: Honeycomb

Back plate 1.6mm

Anchor
10*120mm

Fire sealant
≥5mm

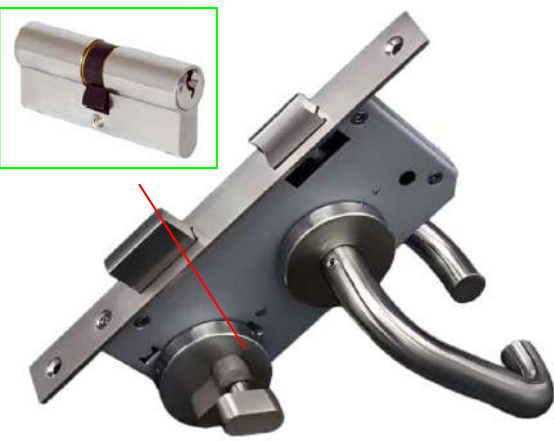

Door closer

euro profile, cylinder with both side key+
solnoid lock (no thumbturn)

Hardware

Name	Description	Qty	Remarks
Lock type	solenoid lock	1	4 pcs lever handle
Hinge	4.5*4*3	12	
Door closer	184	2	
Door stop			
Flush bolt		2	
Glass	150*400mm	2	
Auto Bottom seal		2	
Door coordinator		1	
Smoke seal		1	
Door frame	1.6mm Galvanized steel sheet		
Door leaf	1.2mm Galvanized steel sheet		
Threshold			
Filling	Honeycomb		
Colour			

LHA=	RHA=
LHRA =	RHRA =24



Shanghai Xunzhong Industry Co., Ltd

Project name


By		Drawing title	
Design		Size	
Check		Qty	24
Review		Opening direction	
Approval		Date	2026.05.18
		Page No	3
Total Page	34	Diagram number	

Fire - resistance time: 120 minutes



Door coordinator

Auto bottom sea

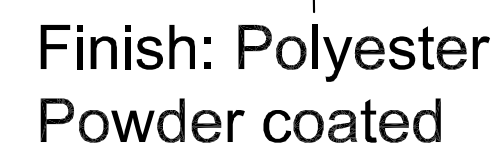

Inside elevation



Door closer



Project name

By		Drawing title	
Design		Size	
Check		Qty	14
Review		Opening direction	
Approval		Date	2026.05.18
		Page No	4
Total Page	34	Diagram number	

FD3

Fire - resistance time: 120 minutes



sealing trip



Hinge




Flush bolt



Door coordinator




Auto bottom seal

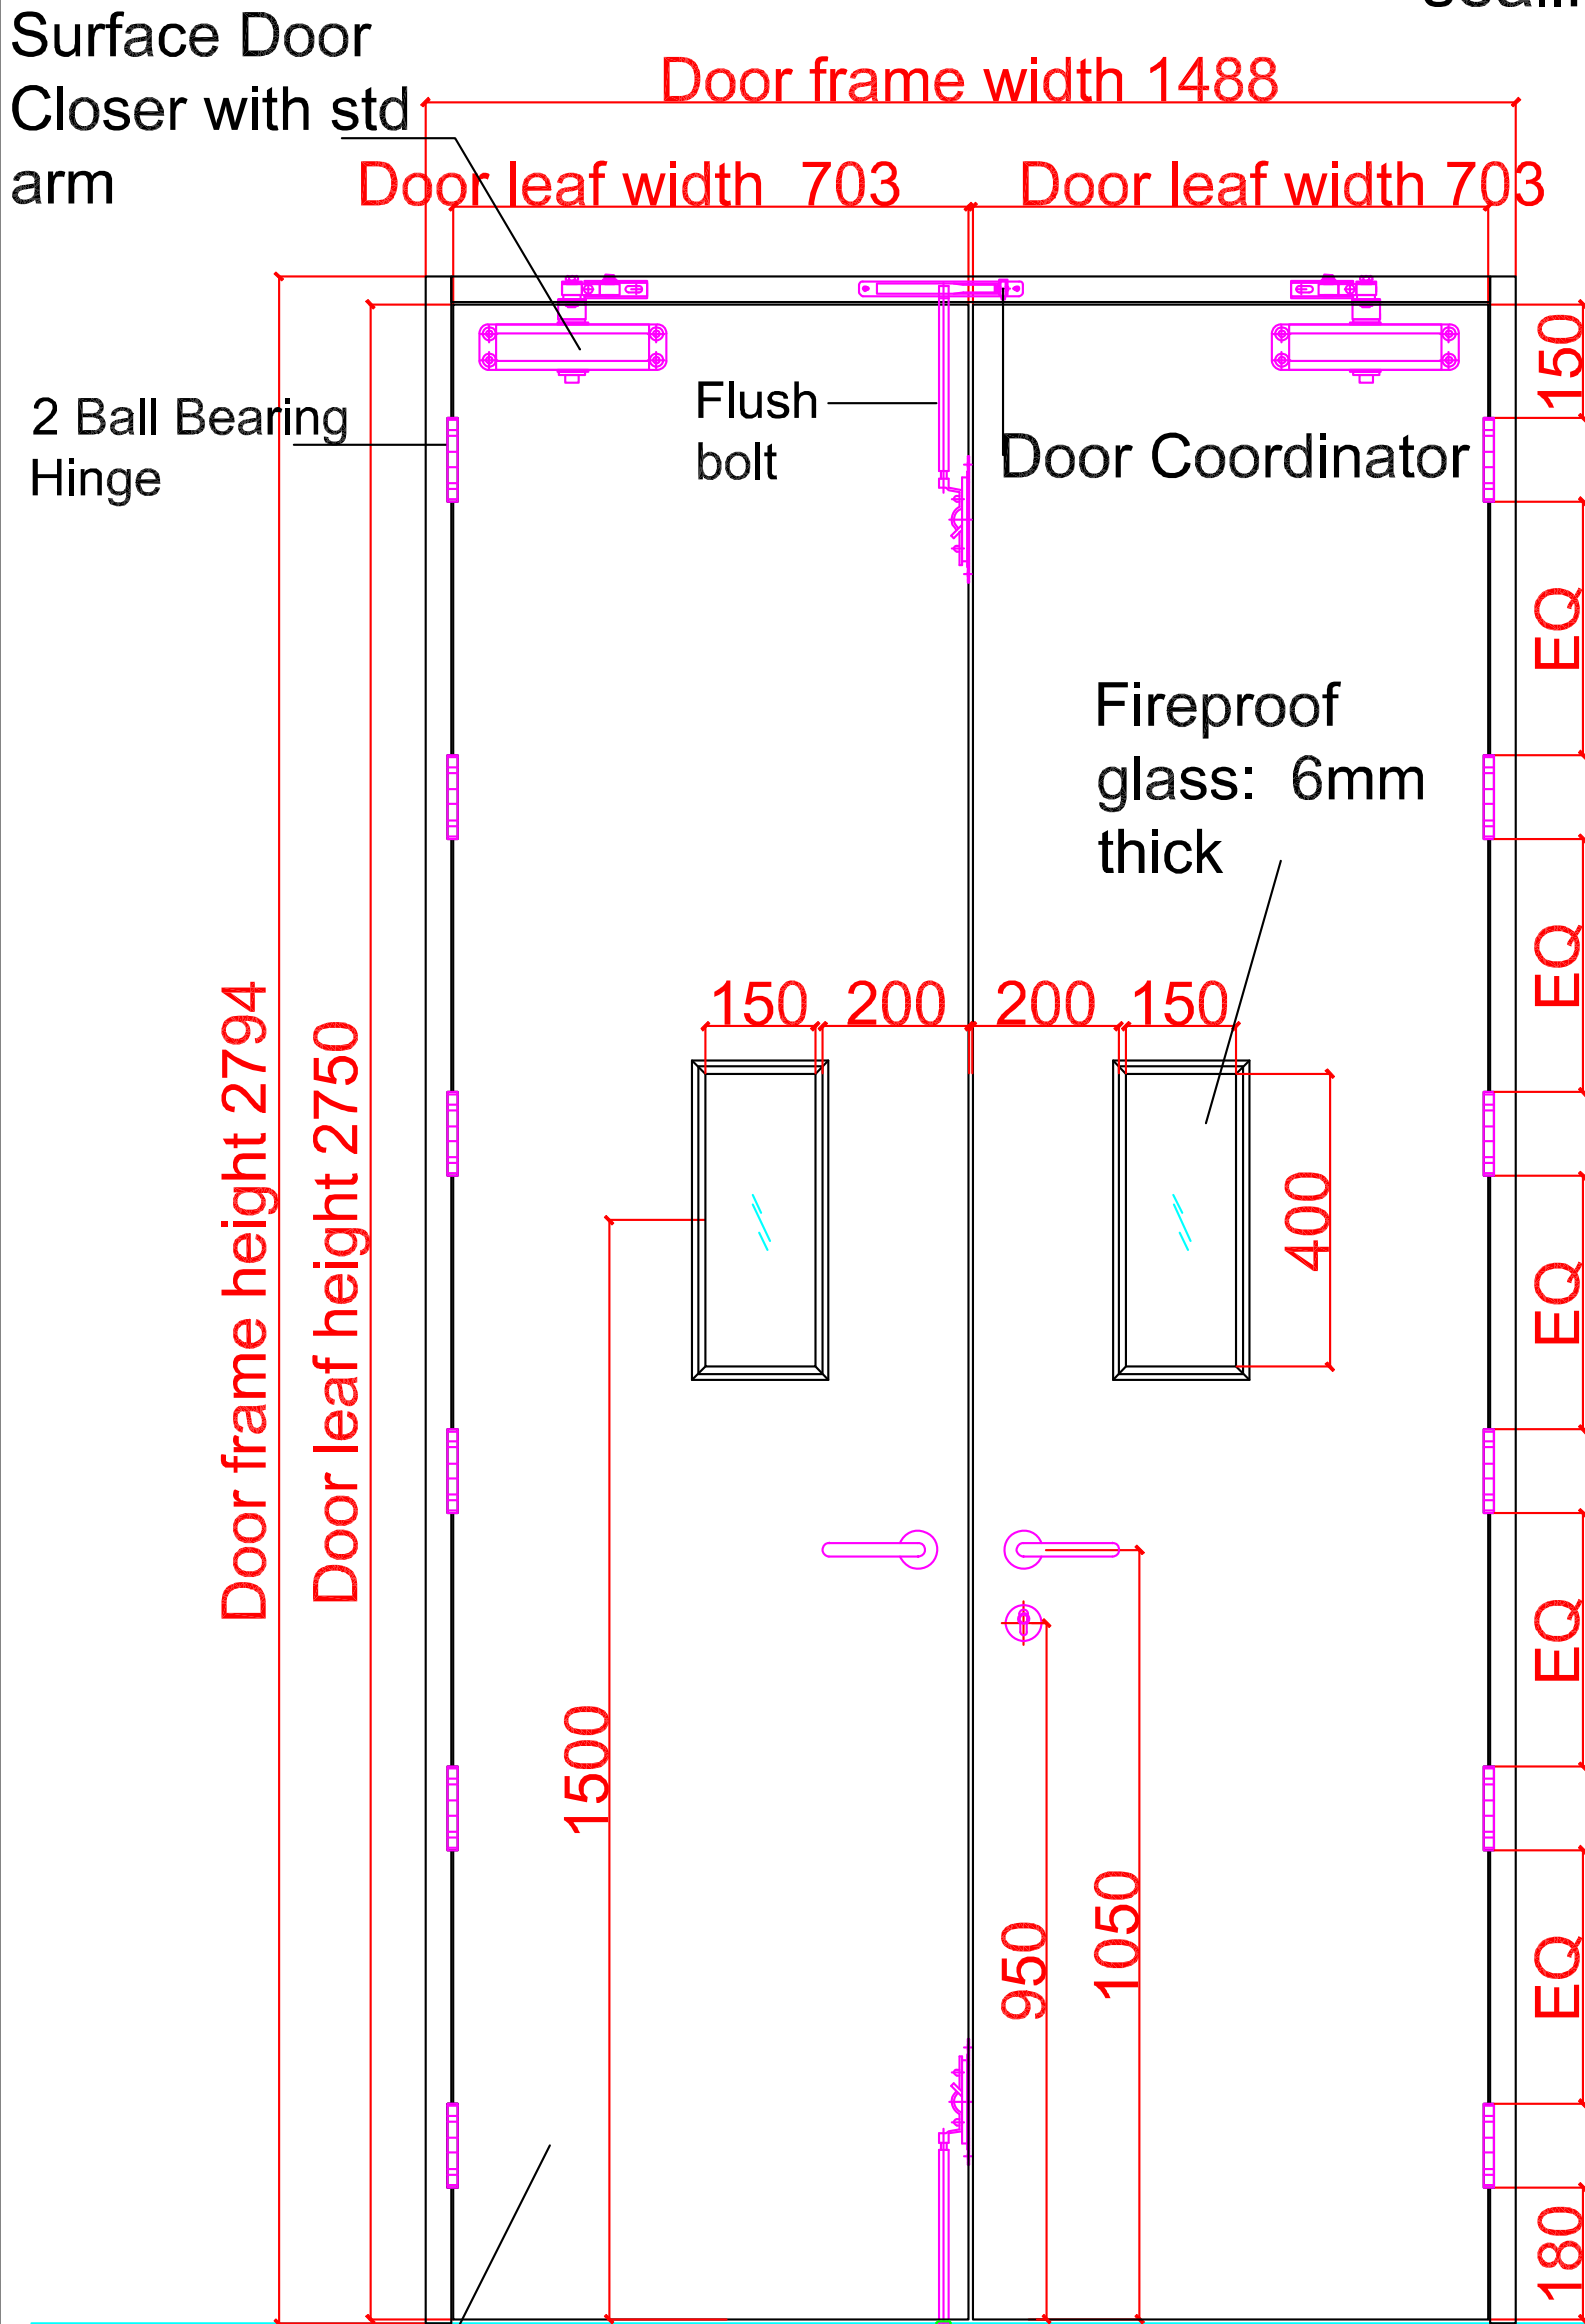


Finish: Polyester Powder coated


Outside elevation

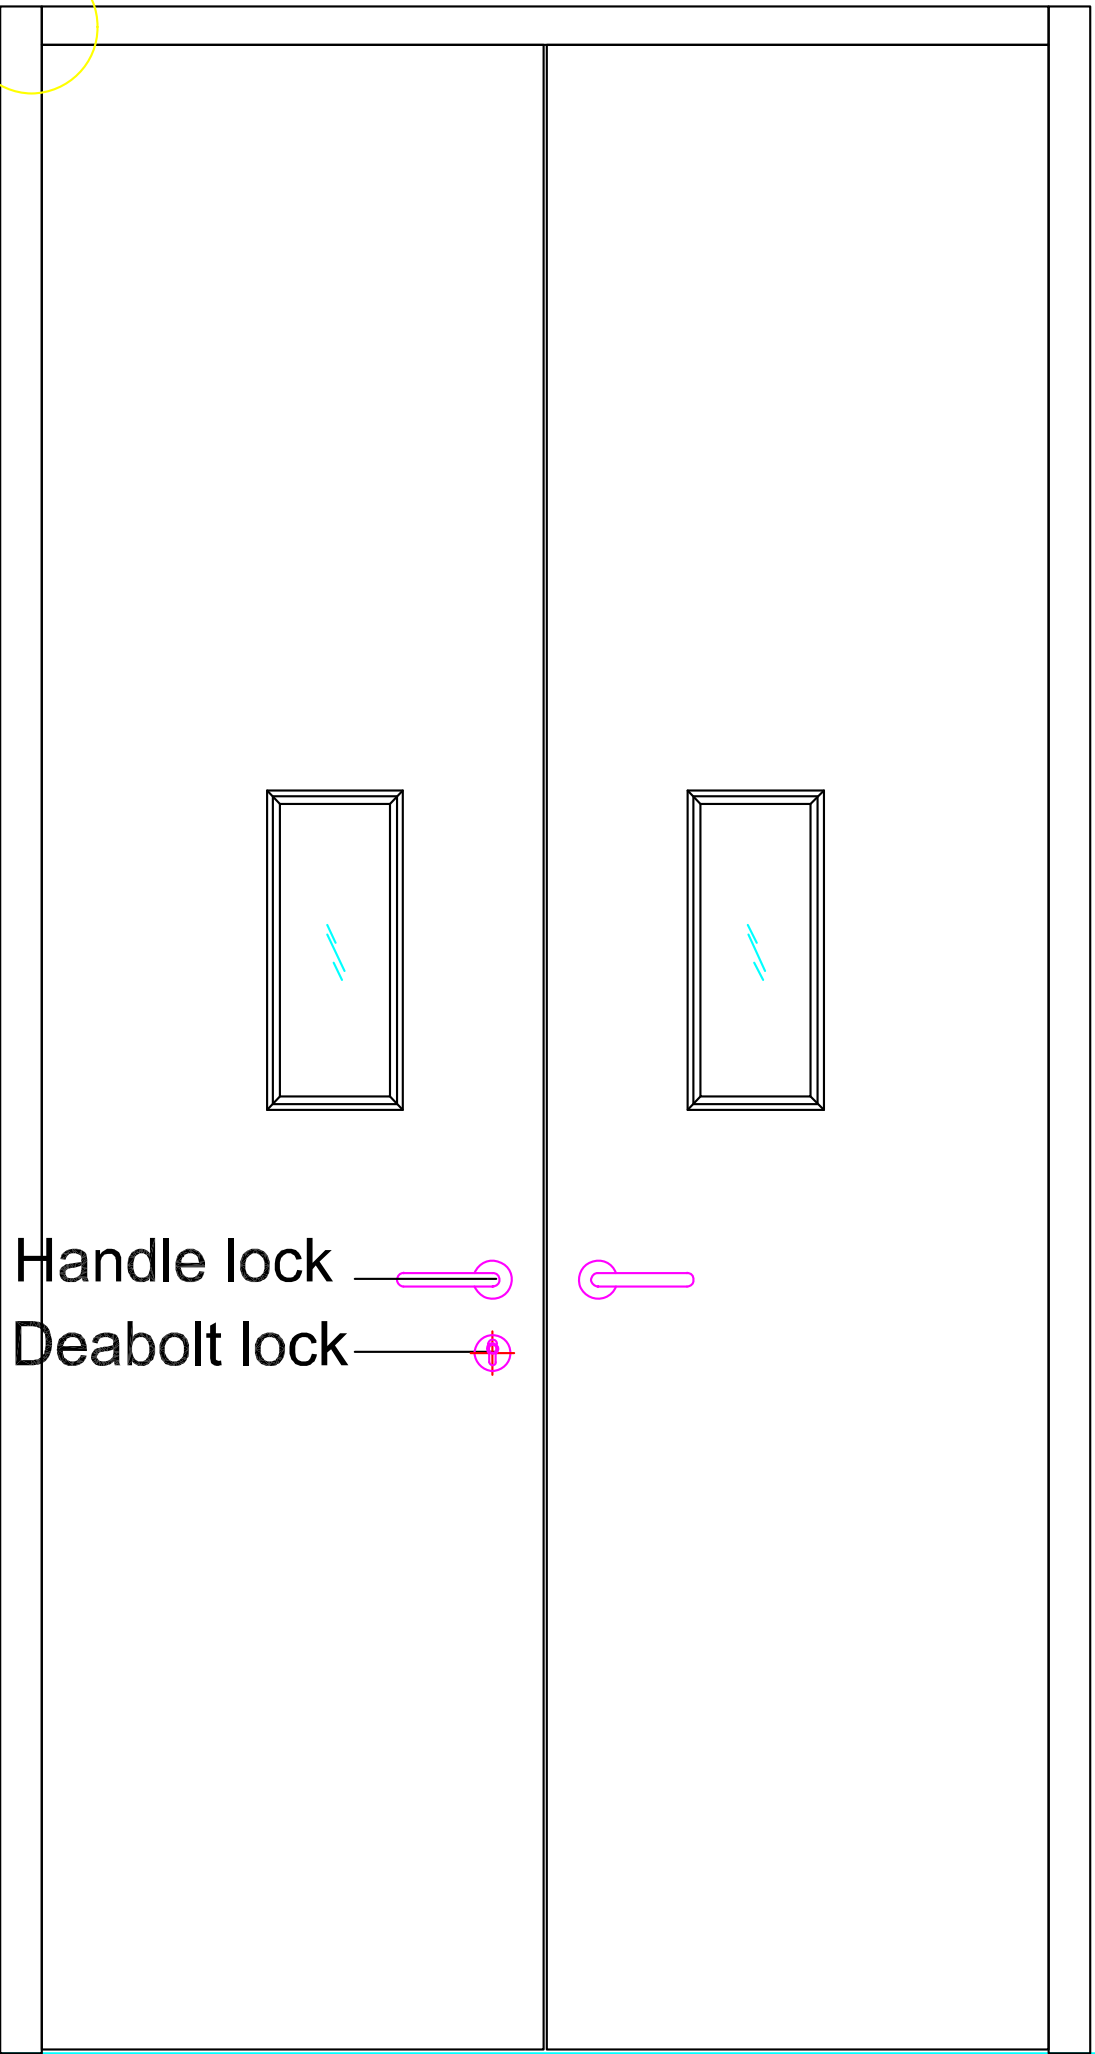

Inside elevation

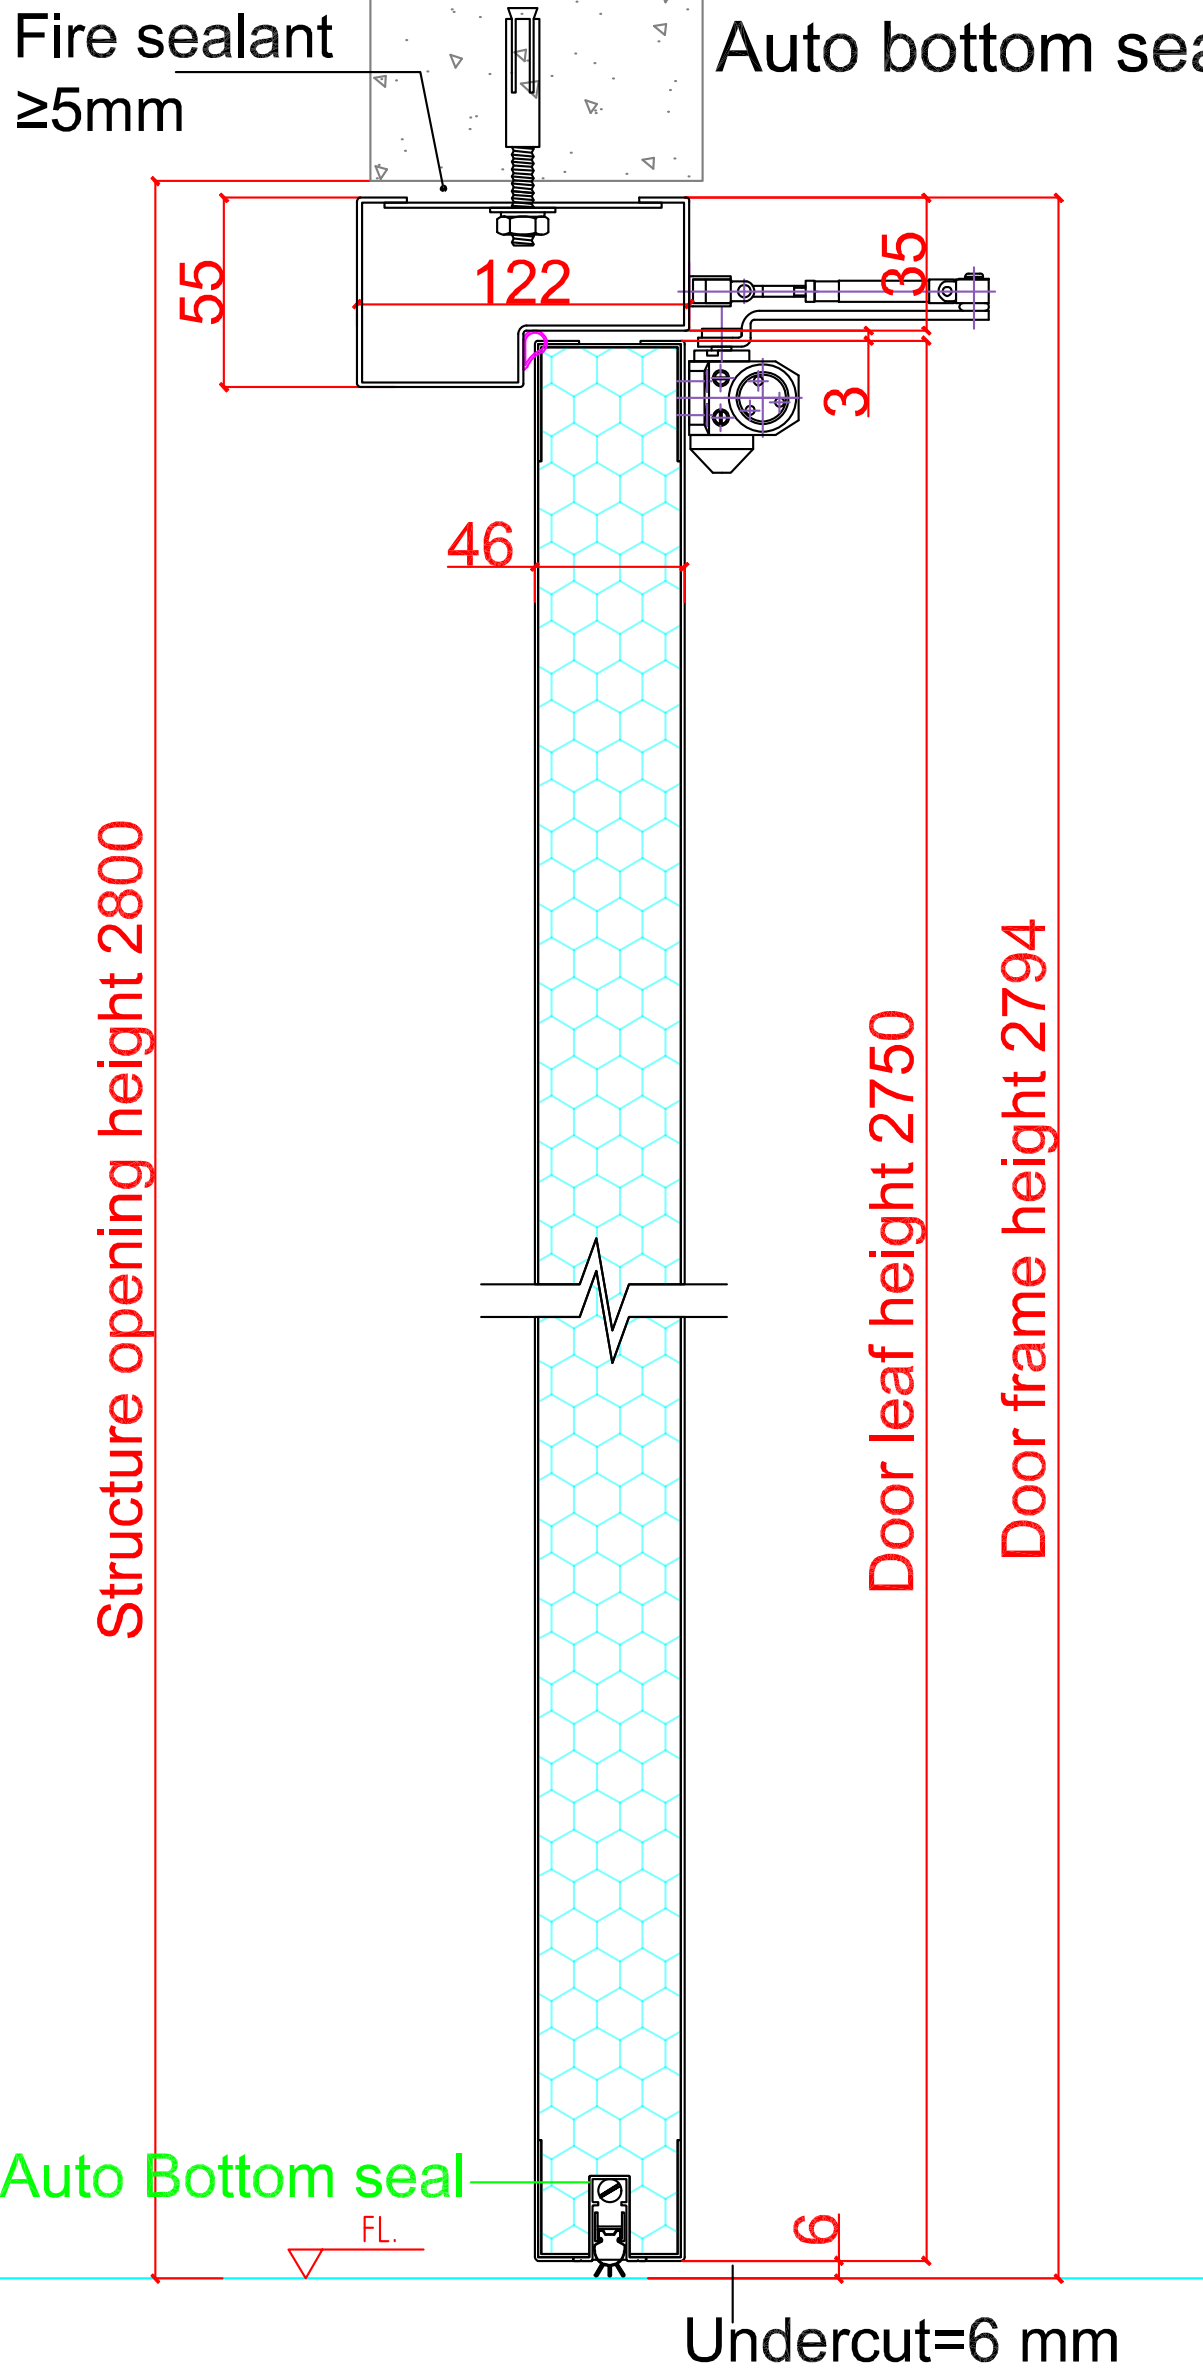


Undercut=6 mm

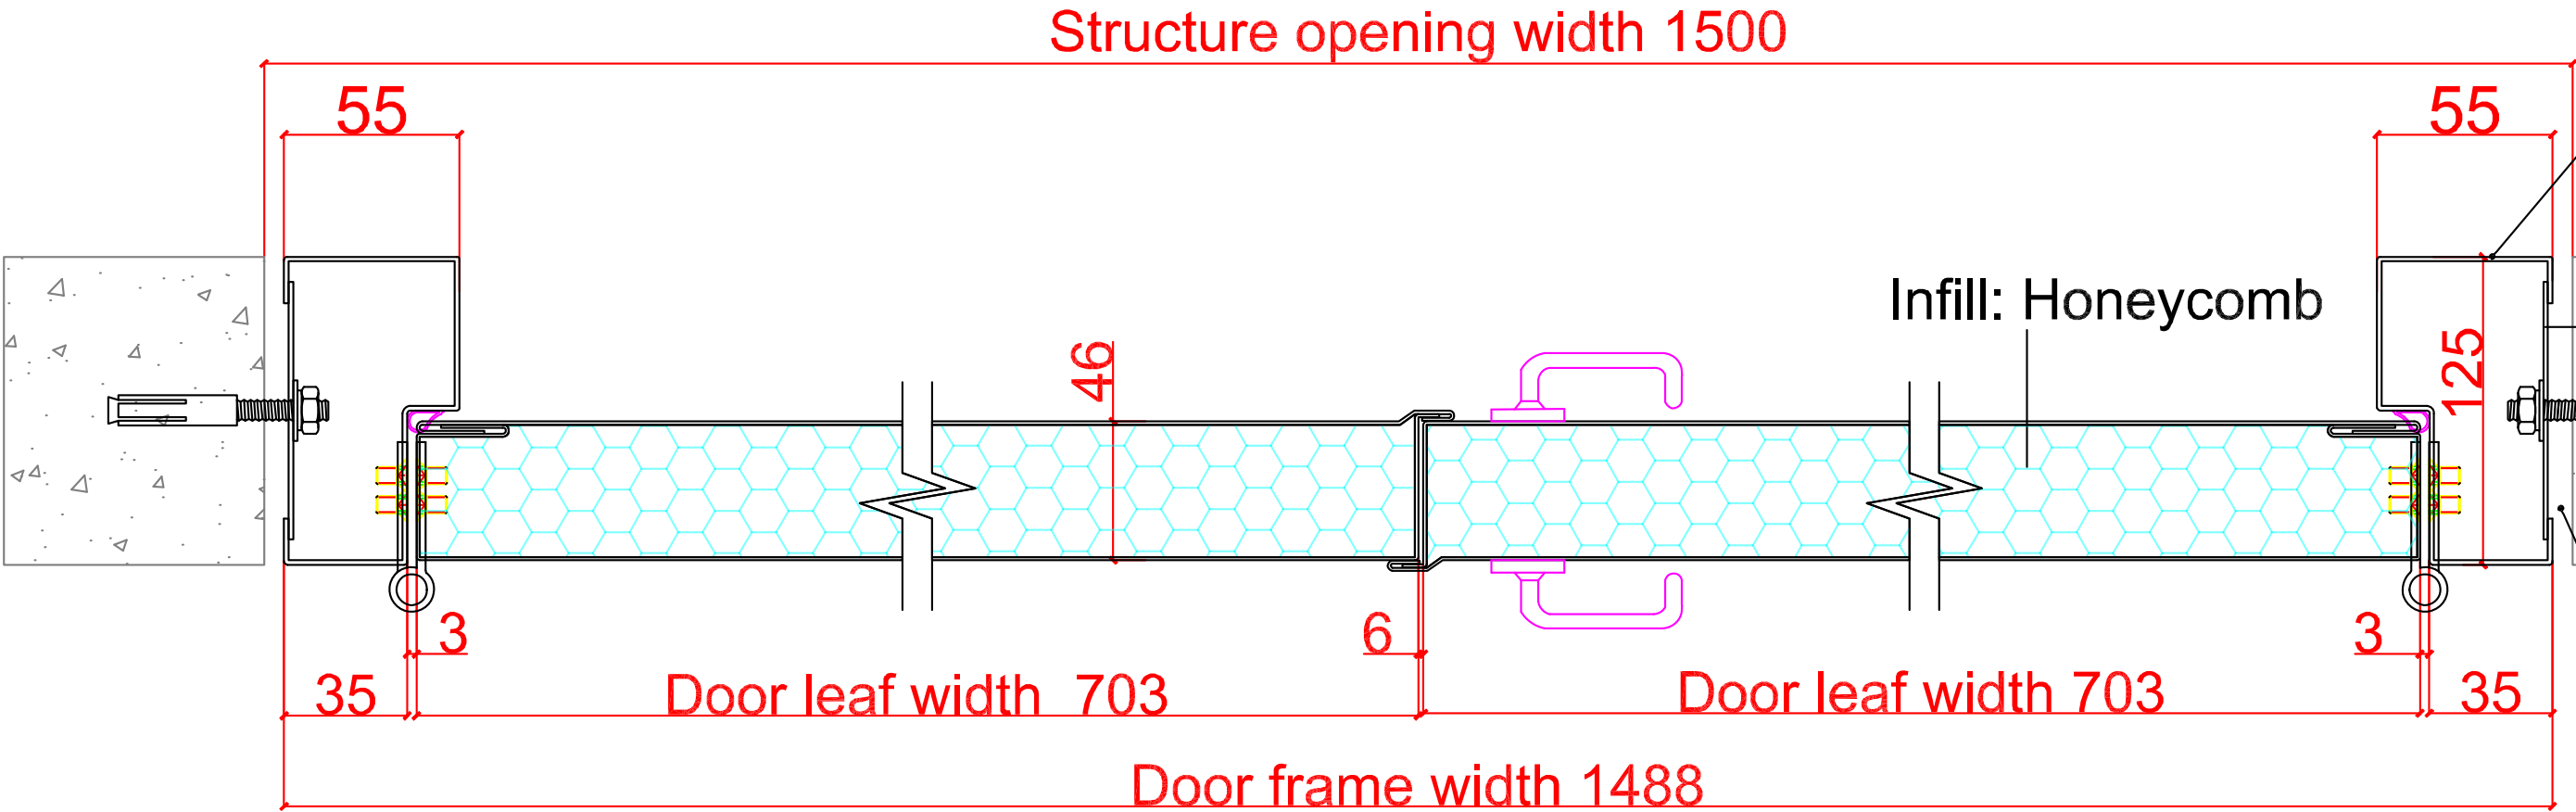

Frame-hollow core frame filling must be installed at site

Back plate 1.6mm
Anchor 10*120mm


Fire sealant ≥5mm

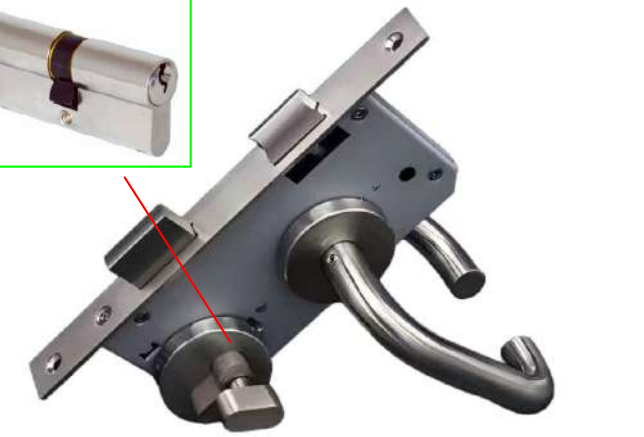

Door closer

Hardware

Name	Description	Qty	Remarks
Lock type	solenoid lock	1	4 pcs lever handle
Hinge	4.5*4*3	12	
Door closer	184	2	
Door stop			
Flush bolt		2	
Glass	150*400mm	2	
Auto Bottom seal		2	
Door coordinator		1	
Smoke seal		1	
Door frame	1.6mm Galvanized steel sheet		
Door leaf	1.2mm Galvanized steel sheet		
Threshold			
Filling	Honeycomb		
Colour			

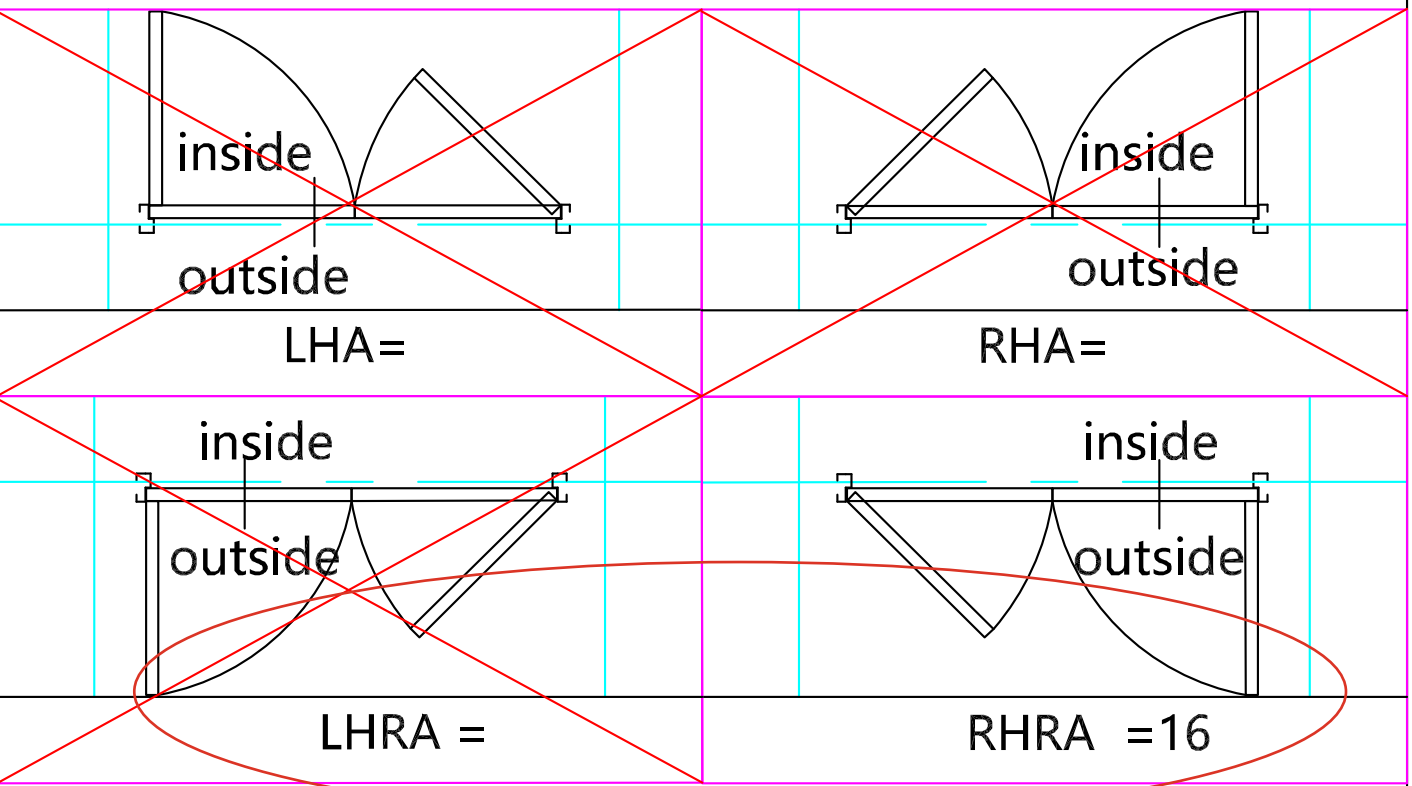

FD3 - LHRA + RHRA = 16




Shanghai Xunzhong Industry Co., Ltd

Project name


By		Drawing title	
Design		Size	
Check		Qty	16
Review		Opening direction	
Approval		Date	2026.05.18
		Page No	5
Total Page	34	Diagram number	

FD4

Fire - resistance time: 120 minutes

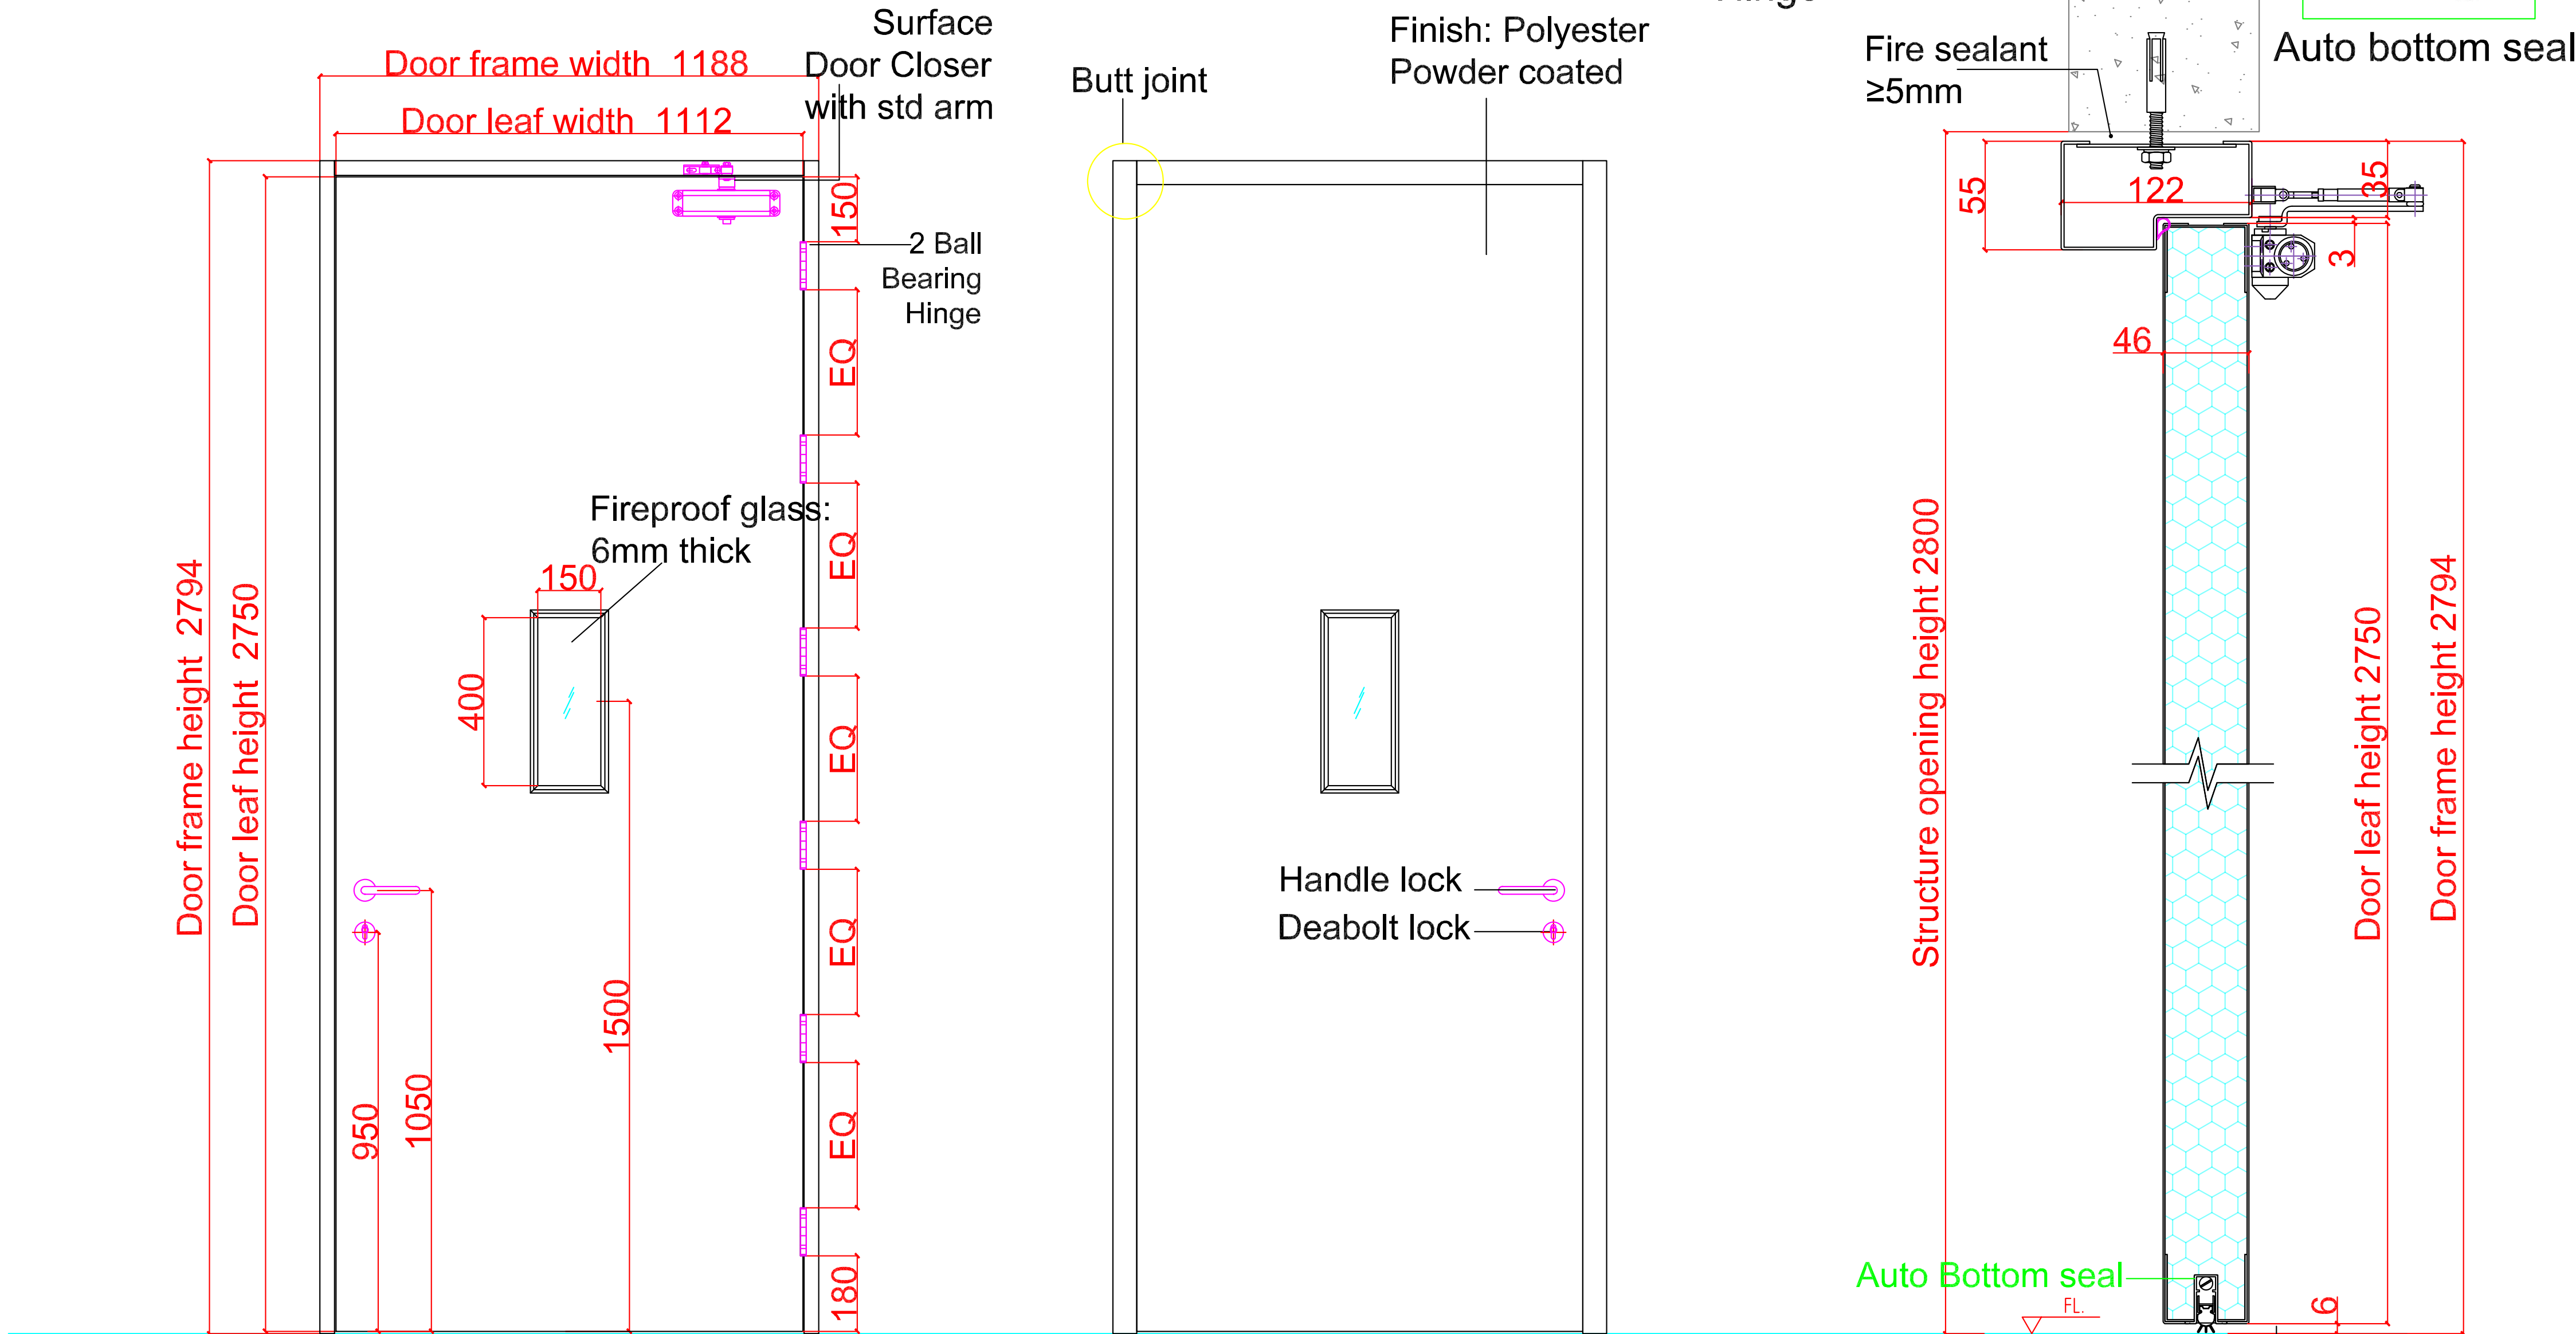

Hardware			
Name	Description	Qty	Remarks
Lock type	solenoid lock	1	4 pcs lever handle
Hinge	4.5*4*3	6	
Door closer	184	1	
Door stop			
Glass	150*400mm	1	
Auto Bottom seal		1	
Smoke seal		1	
Door frame	1.6mm Galvanized steel sheet		
Door leaf	1.2mm Galvanized steel sheet		
Threshold			
Filling	Honeycomb		
Colour			

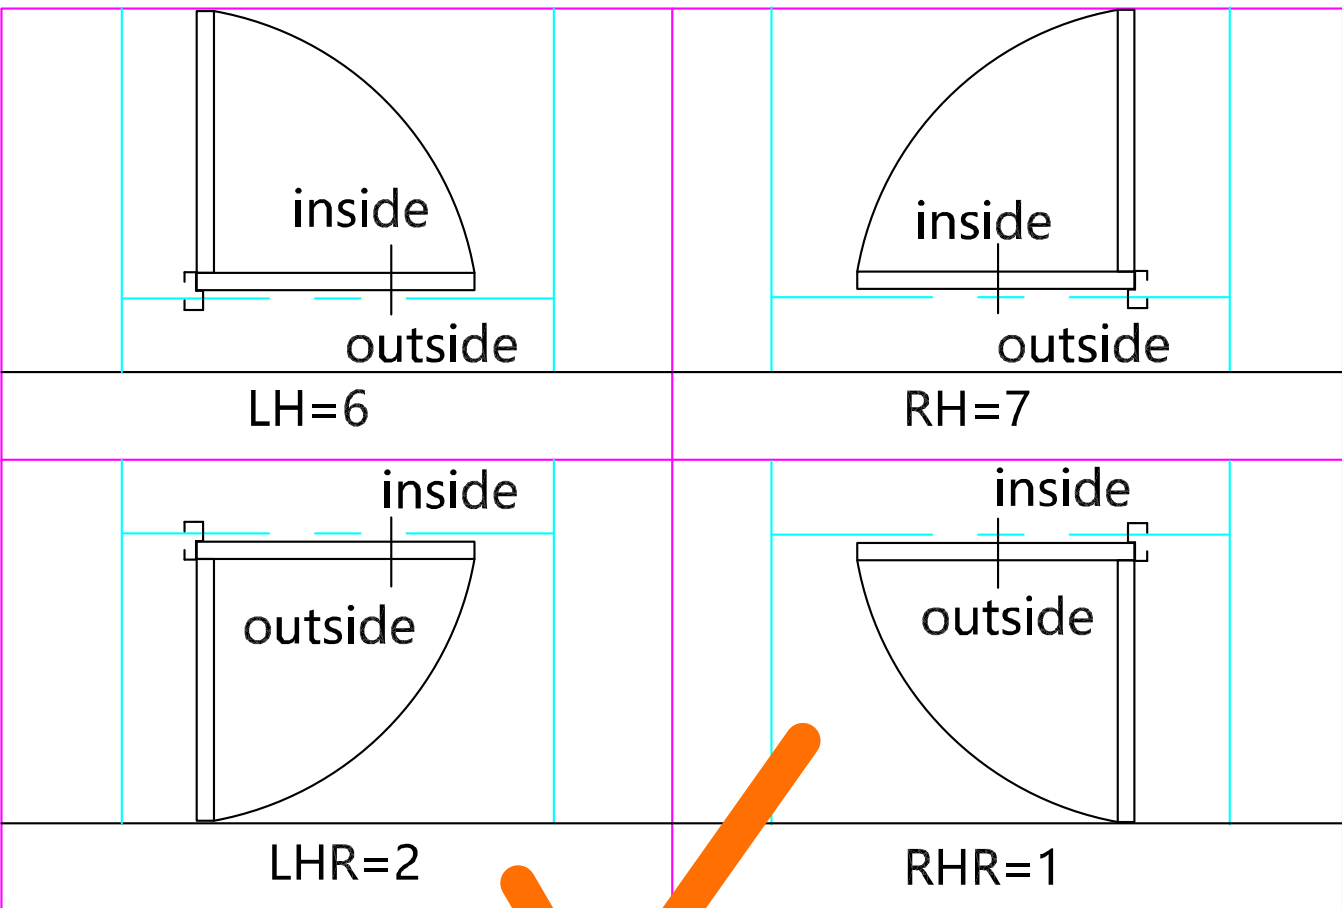



XZIC Shanghai Xunzhong Industry Co., Ltd

Project name

By		Drawing title	
Design		Size	
Check		Qty	16
Review		Opening direction	
Approval		Date	2026.05.18
		Page No	6
Total Page	34	Diagram number	

FD6


Fire - resistance time: 120 minutes

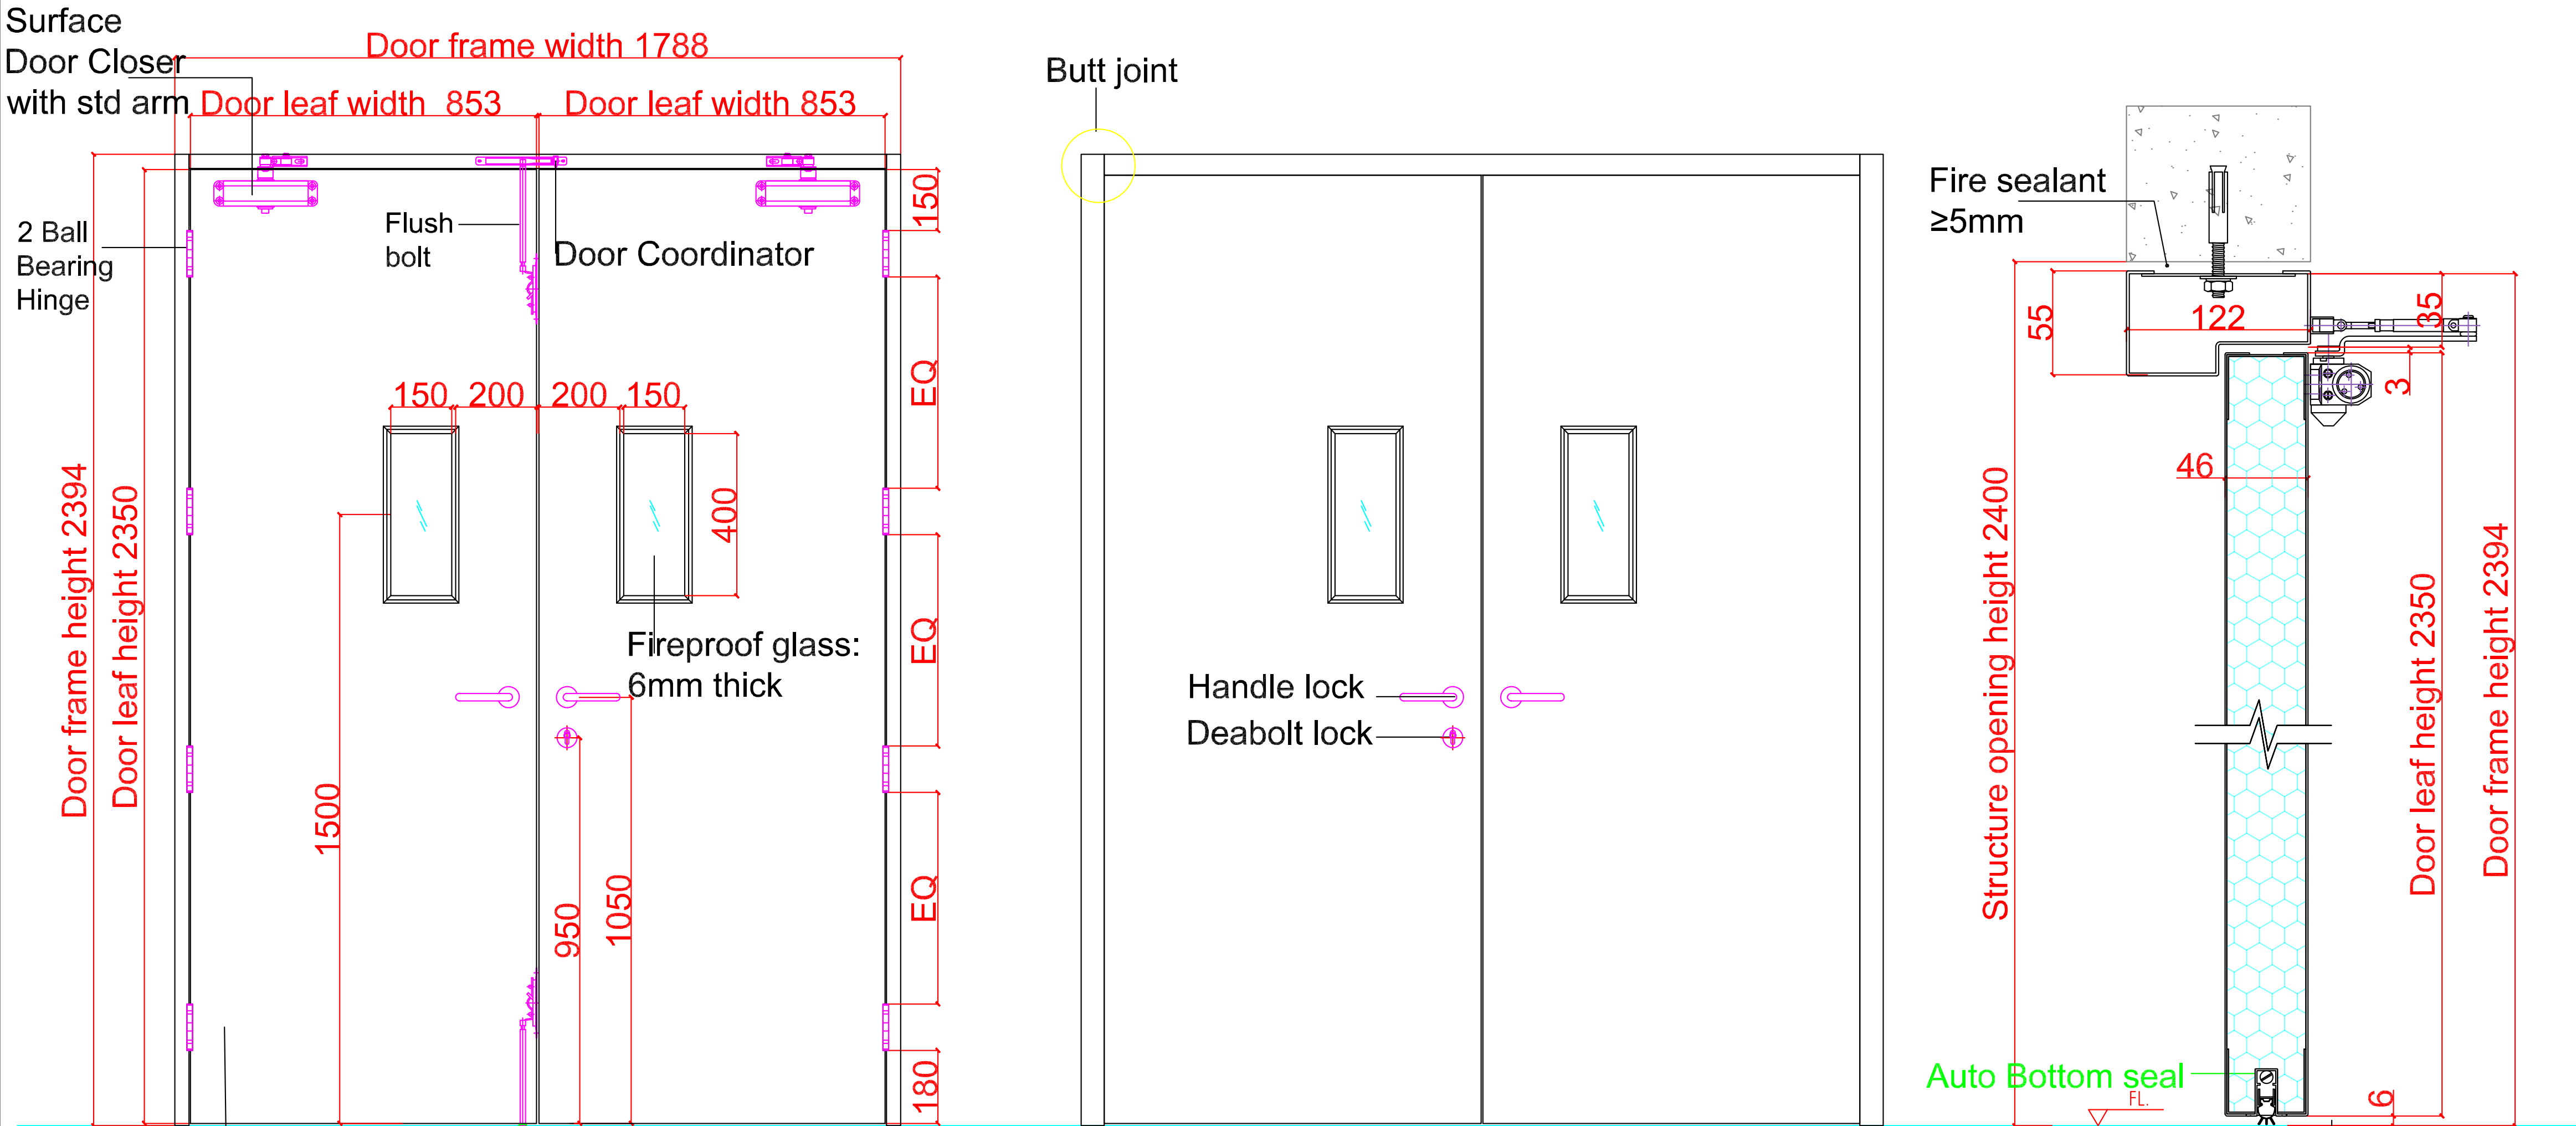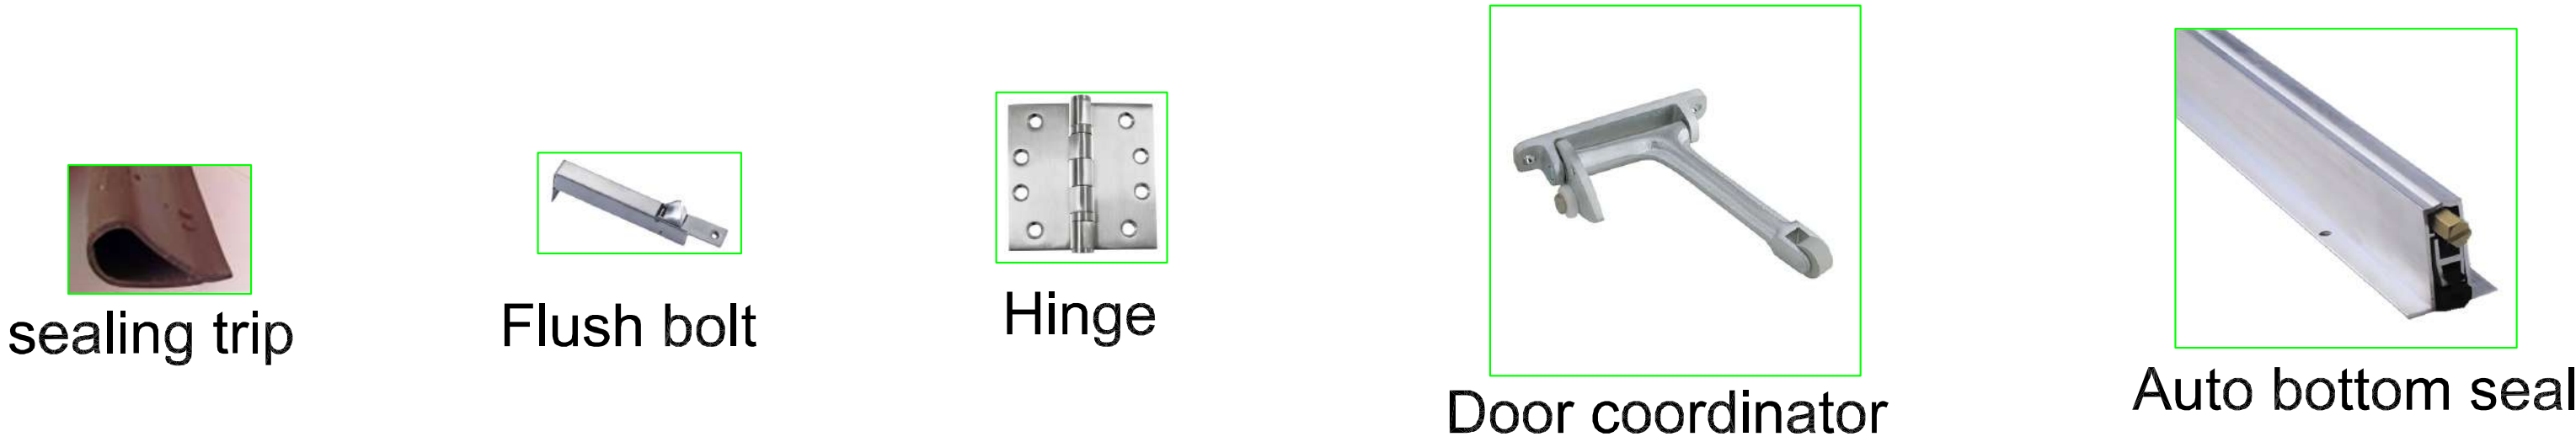


Finish: Polyester Powder coated

Outside elevation

Inside elevation

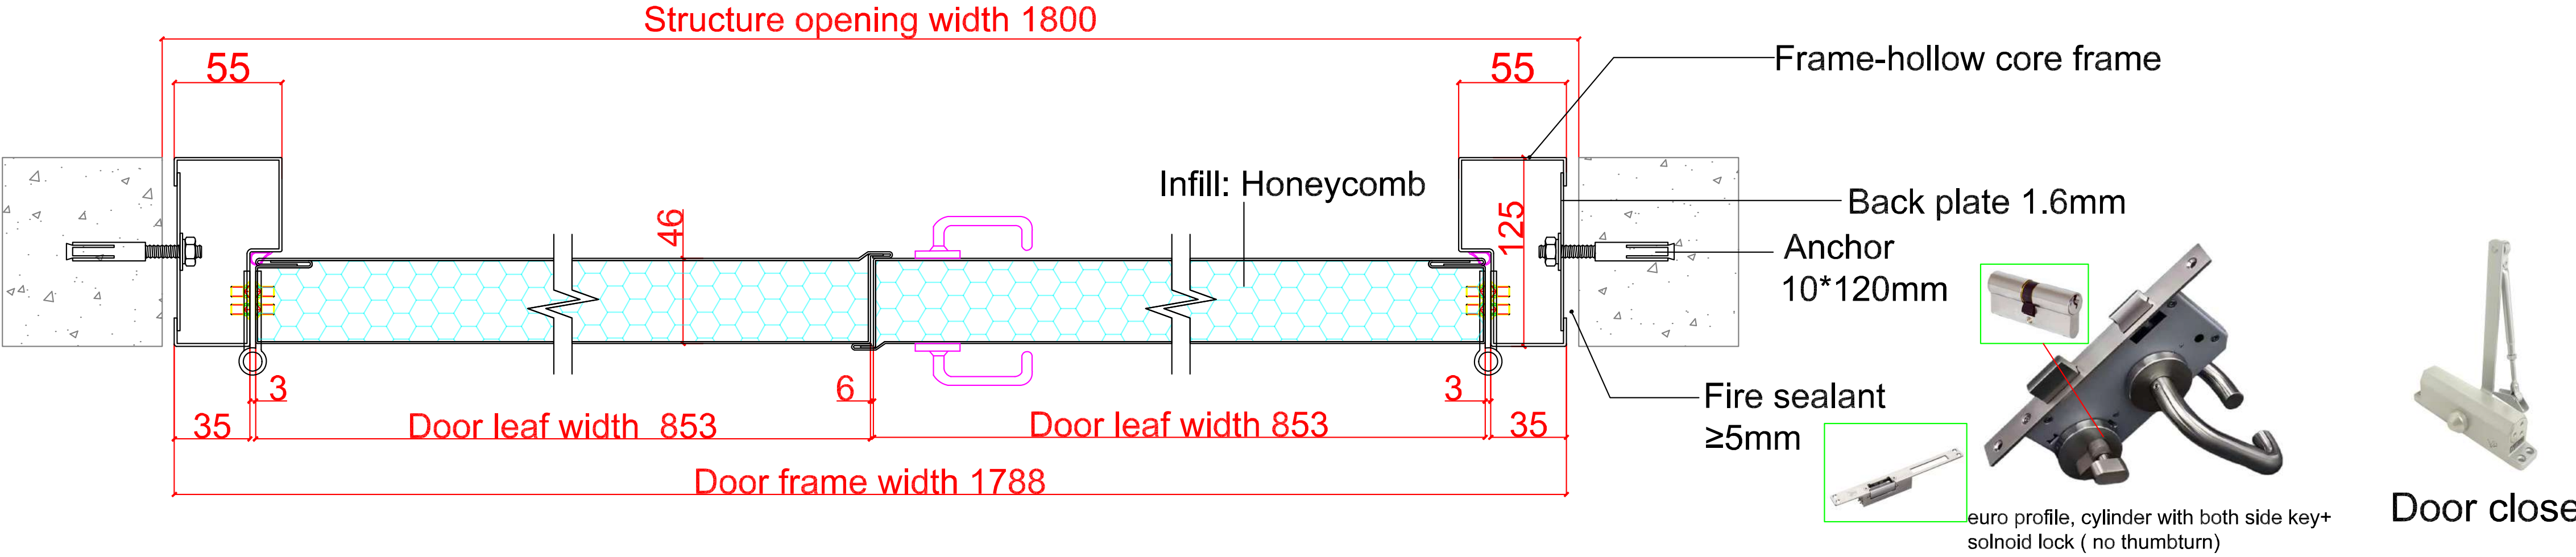

Hardware			
Name	Description	Qty	Remarks
Lock type	solenoid lock	1	4 pcs lever handle
Hinge	4.5*4*3	8	
Door closer	184	2	
Door stop			
Flush bolt		2	
Glass	150*400mm	2	
Auto Bottom seal		2	
Door coordinator		1	
Smoke seal		1	
Door frame	1.6mm Galvanized steel sheet		
Door leaf	1.2mm Galvanized steel sheet		
Threshold			
Filling	Honeycomb		
Colour			




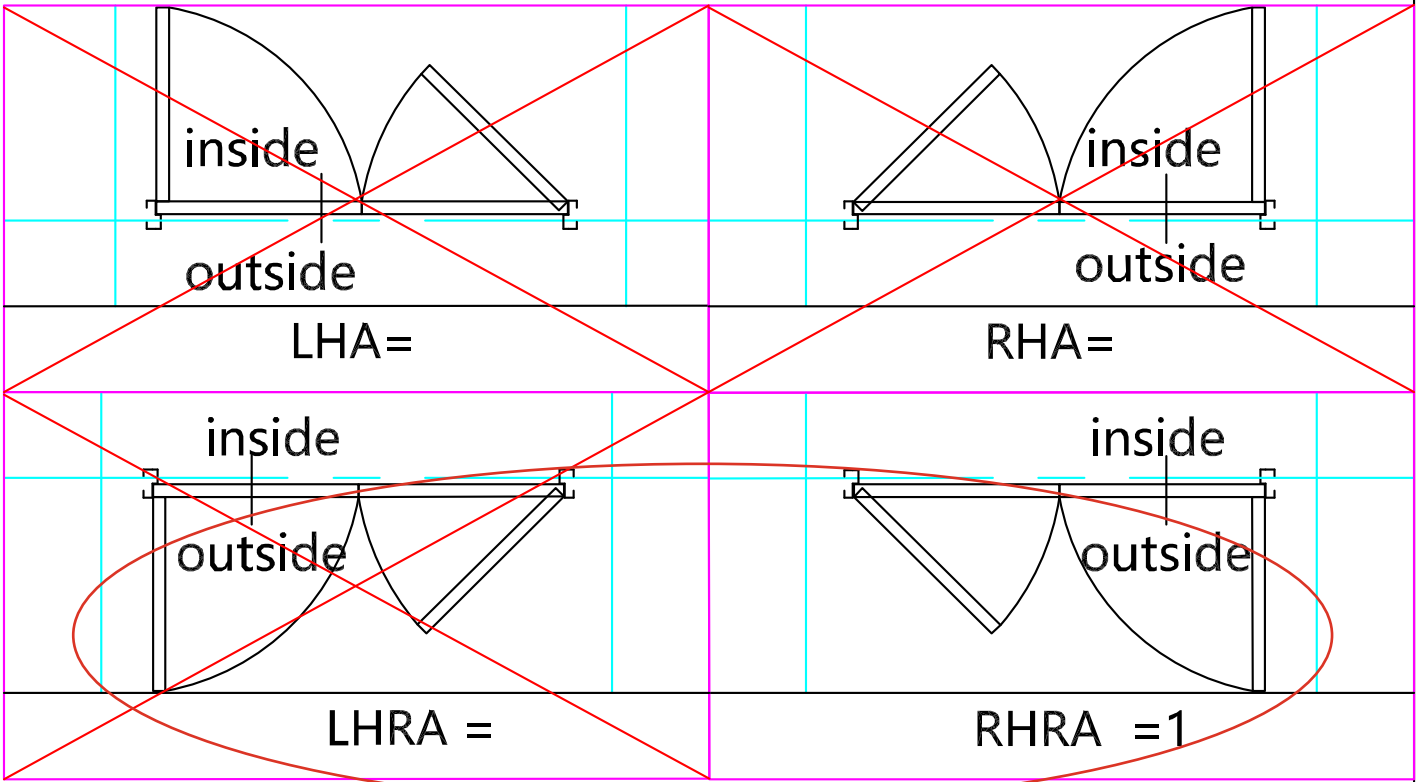


FD3 - LHR + RHR = 1

 Shanghai Xunzhong Industry Co., Ltd			
Project name			
By		Drawing title	
Design		Size	
Check		Qty	1
Review		Opening direction	
Approval		Date	2026.05.18
Total Page	34	Page No	8
		Diagram number	

FD8


Fire - resistance time: 120 minutes

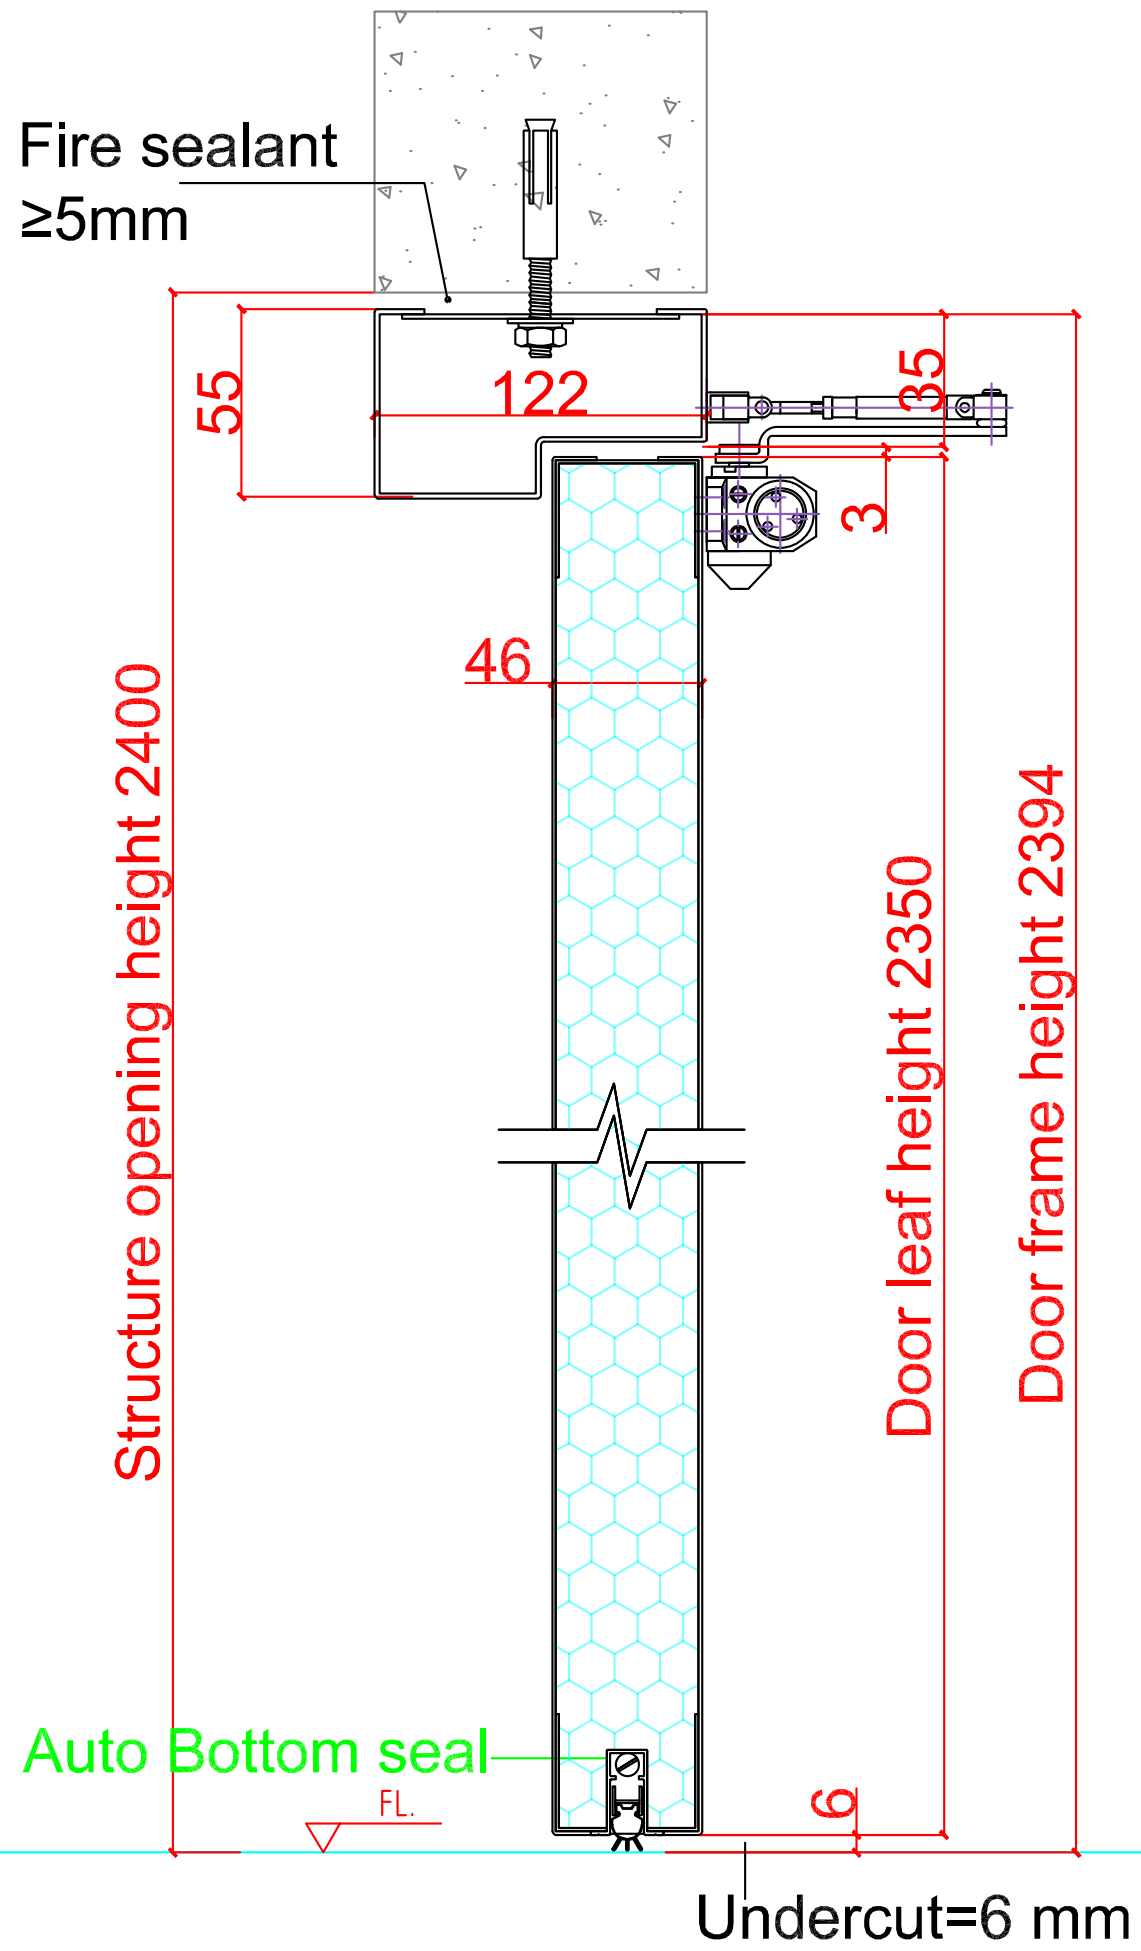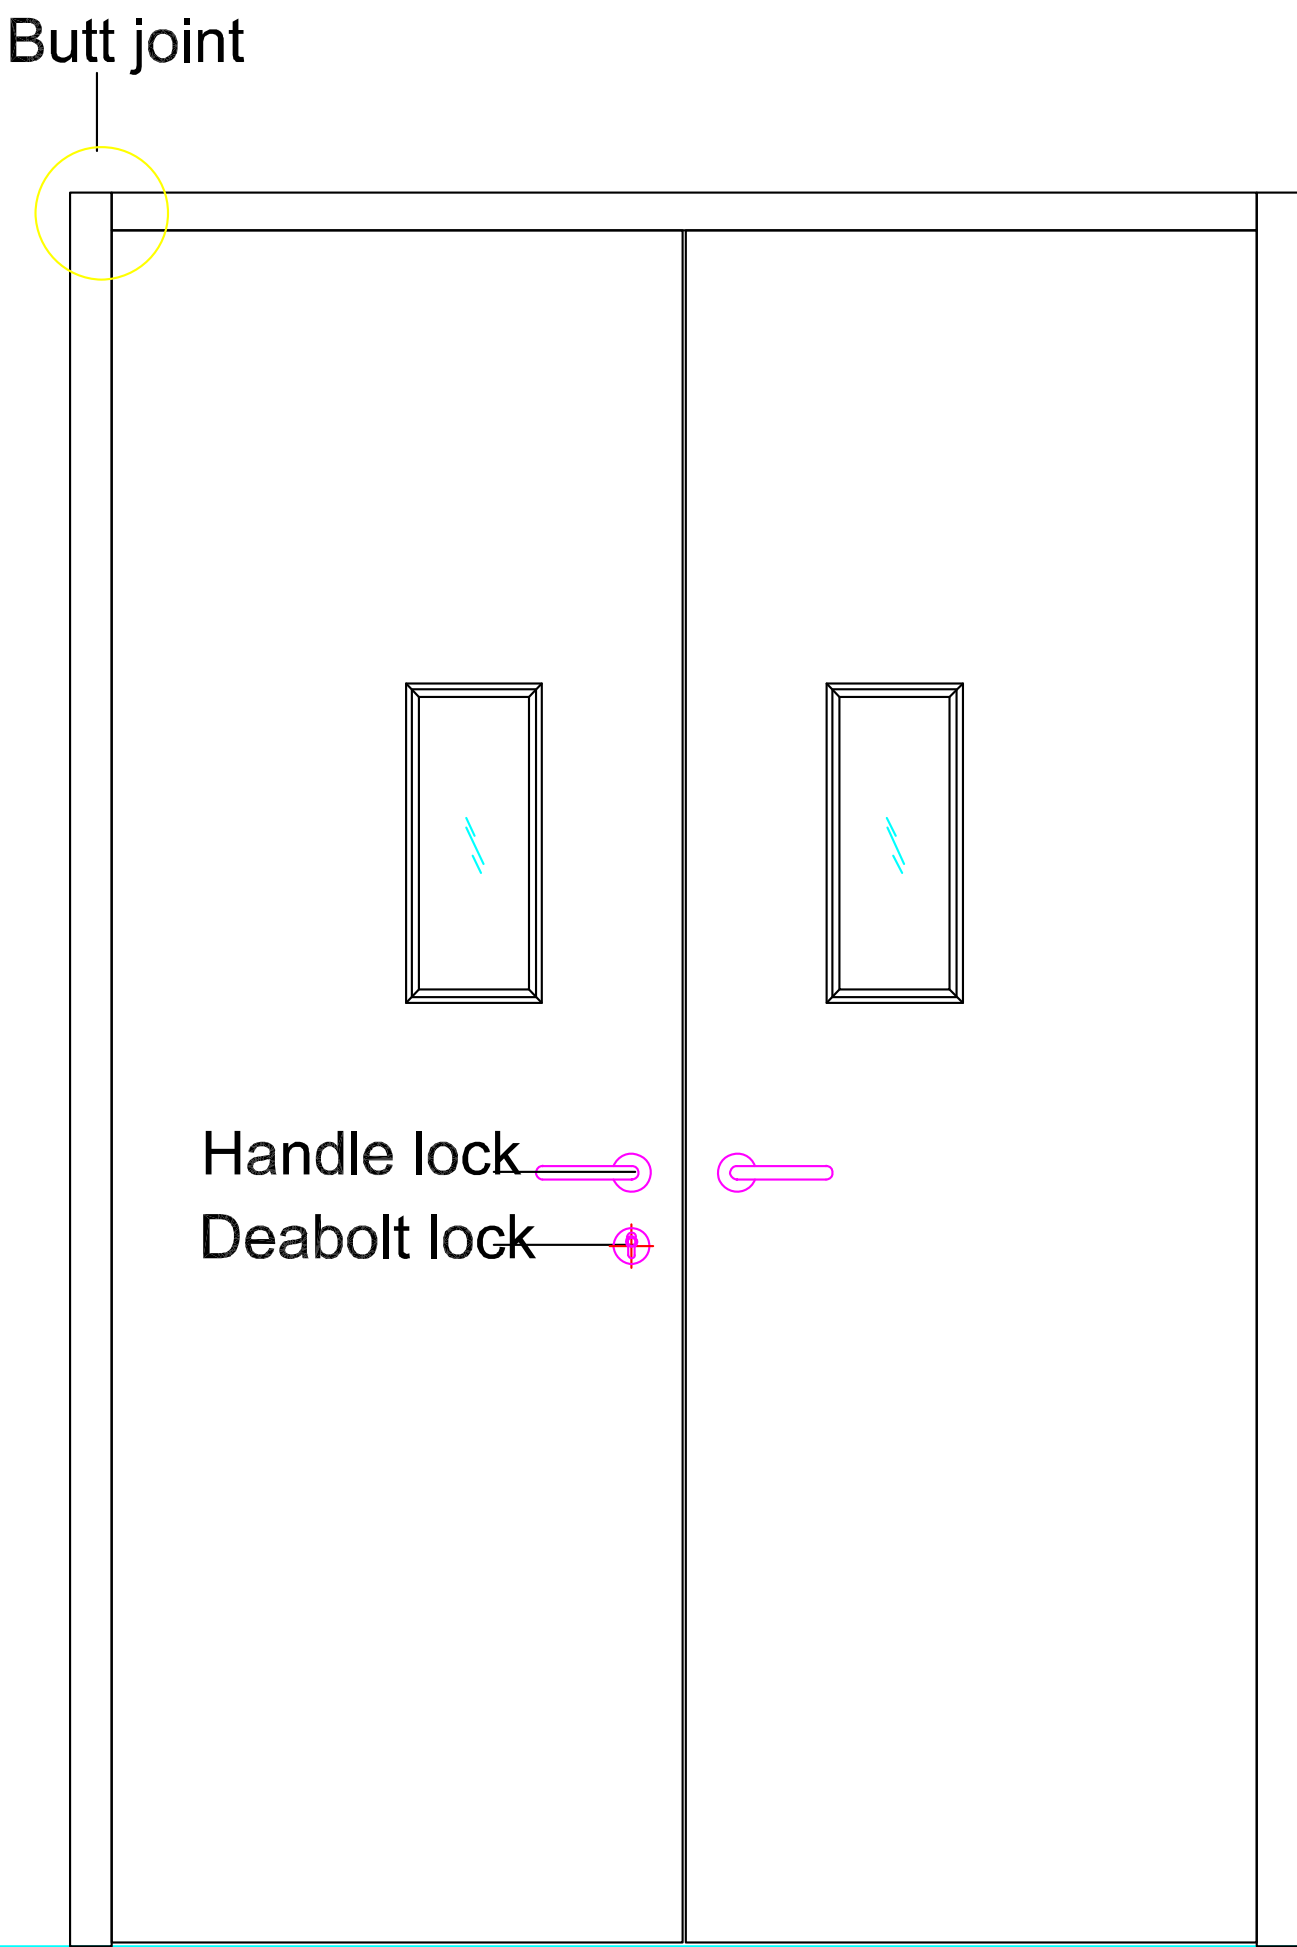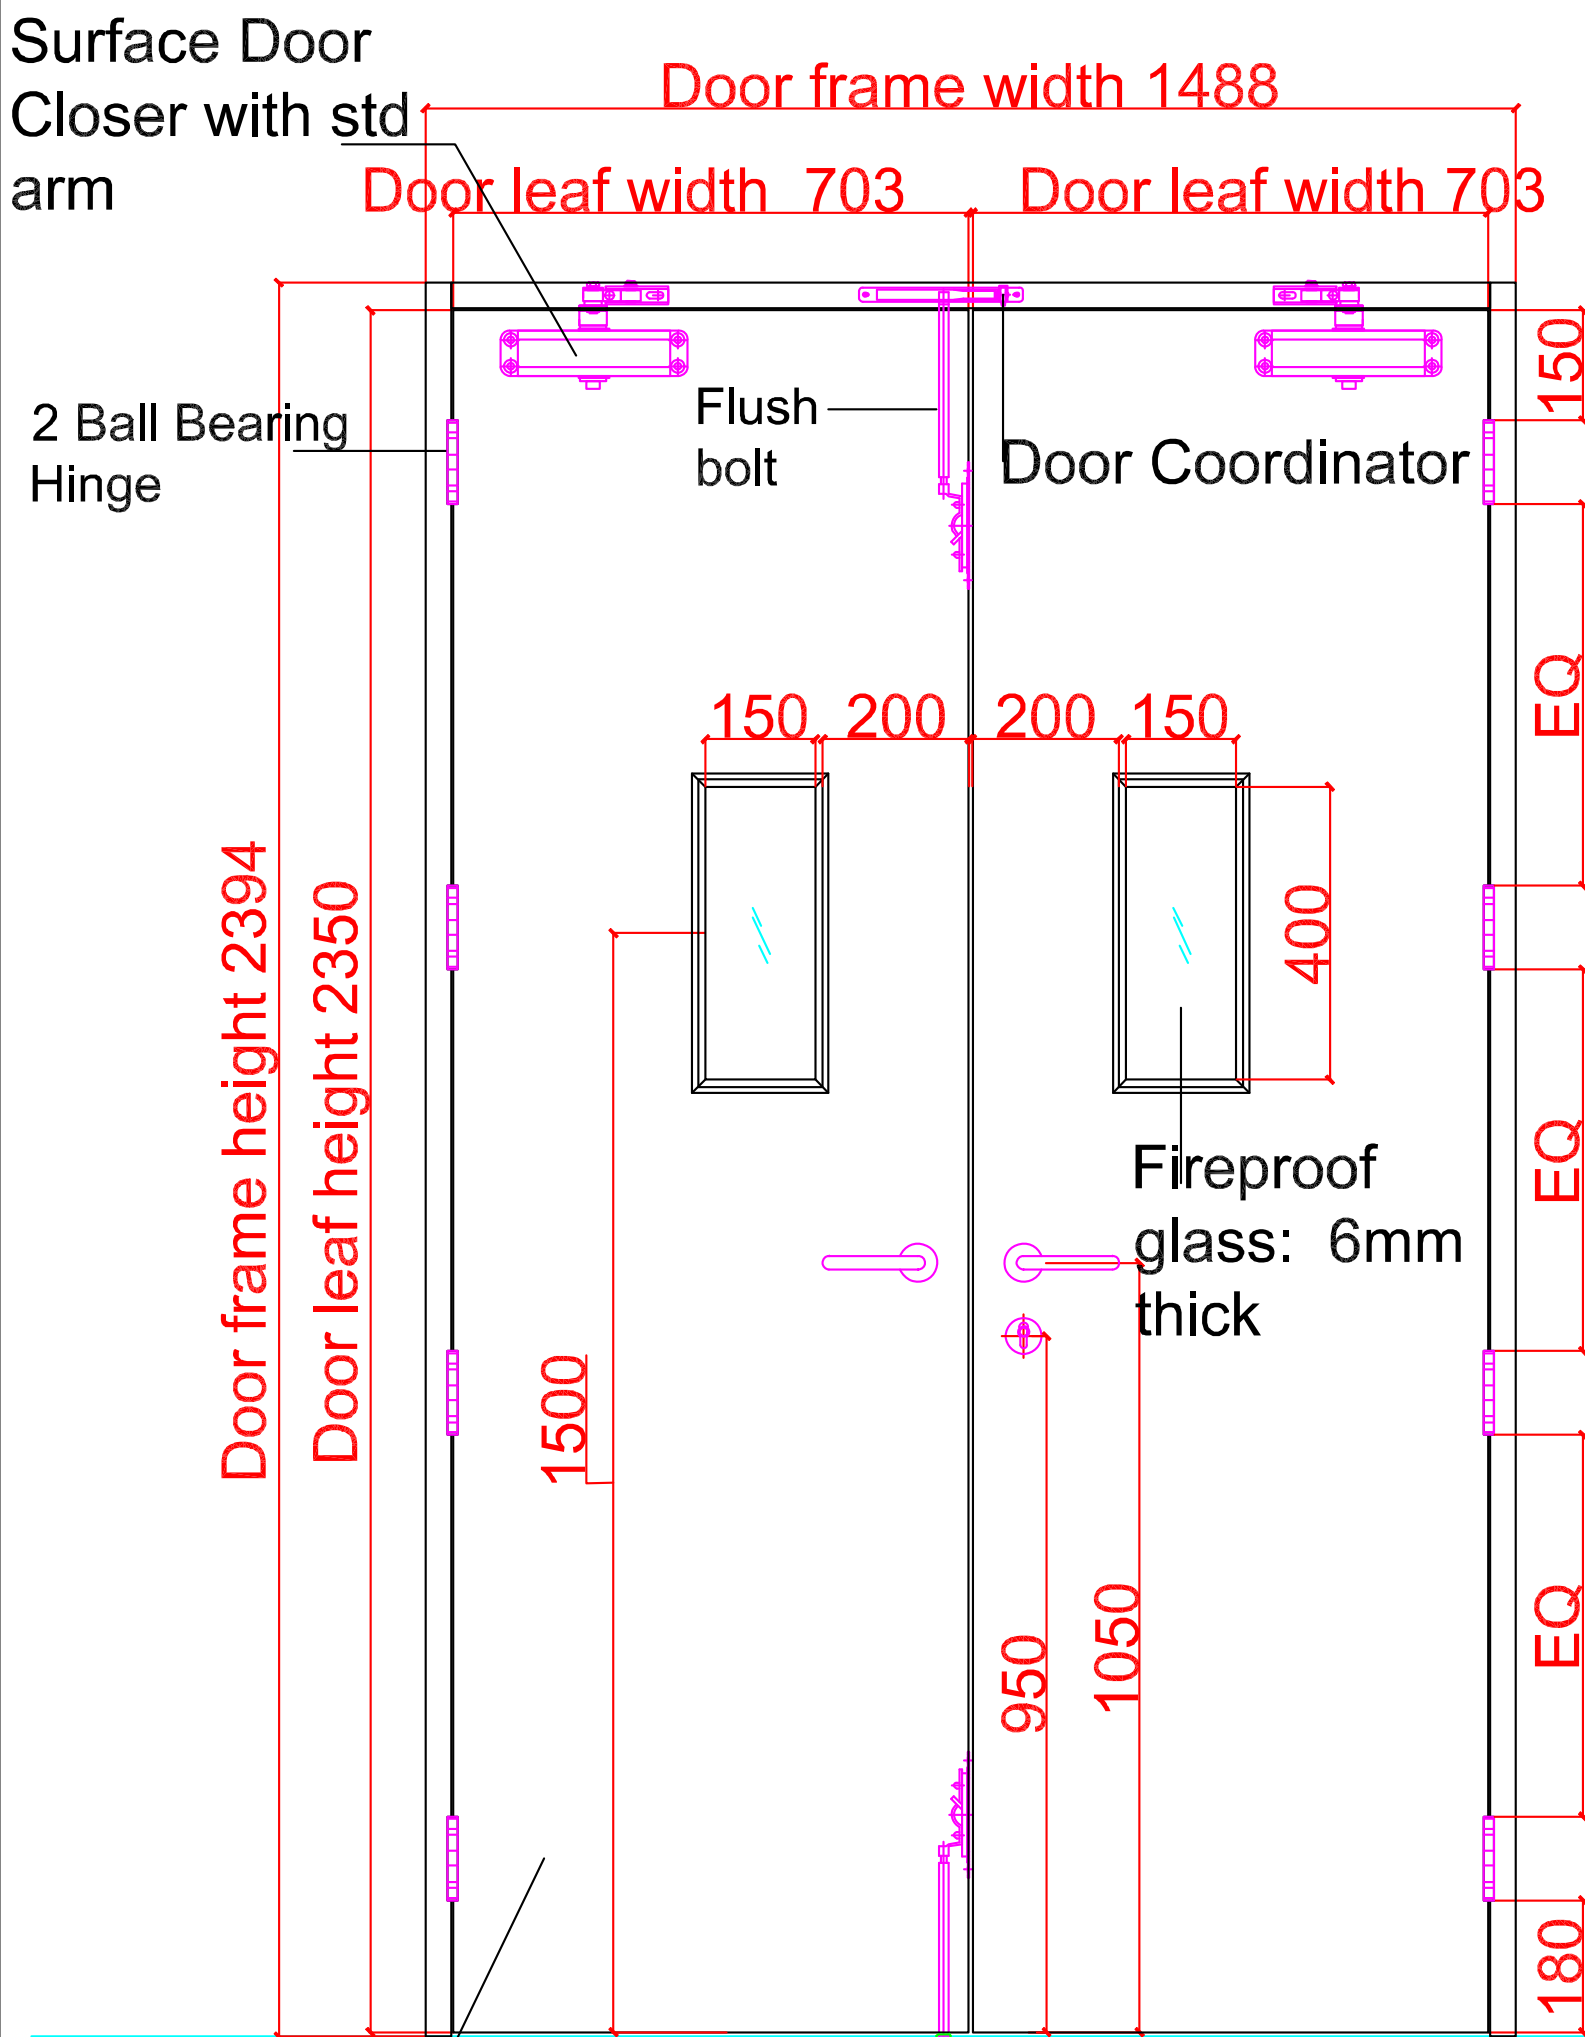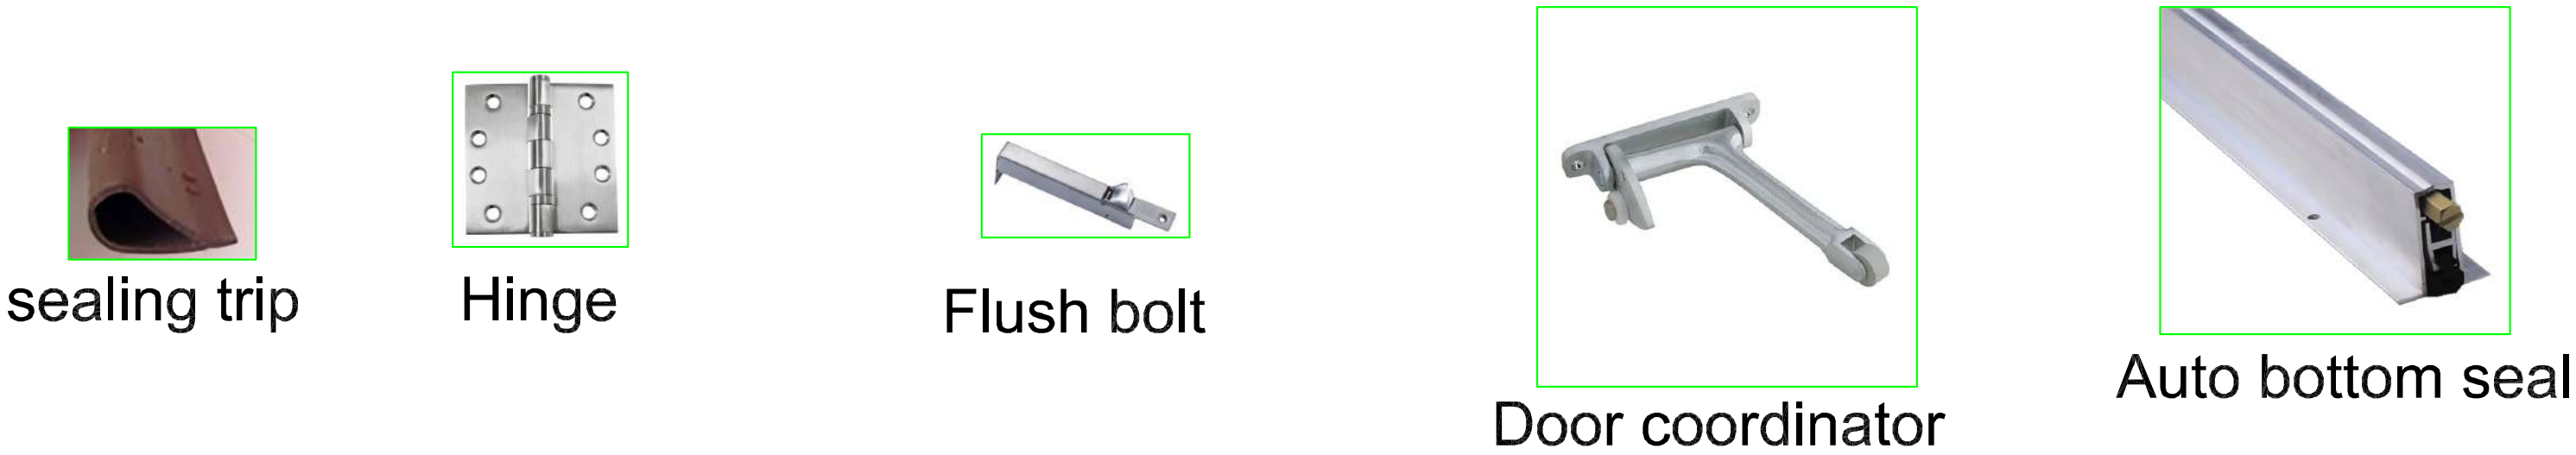


Finish: Polyester Powder coated

Outside elevation

Inside elevation

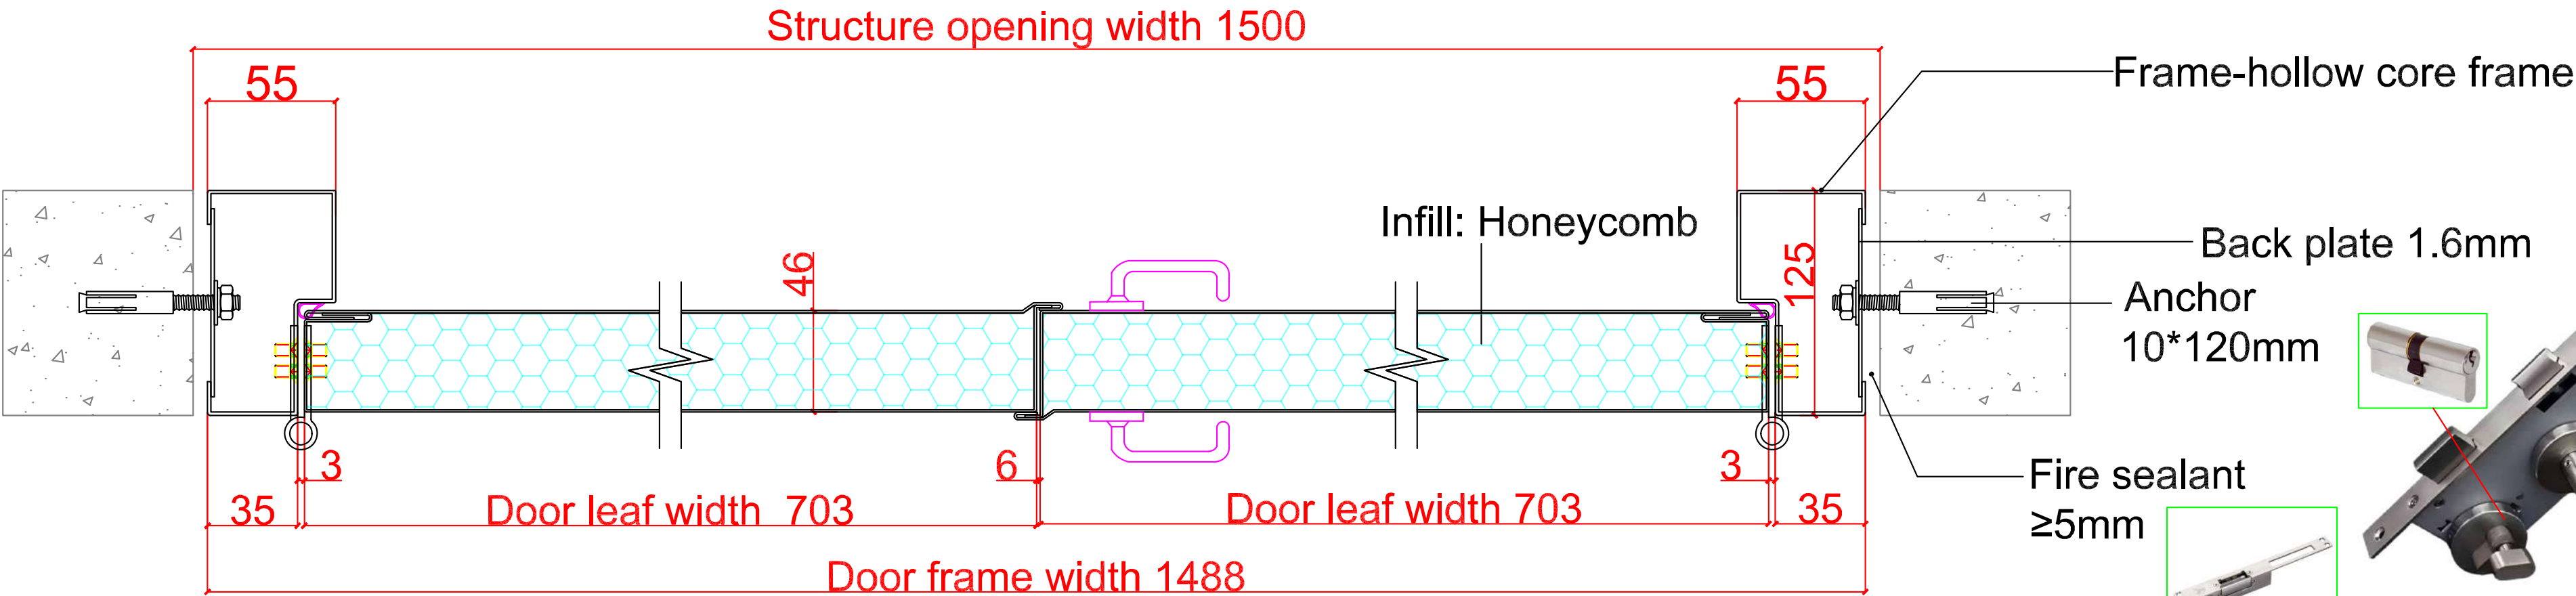


Hardware			
Name	Description	Qty	Remarks
Lock type	solenoid lock	1	4 pcs lever handle
Hinge	4.5*4*3	8	
Door closer	184	2	
Door stop			
Flush bolt		2	
Glass	150*400mm	2	
Auto Bottom seal		2	
Door coordinator		1	
Smoke seal		1	
Door frame	1.6mm Galvanized steel sheet		
Door leaf	1.2mm Galvanized steel sheet		
Threshold			
Filling	Honeycomb		
Colour			

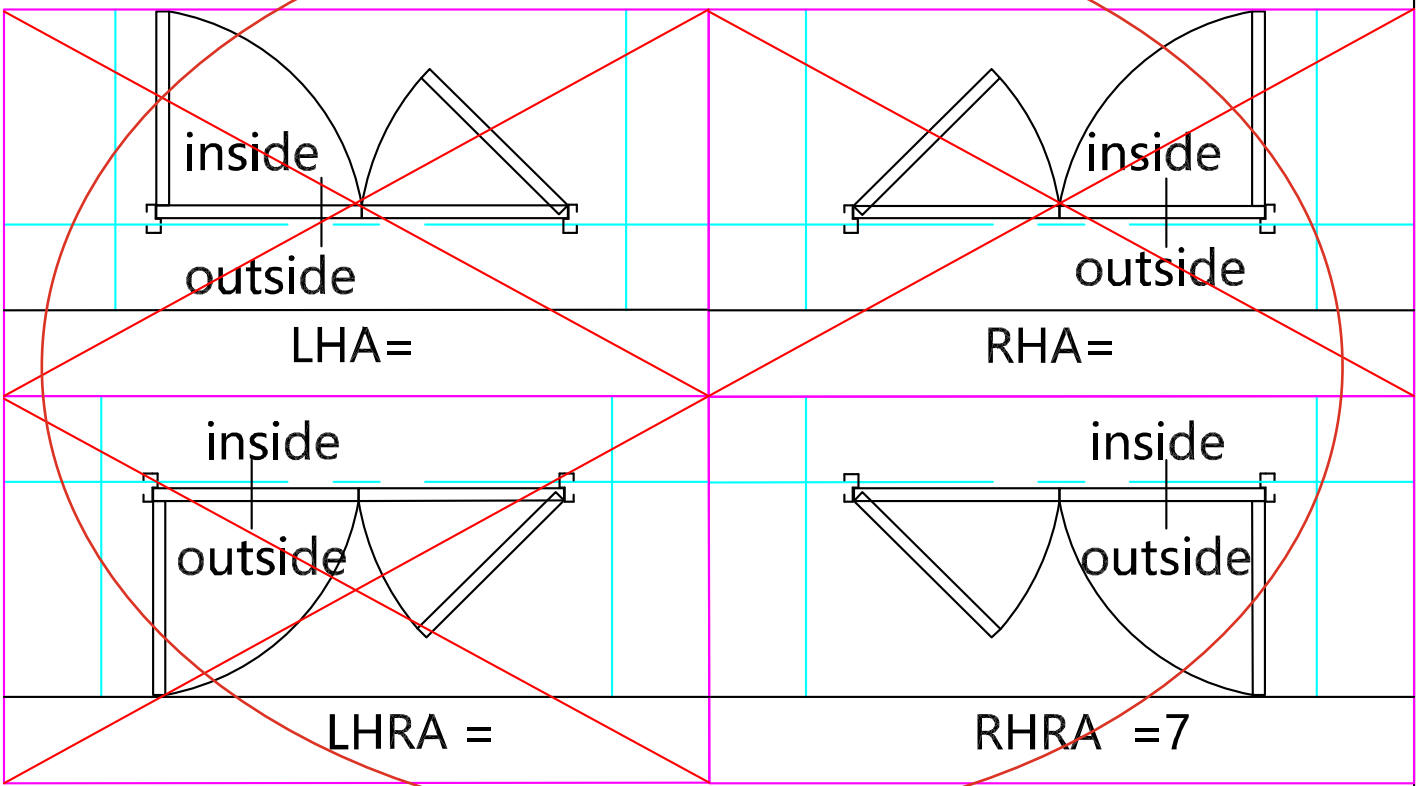

FD8 - LHA + RHA = 2




LHRA + RHRA = 5

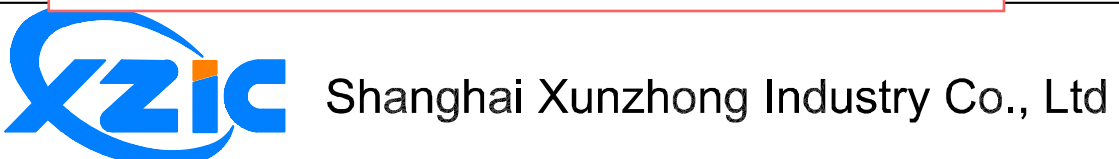

Project name

By		Drawing title	
Design		Size	
Check		Qty	7
Review		Opening direction	
Approval		Date	2026.05.18
		Page No	9
Total Page	34	Diagram number	

Fire - resistance time: 120 minutes

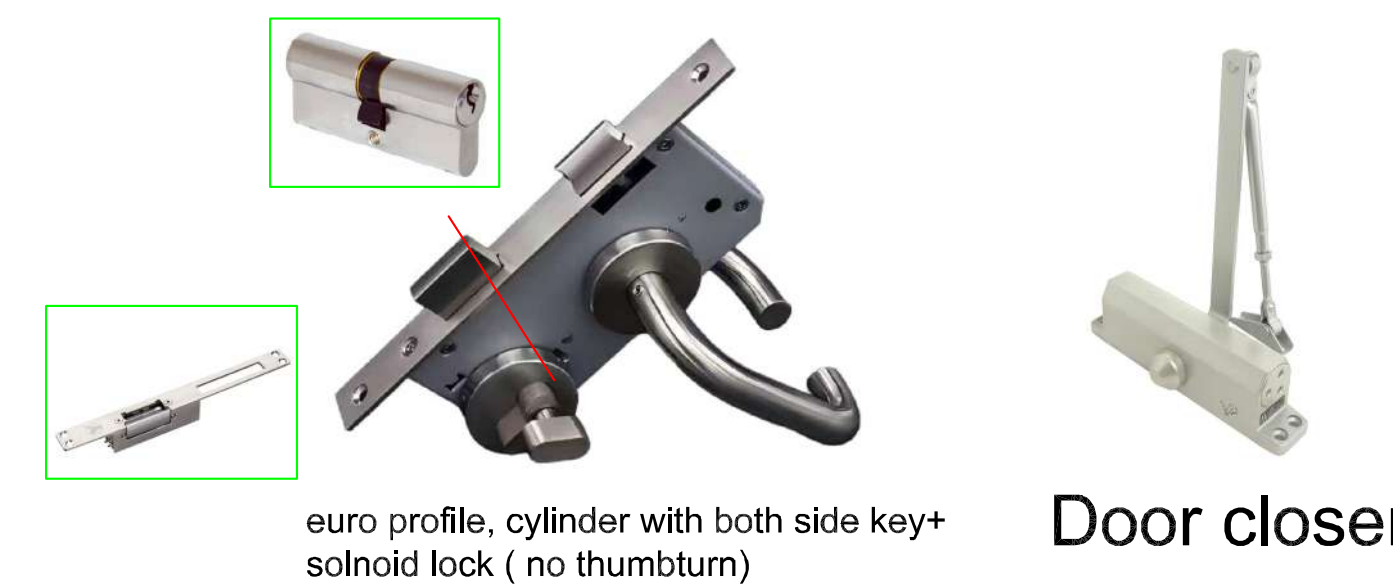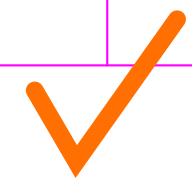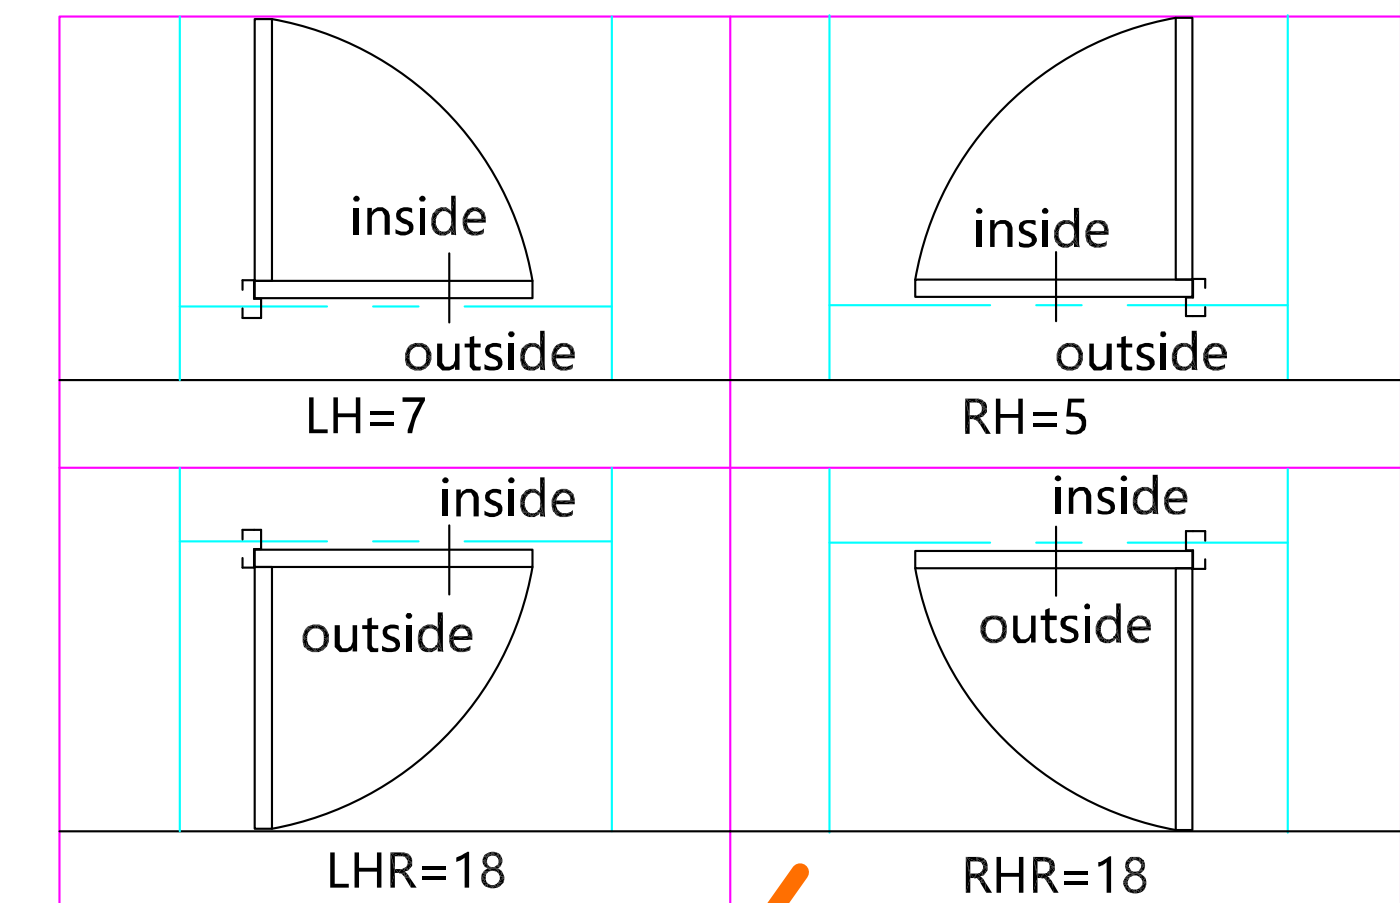

 Shanghai Xunzhong Industry Co., Ltd			
Project name			
By		Drawing title	
Design		Size	
Check		Qty	48
Review		Opening direction	
Approval		Date	2026.05.18
		Page No	10
Total Page	34	Diagram number	

FD11

Fire - resistance time: 120 minutes



sealing trip




Hinge




Auto bottom seal






Hardware			
Name	Description	Qty	Remarks
Lock type	solenoid lock	1	
Hinge	4.5*4*3	4	
Door closer	184	1	
Door stop			
Glass	150*400mm	1	
Auto Bottom seal		1	
Smoke seal		1	
Door frame	1.6mm Galvanized steel sheet		
Door leaf	1.2mm Galvanized steel sheet		
Threshold			
Filling	Honeycomb		
Colour			

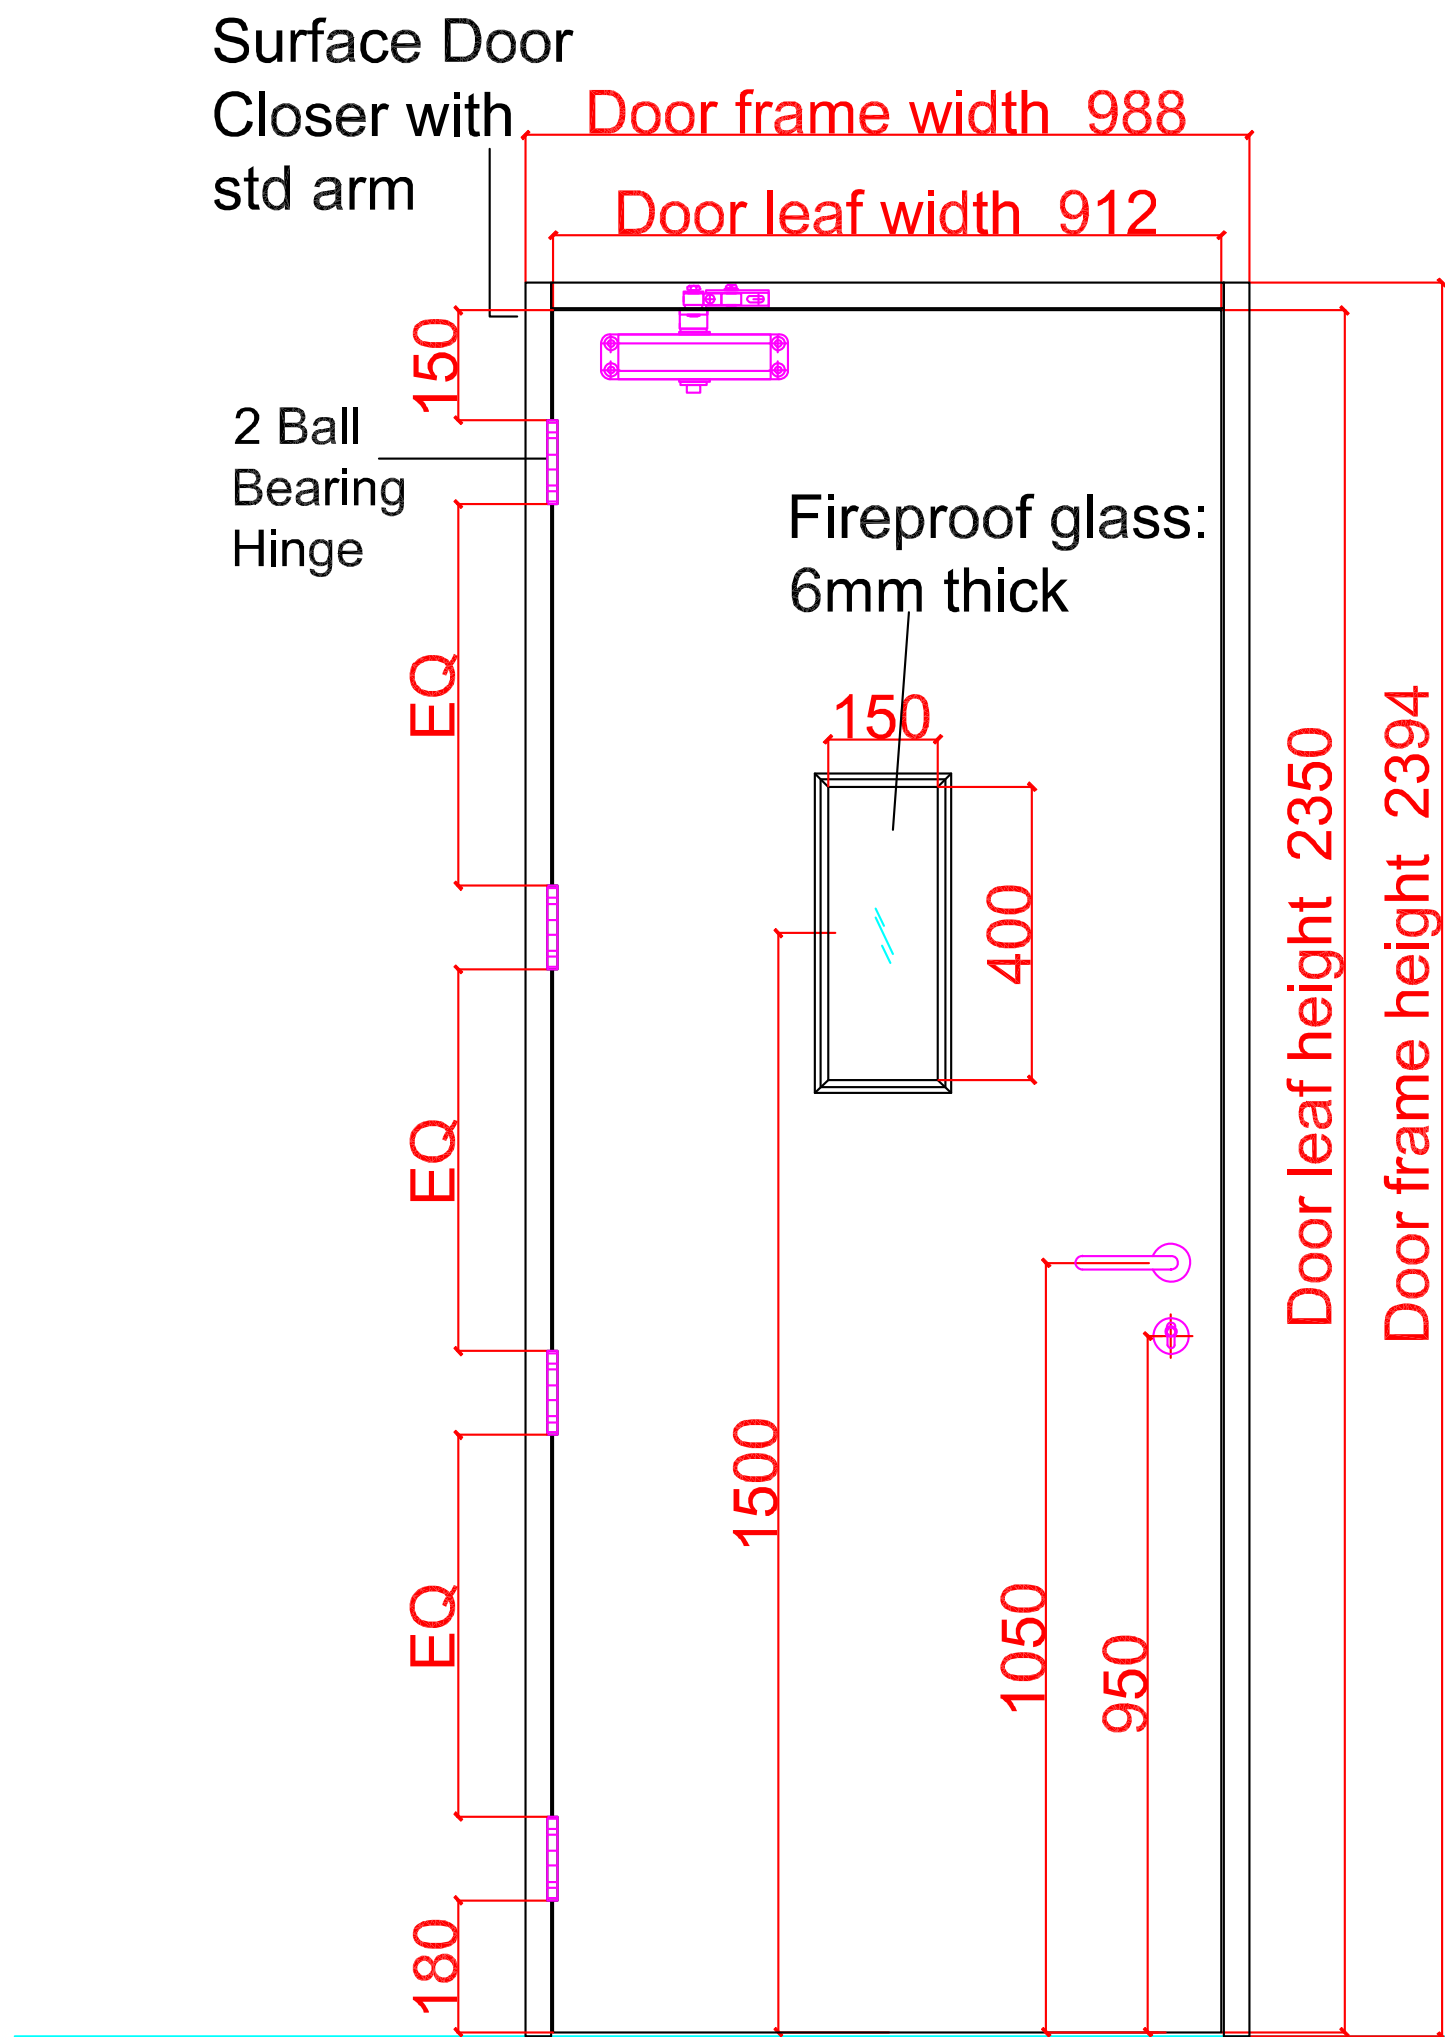

Outside elevation

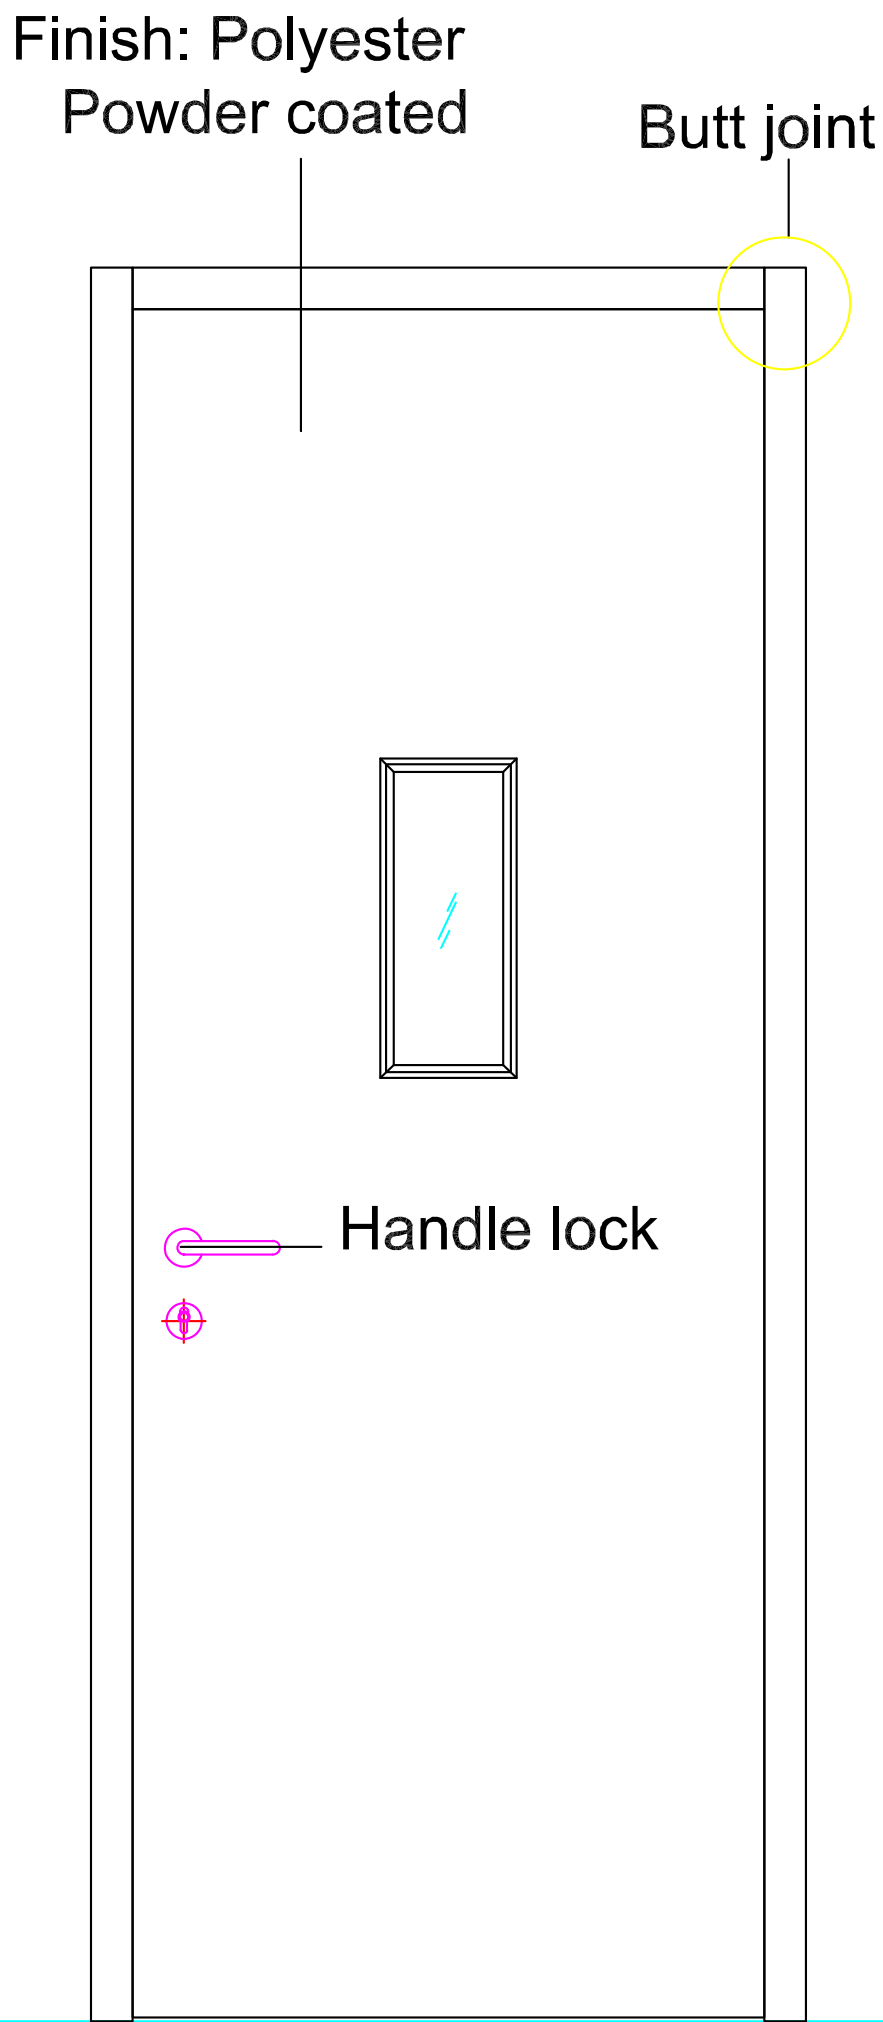

Inside elevation

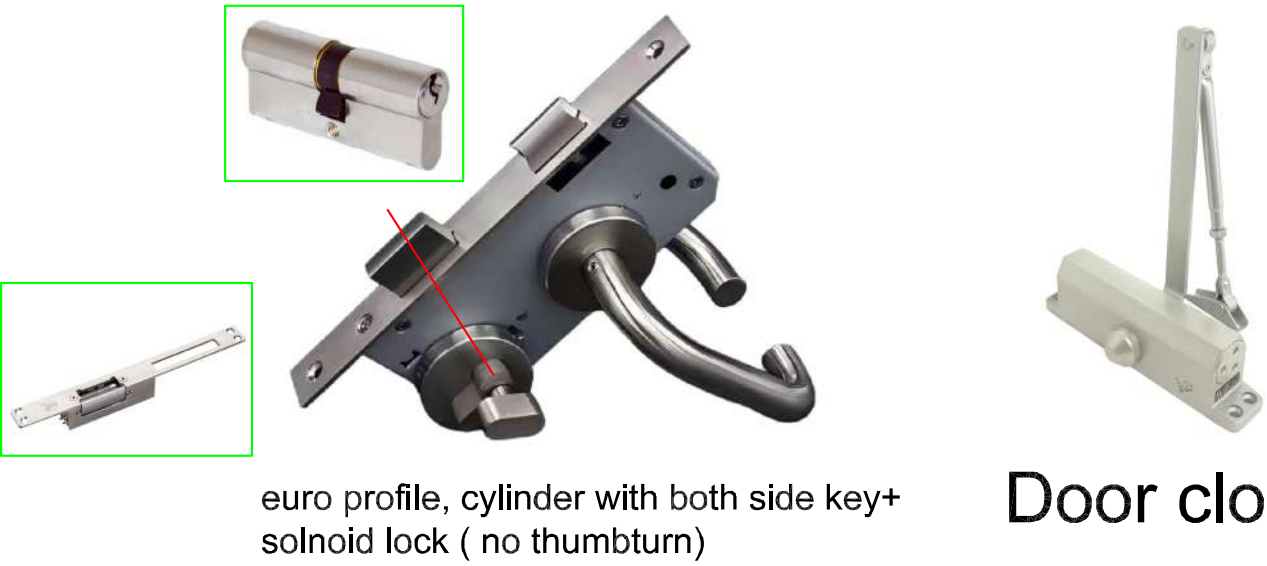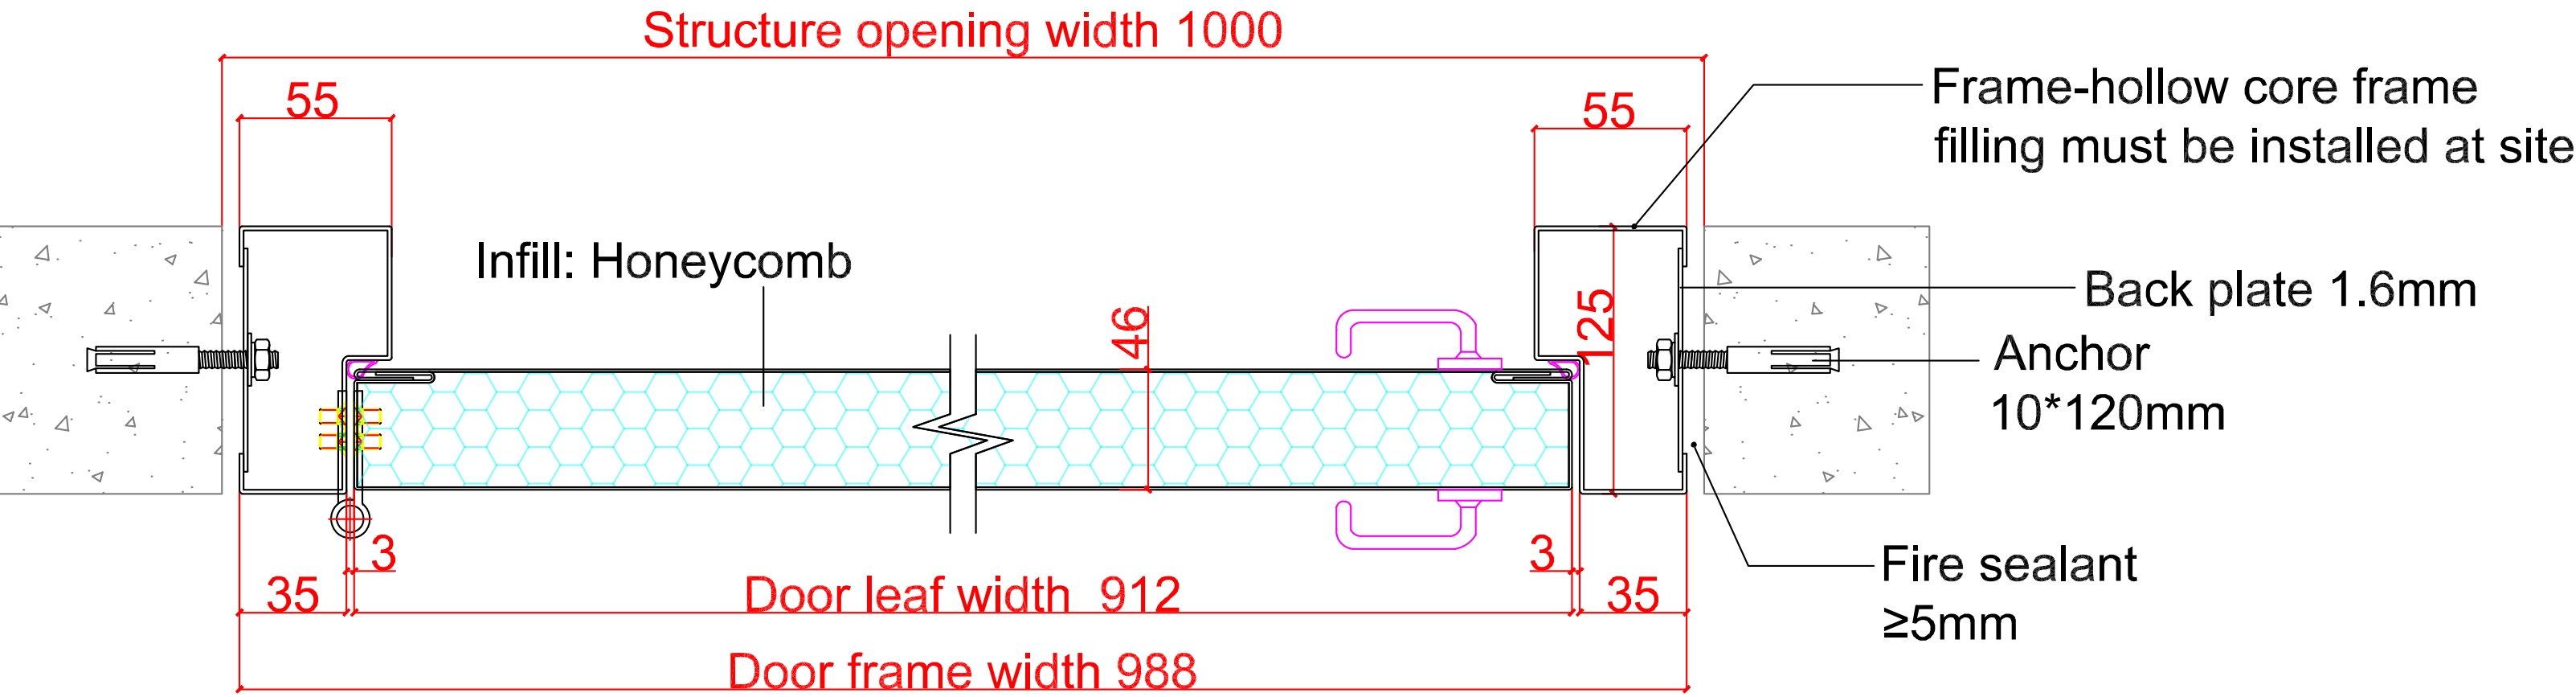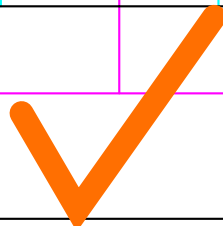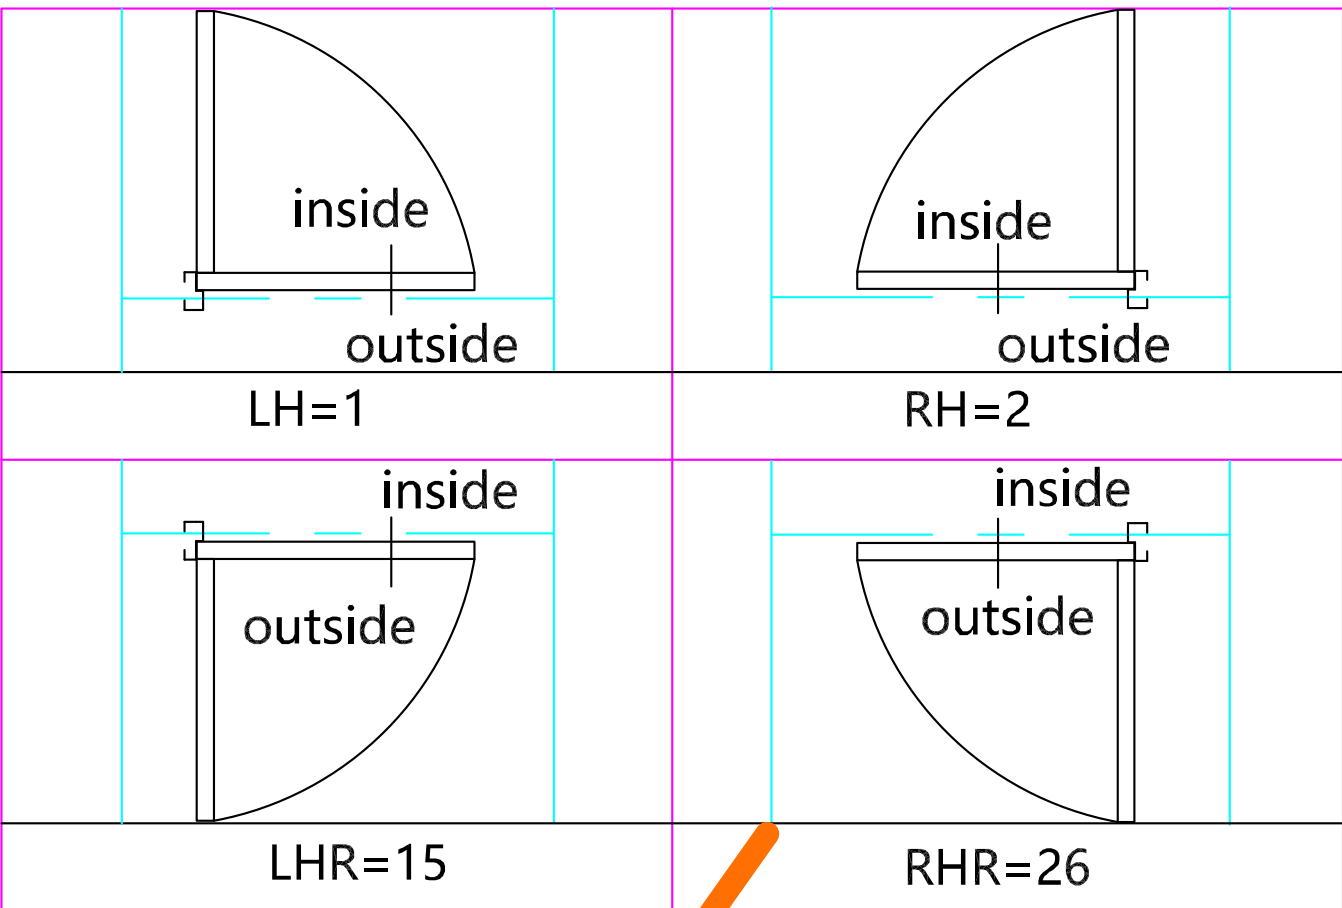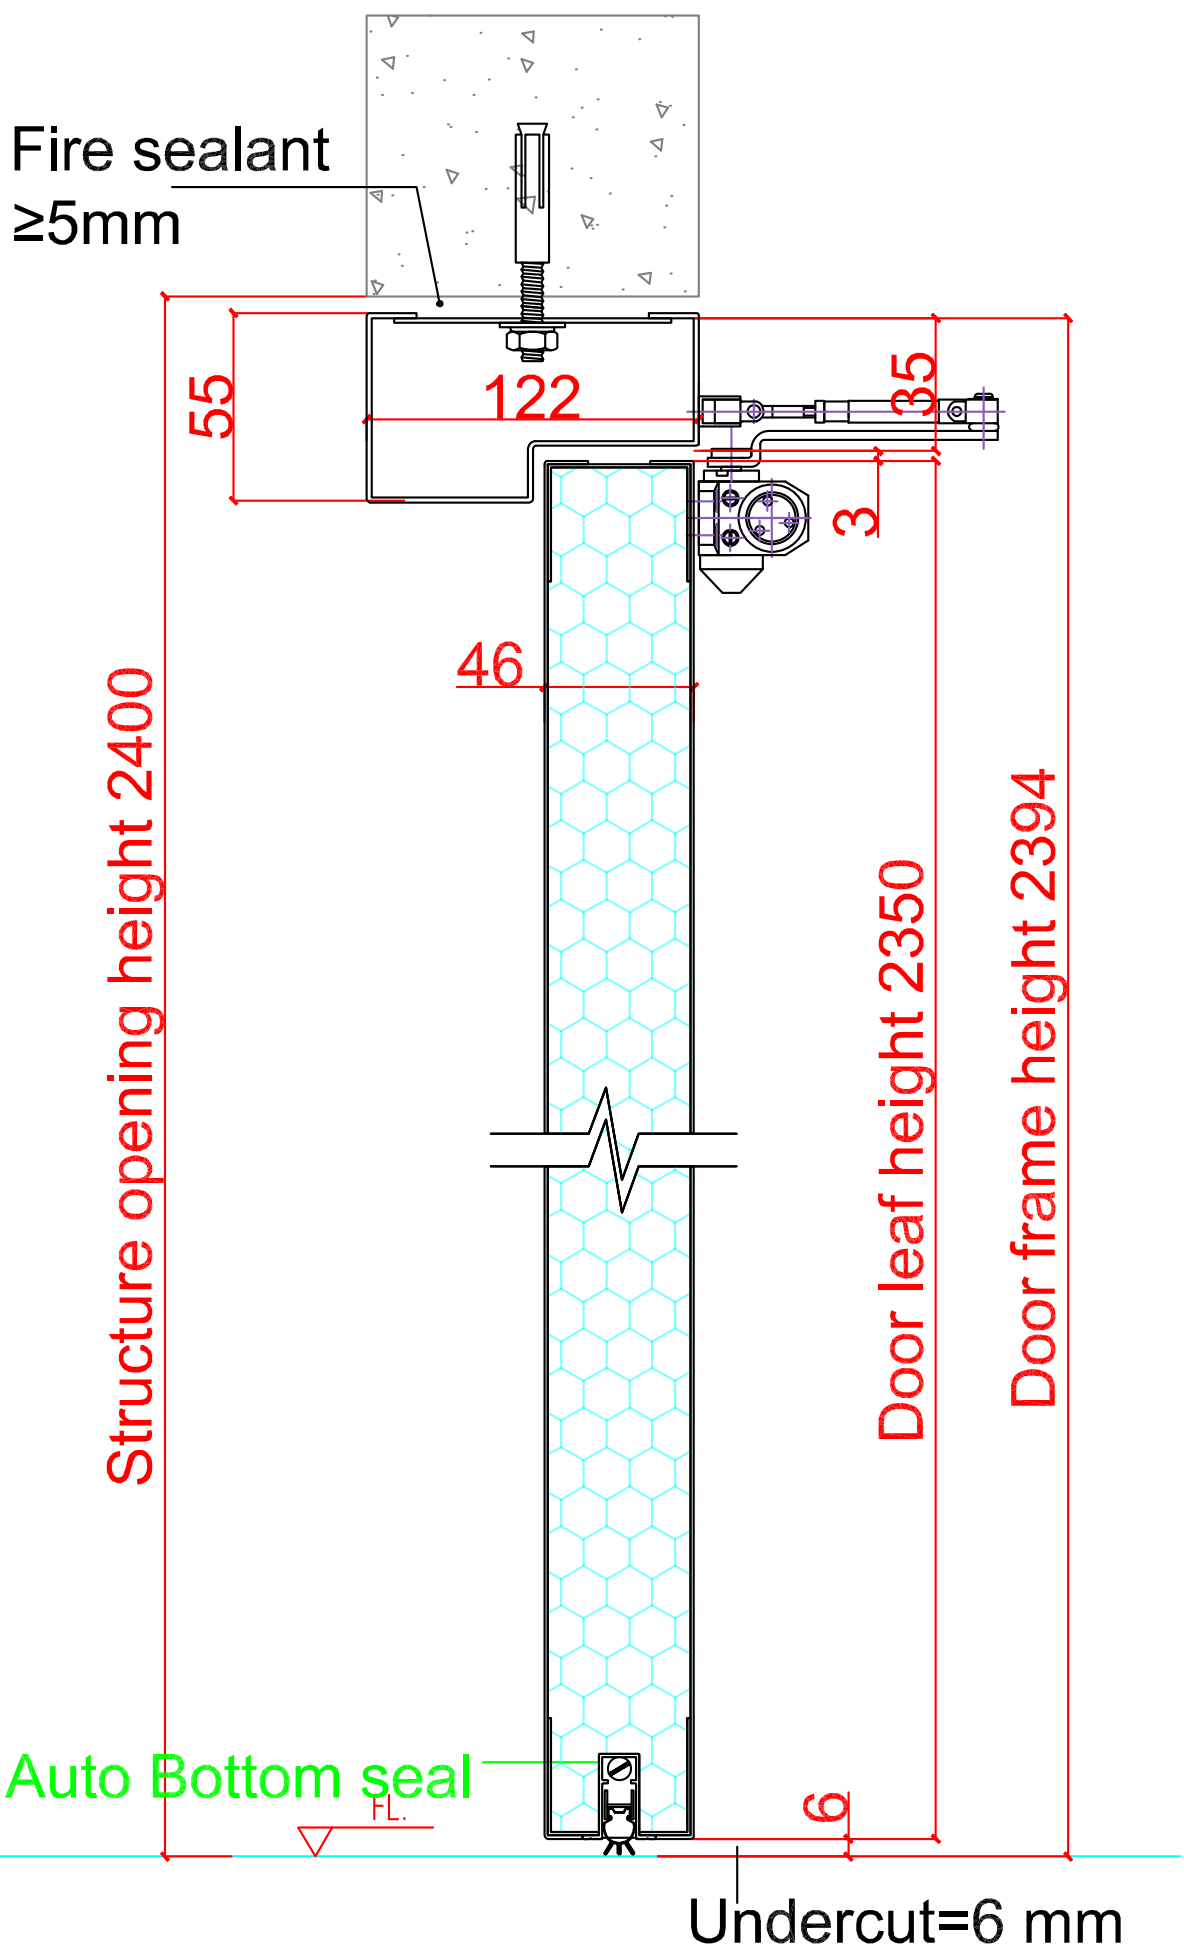



 Shanghai Xunzhong Industry Co., Ltd			
Project name			
By		Drawing title	
Design		Size	
Check		Qty	44
Review		Opening direction	
Approval		Date	2026.05.18
Total Page	34	Page No	11
		Diagram number	

Fire - resistance time: 120 minutes




Project name

By		Drawing title	
Design		Size	
Check		Qty	12
Review		Opening direction	
Approval		Date	2026.05.18
		Page No	12
Total Page	34	Diagram number	


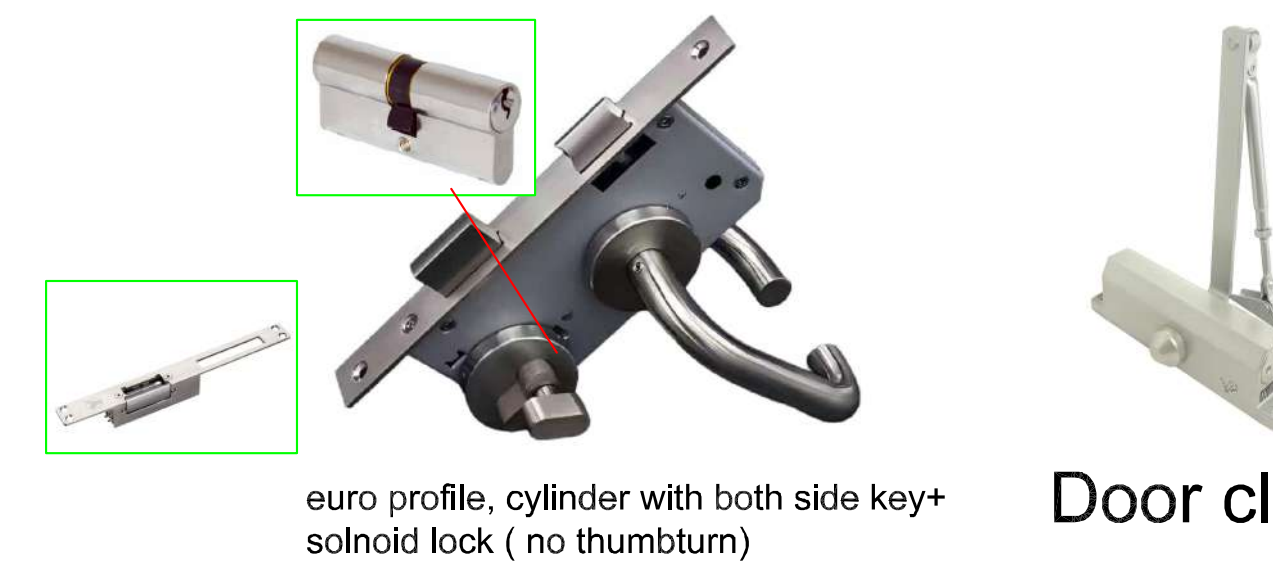
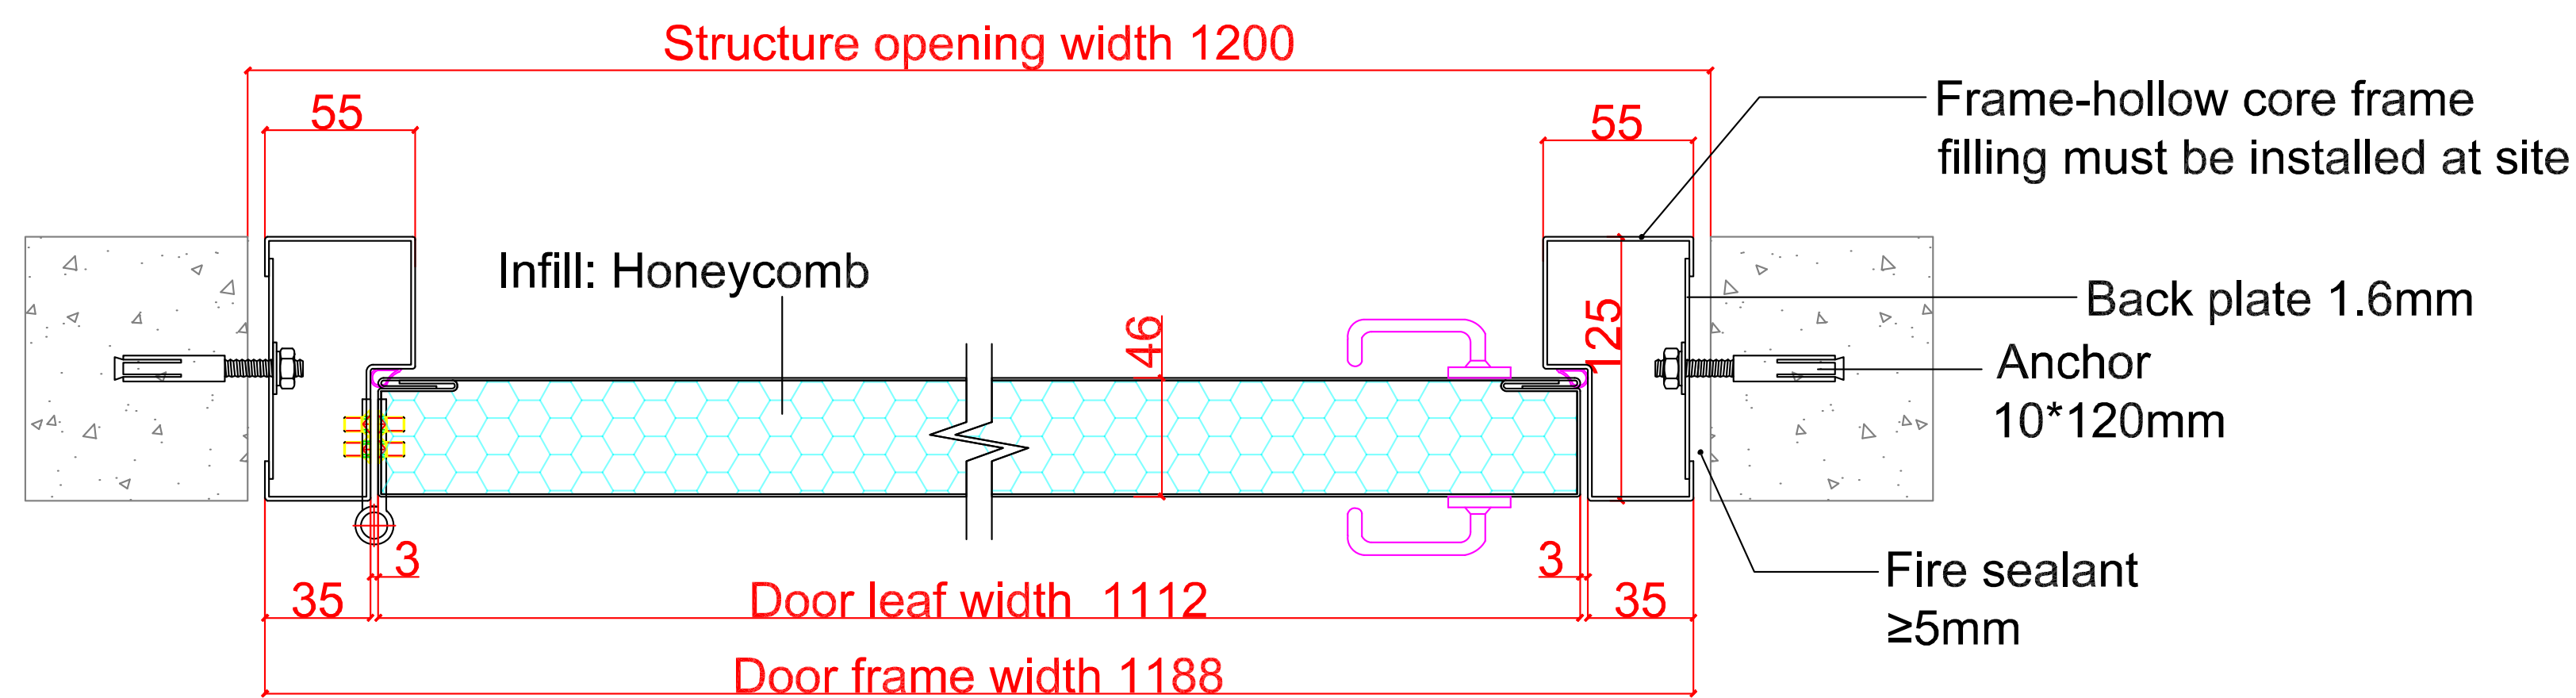


FD13

Fire - resistance time: 120 minutes

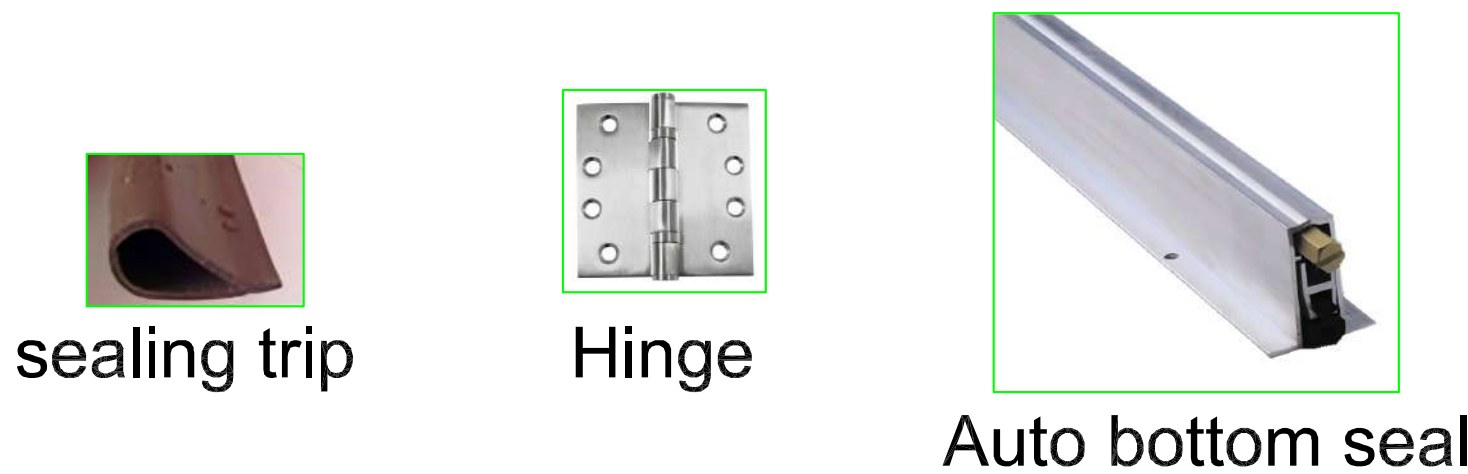

Hardware			
Name	Description	Qty	Remarks
Lock type	solenoid lock	1	
Hinge	4.5*4*3	3	
Door closer	184	1	
Door stop			
Glass	150*400mm	1	
Auto Bottom seal		1	
Smoke seal		1	
Door frame	1.6mm Galvanized steel sheet		
Door leaf	1.2mm Galvanized steel sheet		
Threshold			
Filling	Honeycomb		
Colour			

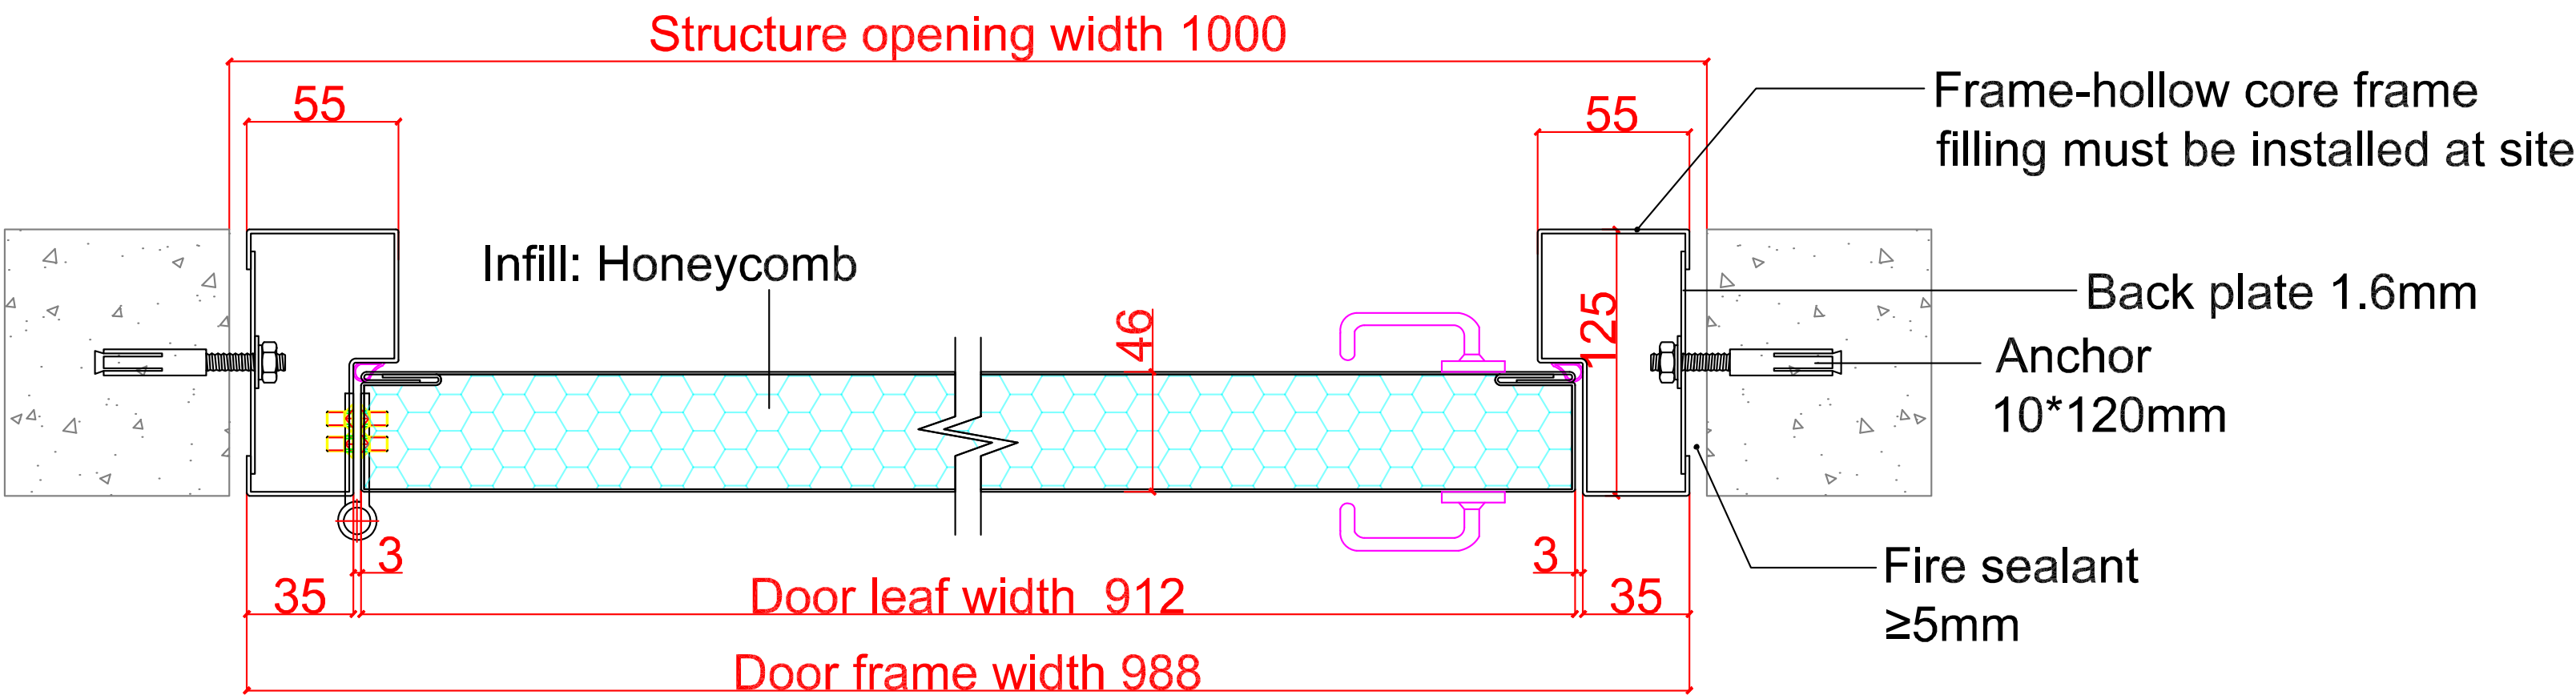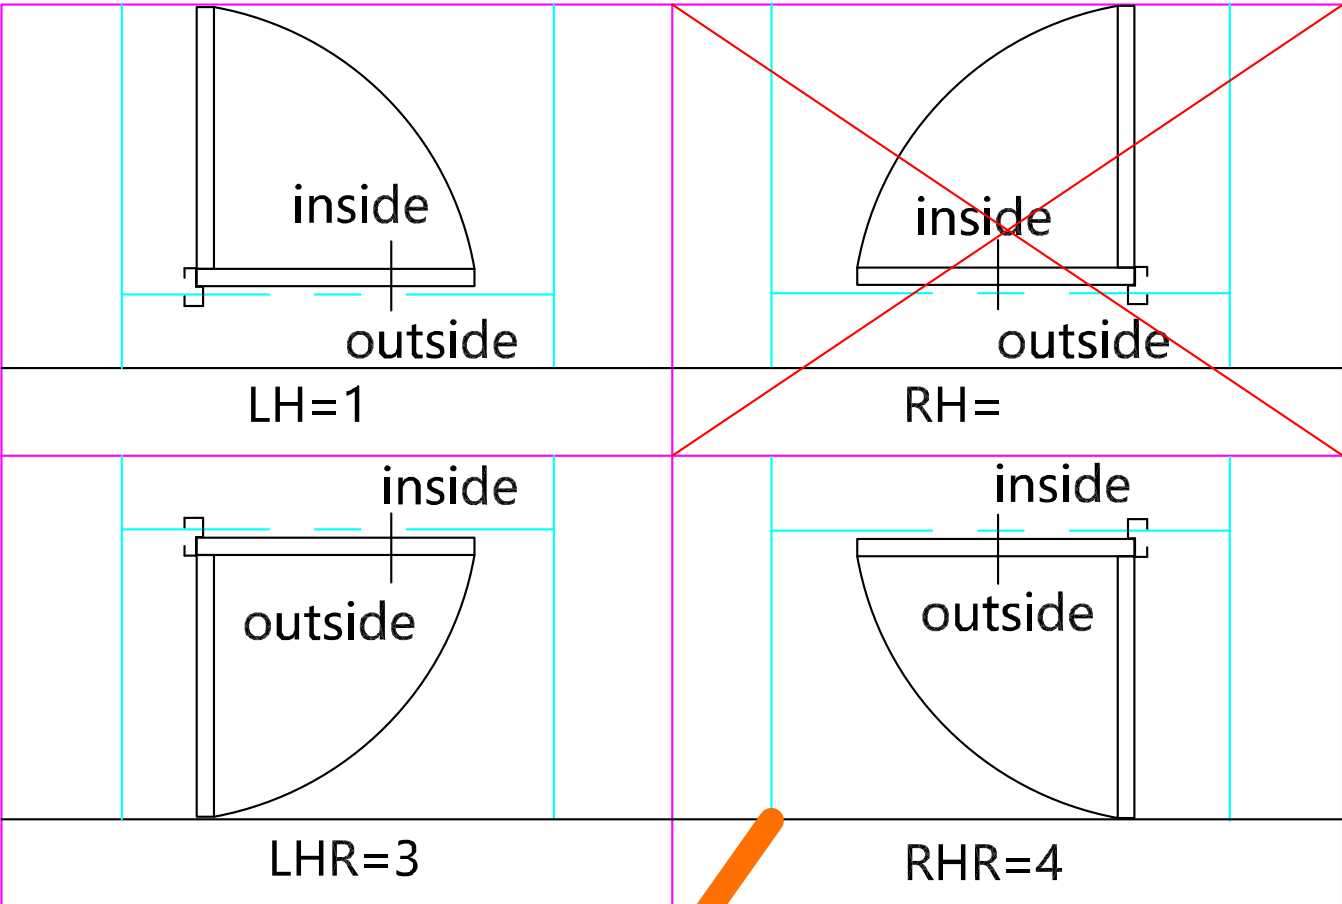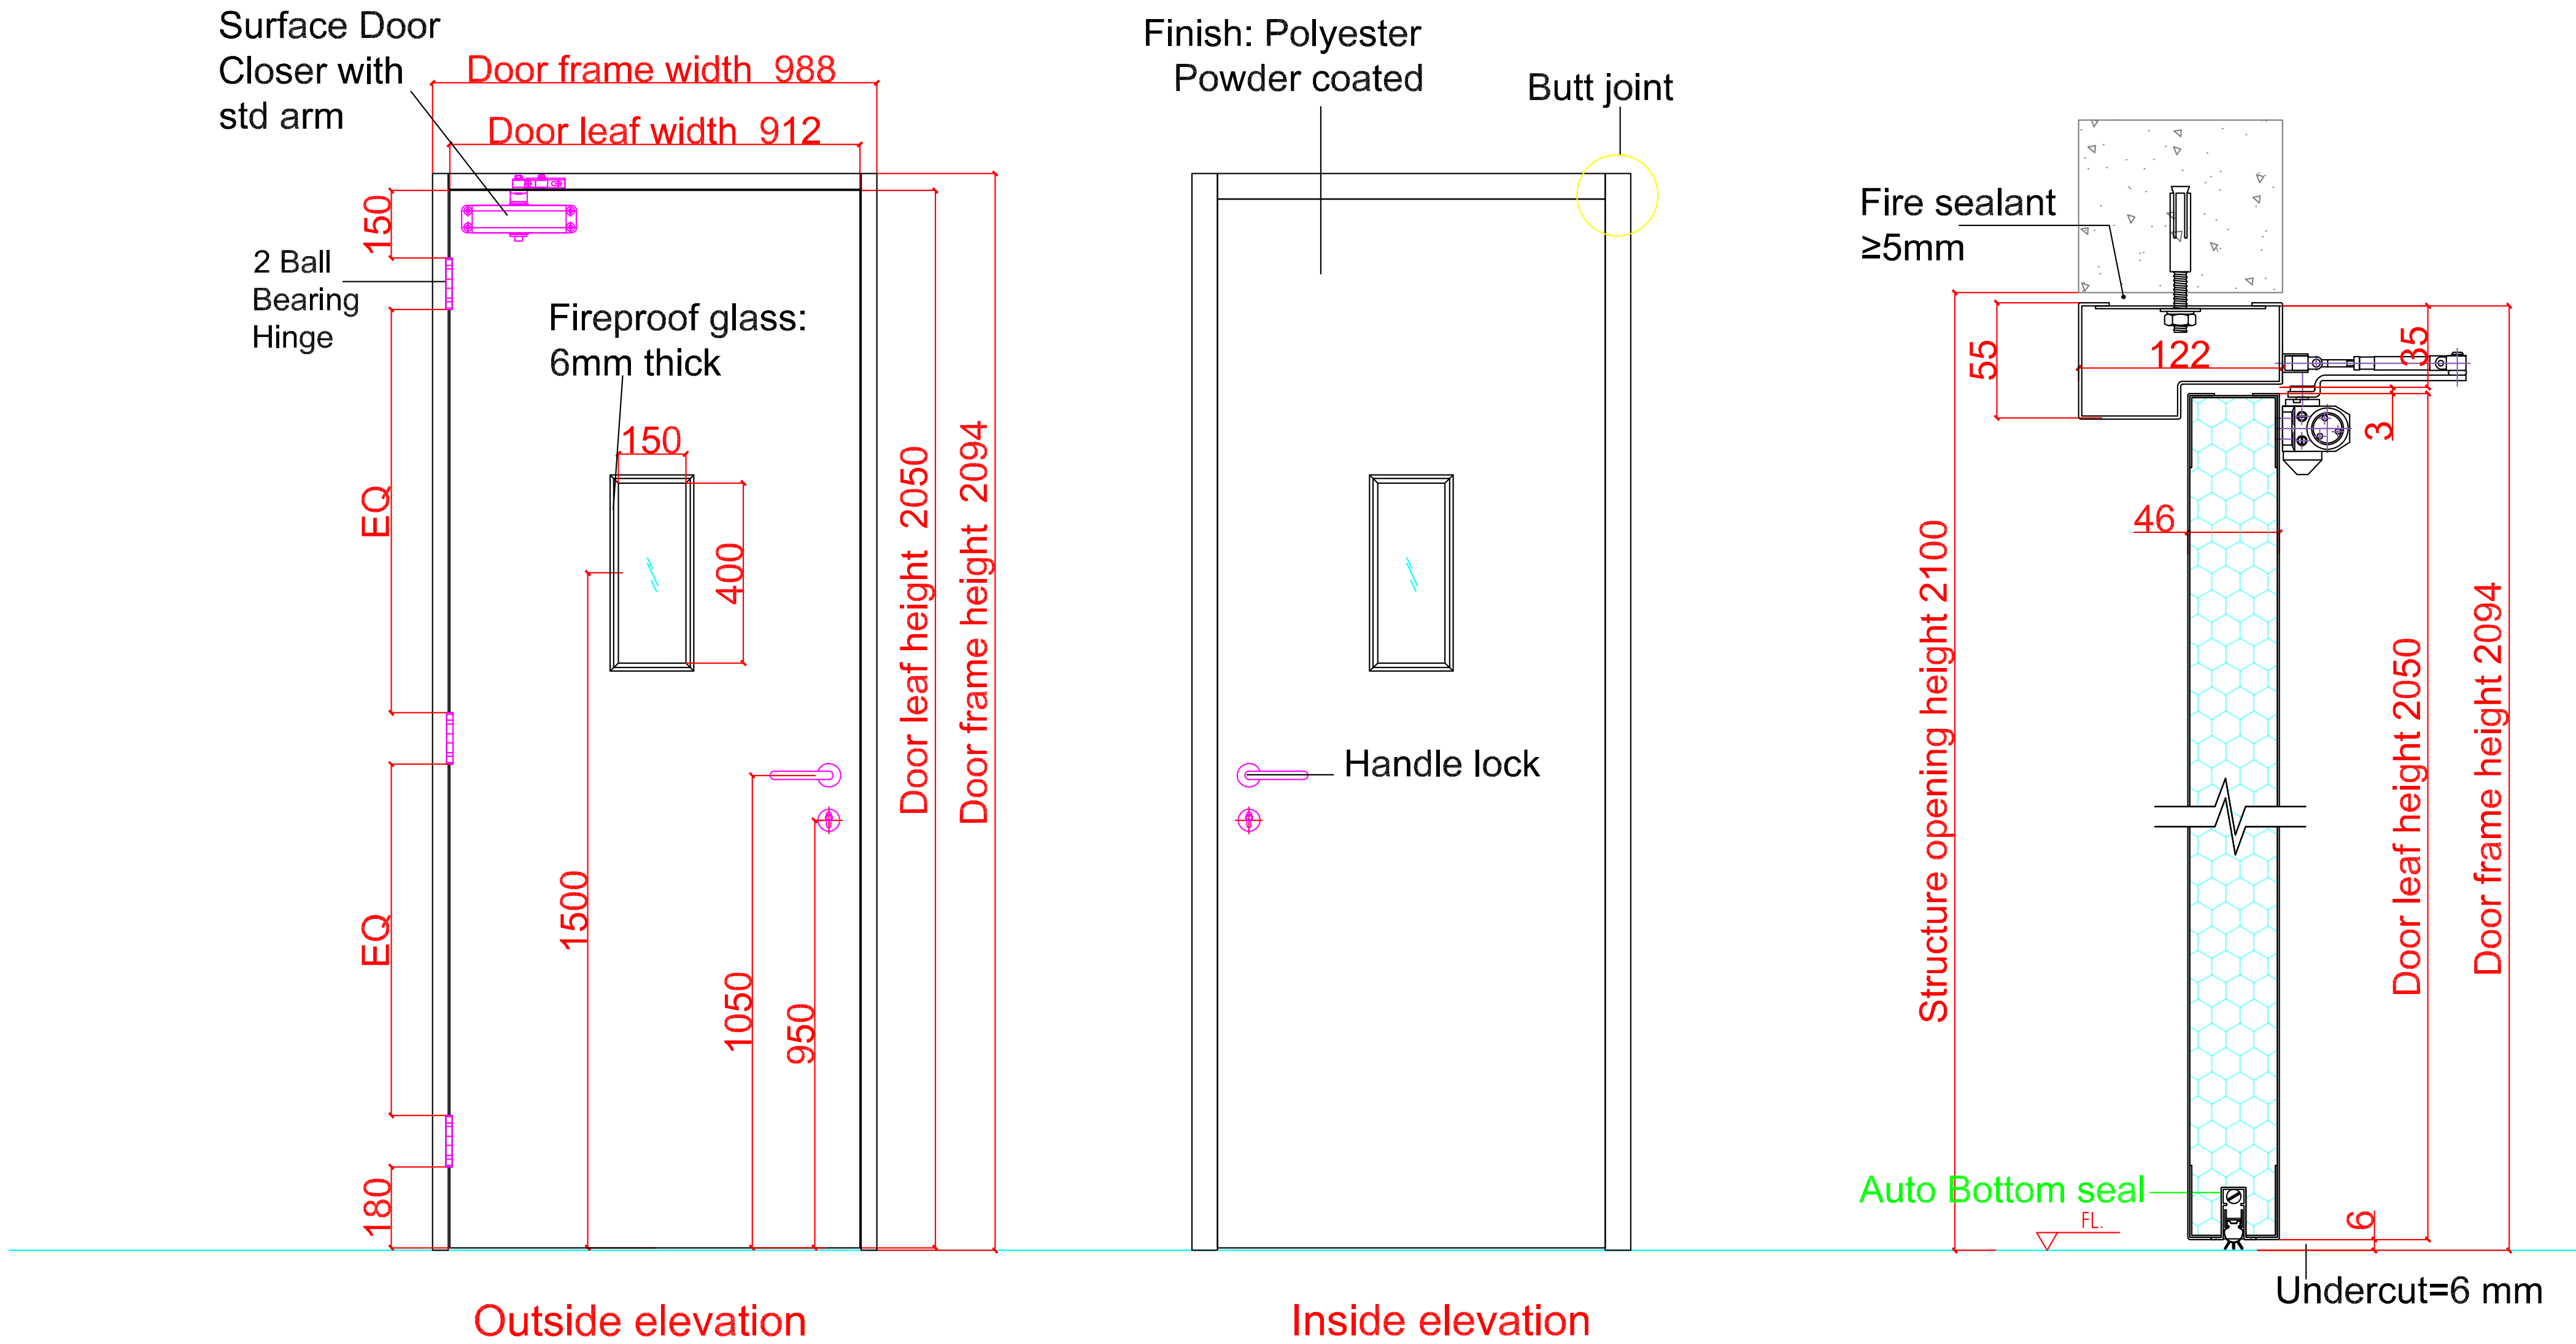


 Shanghai Xunzhong Industry Co., Ltd			
Project name			
By		Drawing title	
Design		Size	
Check		Qty	8
Review		Opening direction	
Approval		Date	2026.05.18
Total Page	34	Page No	13
		Diagram number	


FD14

Fire - resistance time: 120 minutes



Hardware			
Name	Description	Qty	Remarks
Lock type	Deadlock+Flush pull	1	
Hinge	4.5*4*3	3	
Smoke seal		1	
Door frame	1.6mm Galvanized steel sheet		
Door leaf	1.2mm Galvanized steel sheet		
Threshold			
Filling	Honeycomb		
Colour			
Fire sealant	≥5mm		

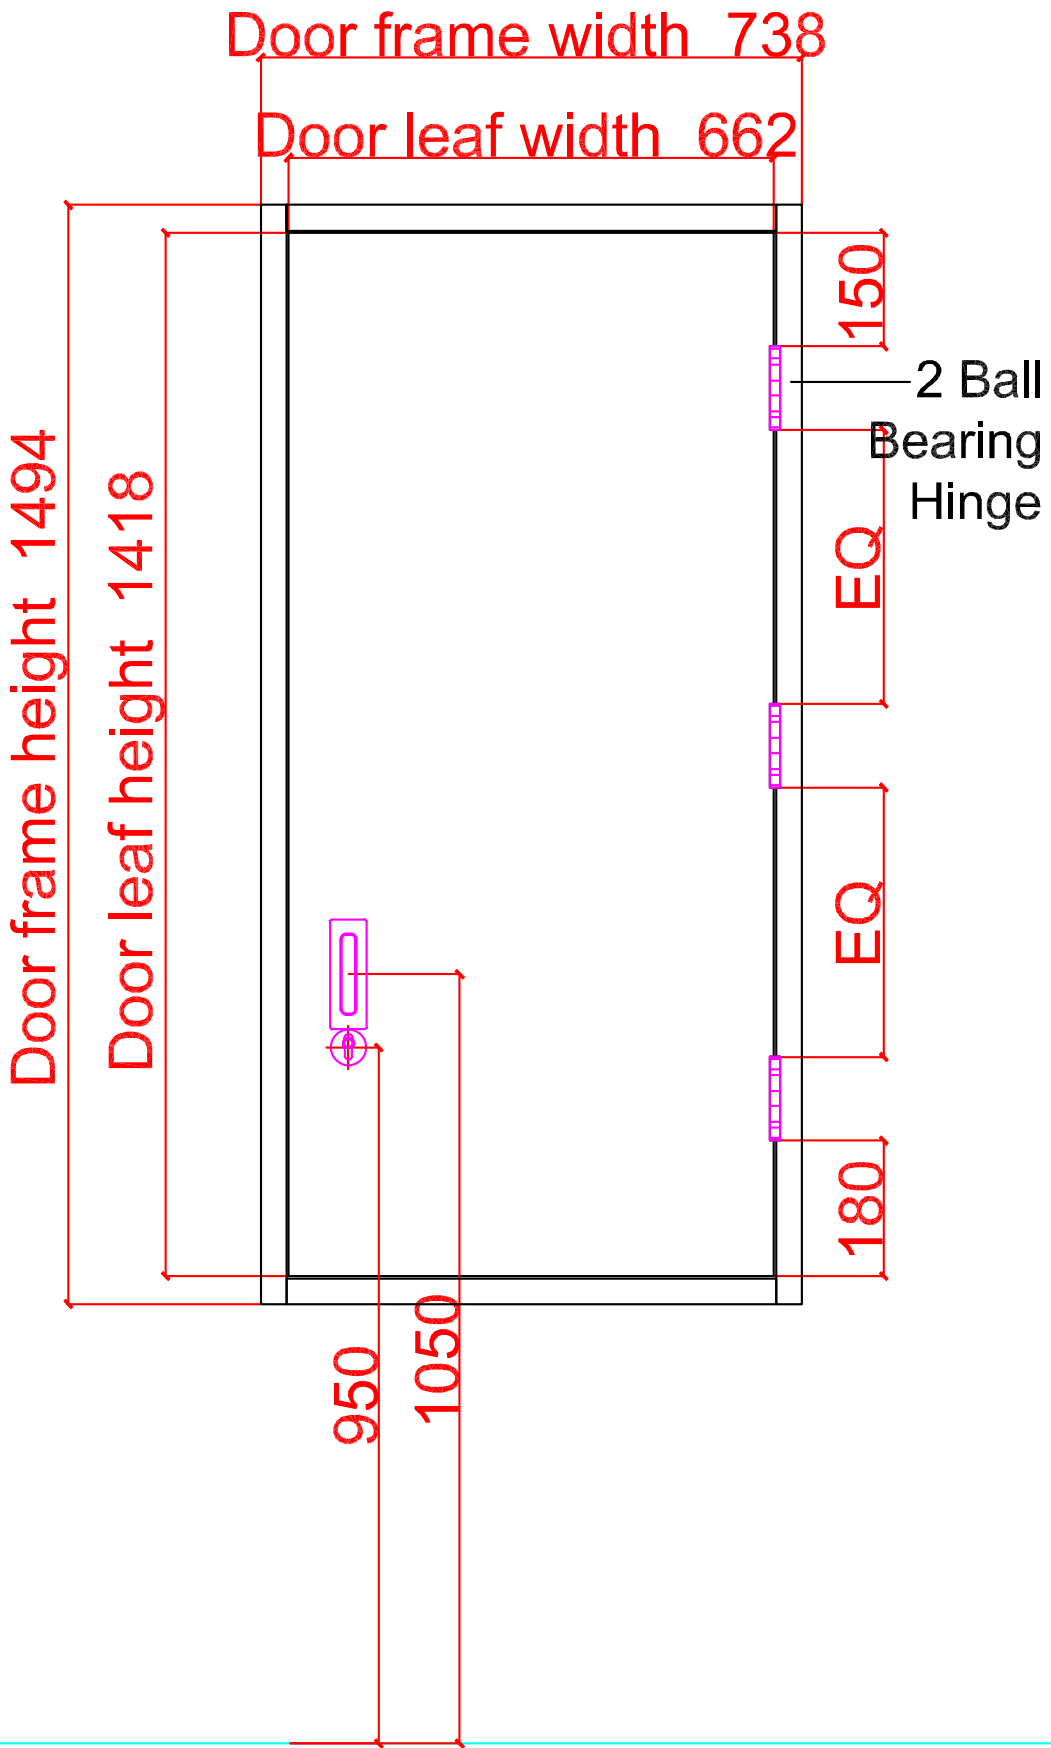

Outside elevation

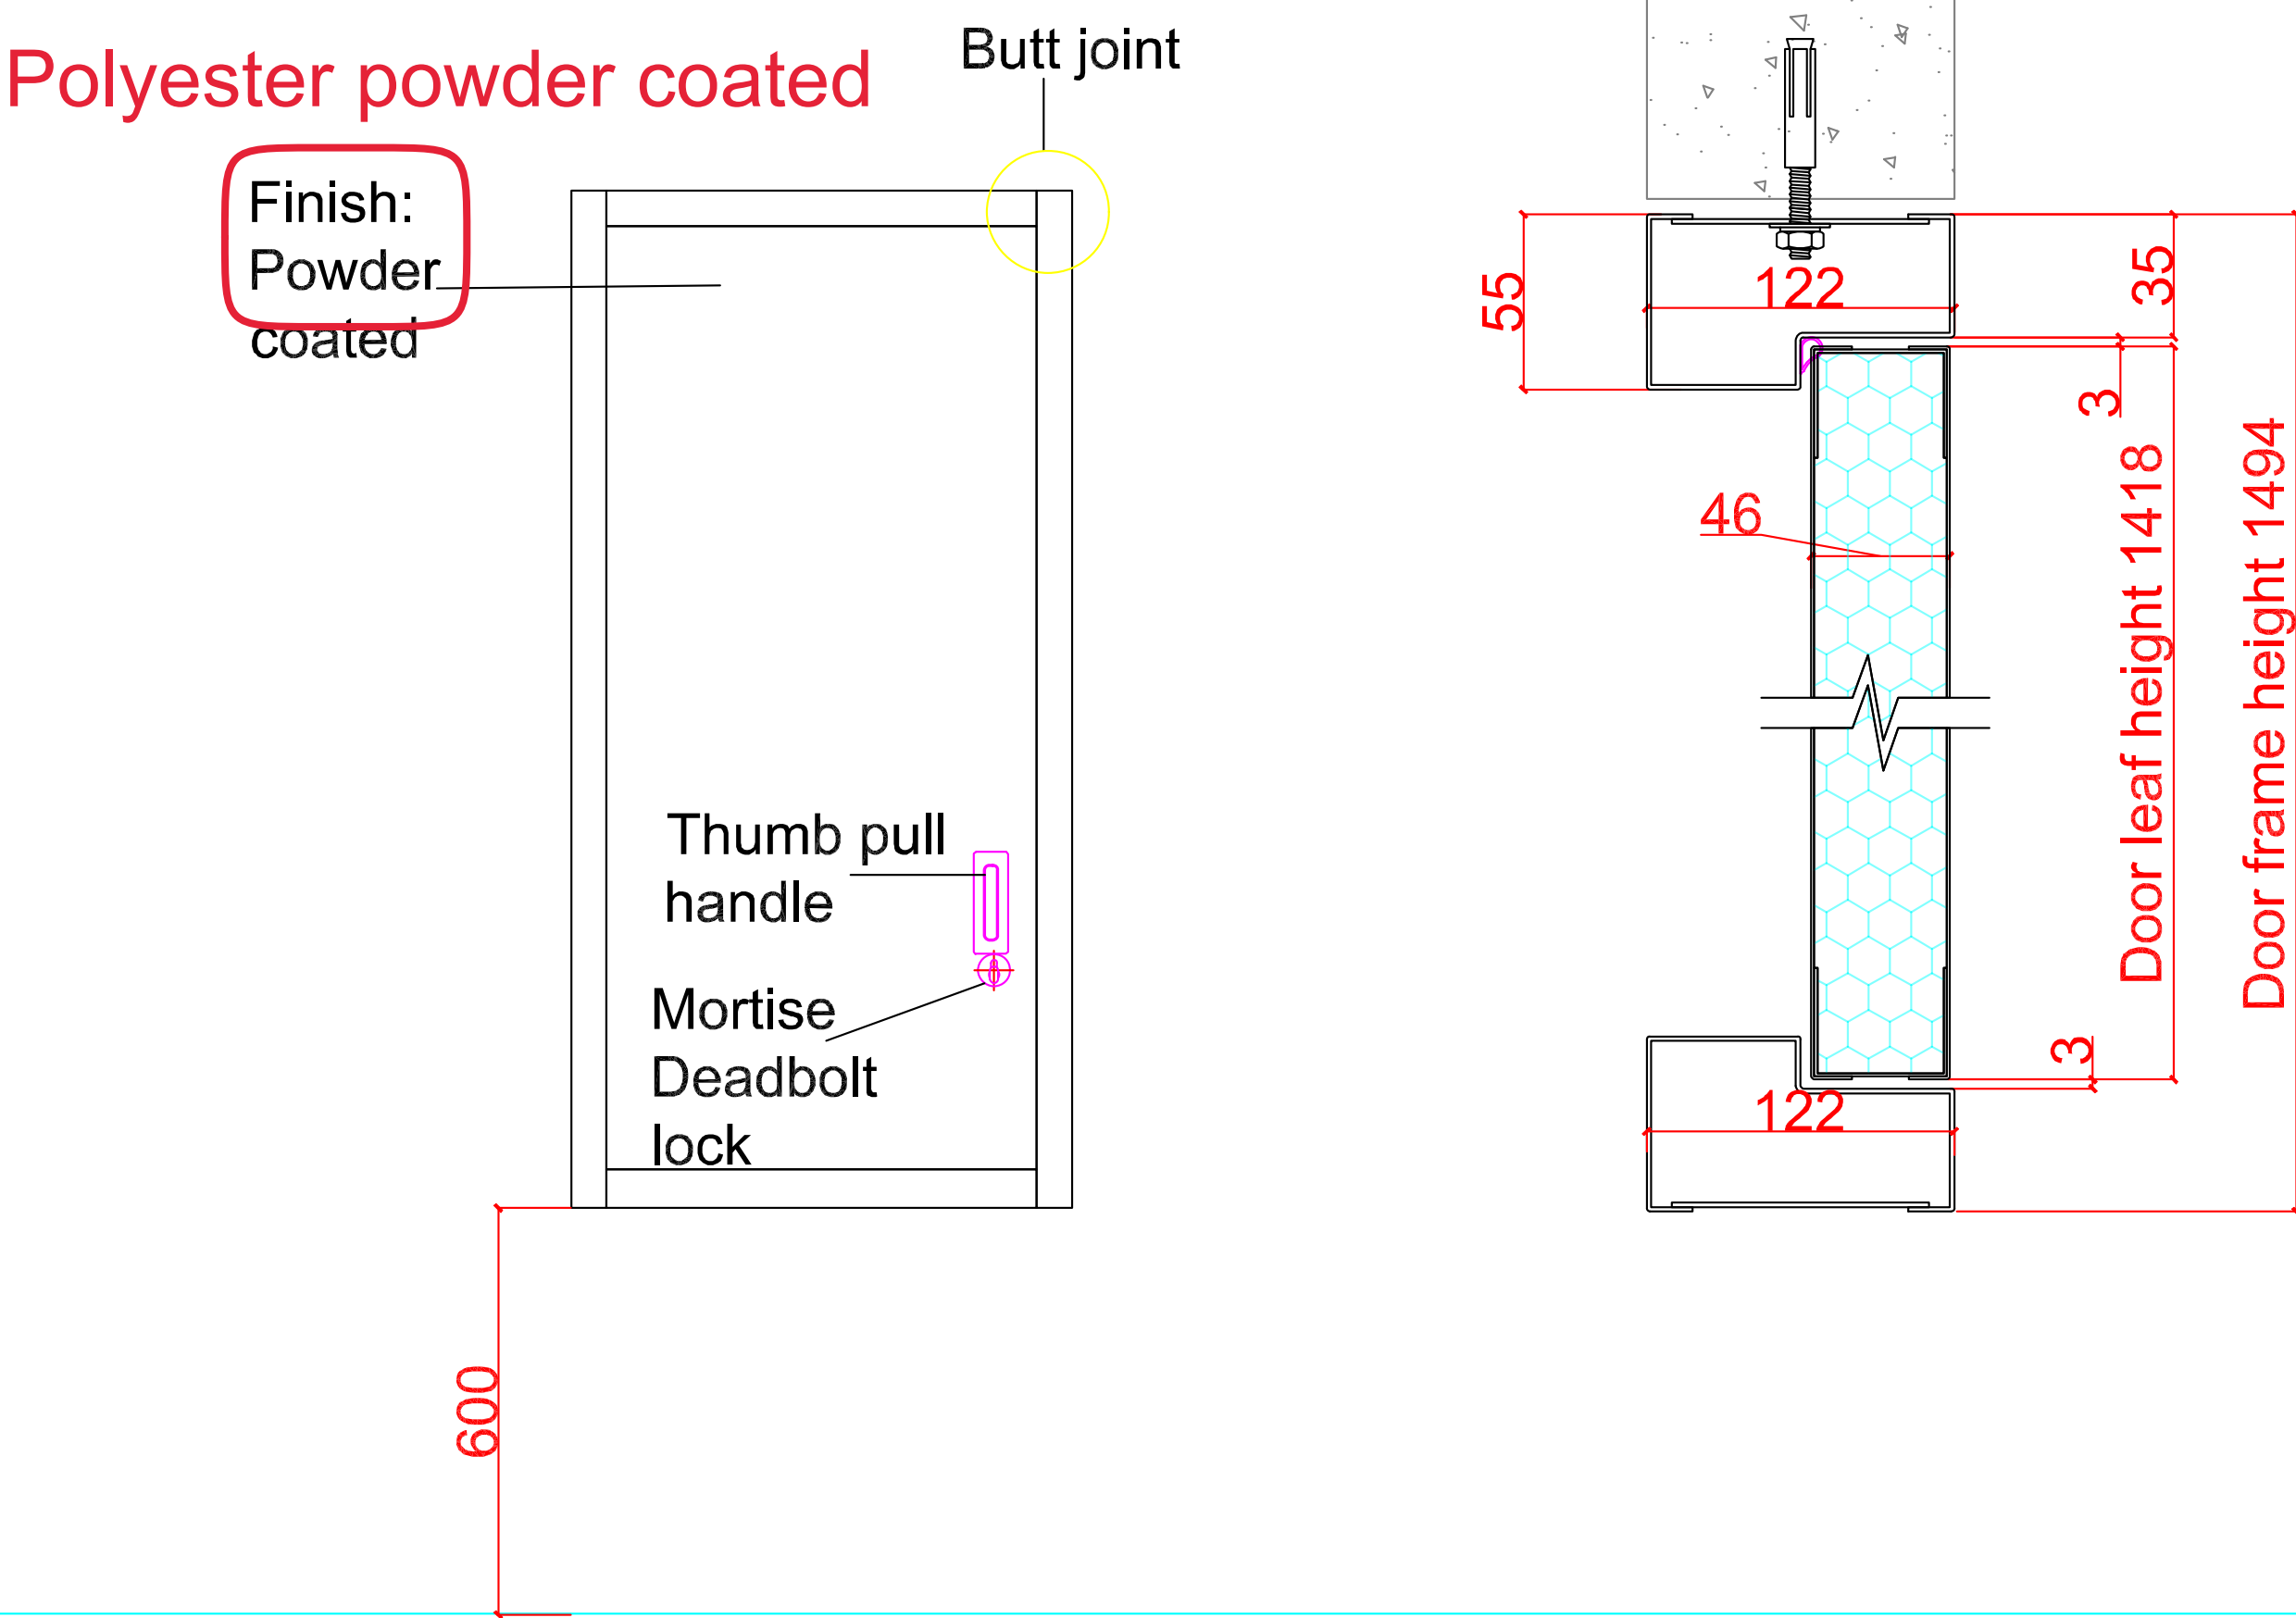

Inside elevation

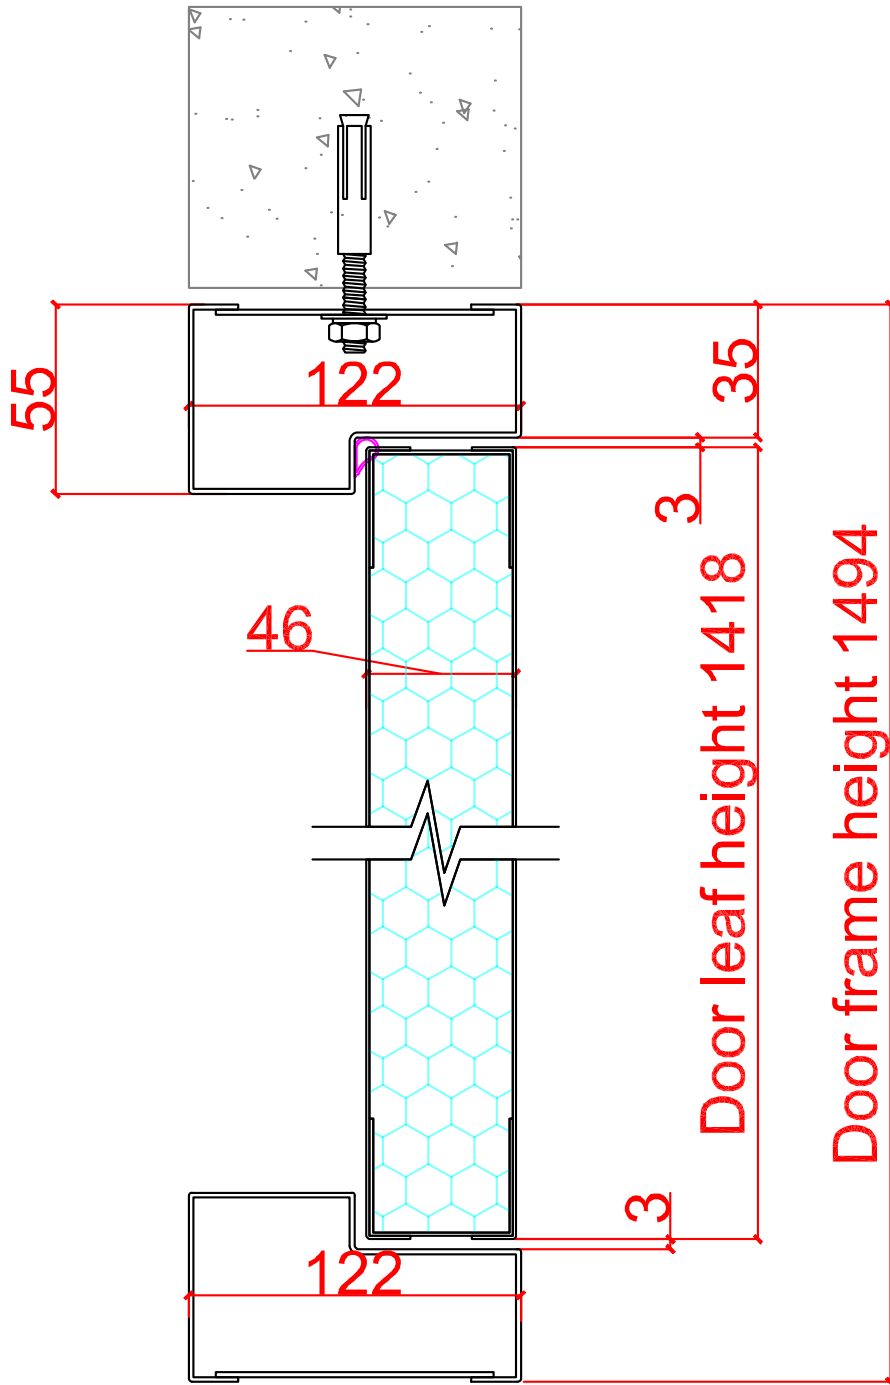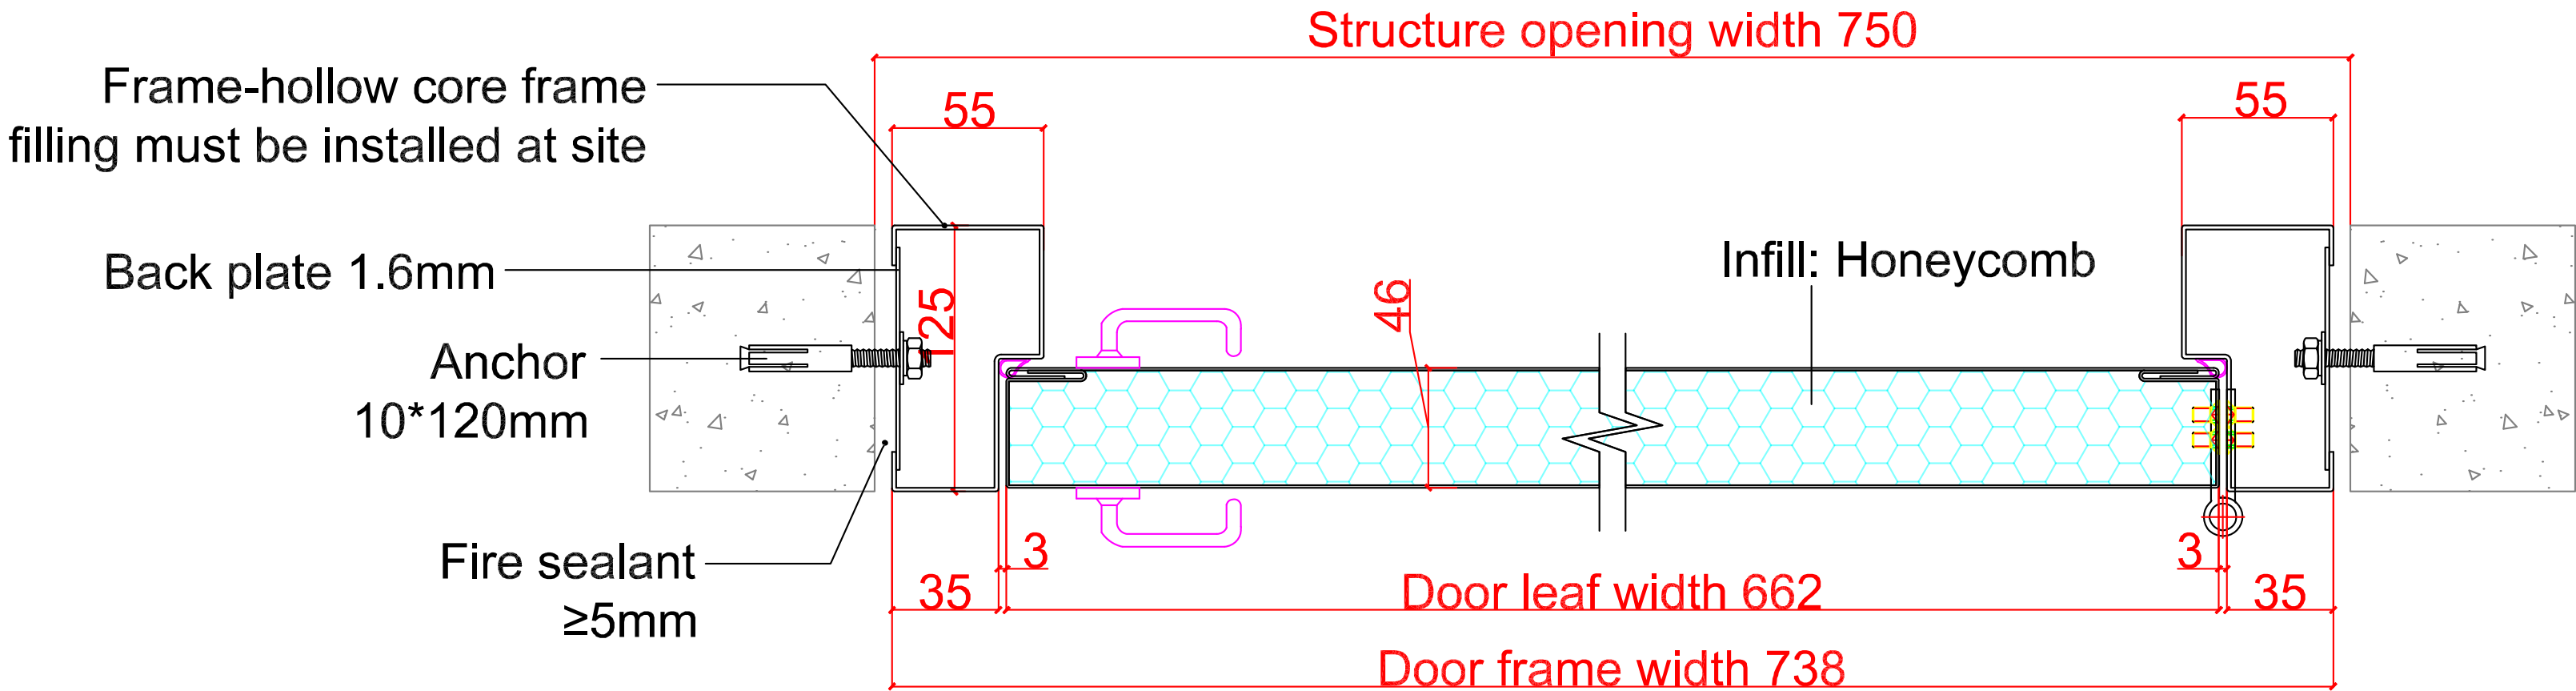

Hinge




sealing trip



Deadlock



Thumb pull handle

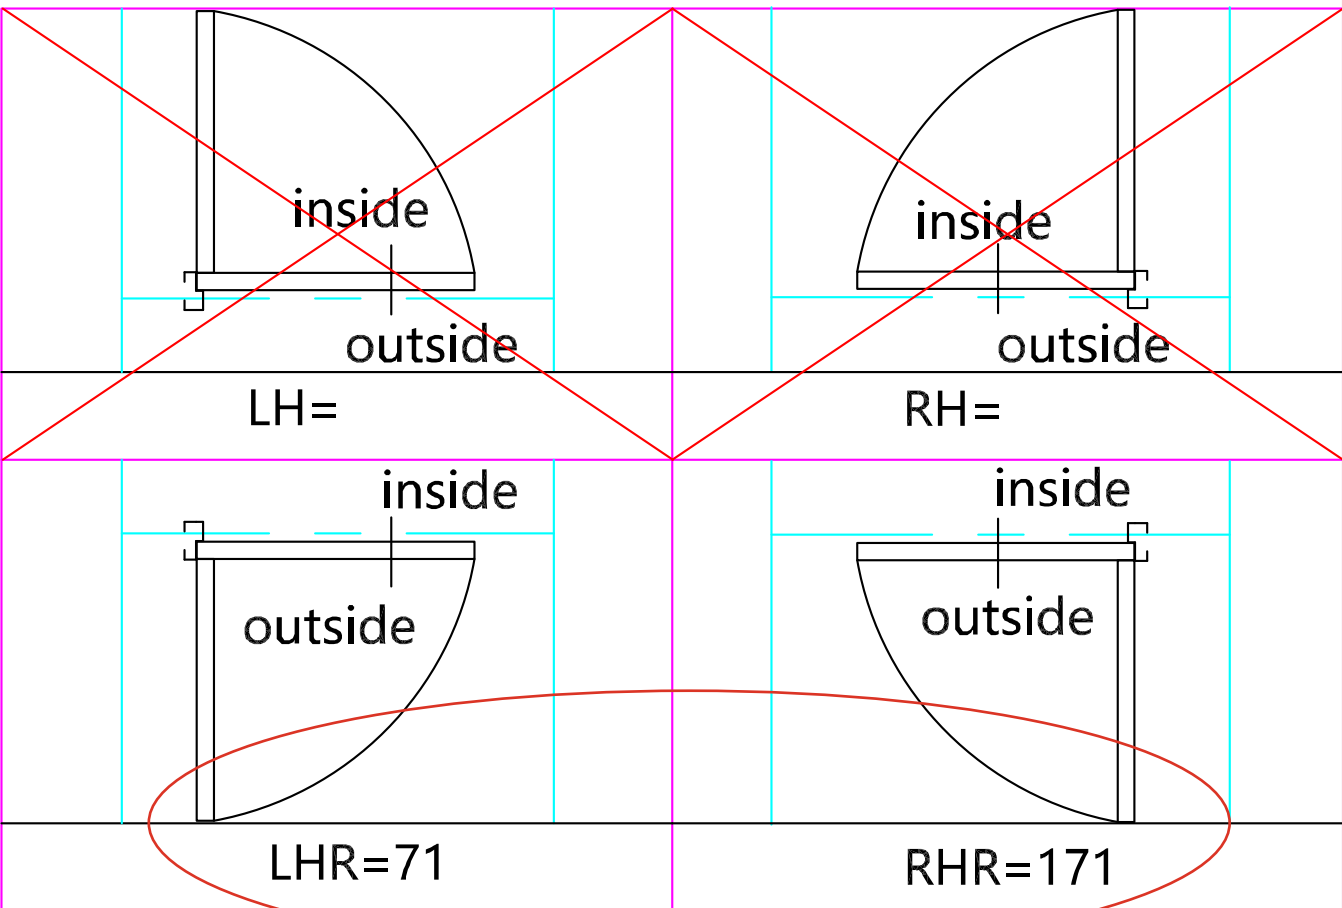

FD14 LHR = 72, RHR = 170




Shanghai Xunzhong Industry Co., Ltd

Project name


By		Drawing title	
Design		Size	
Check		Qty	242
Review		Opening direction	
Approval		Date	2026.05.18
		Page No	14
Total Page	34	Diagram number	

FD15



Fire - resistance time: 120 minutes

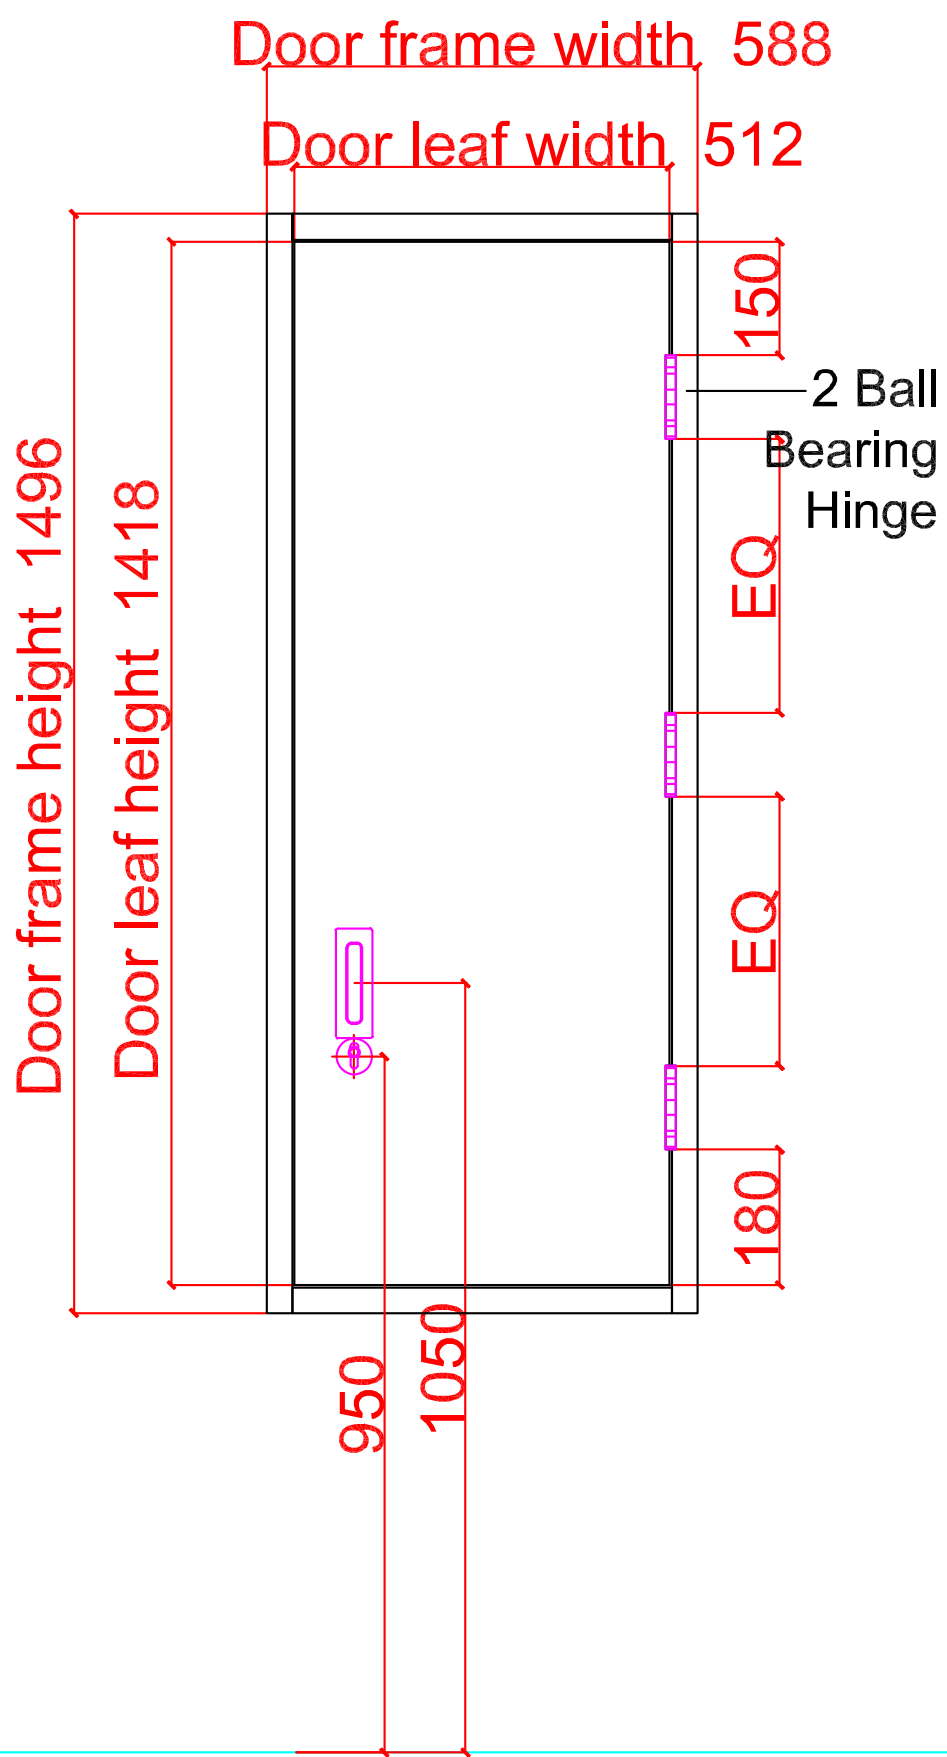

Outside elevation

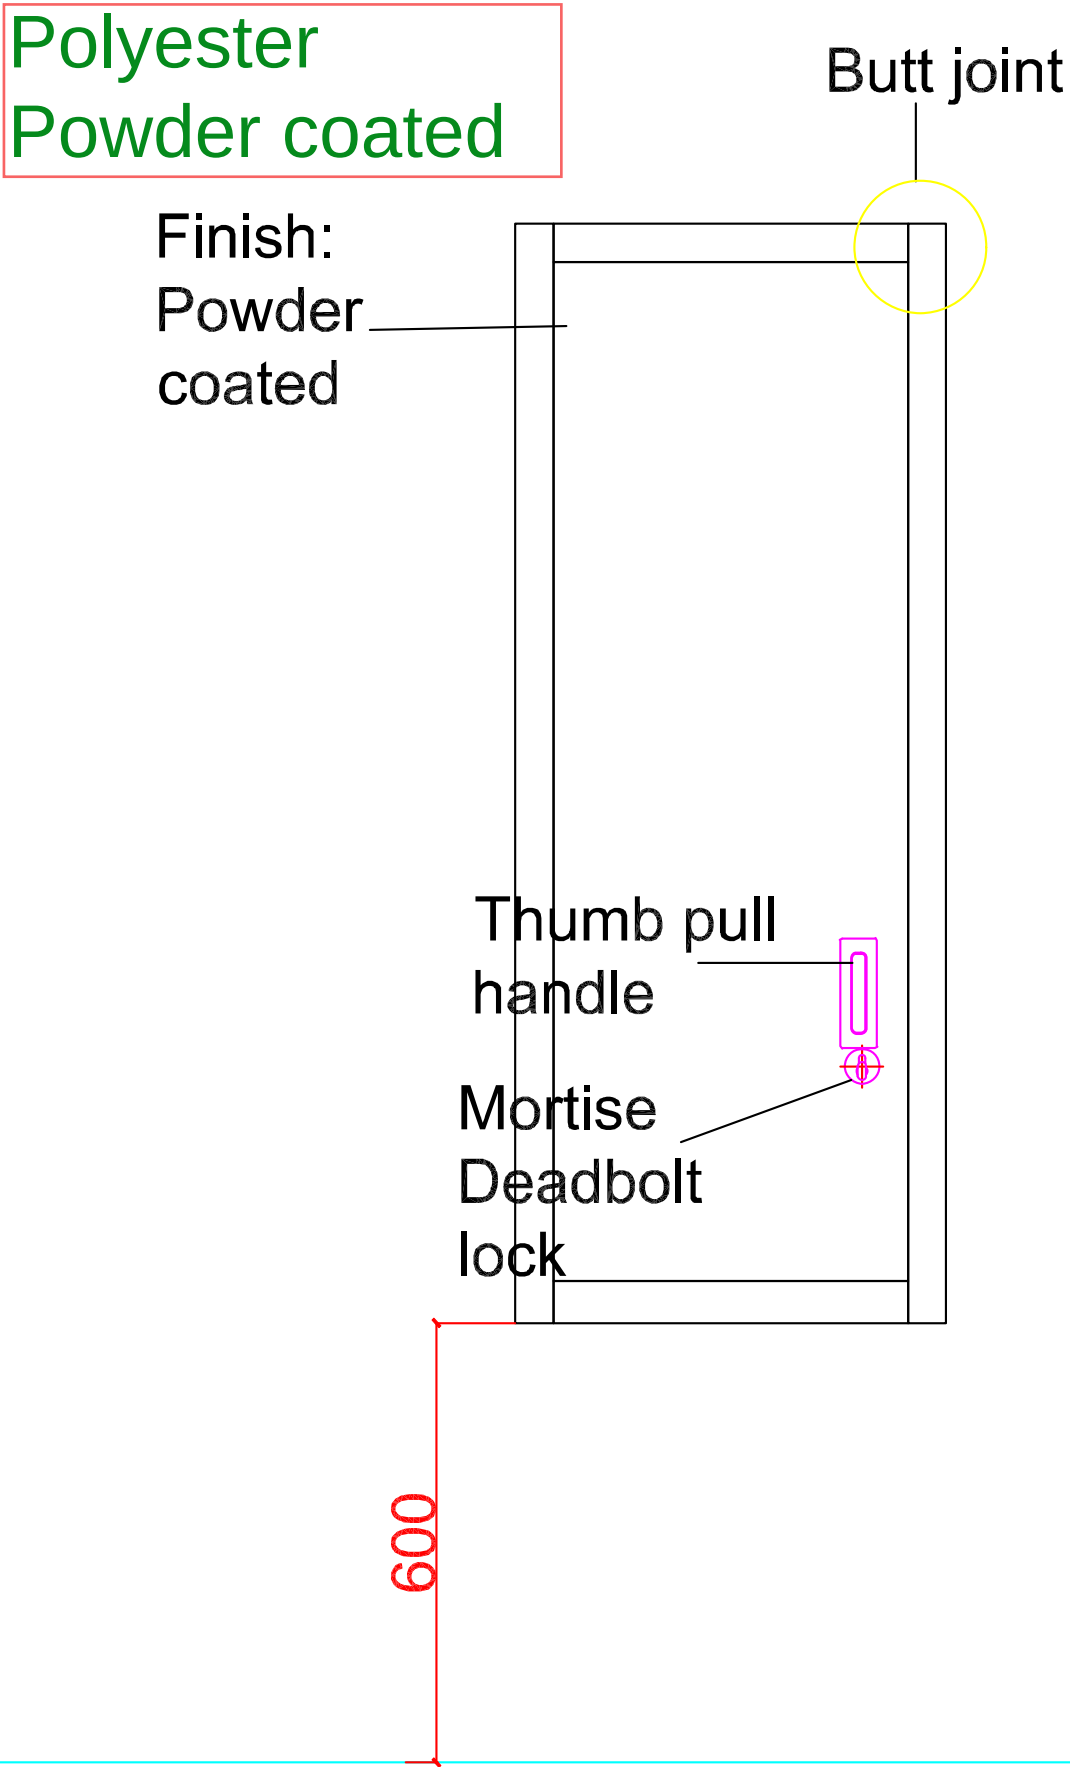

Inside elevation

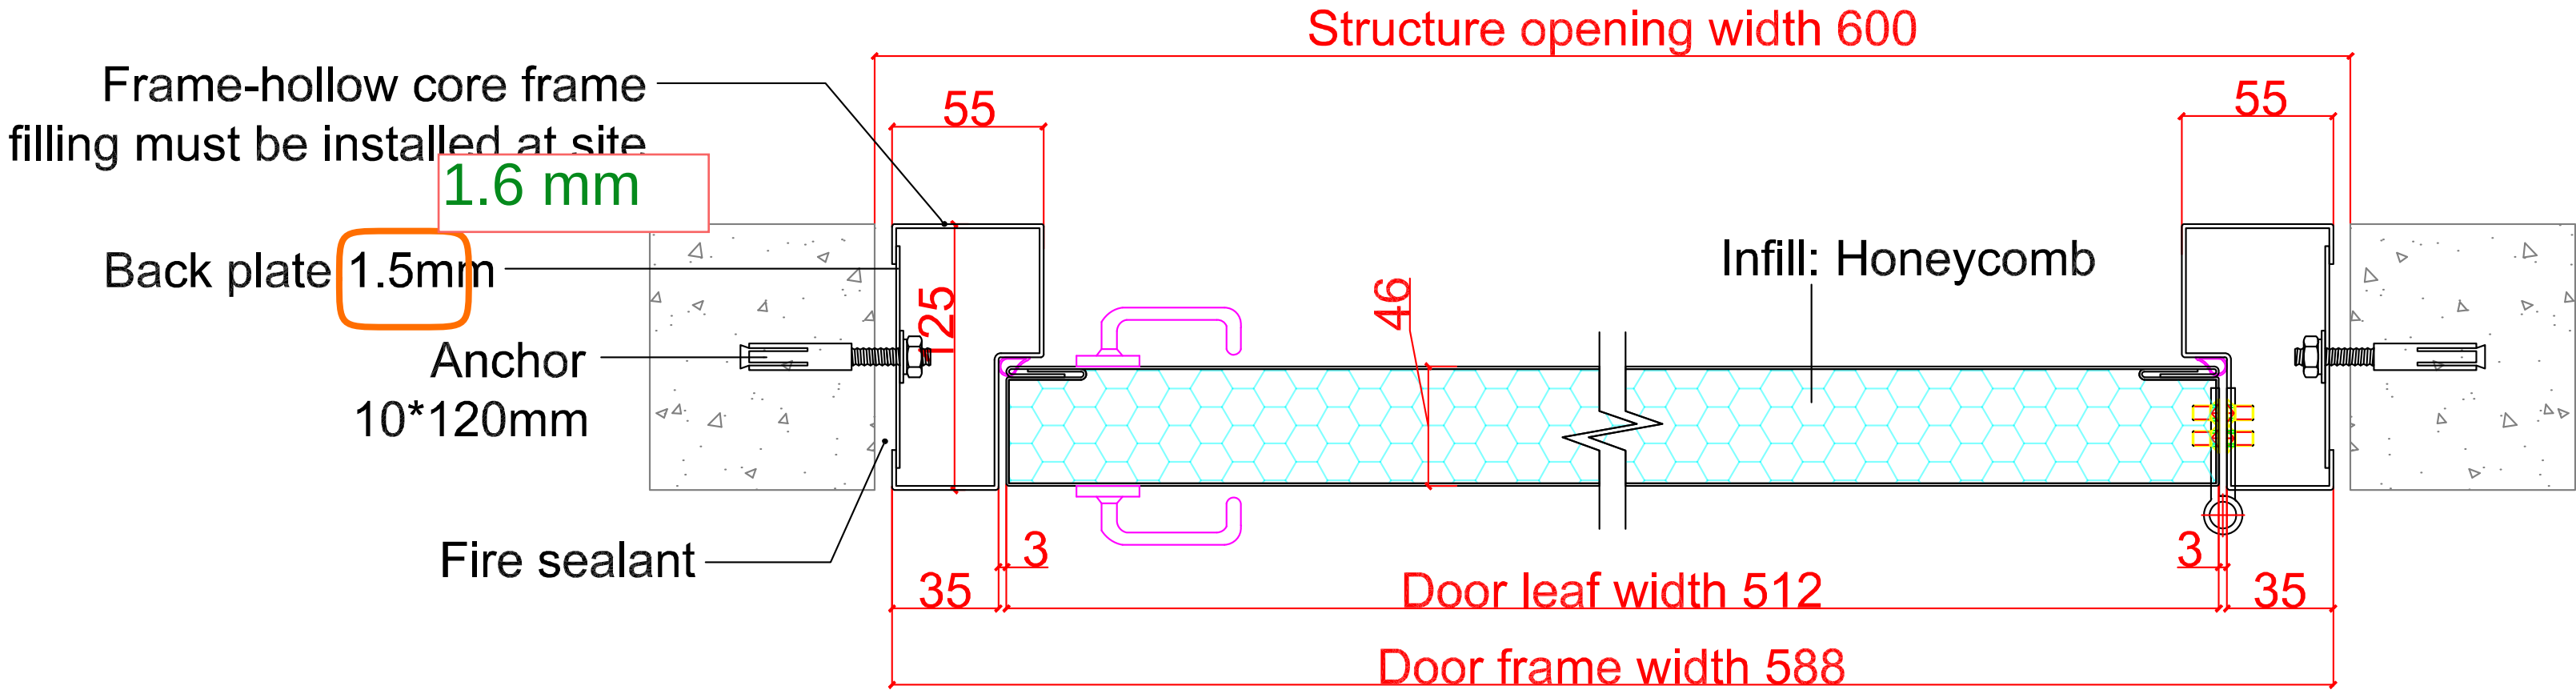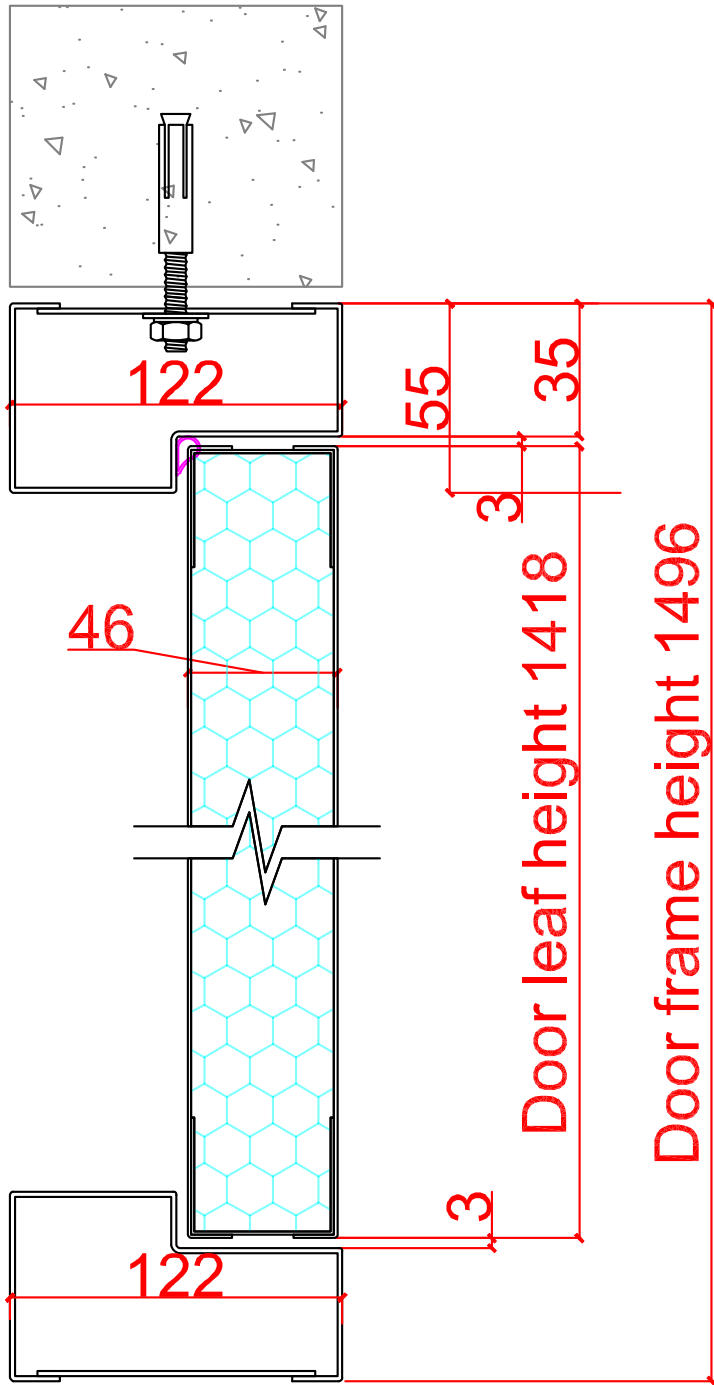

Hinge



sealing trip




Deadlock



Thumb pull handle

Hardware			
Name	Description	Qty	Remarks
Lock type	Deadlock+Flush pull	1	
Hinge	4.5*4*3	3	
Smoke seal		1	
Door frame	1.6mm Galvanized steel sheet		
Door leaf	1.2mm Galvanized steel sheet		
Threshold			
Filling	Honeycomb		
Colour			

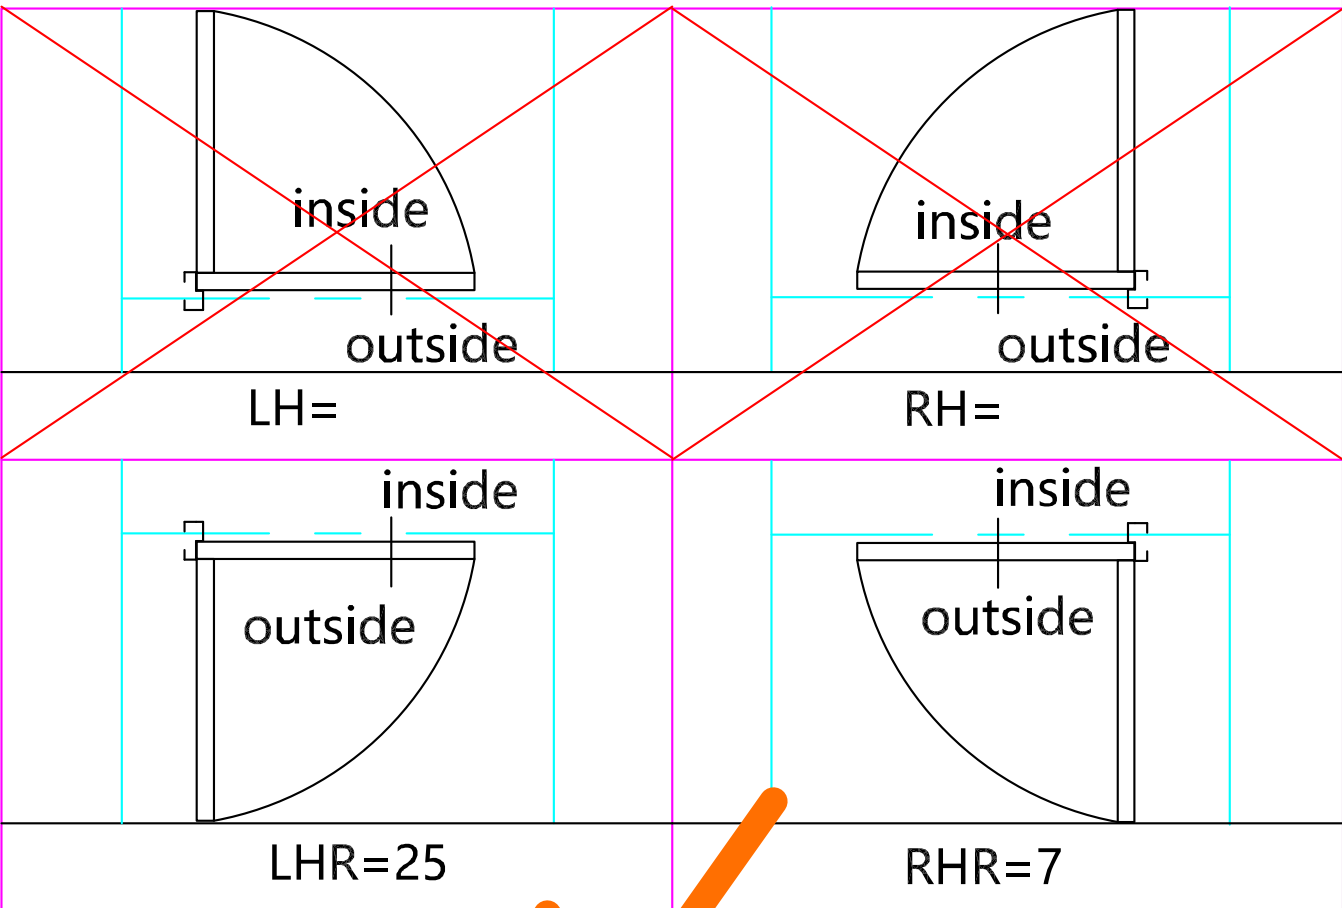


Shanghai Xunzhong Industry Co., Ltd

Project name


By		Drawing title	
Design		Size	
Check		Qty	32
Review		Opening direction	
Approval		Date	2026.05.18
		Page No	15
Total Page	34	Diagram number	

FD16



Fire - resistance time: 120 minutes

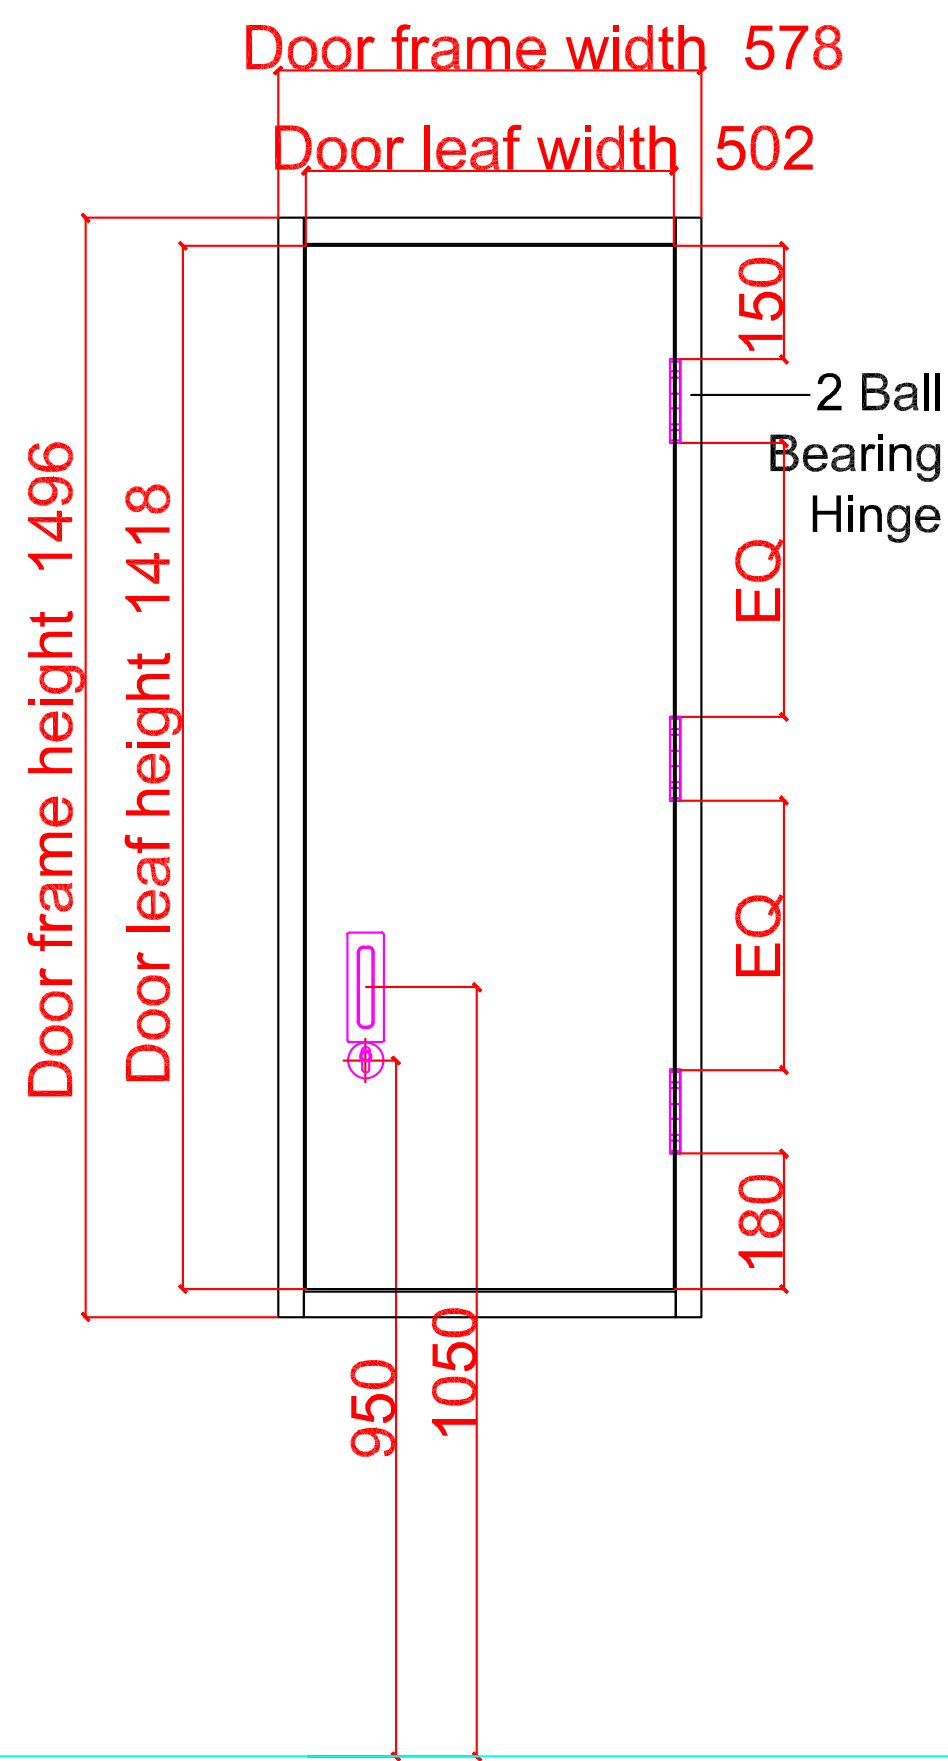

Outside elevation

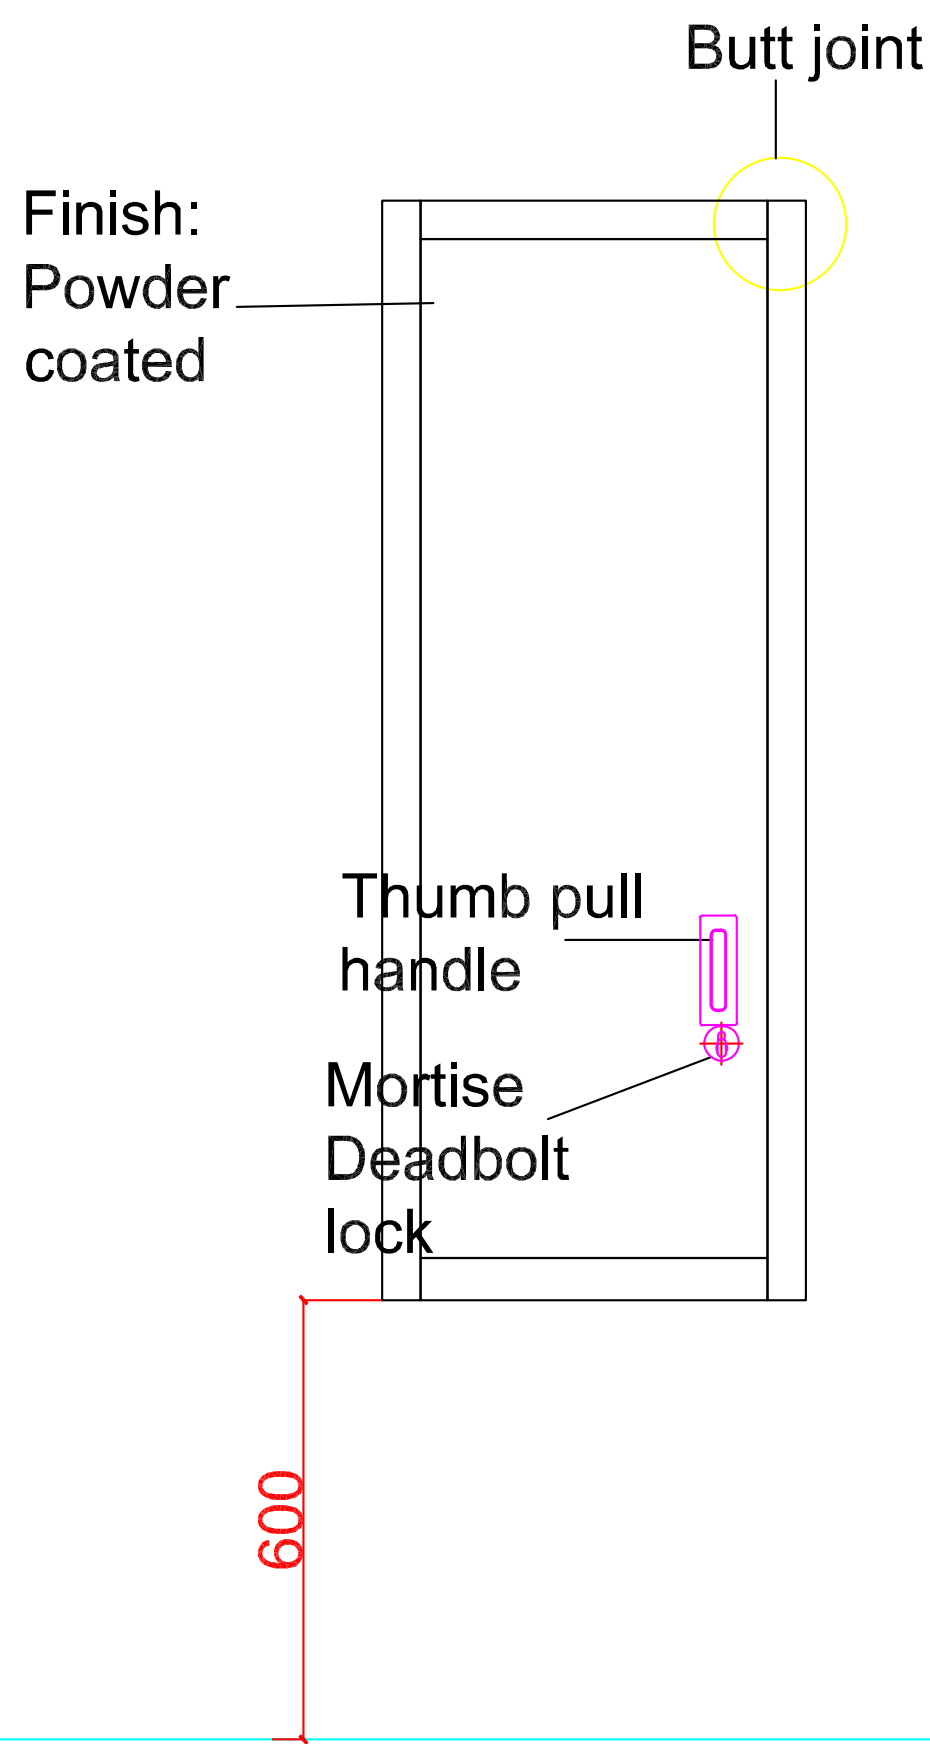

Inside elevation

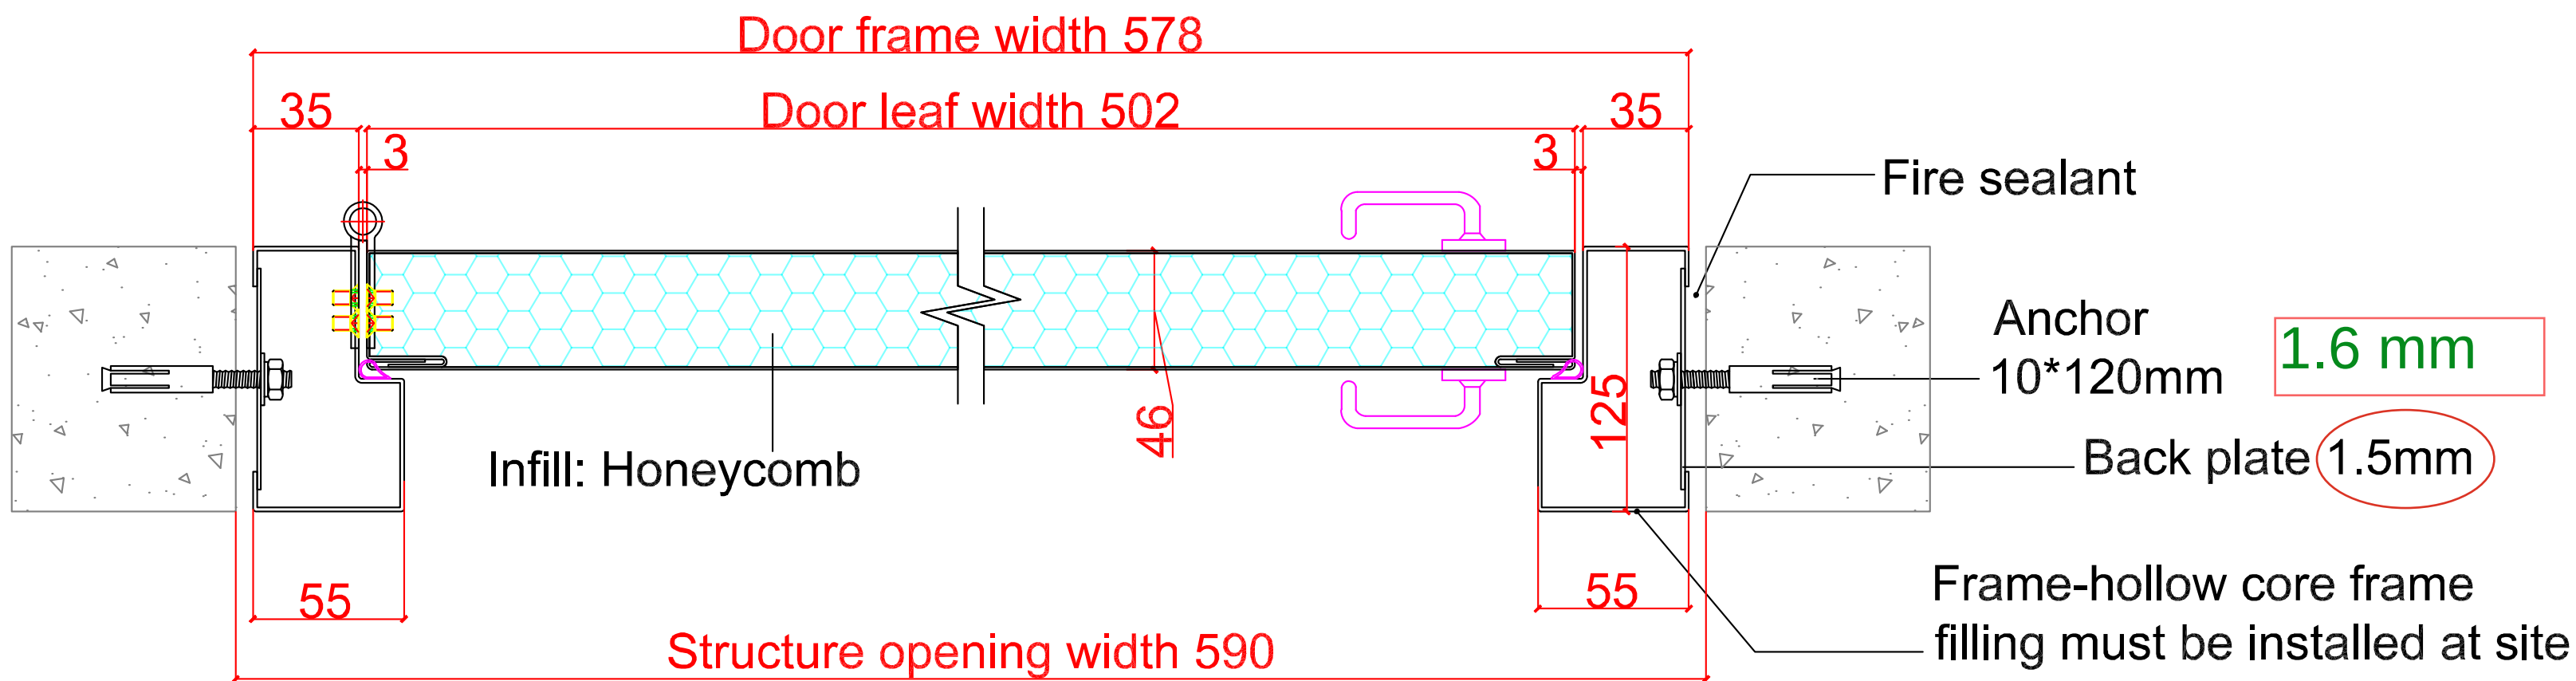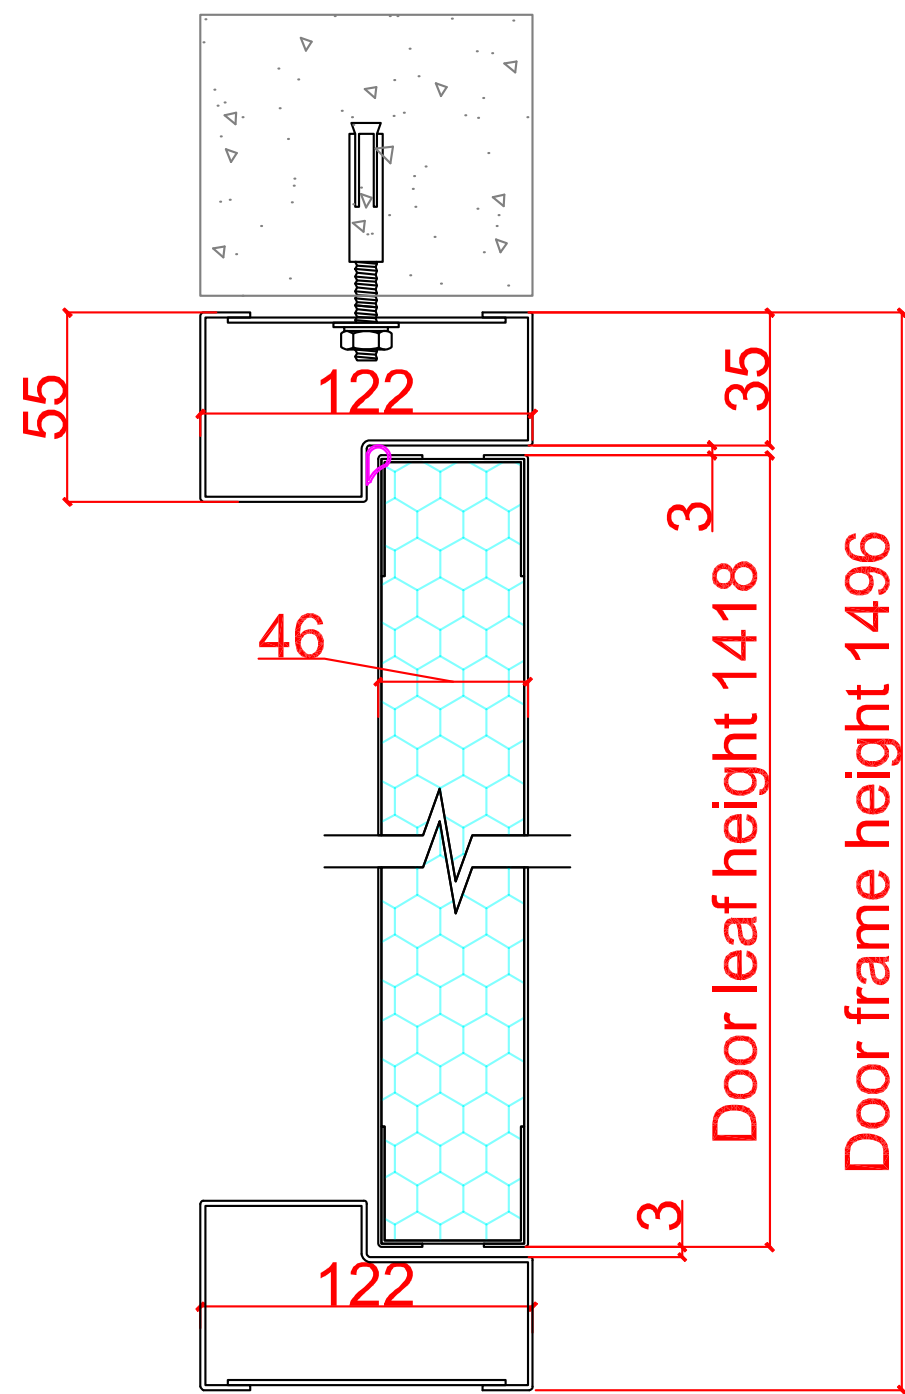

Hinge



sealing trip




Deadlock



Thumb pull handle

Hardware			
Name	Description	Qty	Remarks
Lock type	Deadlock+Flush pull	1	
Hinge	4.5*4*3	3	
Smoke seal		1	
Door frame	1.6mm Galvanized steel sheet		
Door leaf	1.2mm Galvanized steel sheet		
Threshold			
Filling	Honeycomb		
Colour			

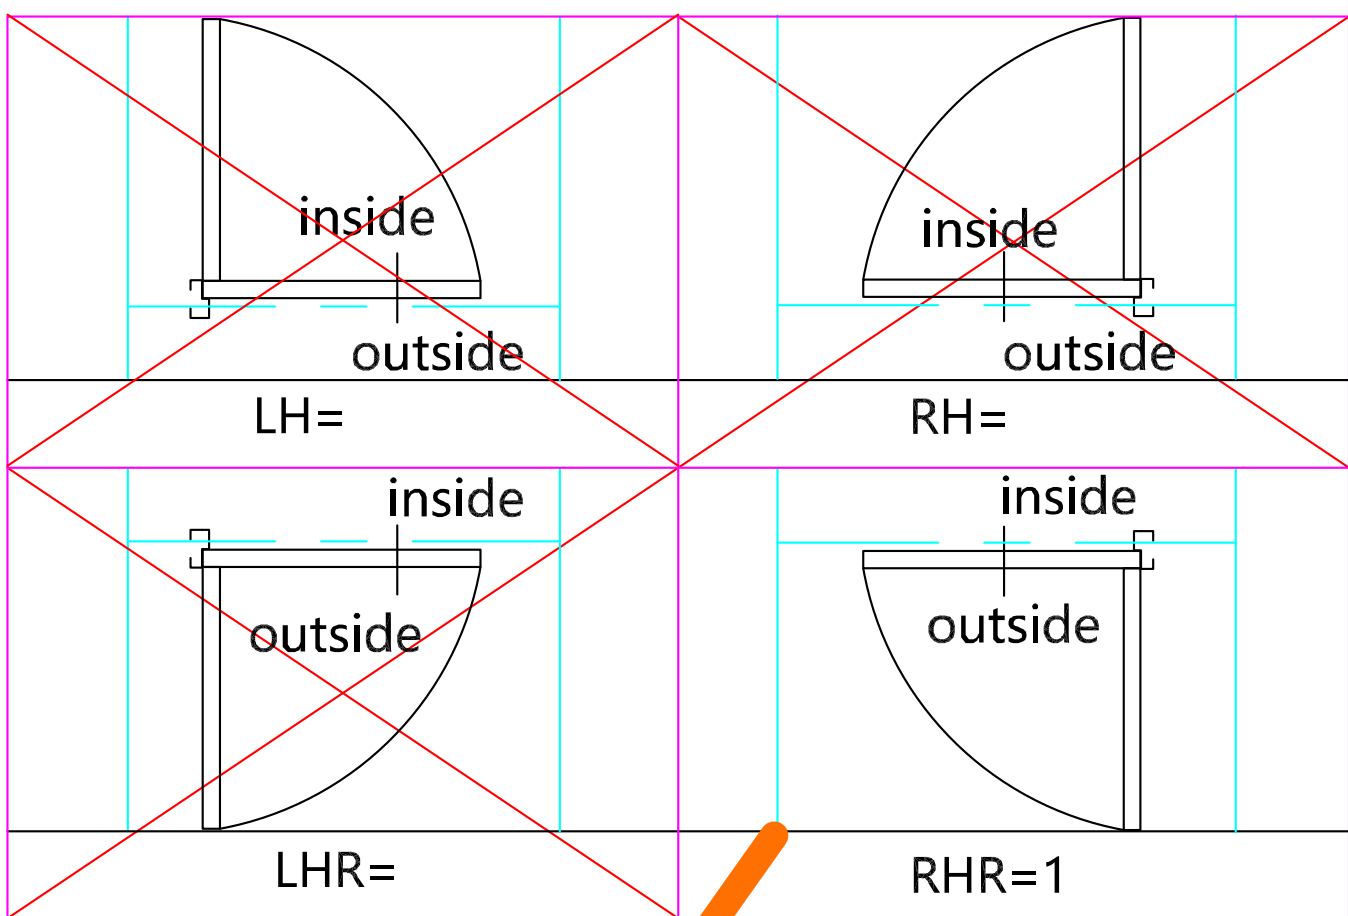


 Shanghai Xunzhong Industry Co., Ltd

Project name

By		Drawing title	
Design		Size	
Check		Qty	1
Review		Opening direction	
Approval		Date	2026.05.18
		Page No	15
Total Page	34	Diagram number	


FD9

Fire - resistance time: 120/30 minutes

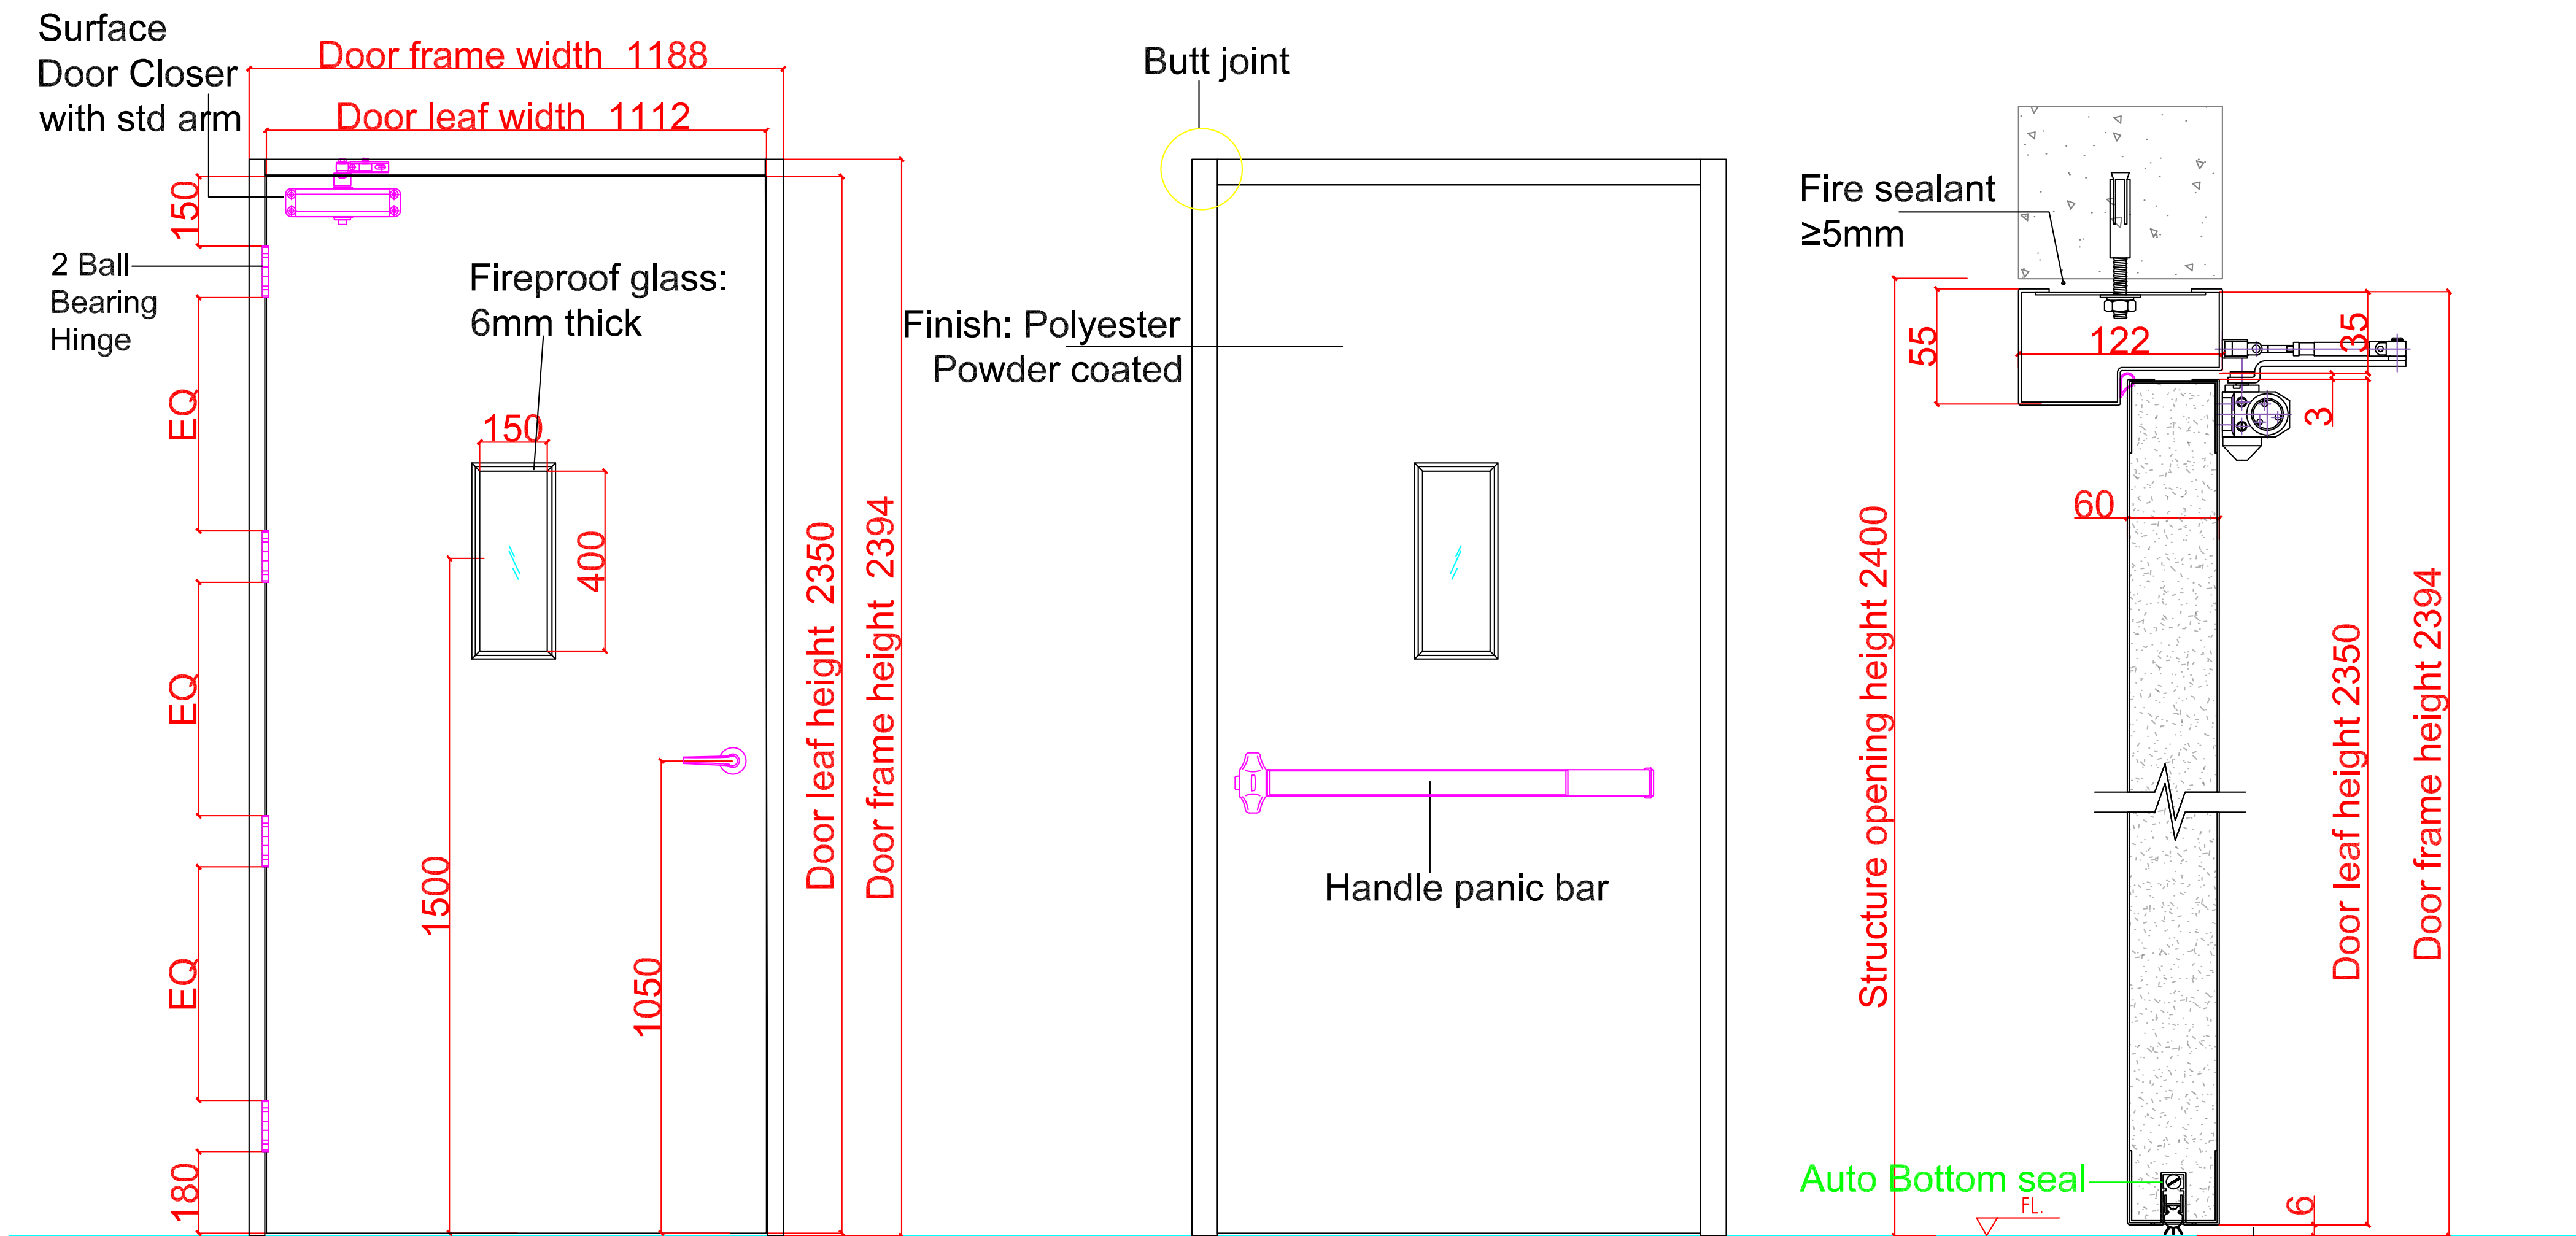

Outside elevation


Inside elevation

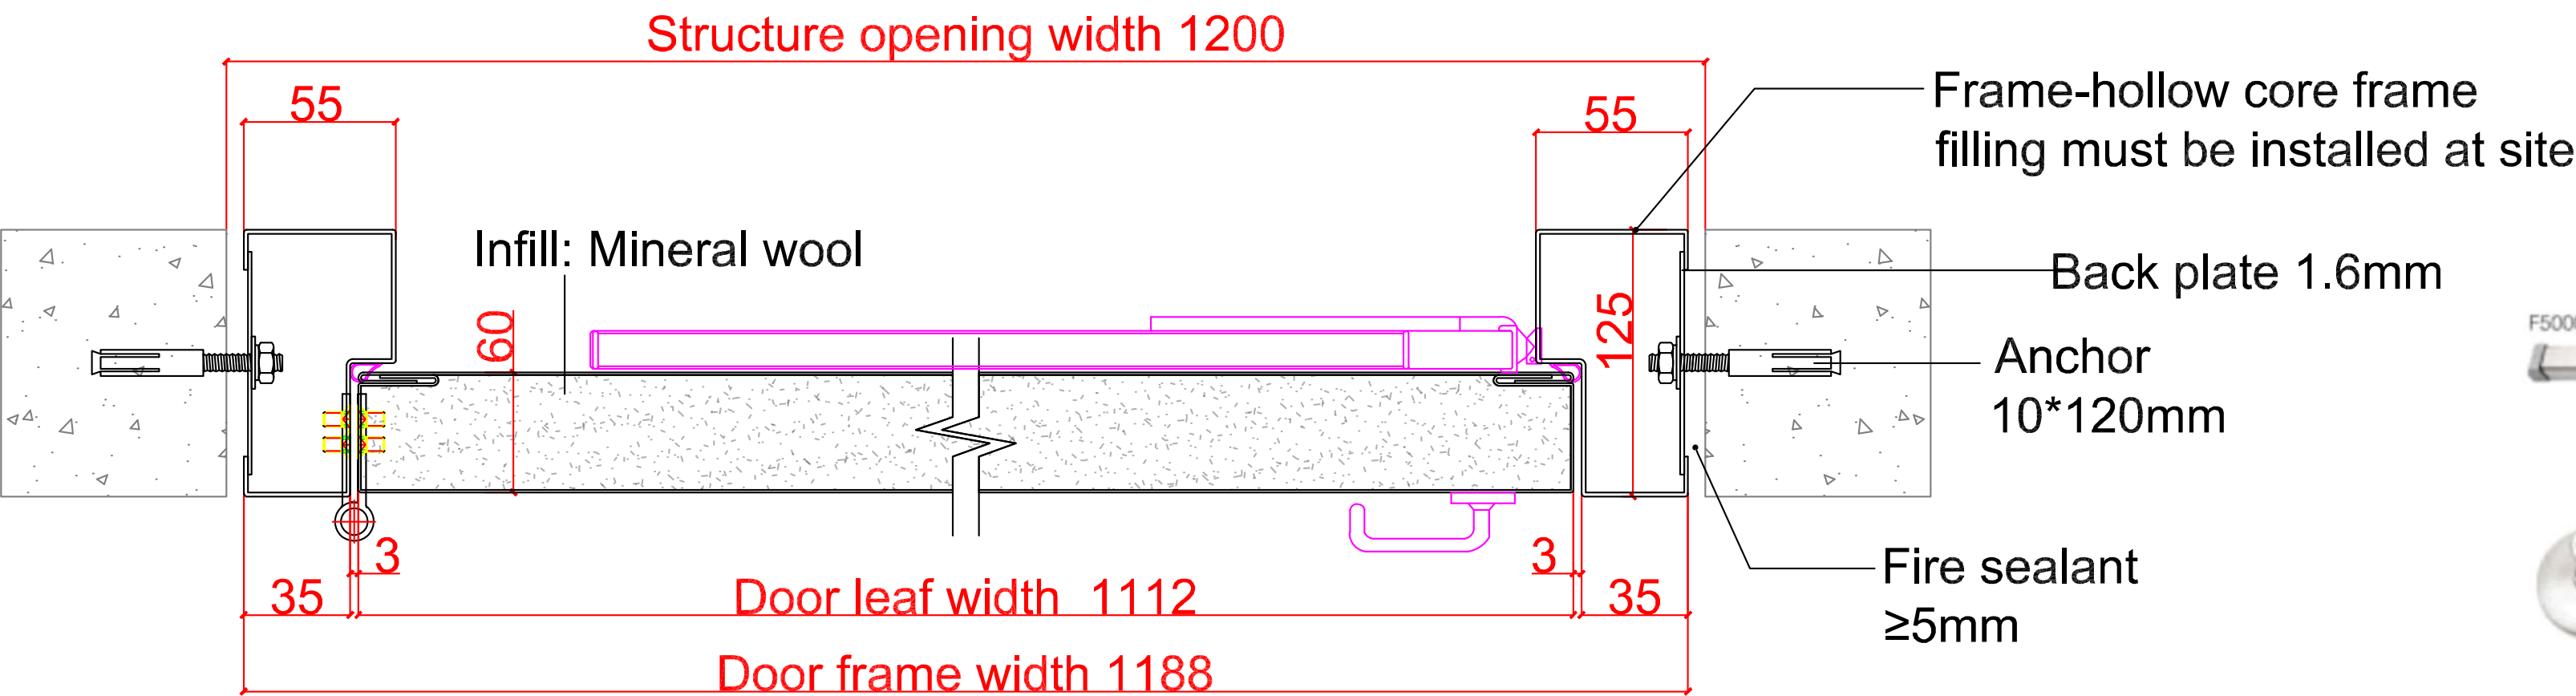

sealing trip



Hinge

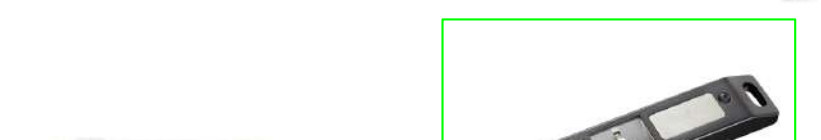


Panic Bar+Lever
euro profile, cylinder with one side key+ solnoid lock



Door closer

Hardware			
Name	Description	Qty	Remarks
Lock type	F5000P+017P+solenoid lock	1	
Hinge	4.5*4*3	4	
Door closer	184	1	
Door stop		1	
Glass	150*400mm	1	
Auto Bottom seal		1	
Smoke seal		1	
Door frame	1.6mm Galvanized steel sheet		
Door leaf	1.2mm Galvanized steel sheet		
Threshold			
Filling	Mineral wool		
Colour			

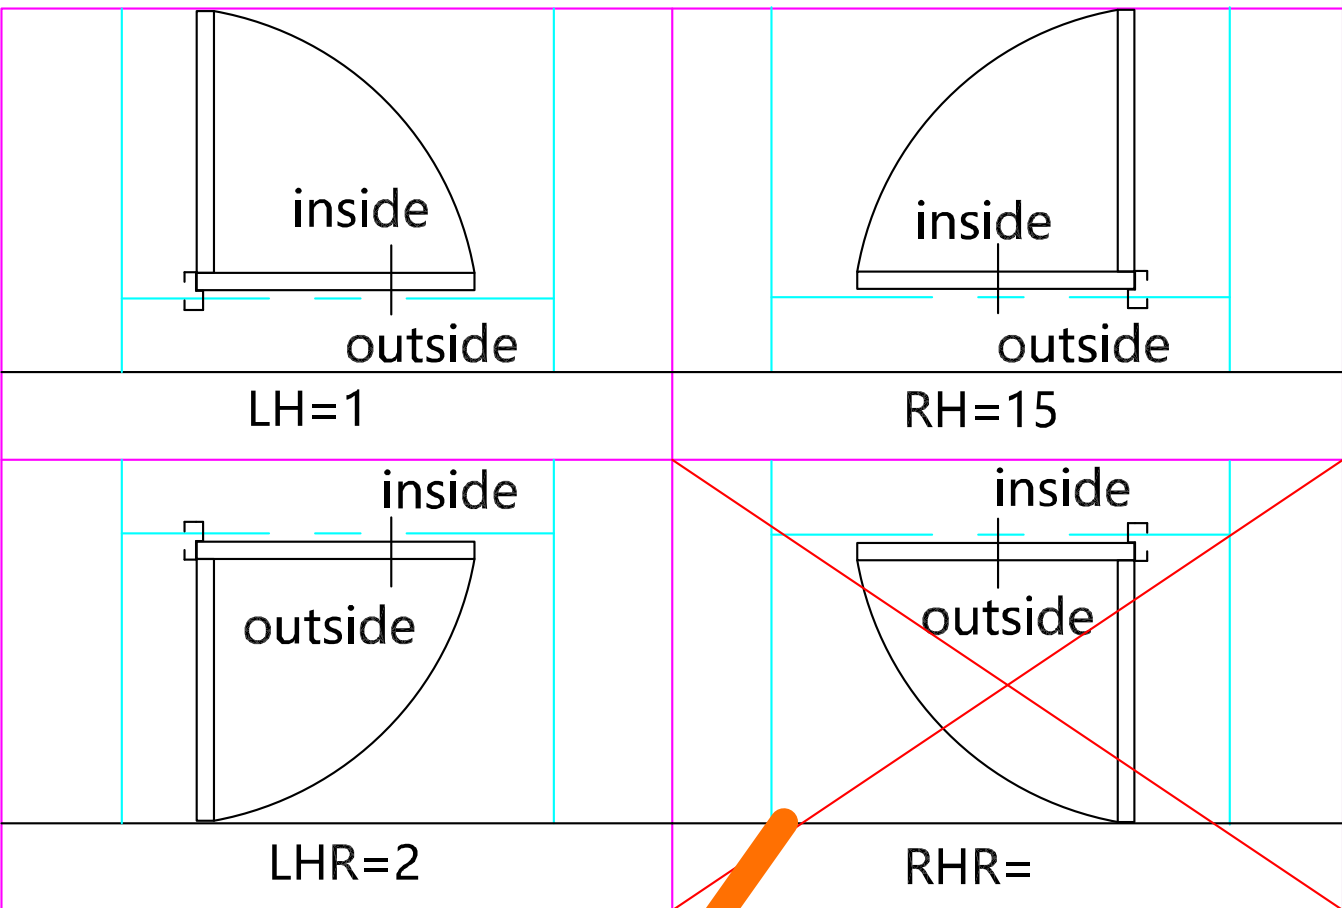



Shanghai Xunzhong Industry Co., Ltd

Project name


By		Drawing title	
Design		Size	
Check		Qty	18
Review		Opening direction	
Approval		Date	2026.05.18
		Page No	16
Total Page	34	Diagram number	

FD9a


Fire - resistance time: 120/30 minutes

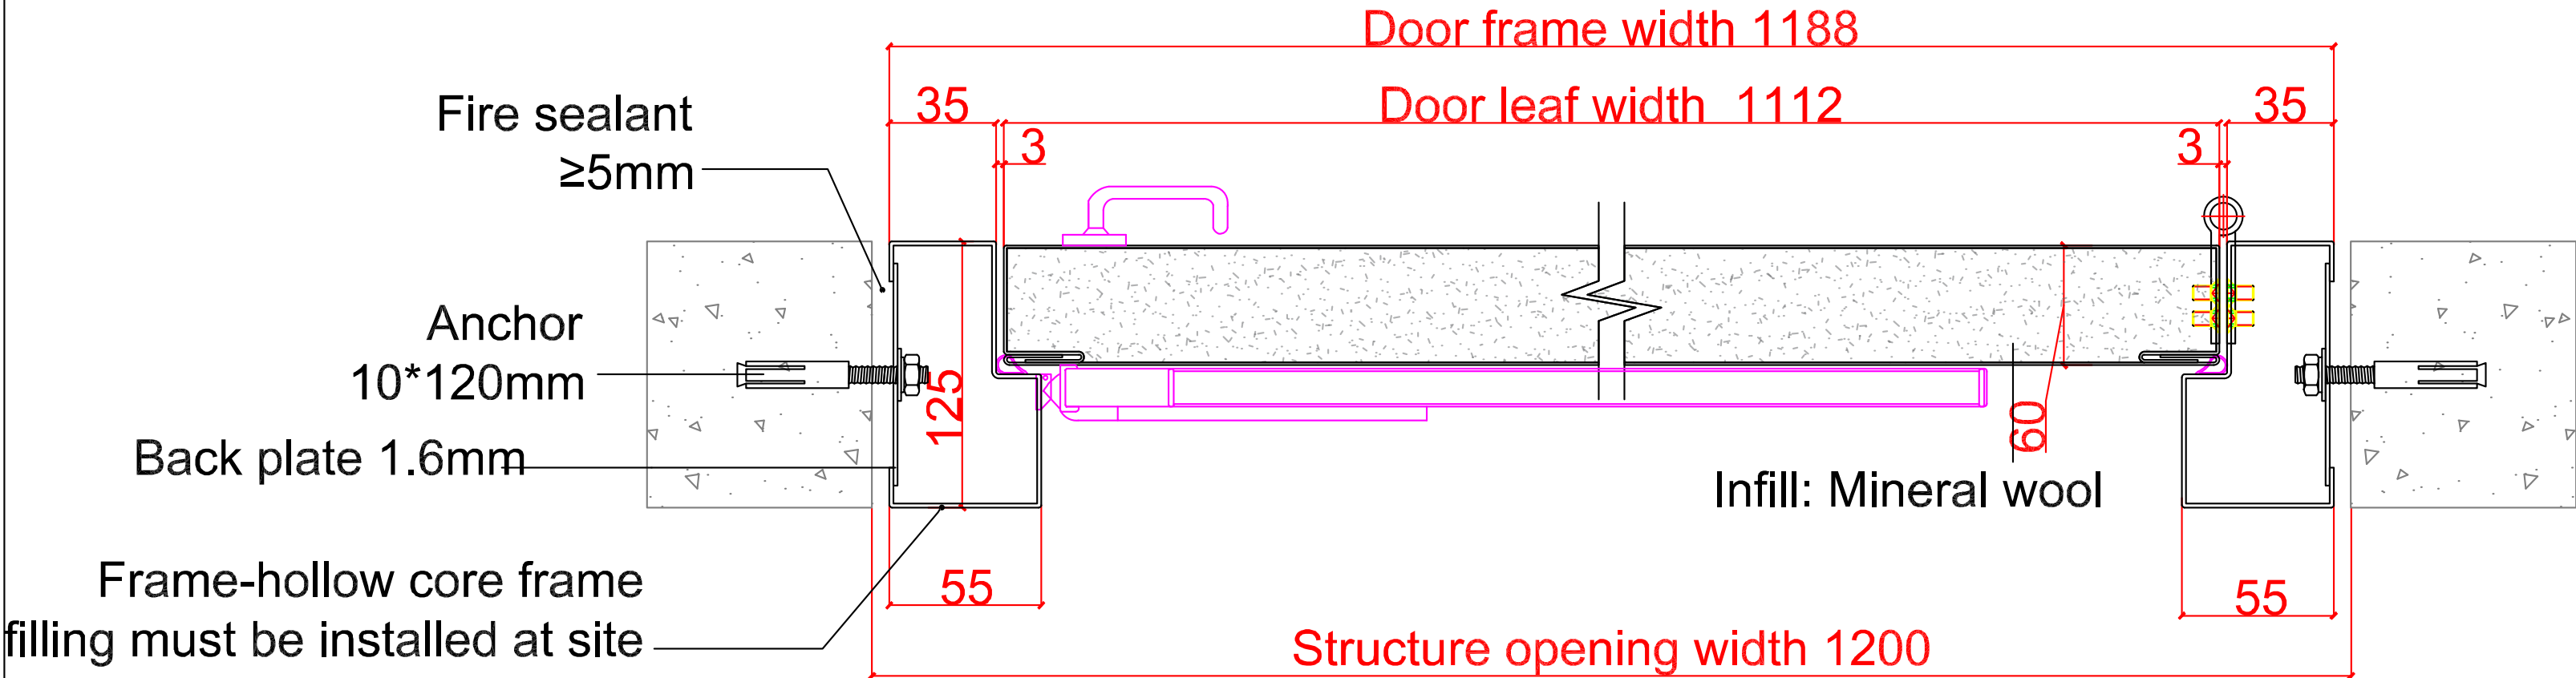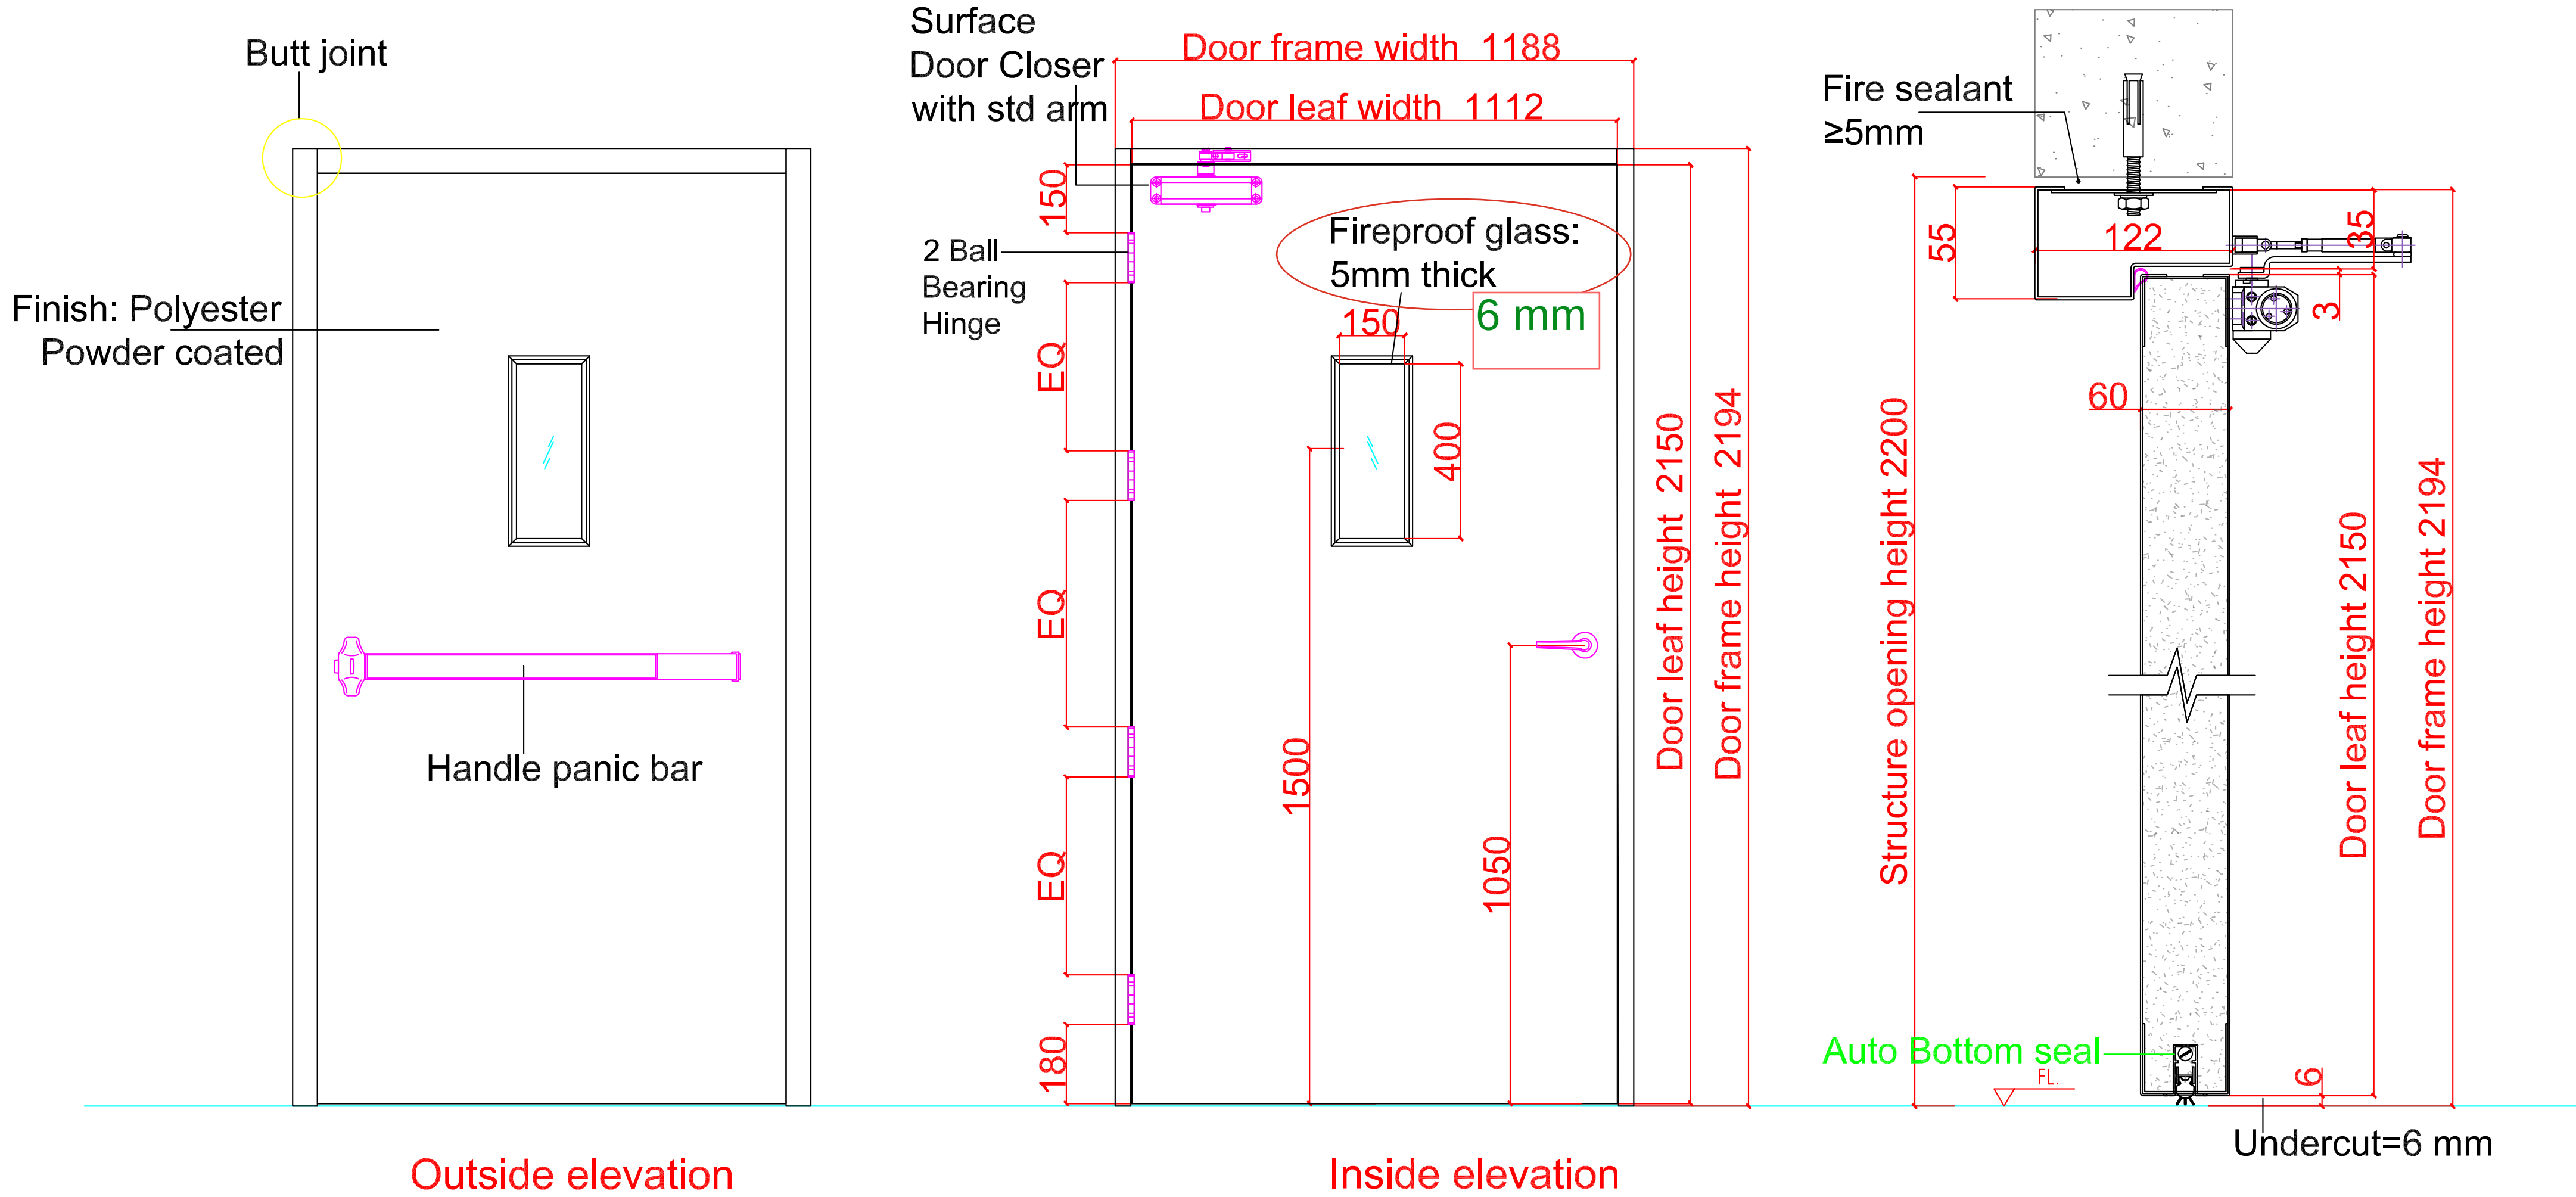

Hardware			
Name	Description	Qty	Remarks
Lock type	F5000P+017P+solenoid lock	1	
Hinge	4.5*4*3	4	
Door closer	184	1	
Door stop			
Glass	150*400mm	1	
Auto		1	
Bottom seal		1	
Smoke seal		1	
Door frame	1.6mm Galvanized steel sheet		
Door leaf	1.2mm Galvanized steel sheet		
Threshold			
Filling	Mineral wool		
Colour			

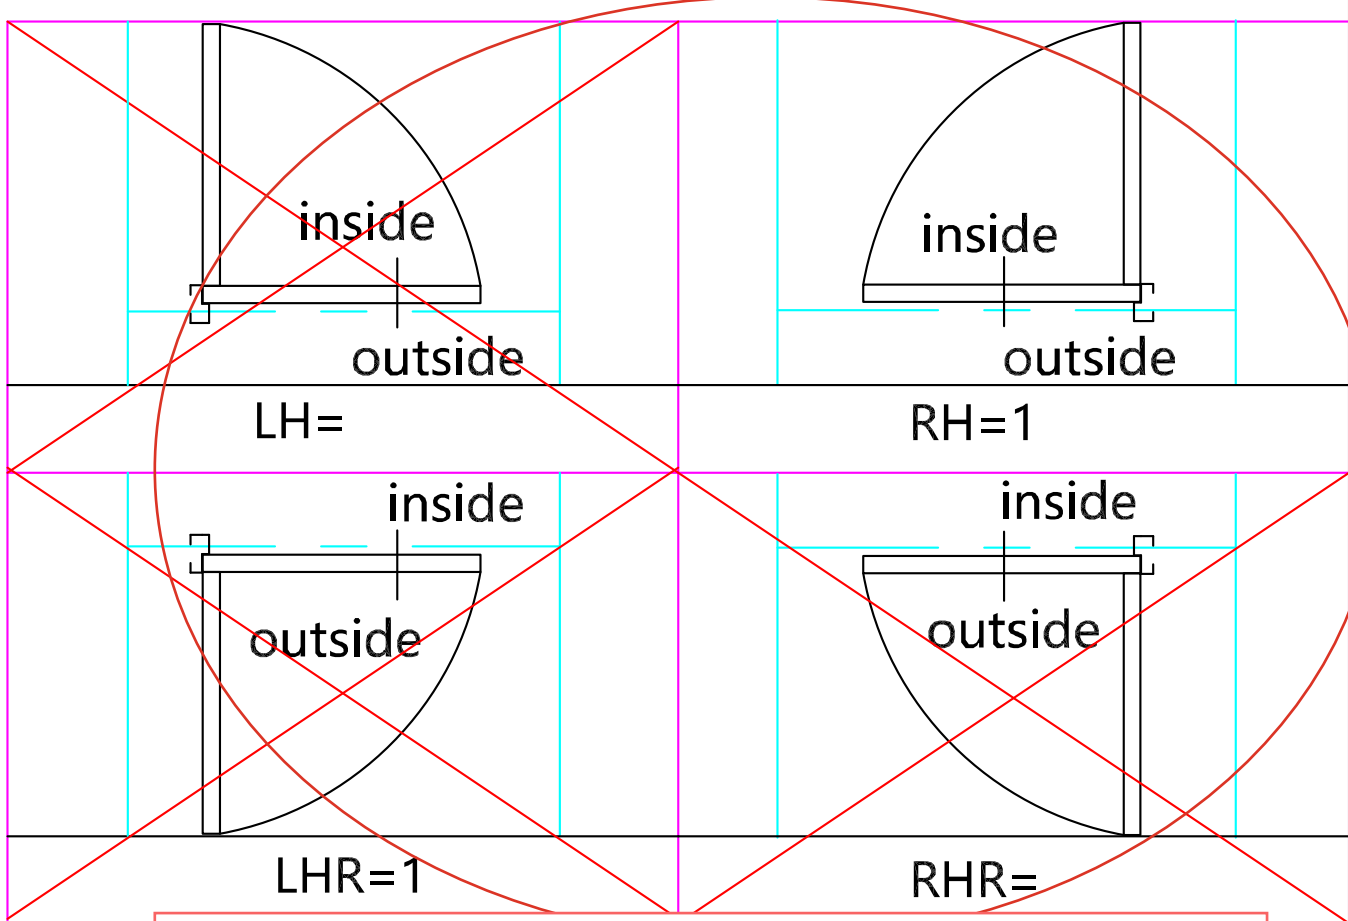


FD9a - RH-1
TOTAL QUANTITY 01

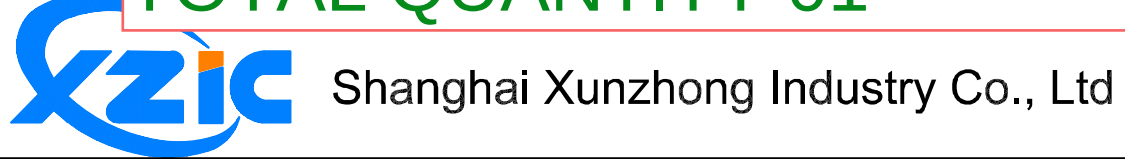

Project name			
By		Drawing title	
Design		Size	
Check		Qty	1
Review		Opening direction	
Approval		Date	2026.05.18
		Page No	17
Total Page	34	Diagram number	


FD9b

Fire - resistance time: 120/30 minutes

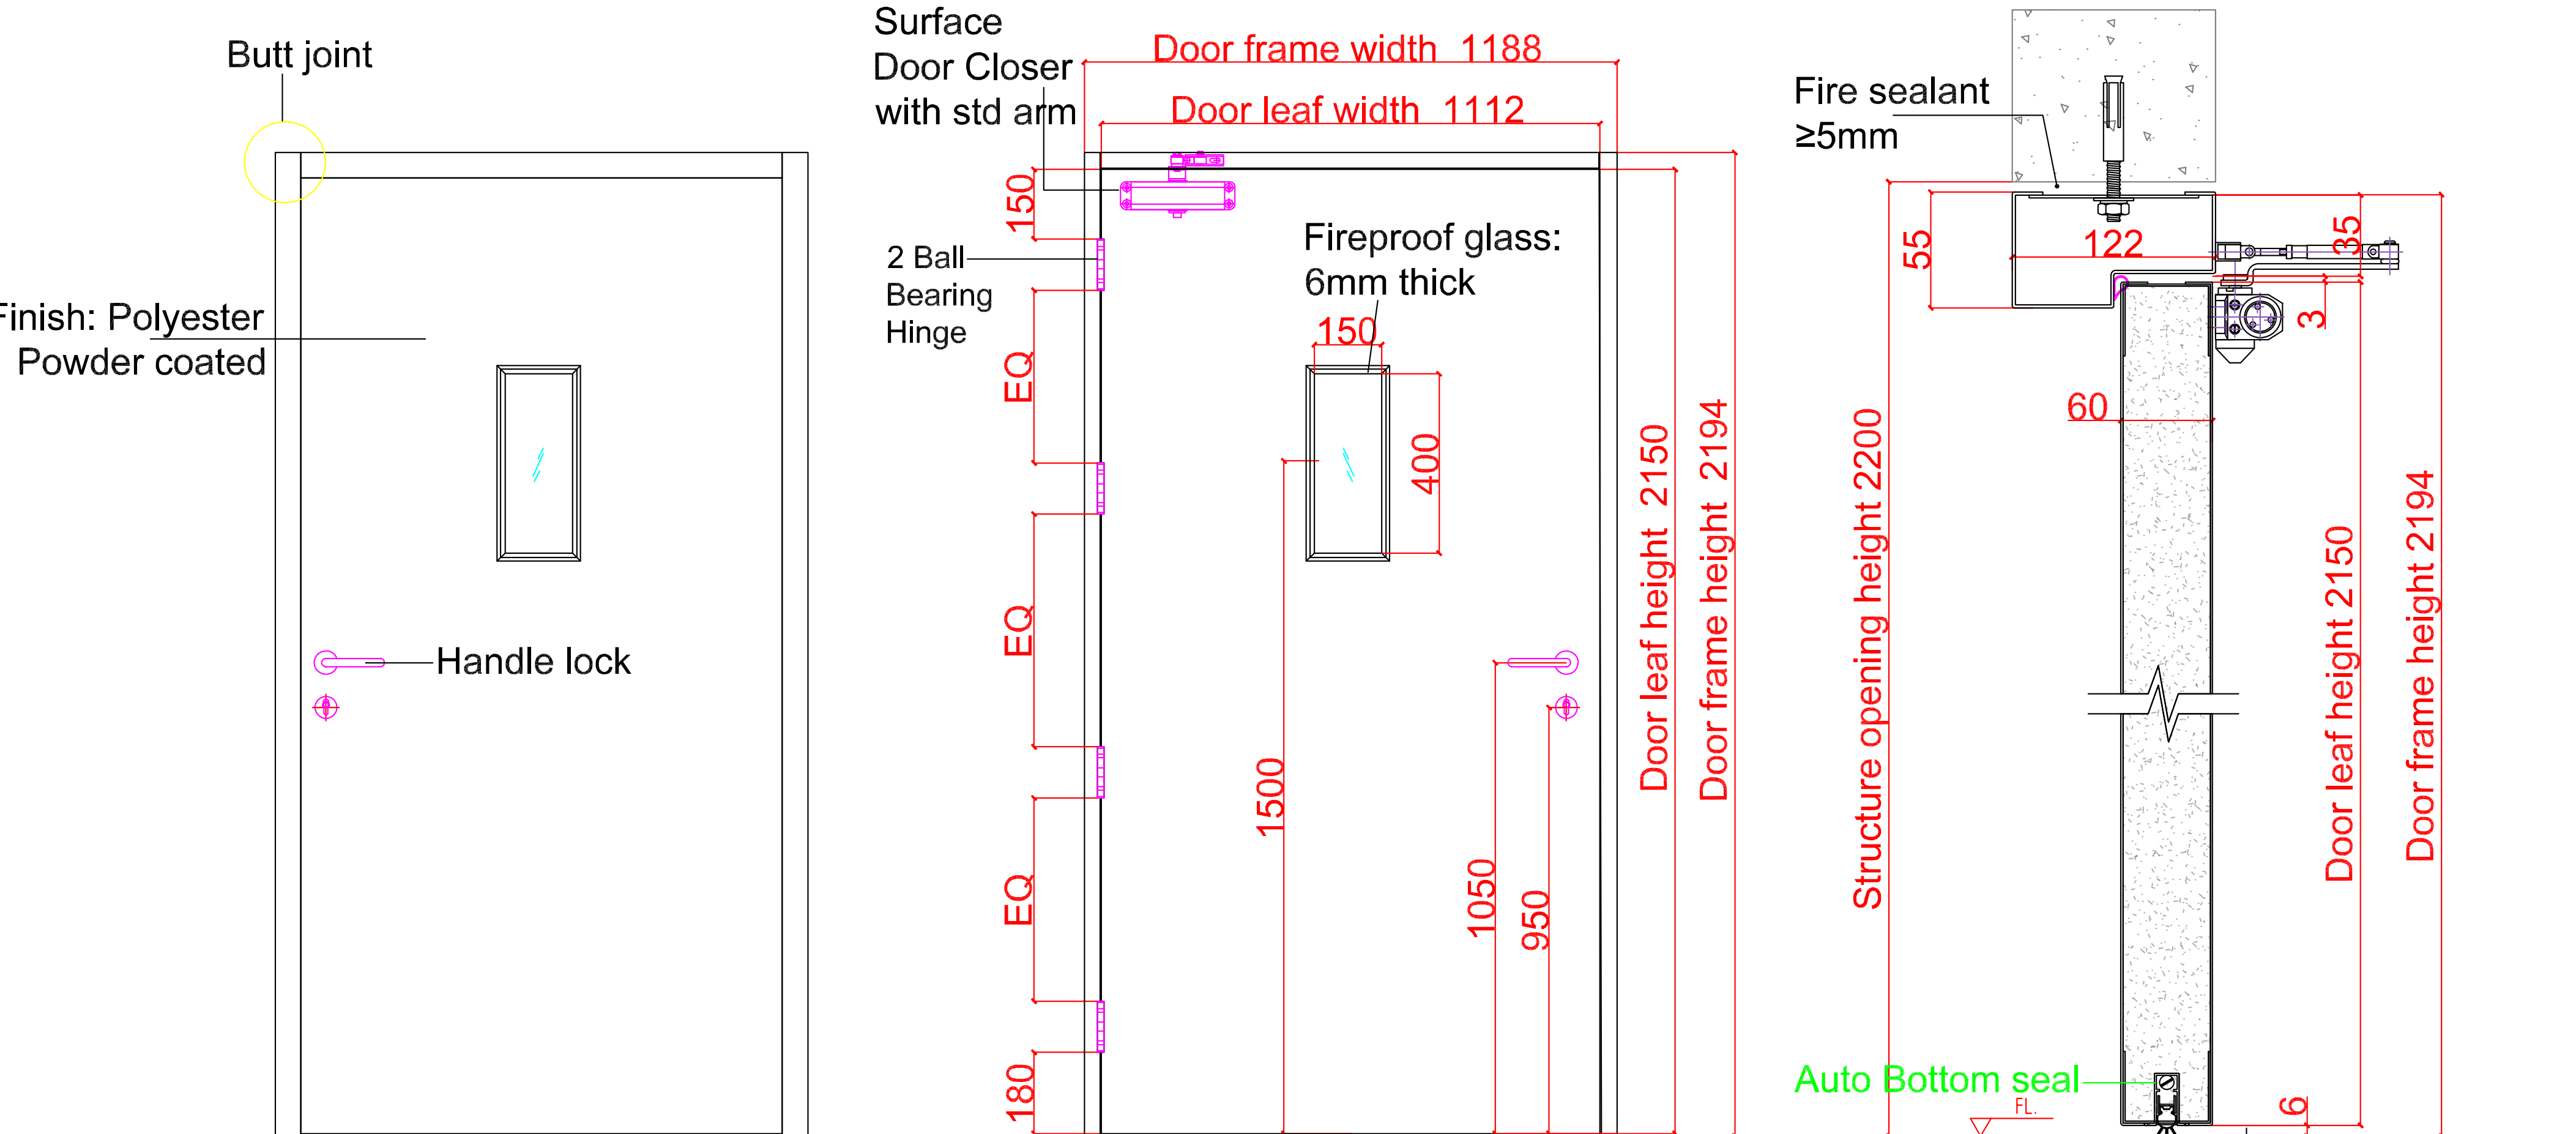


Outside elevation

Inside elevation

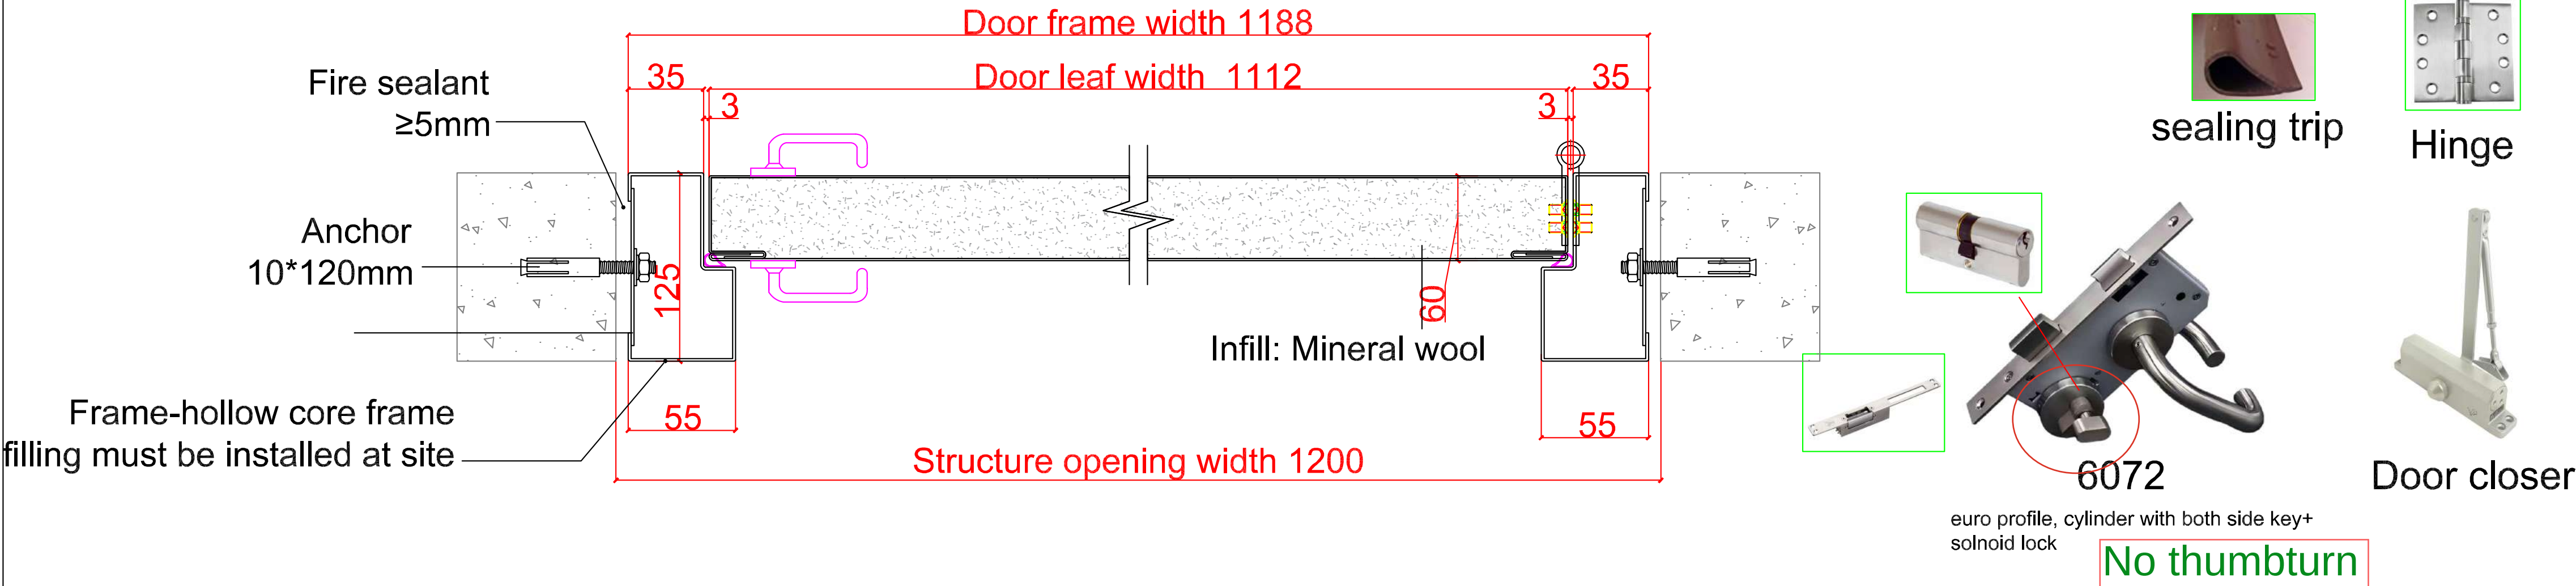


Hardware			
Name	Description	Qty	Remarks
Lock type	solenoid lock	1	
Hinge	4.5*4*3	4	
Door closer	184	1	
Door stop			
Glass	150*400mm	1	
Auto Bottom seal		1	
Smoke seal		1	
Door frame	1.6mm Galvanized steel sheet		
Door leaf	1.2mm Galvanized steel sheet		
Threshold			
Filling	Mineral wool		
Colour			

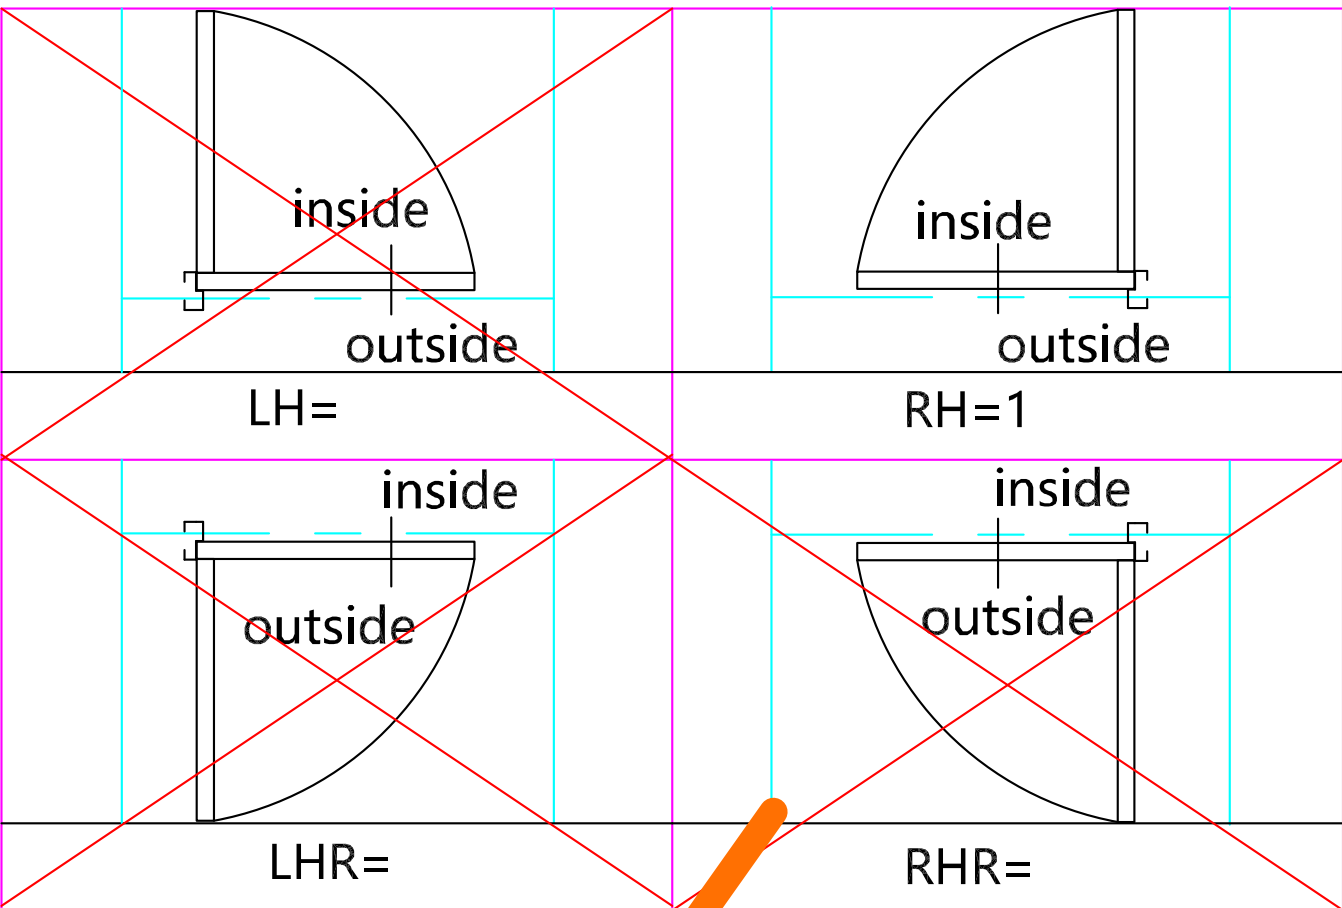


 Shanghai Xunzhong Industry Co., Ltd			
Project name			
By		Drawing title	
Design		Size	
Check		Qty	1
Review		Opening direction	
Approval		Date	2026.05.18
		Page No	18
Total Page	34	Diagram number	

FD9c

Fire - resistance time: 120/30 minutes


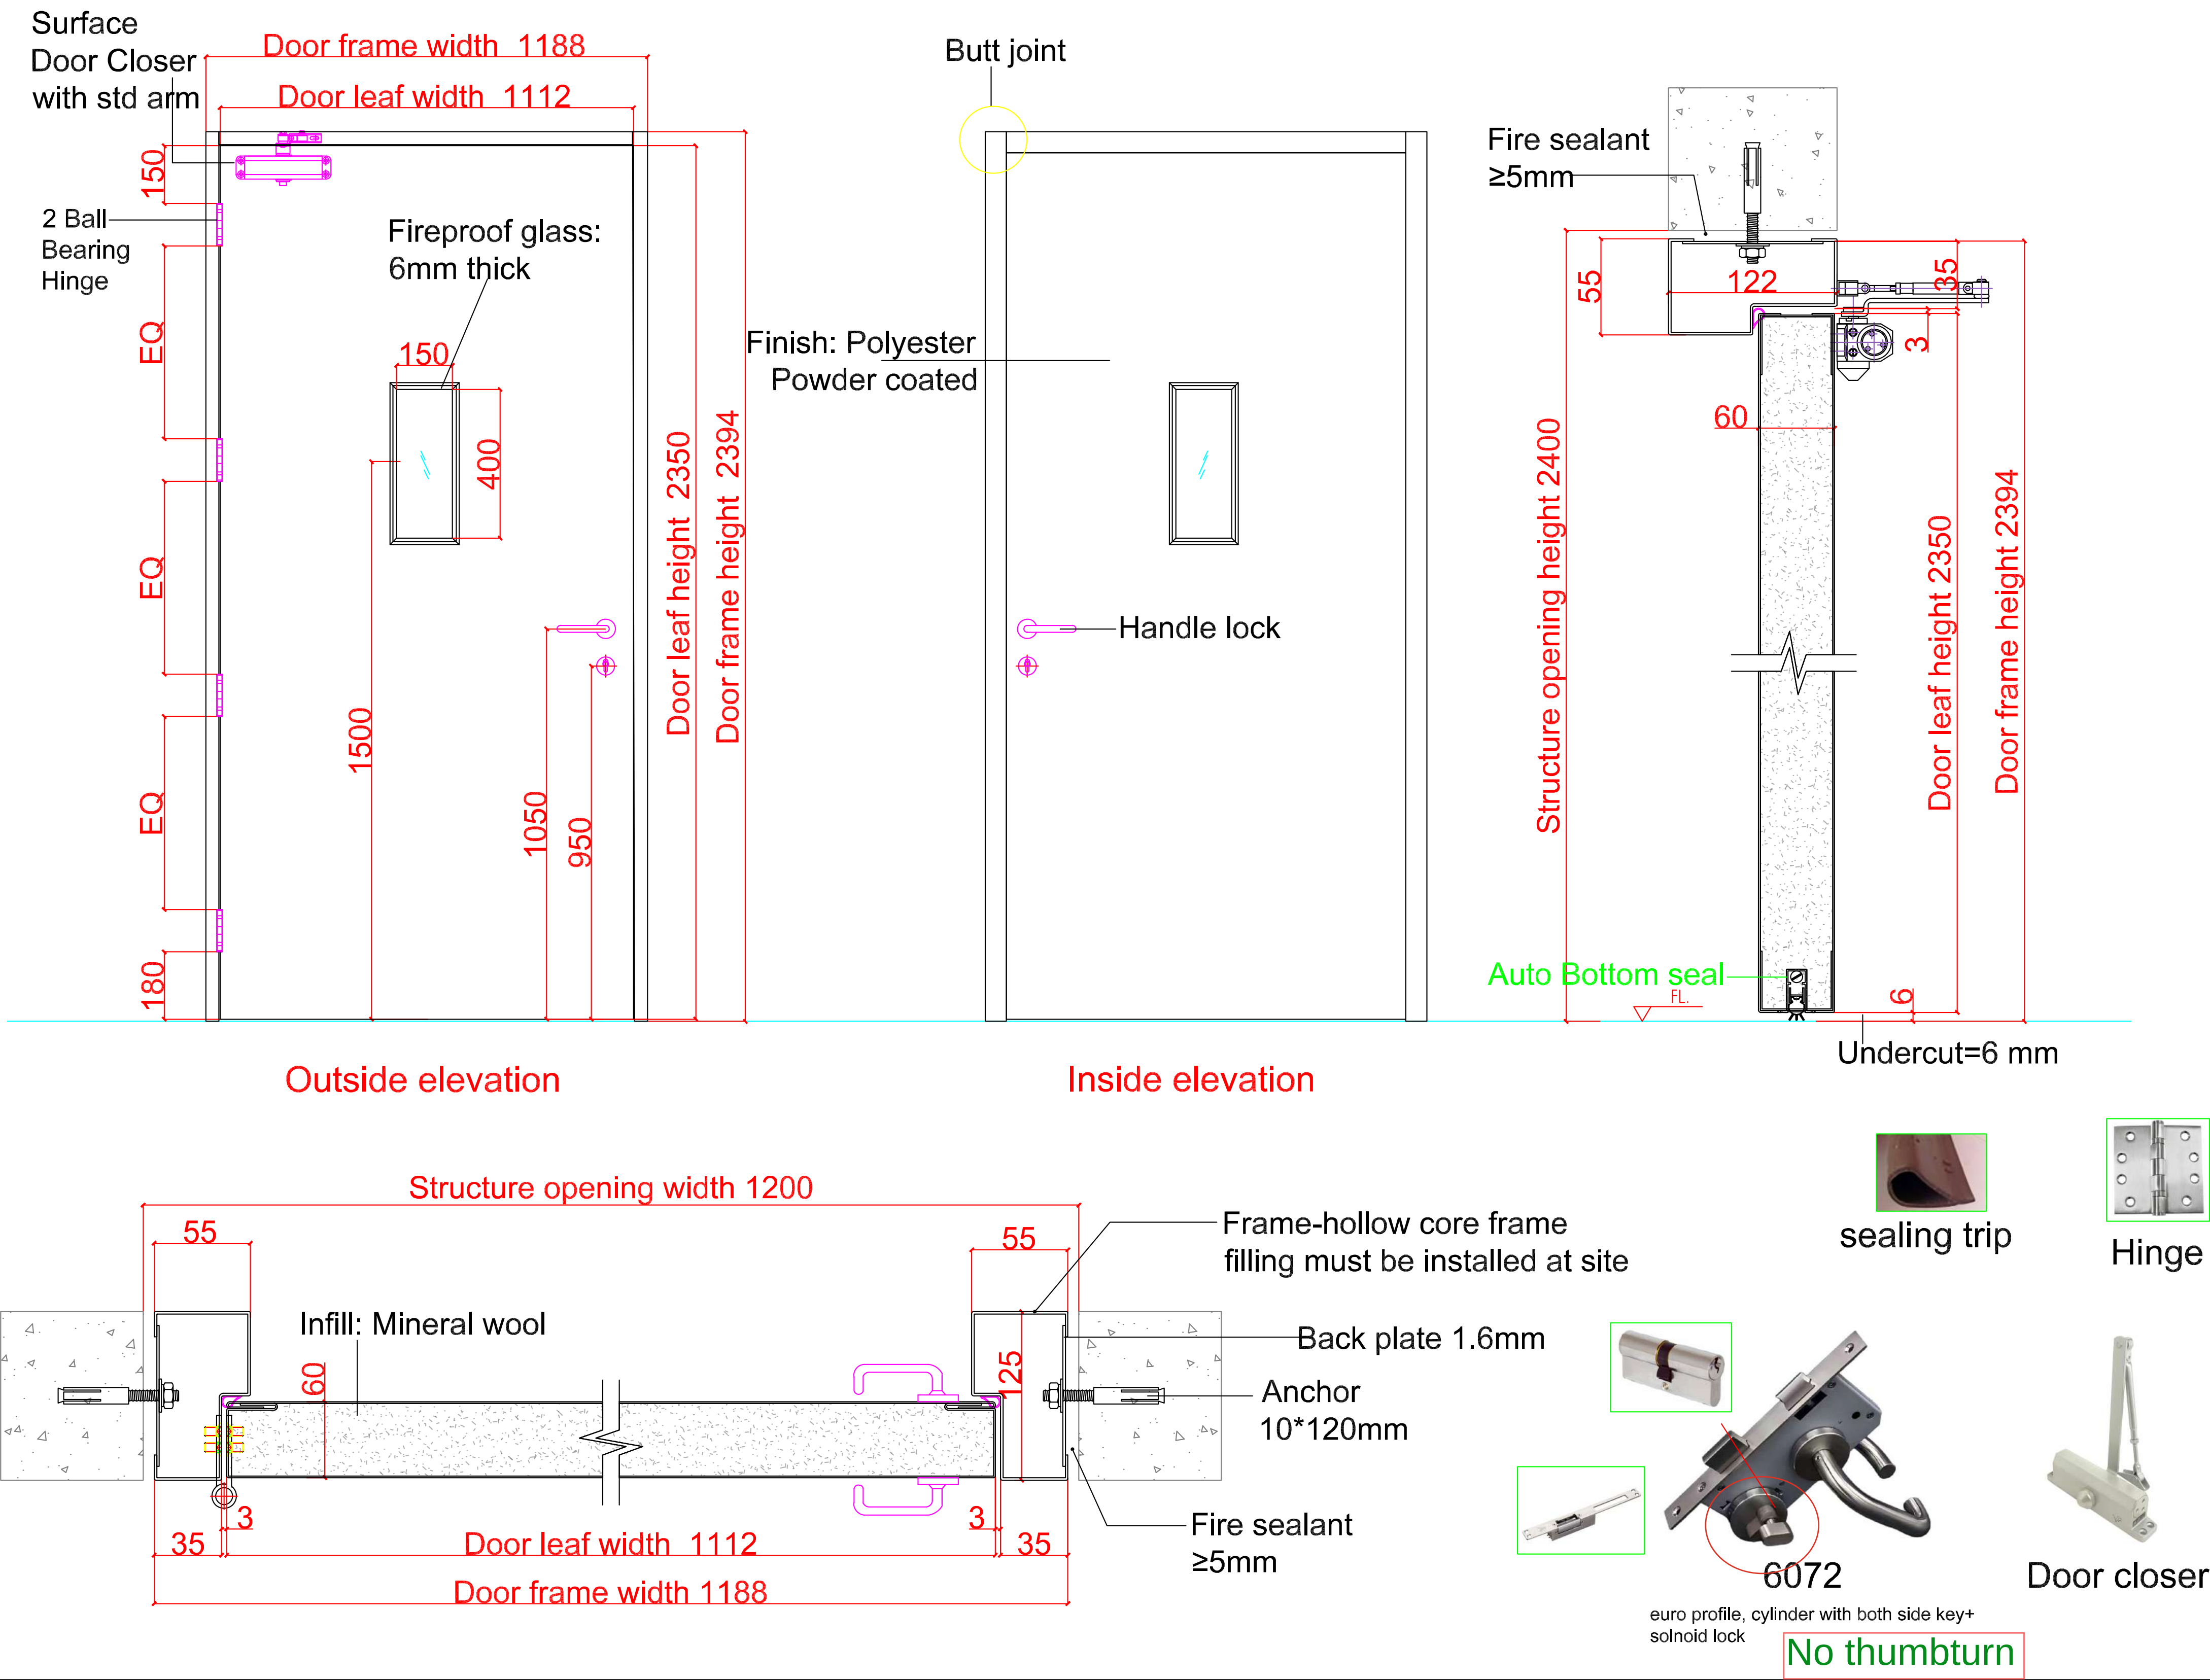


Hardware			
Name	Description	Qty	Remarks
Lock type	solenoid lock	1	
Hinge	4.5*4*3	4	
Door closer	184	1	
Door stop			
Glass	150*400mm	1	
Auto Bottom seal		1	
Smoke seal		1	
Door frame	1.6mm Galvanized steel sheet		
Door leaf	1.2mm Galvanized steel sheet		
Threshold			
Filling	Mineral wool		
Colour			

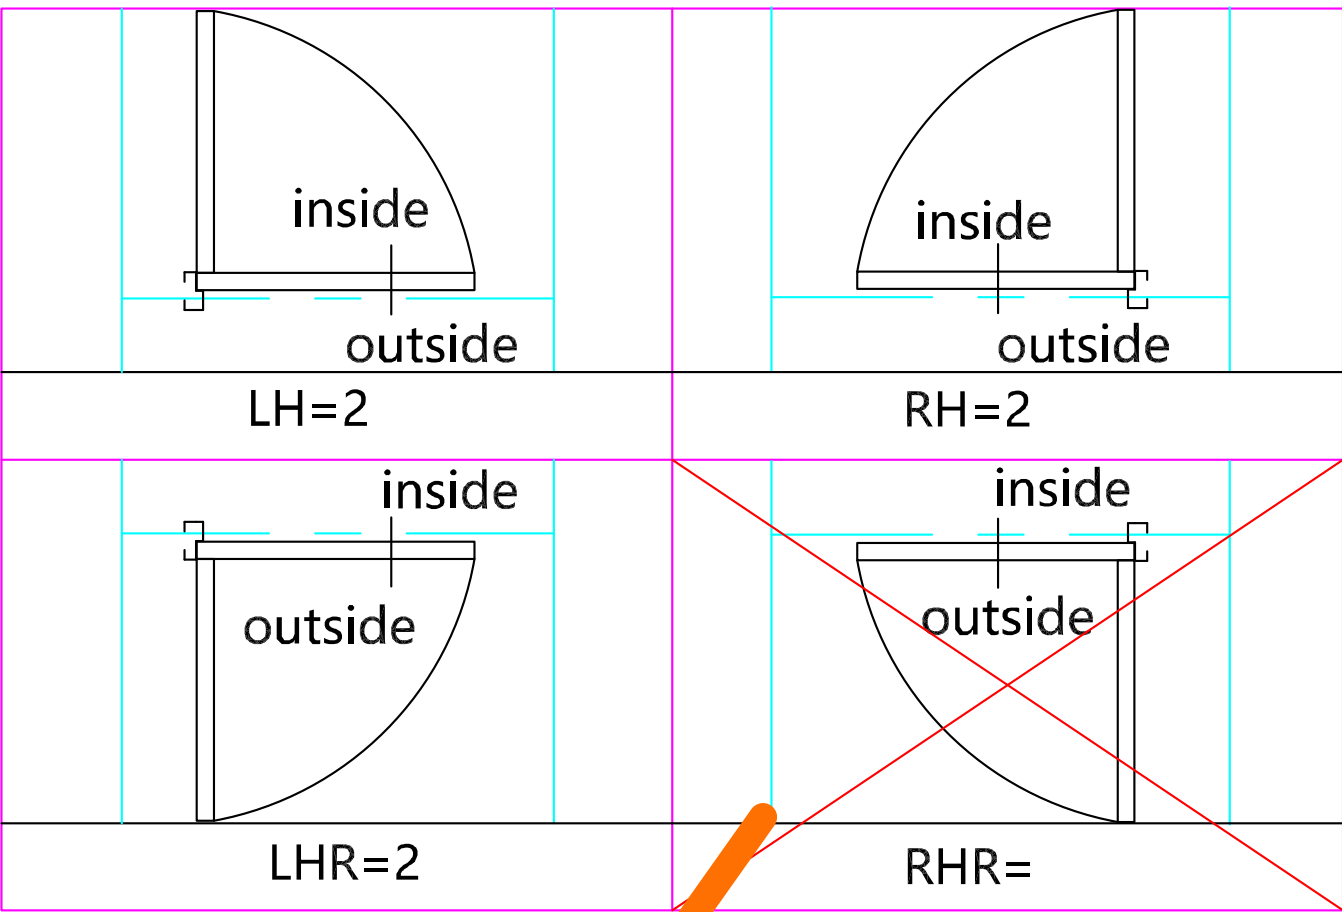


 Shanghai Xunzhong Industry Co., Ltd			
Project name			
By		Drawing title	
Design		Size	
Check		Qty	6
Review		Opening direction	
Approval		Date	2026.05.18
Total Page	34	Page No	19
		Diagram number	

SD1

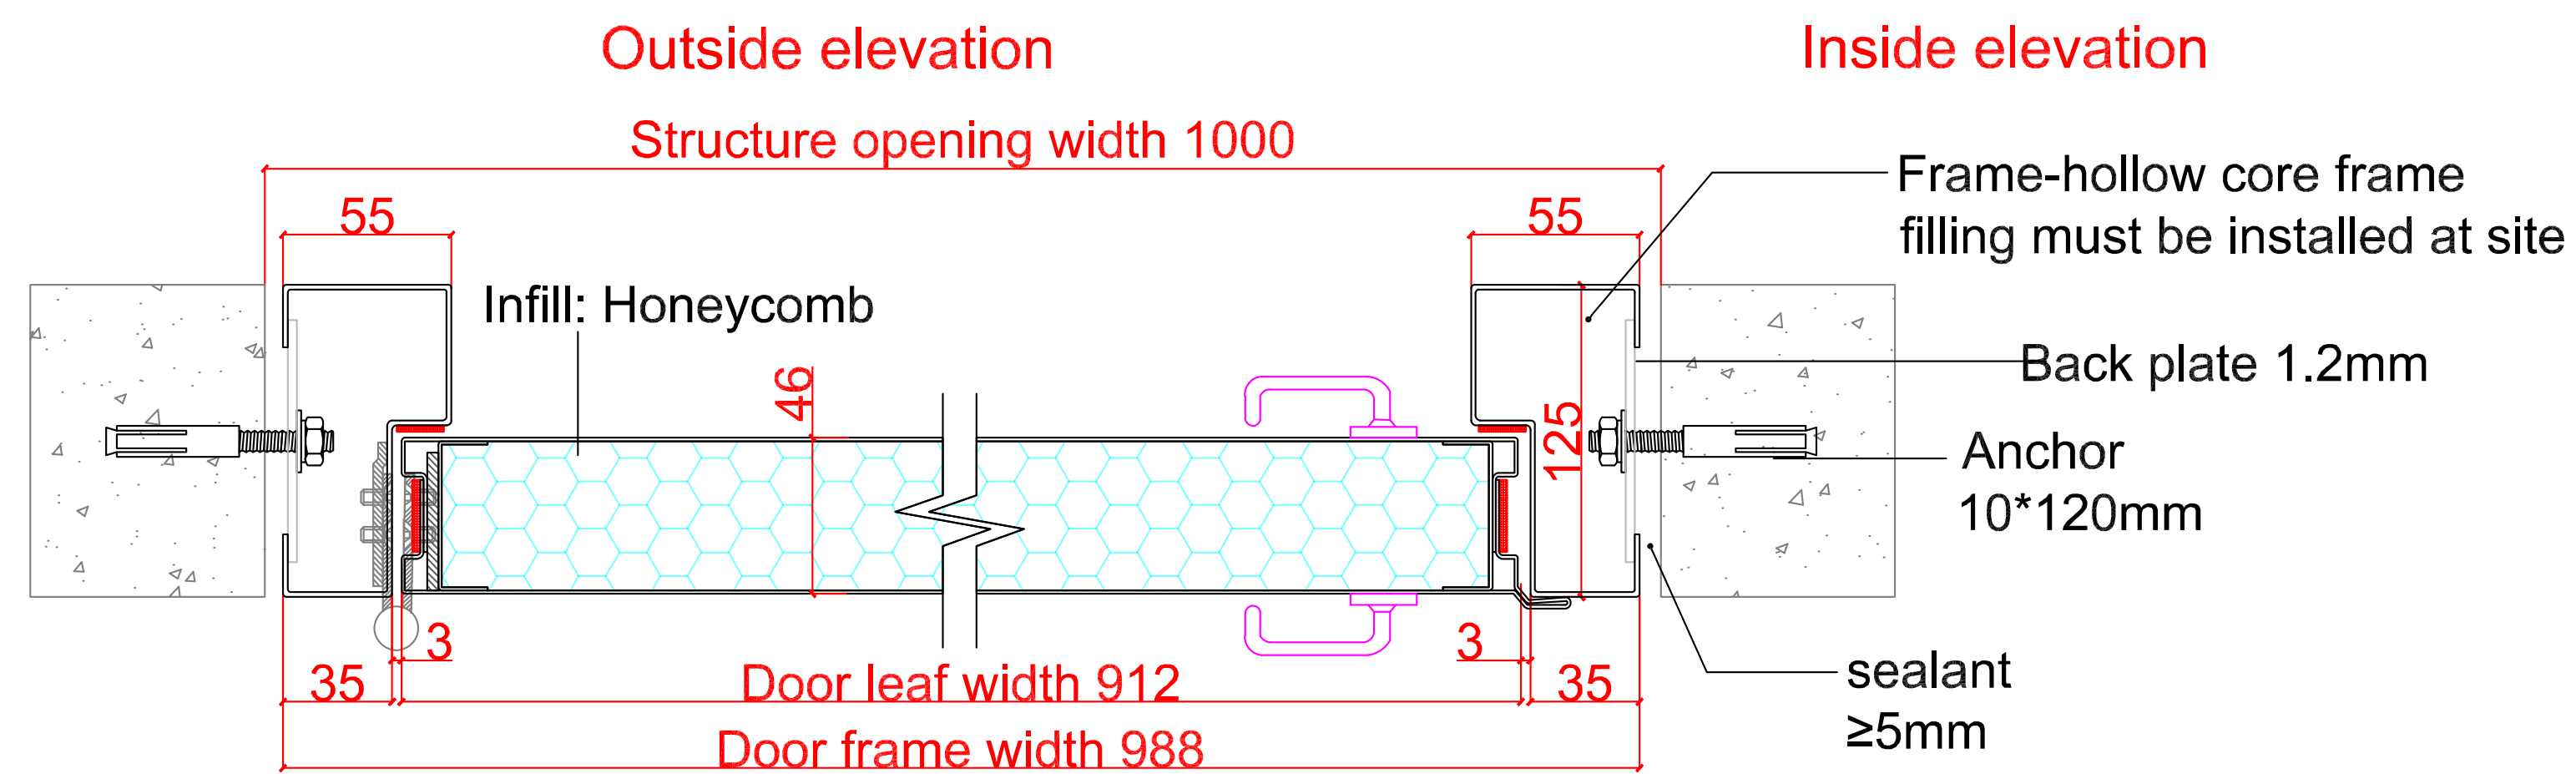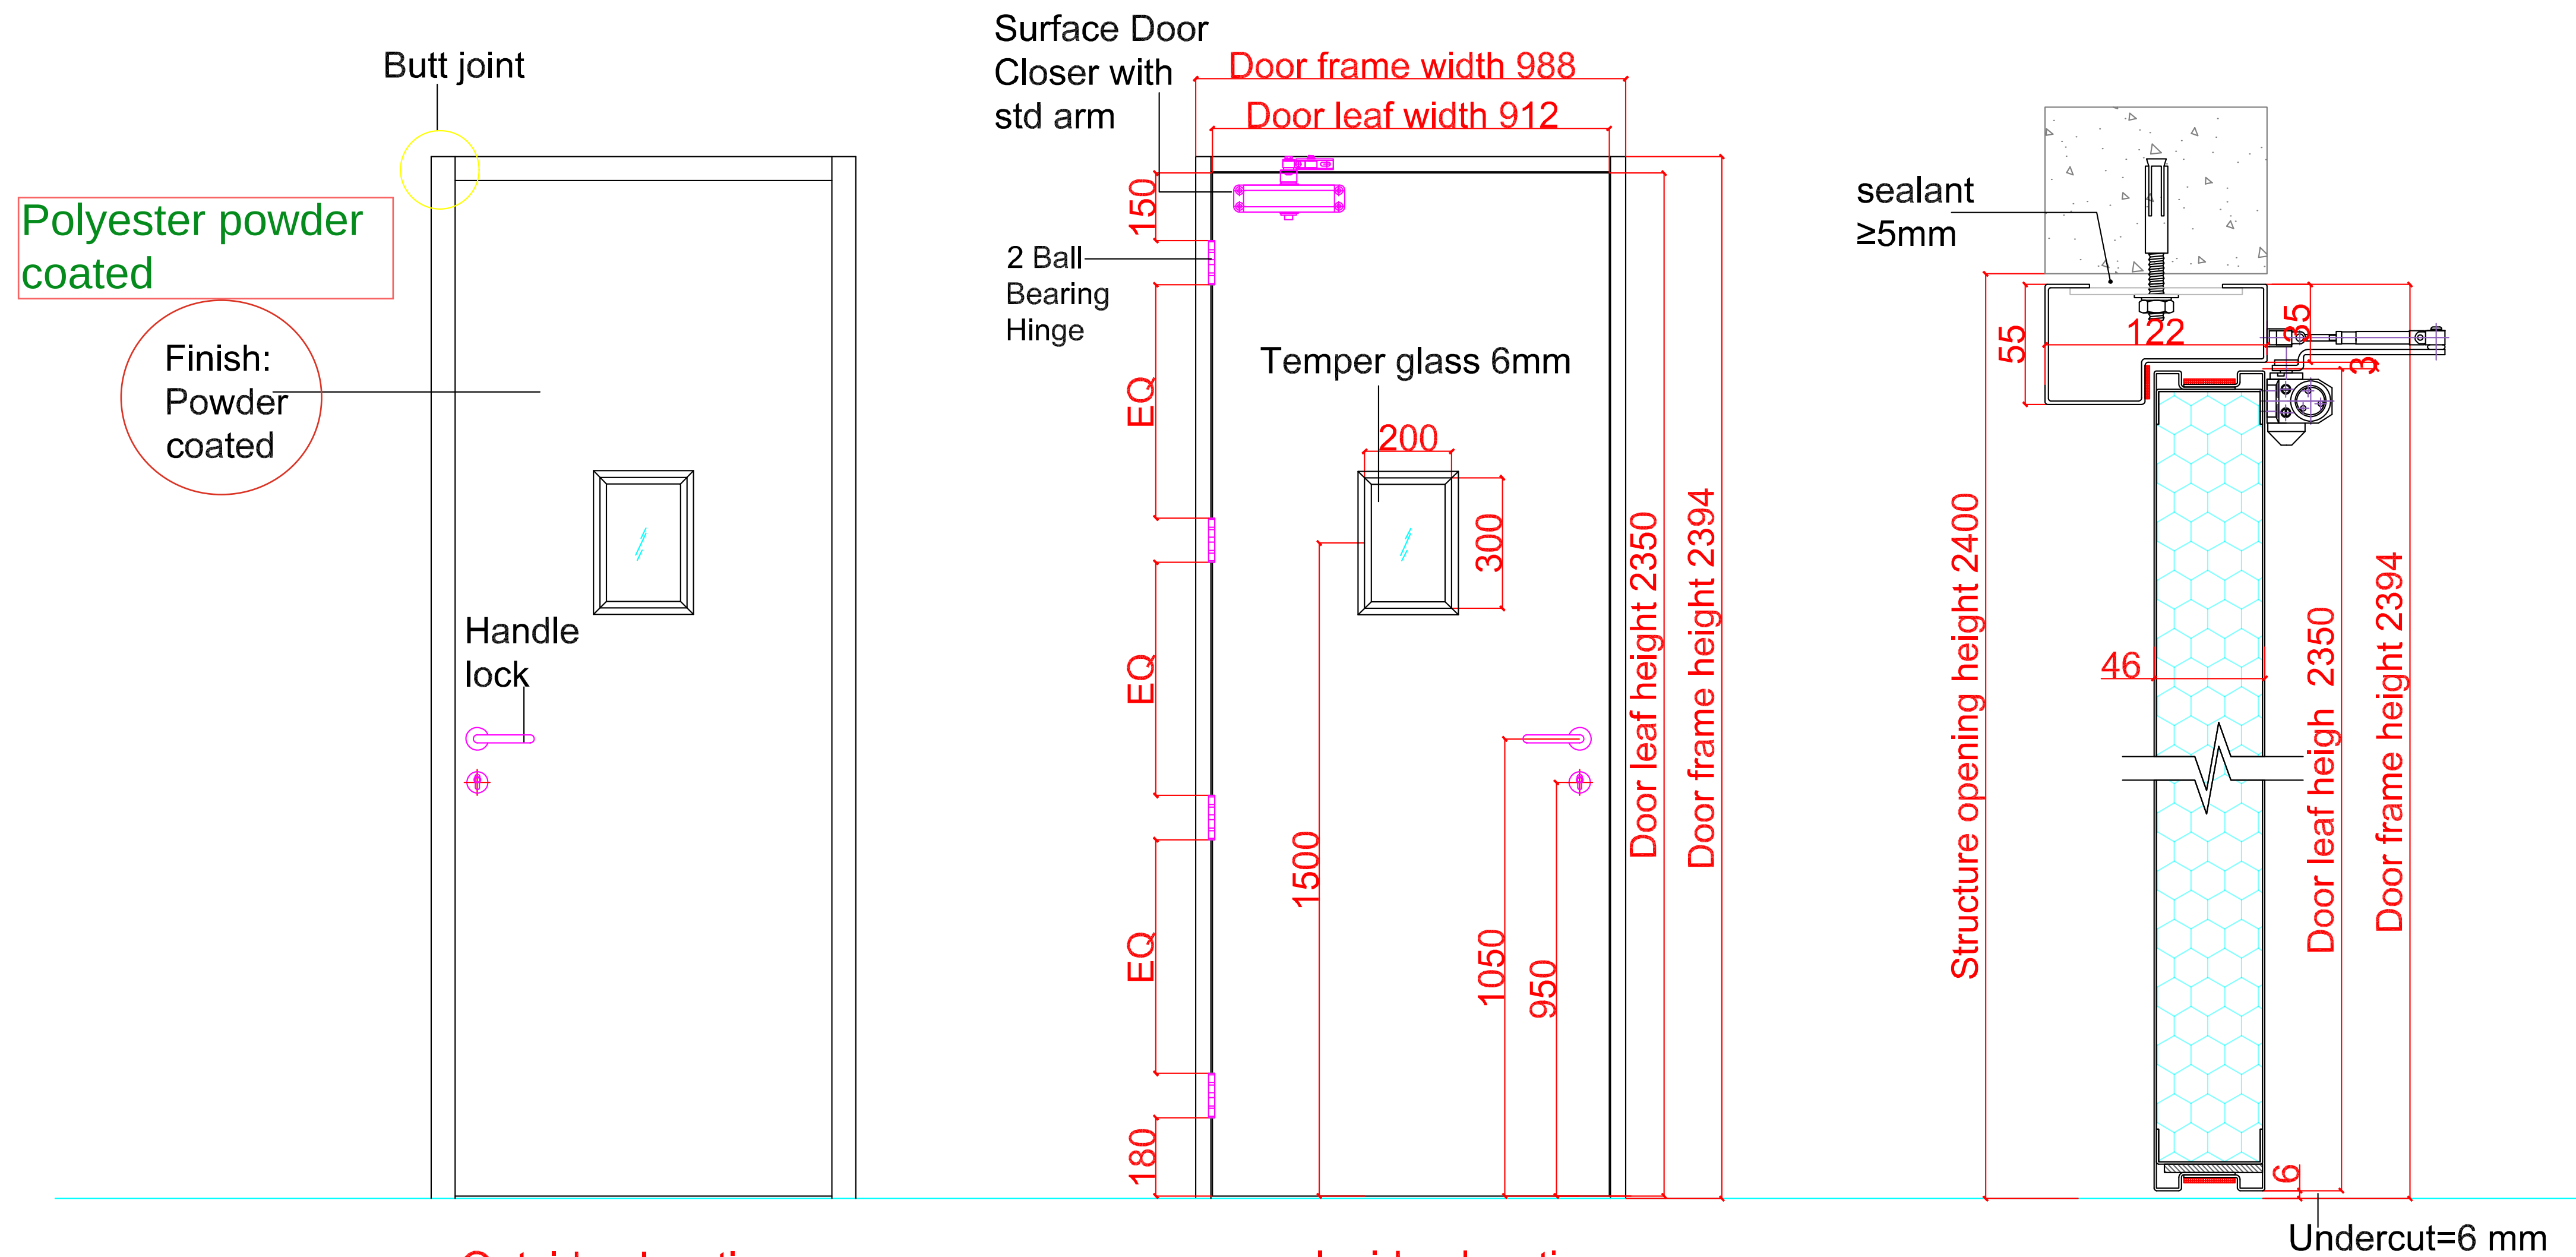

Hardware			
Name	Description	Qty	Remarks
Lock type	Mortise lock	1	
Hinge	4*4*3	4	
Door closer	184	1	
Door stop			
Glass	200*300mm	1	
Smoke seal			
Door frame	1.2mm Galvanized steel sheet		
Door leaf	0.8mm Galvanized steel sheet		
Threshold			
Filling	Honeycomb		
Colour			


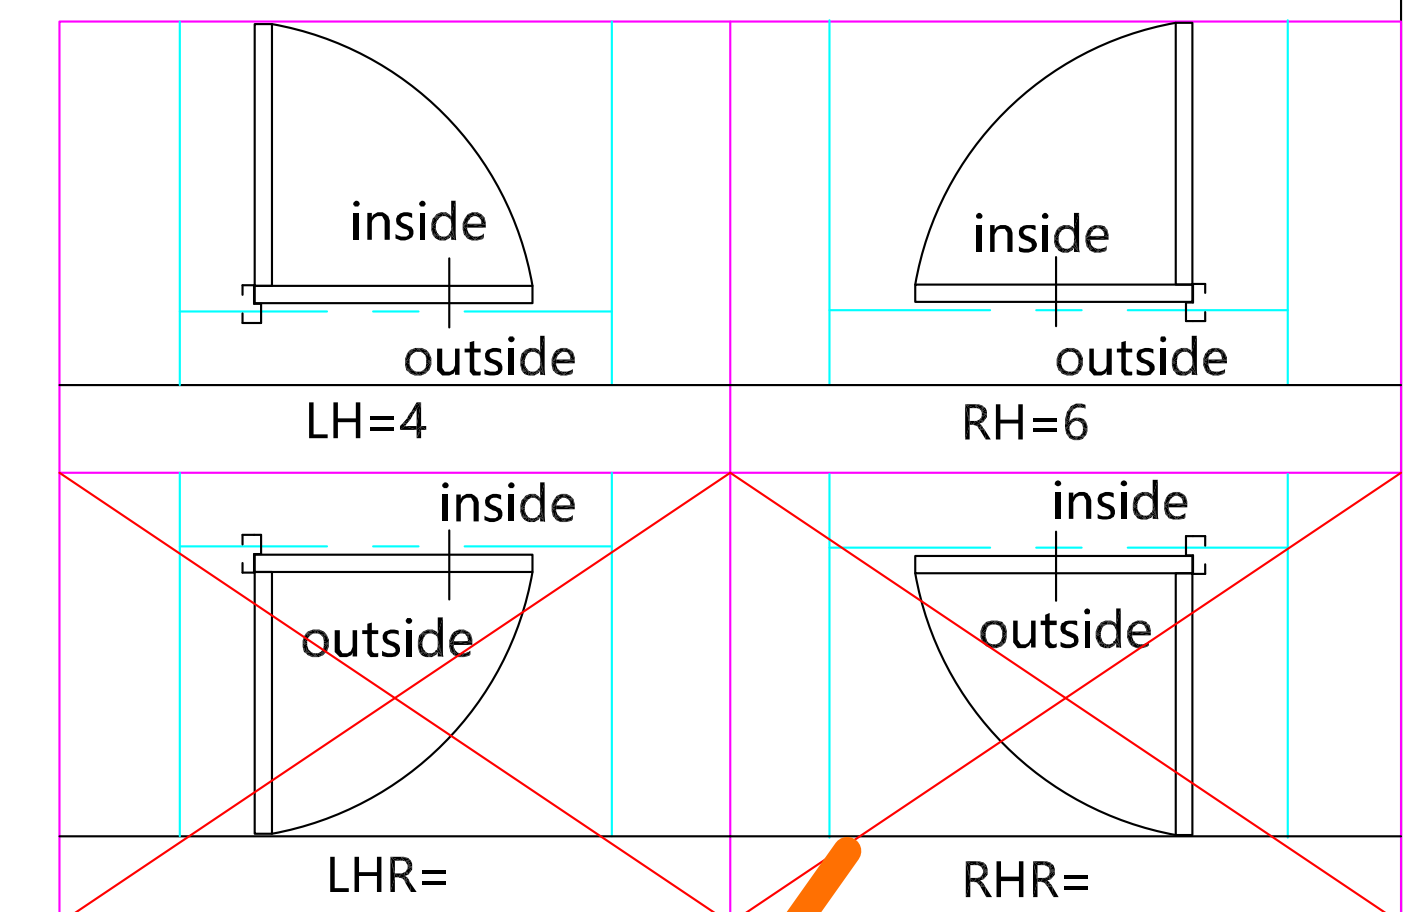


 Shanghai Xunzhong Industry Co., Ltd


Project name

By		Drawing title	
Design		Size	
Check		Qty	10
Review		Opening direction	
Approval		Date	2026.05.18
		Page No	20
Total Page	34	Diagram number	

SD1a

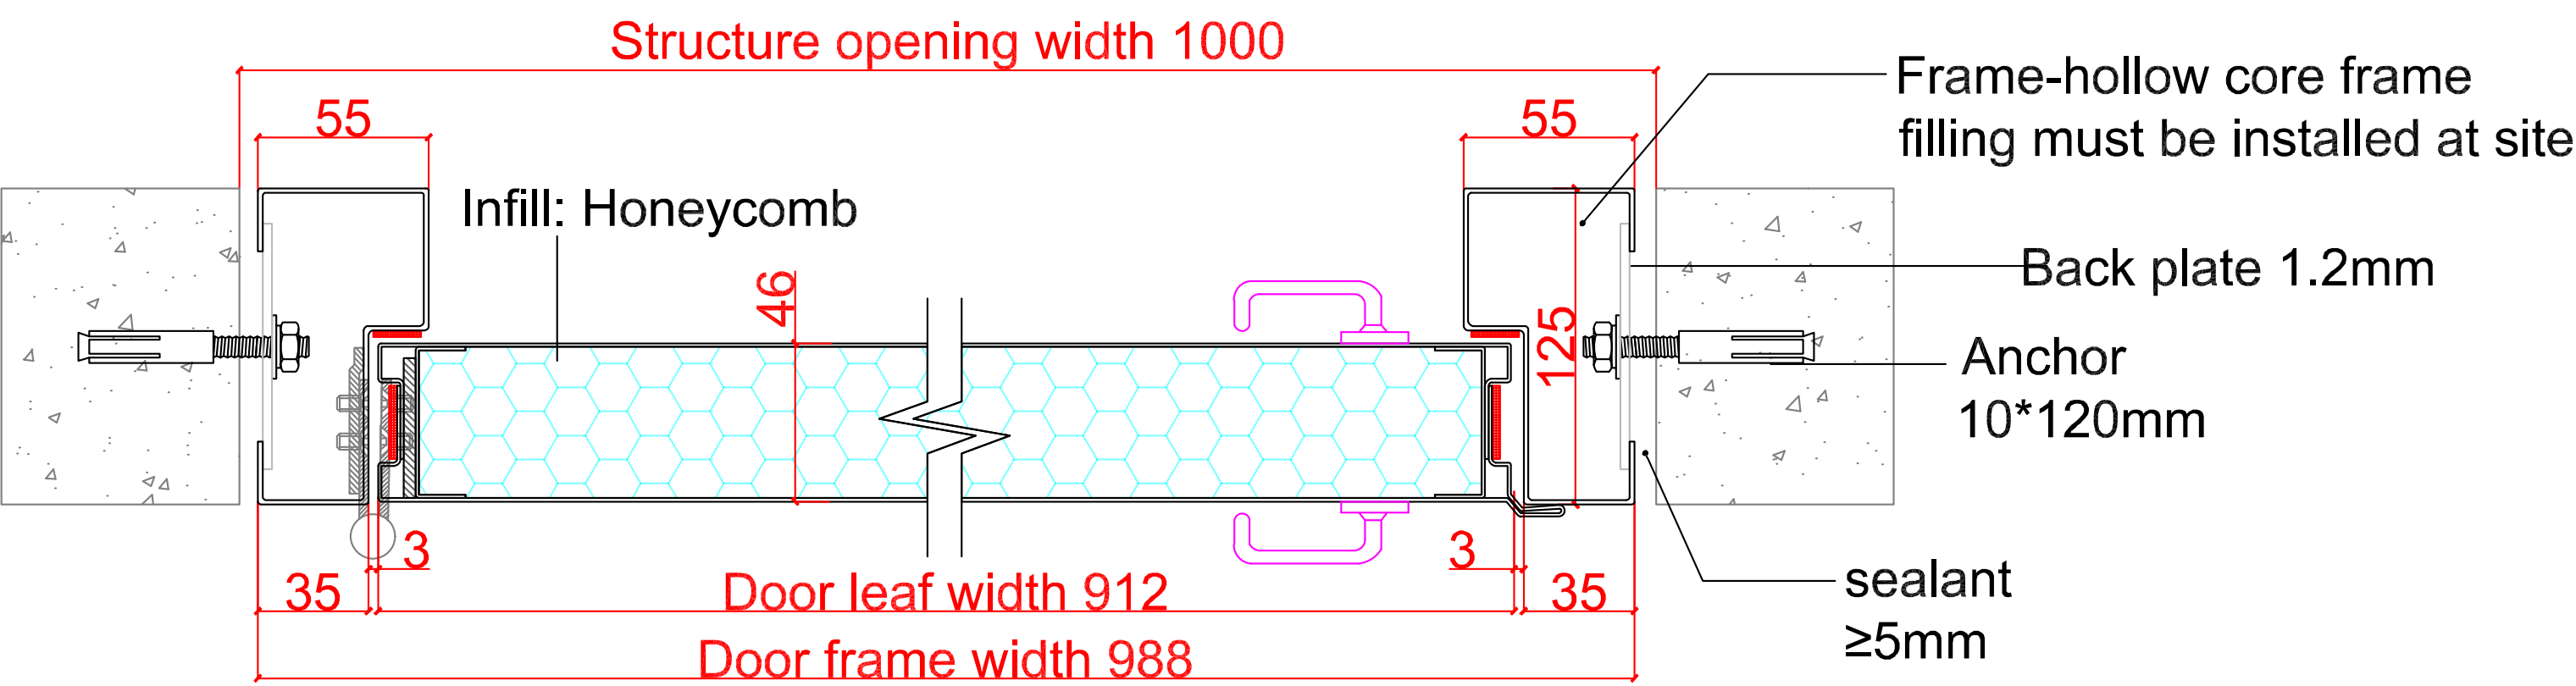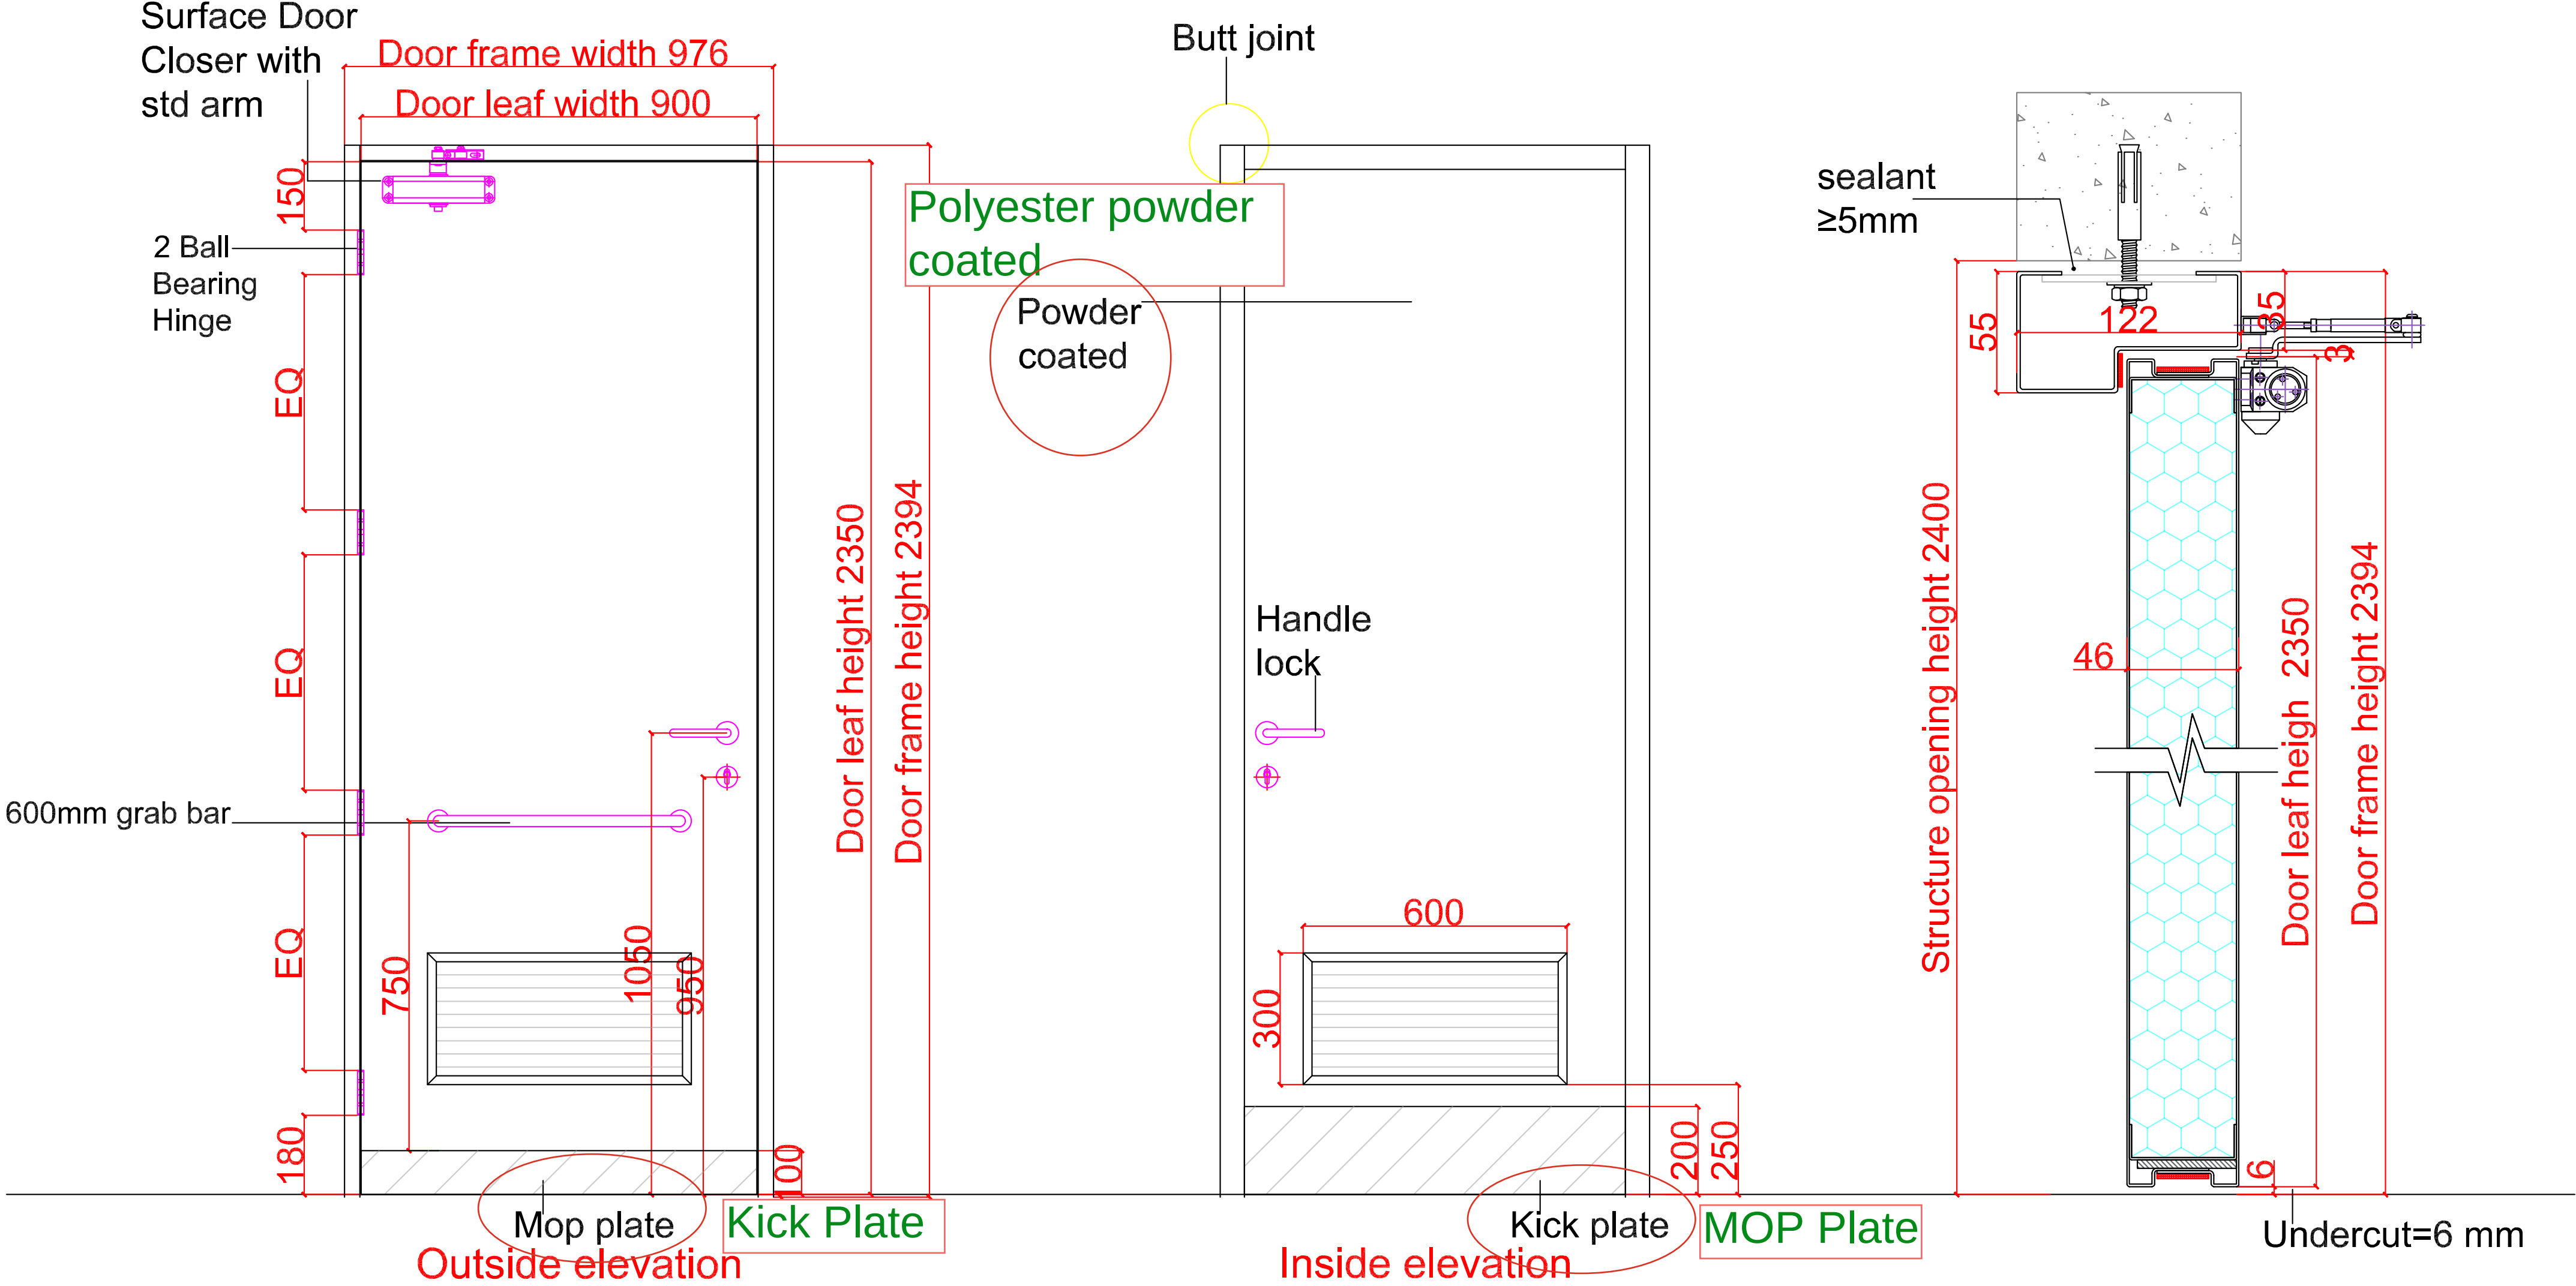


Hardware			
Name	Description	Qty	Remarks
Lock type	Mortise deadlock	1	
Hinge	4*4*3	4	
Door closer	184	1	
Door stop	No doorstop	1	
Kick plate	H:200mm		
Kick plate	H:100mm	1	
Louver	600*300mm	1	
Glass			
Smoke seal			
Door frame	1.2mm Galvanized steel sheet		
Door leaf	0.8mm Galvanized steel sheet		
Threshold			
Filling	Honeycomb		
Colour			

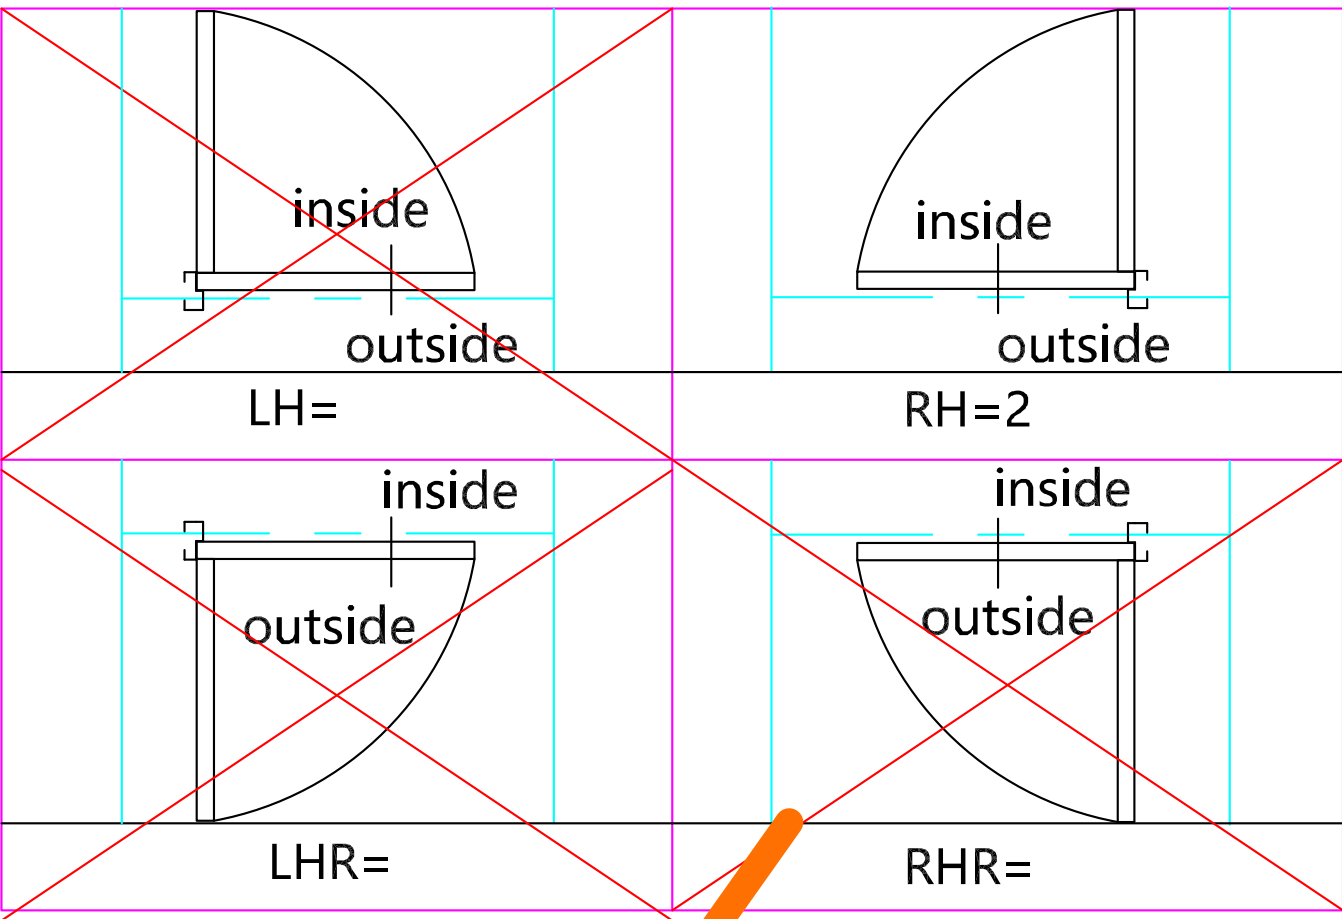


 Shanghai Xunzhong Industry Co., Ltd			
Project name			
By		Drawing title	
Design		Size	
Check		Qty	2
Review		Opening direction	
Approval		Date	2026.05.18
		Page No	21
Total Page	34	Diagram number	

SD2

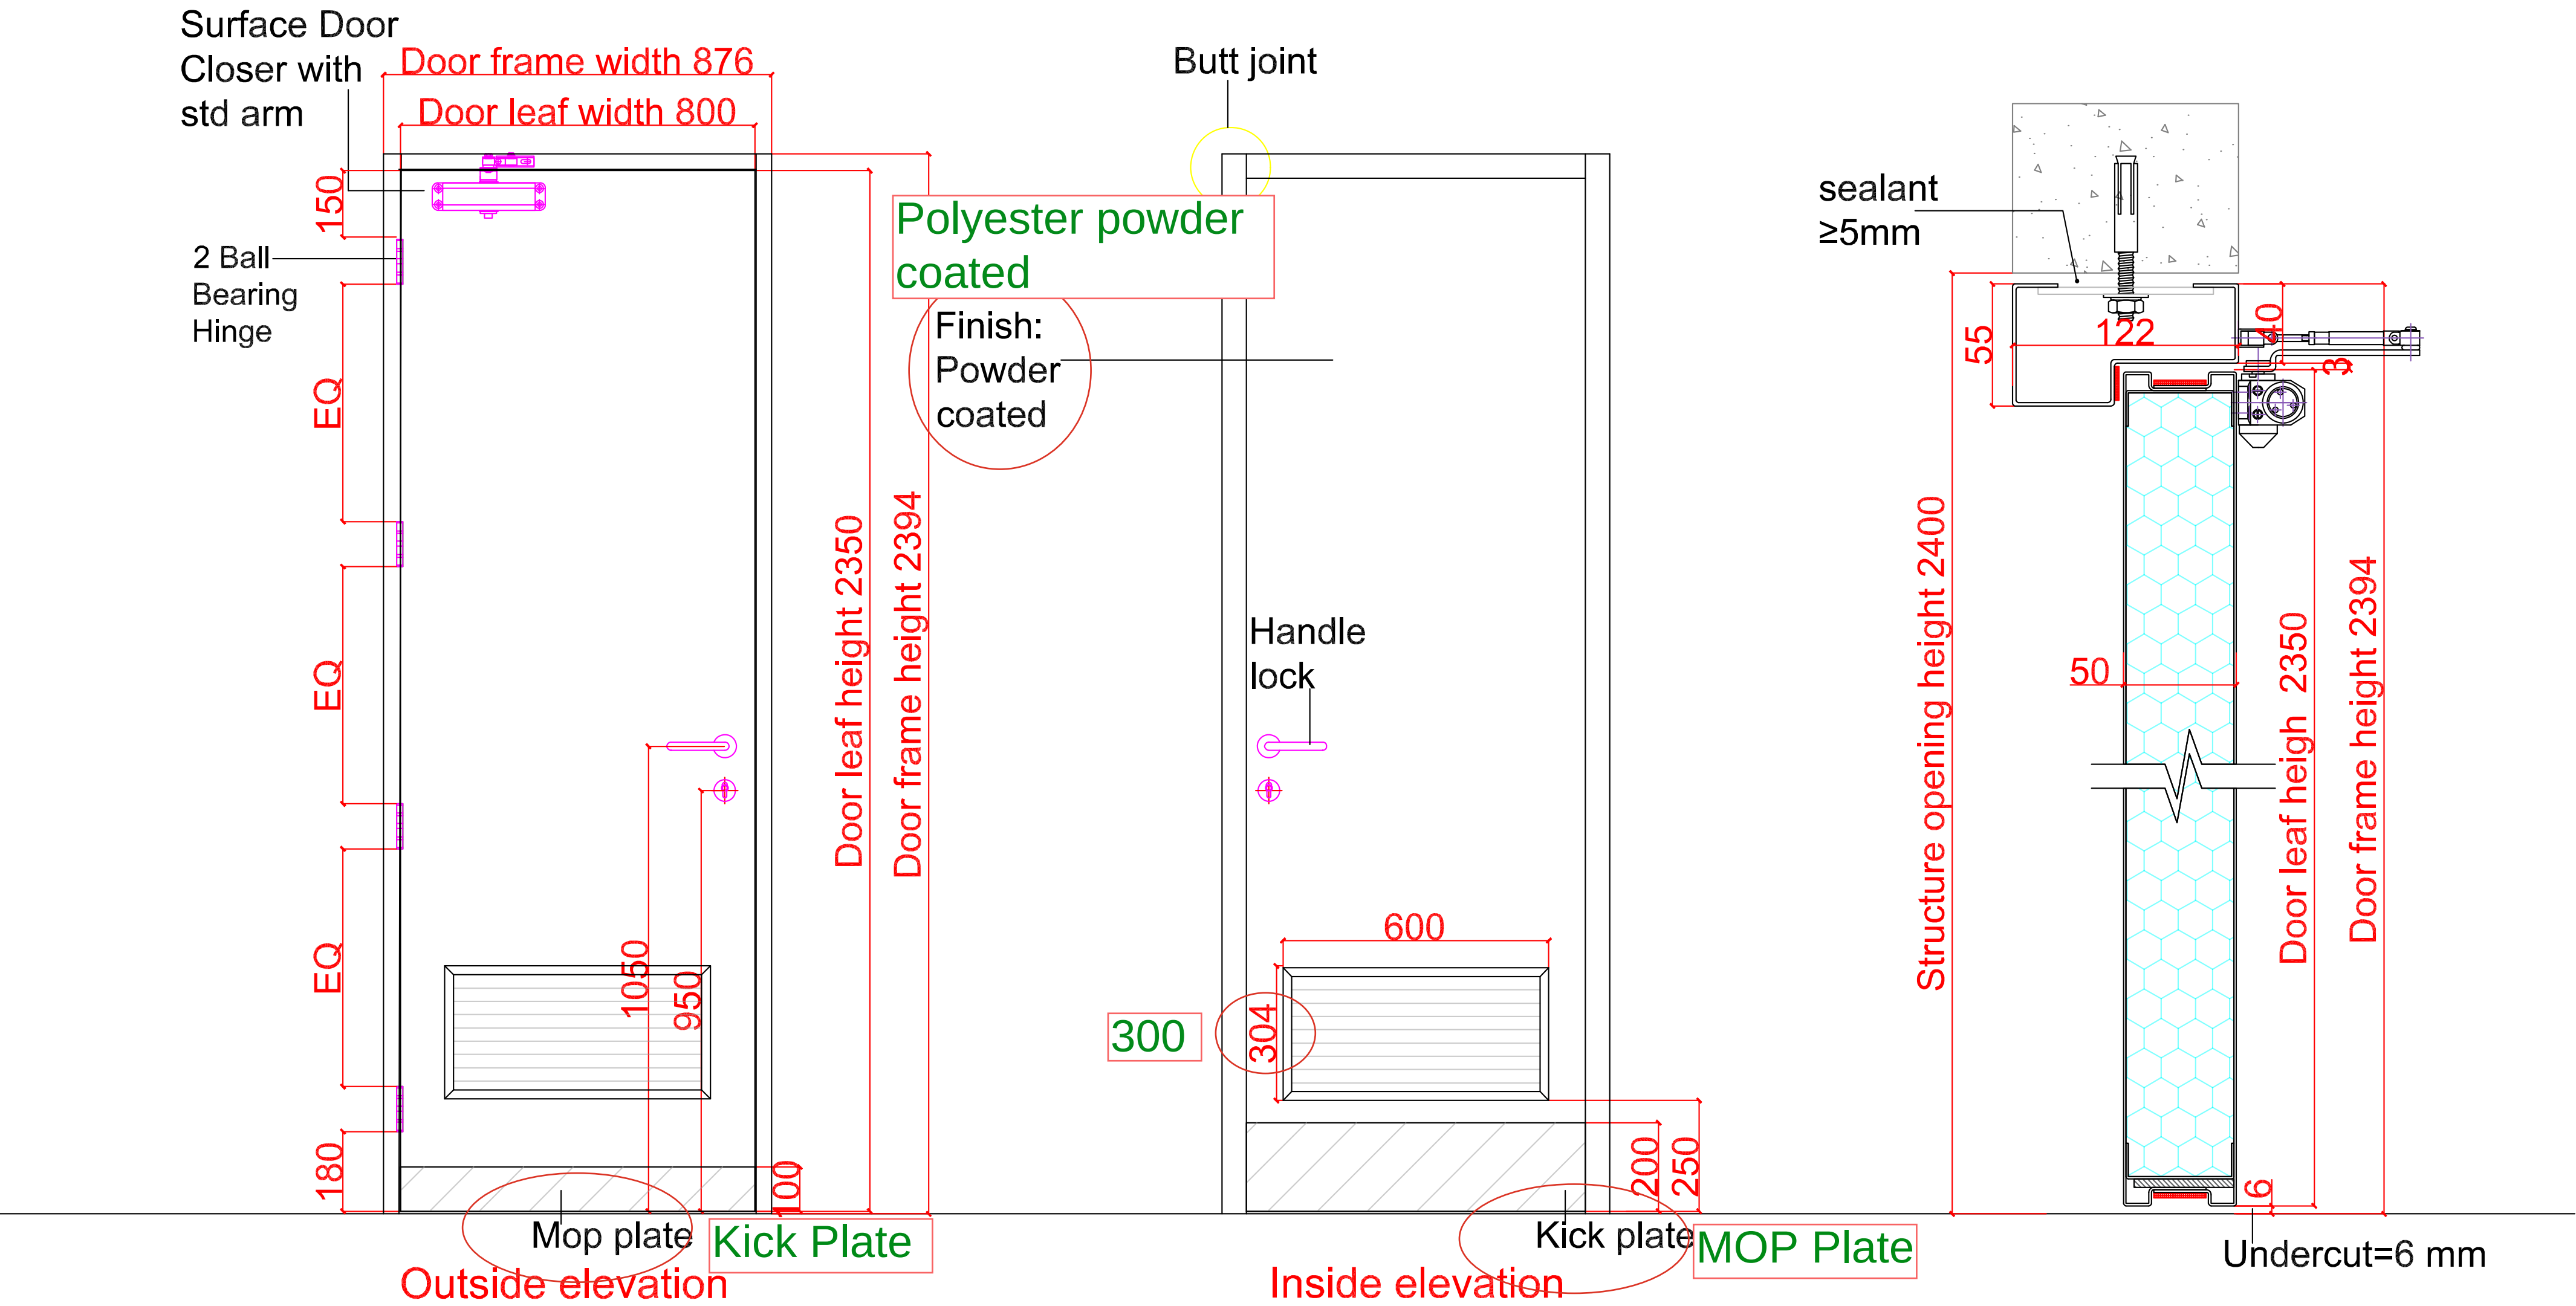


Hardware			
Name	Description	Qty	Remarks
Lock type	Mortise deadlock	1	
Hinge	4*4*3	4	
Door closer	184	1	
Door stop			
Kick plate	H:200mm	1	
Kick plate	H:100mm	1	
Louver	600*300mm	1	
Glass			
Smoke seal			
Door frame	1.2mm Galvanized steel sheet		
Door leaf	0.8mm Galvanized steel sheet		
Threshold			
Filling	Honeycomb		
Colour			

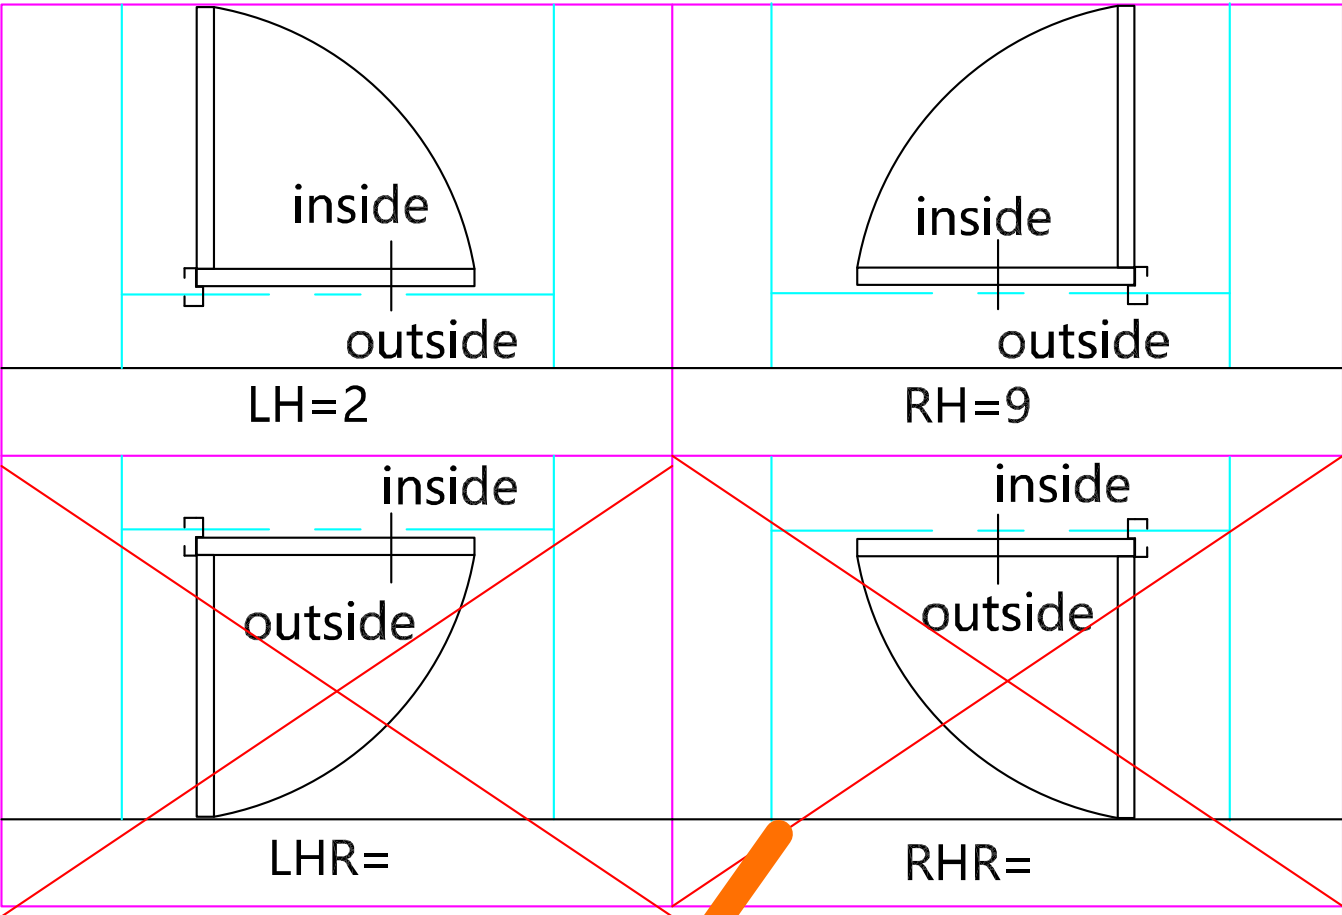


Shanghai Xunzhong Industry Co., Ltd

Project name

By		Drawing title	
Design		Size	
Check		Qty	11
Review		Opening direction	
Approval		Date	2026.05.18
		Page No	22
Total Page	34	Diagram number	

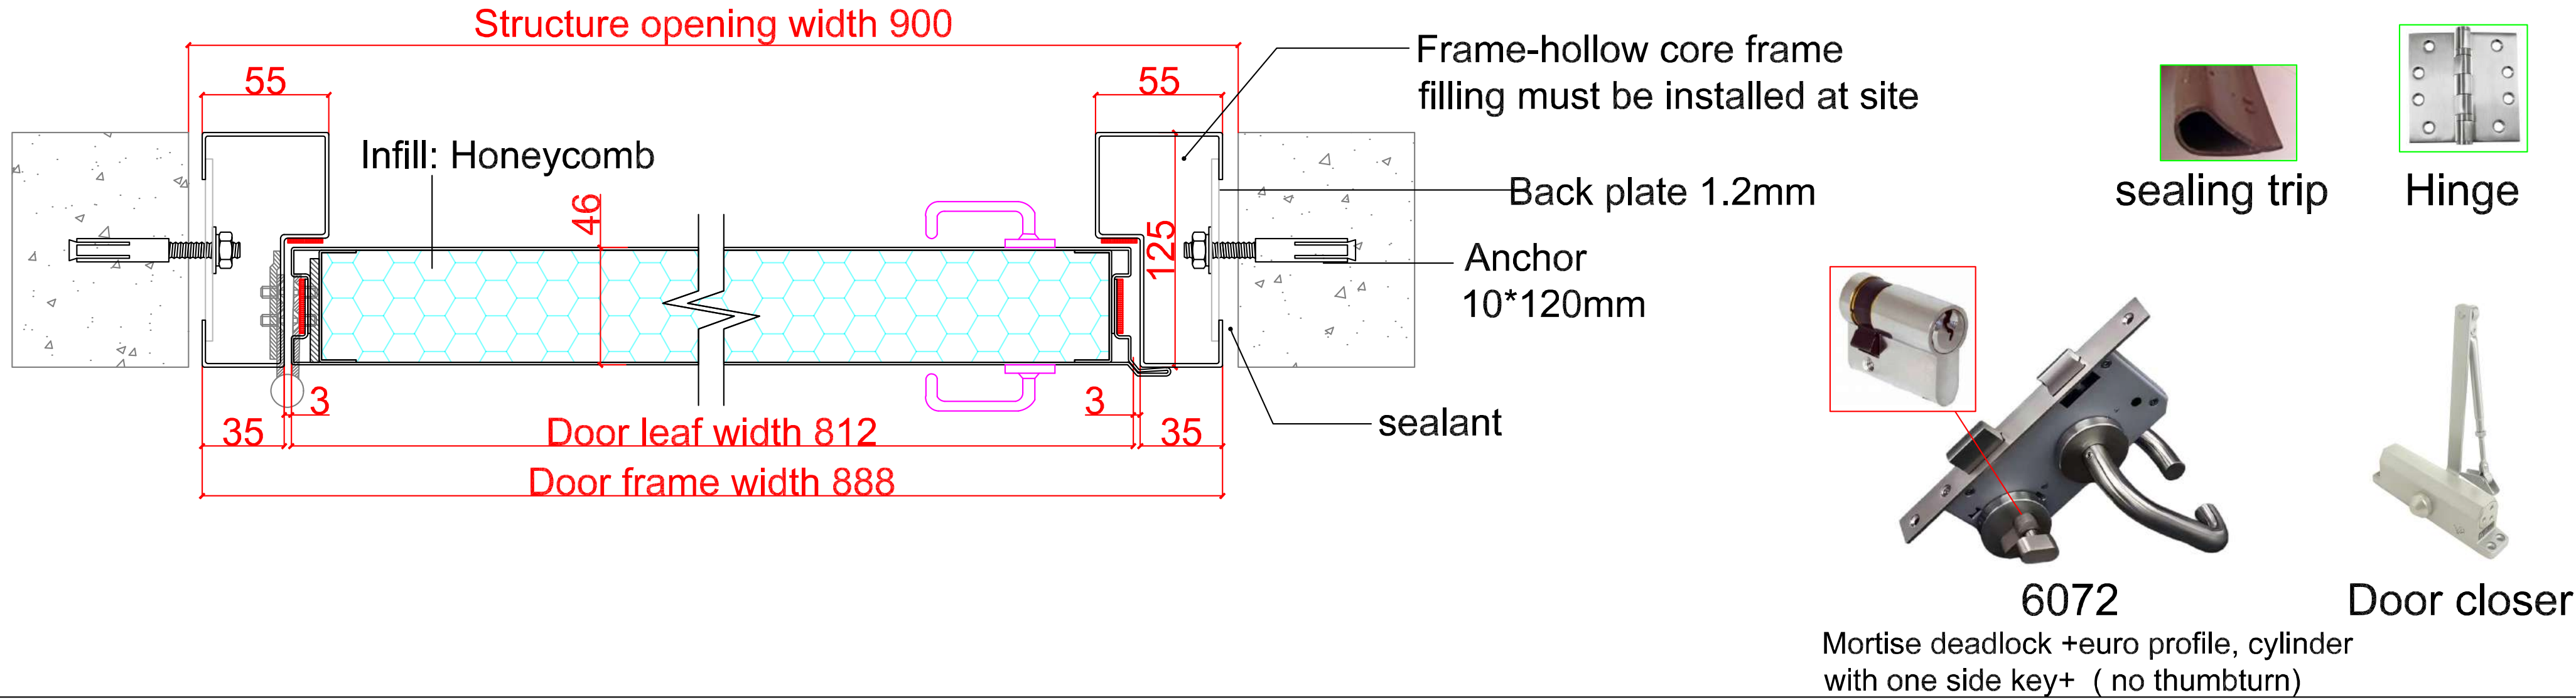



SD2a

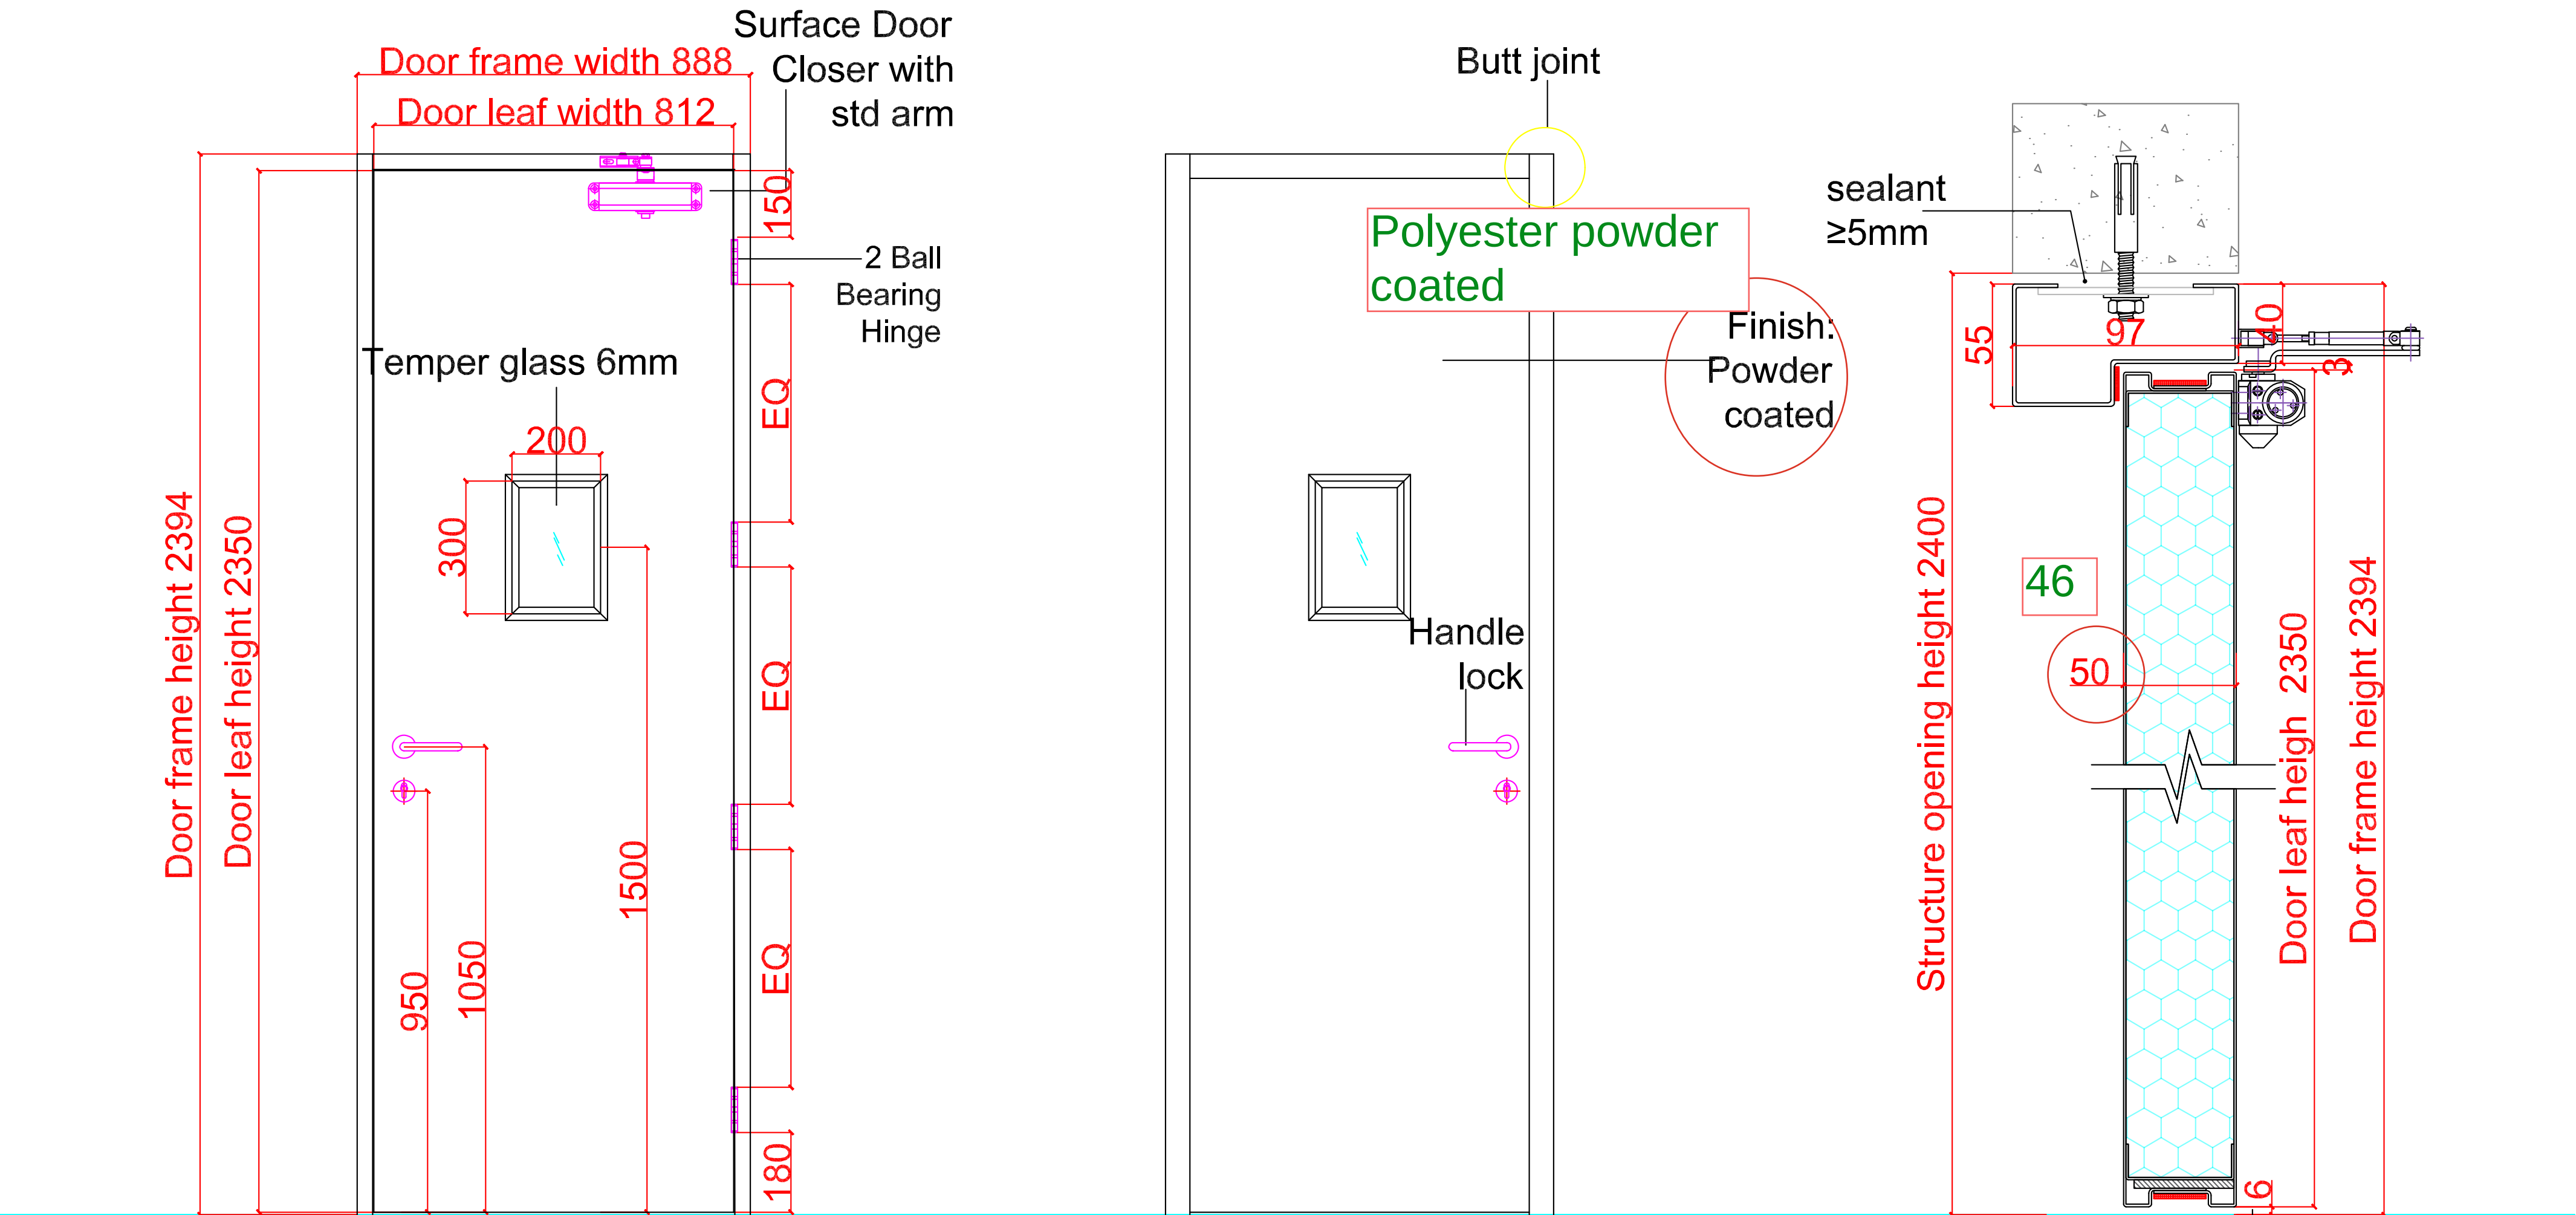


Outside elevation

Inside elevation

Undercut=6 mm

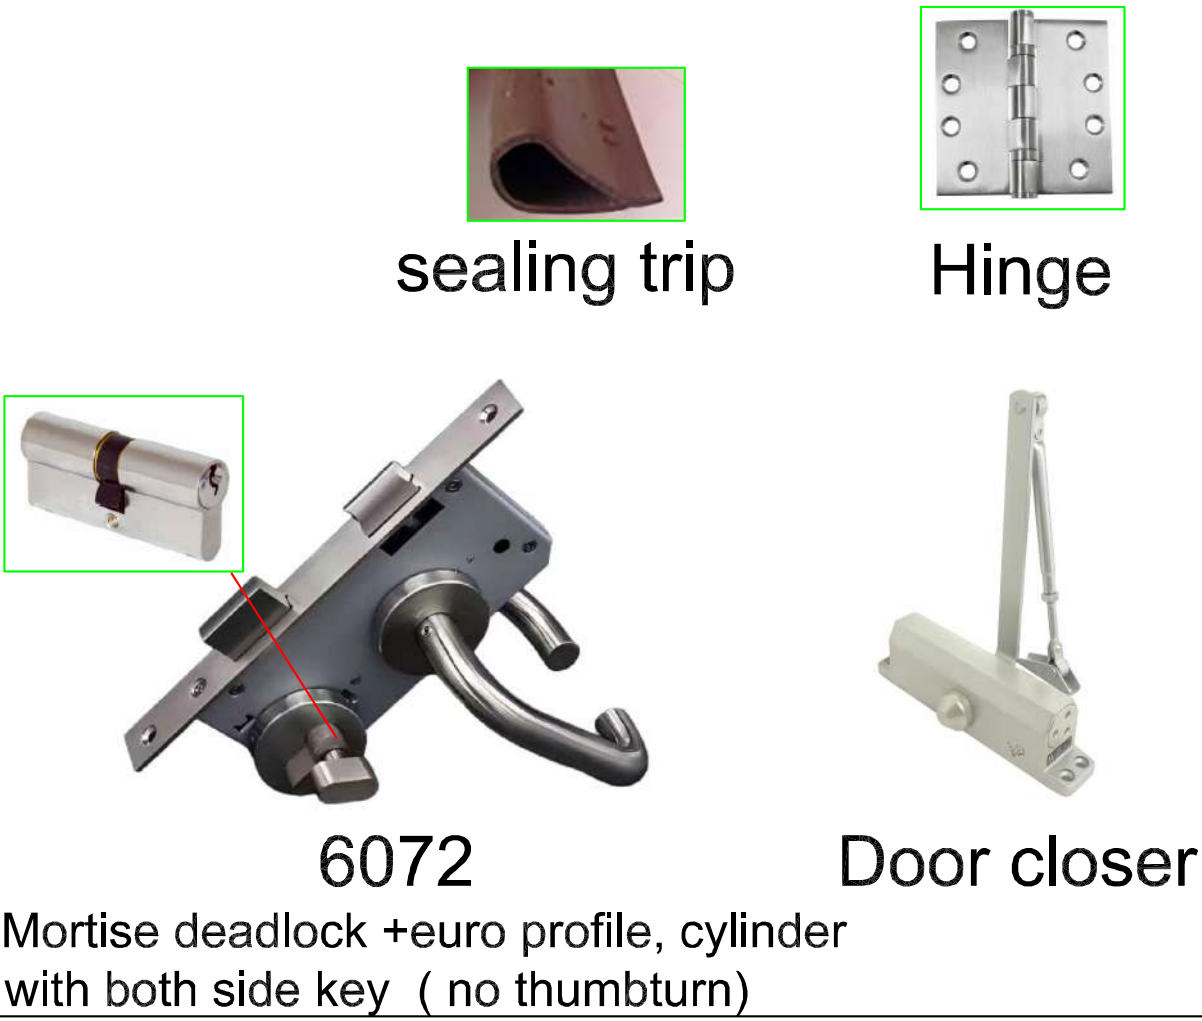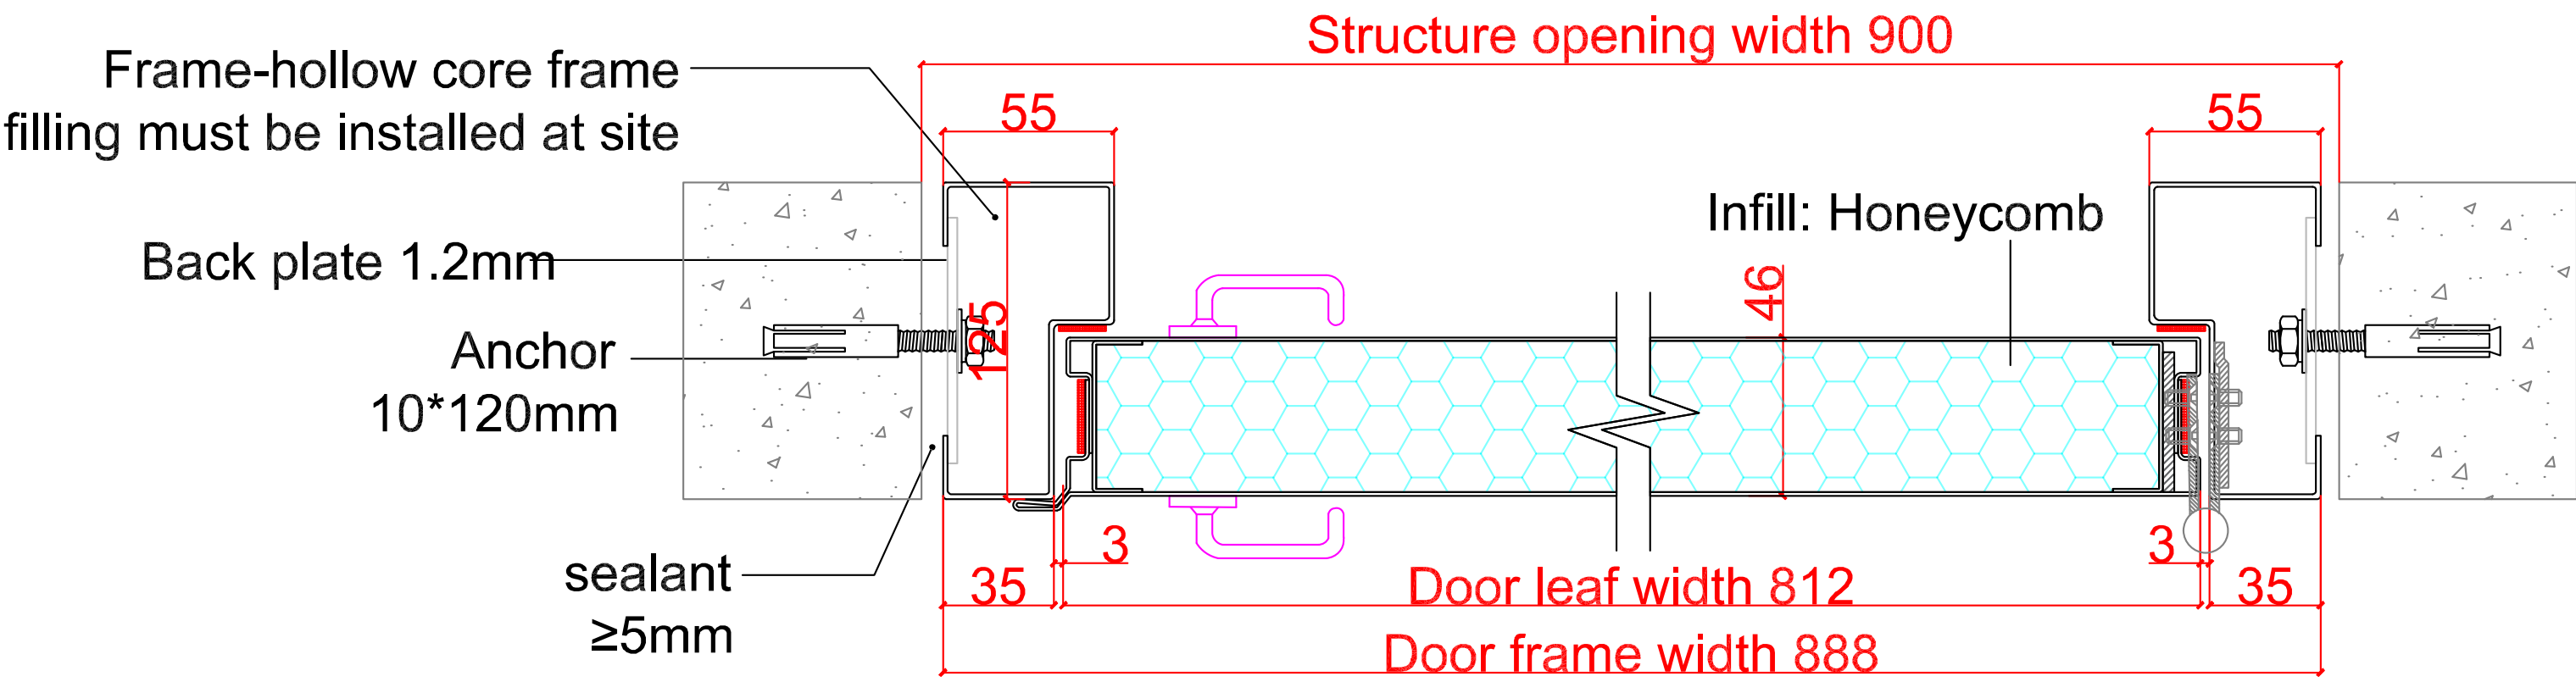

Hardware			
Name	Description	Qty	Remarks
Lock type	Mortise lock	1	deadlock
Hinge	4*4*3	4	
Door closer	184	1	
Door stop			
Glass	200*300mm	1	
Smoke seal			
Door frame	1.2mm Galvanized steel sheet		
Door leaf	0.8mm Galvanized steel sheet		
Threshold			
Filling	Honeycomb		
Colour			

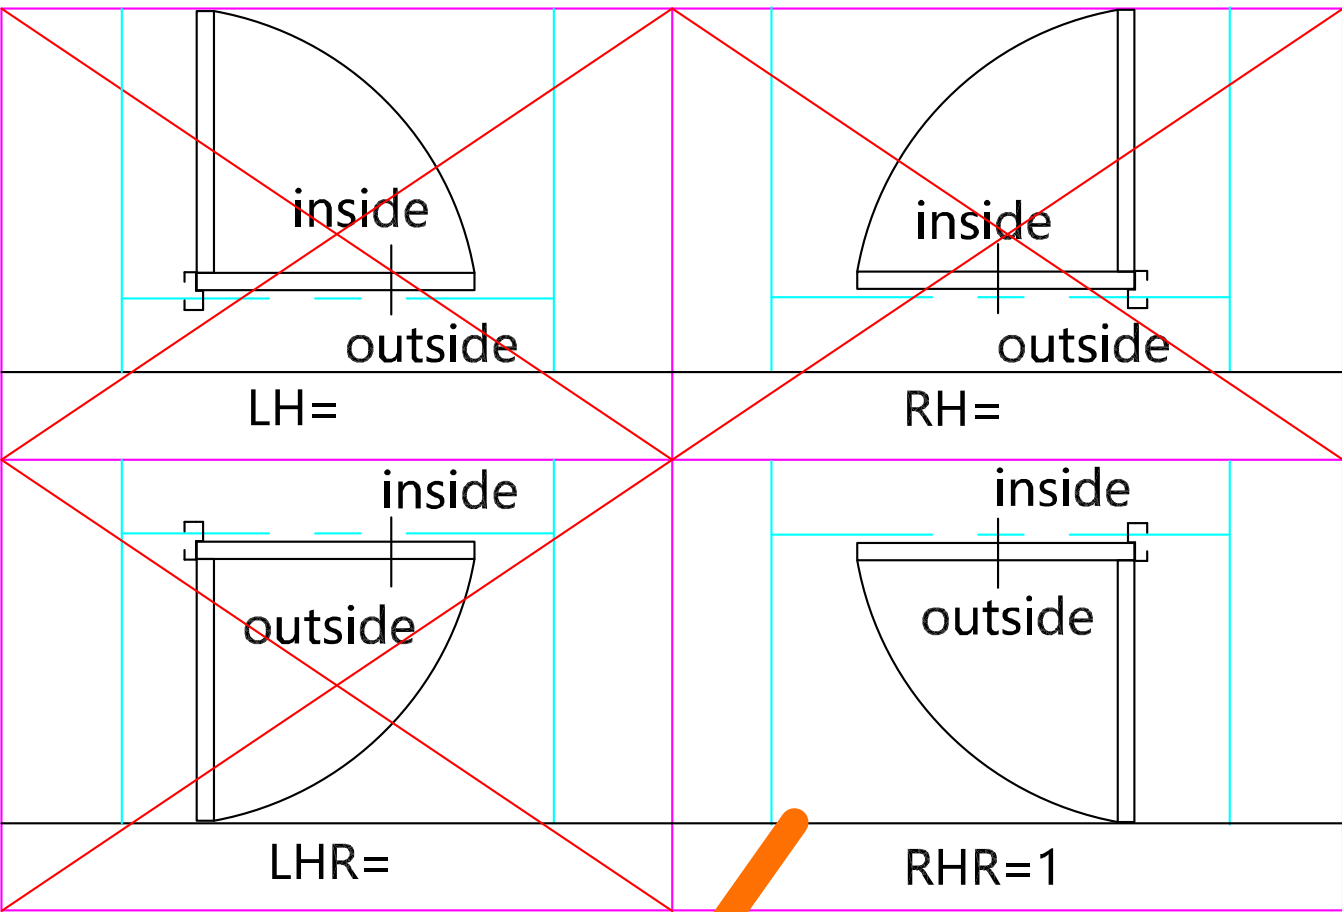


Shanghai Xunzhong Industry Co., Ltd

Project name


By		Drawing title	
Design		Size	
Check		Qty	1
Review		Opening direction	
Approval		Date	2026.05.18
		Page No	23
Total Page	34	Diagram number	

Polyester powder coated



Finish:
Powder
coated

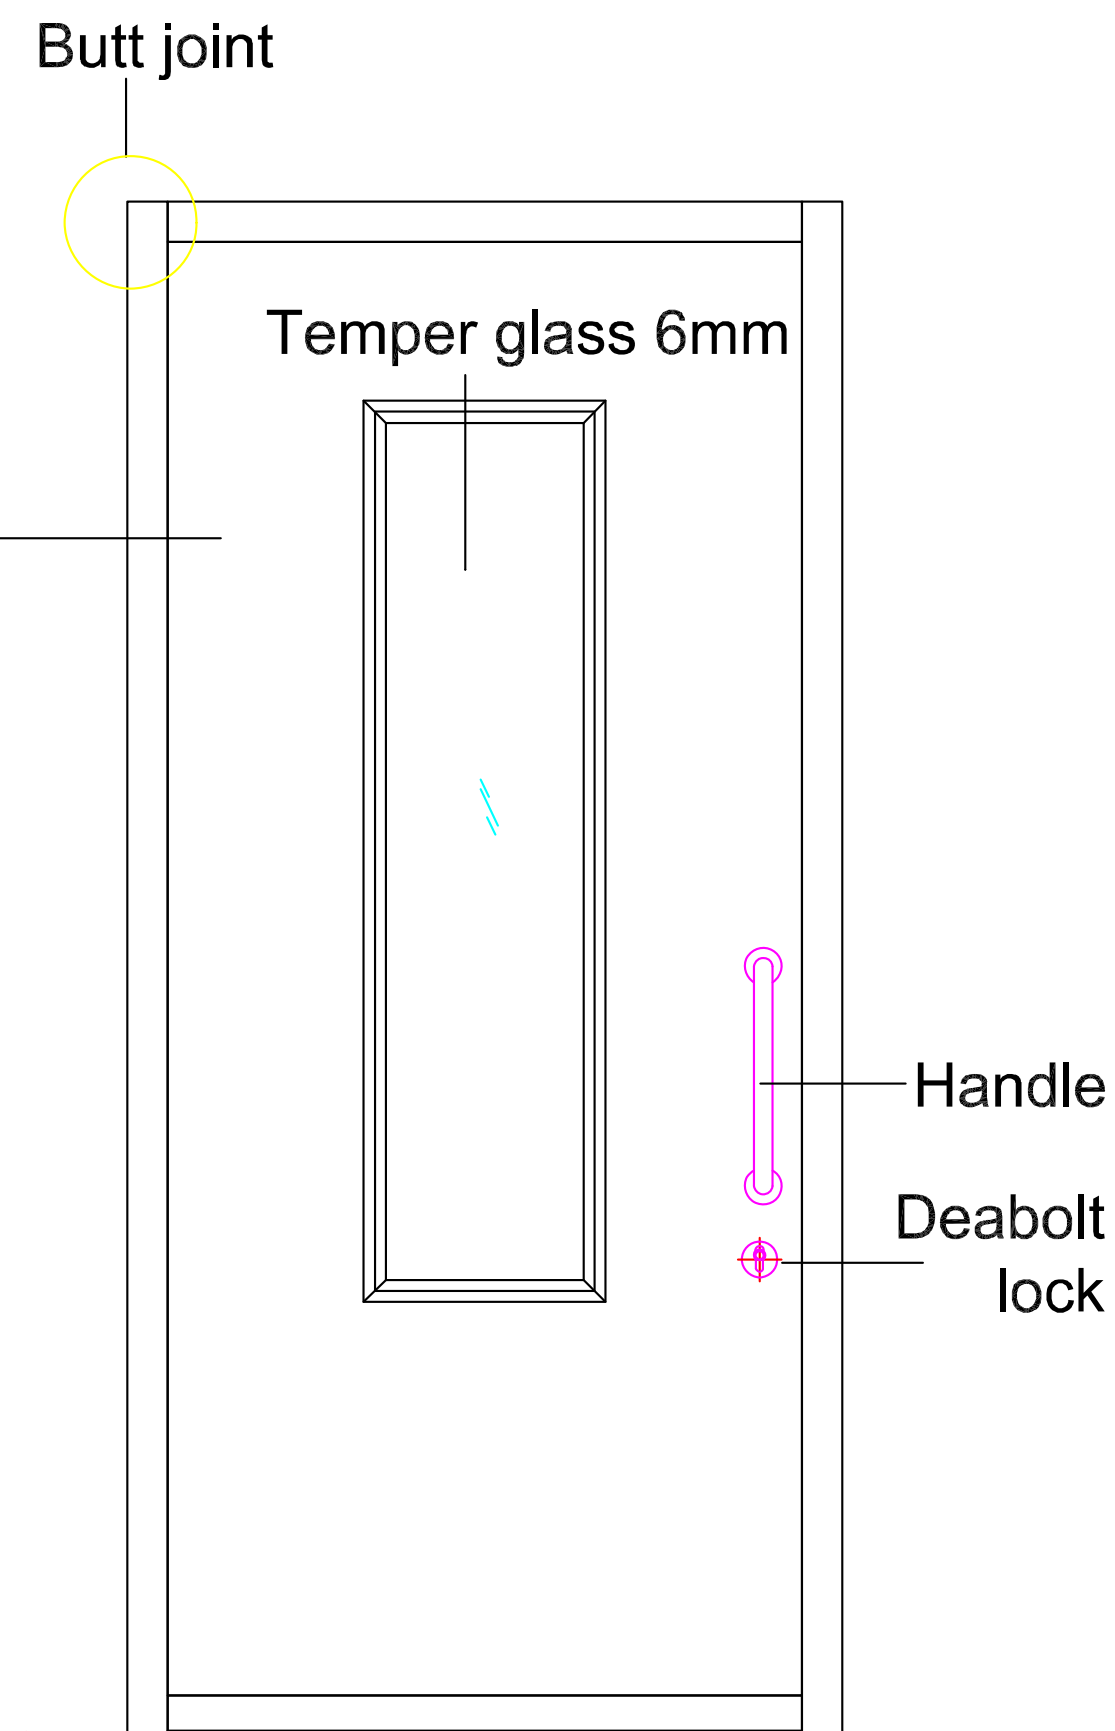

Outside elevation

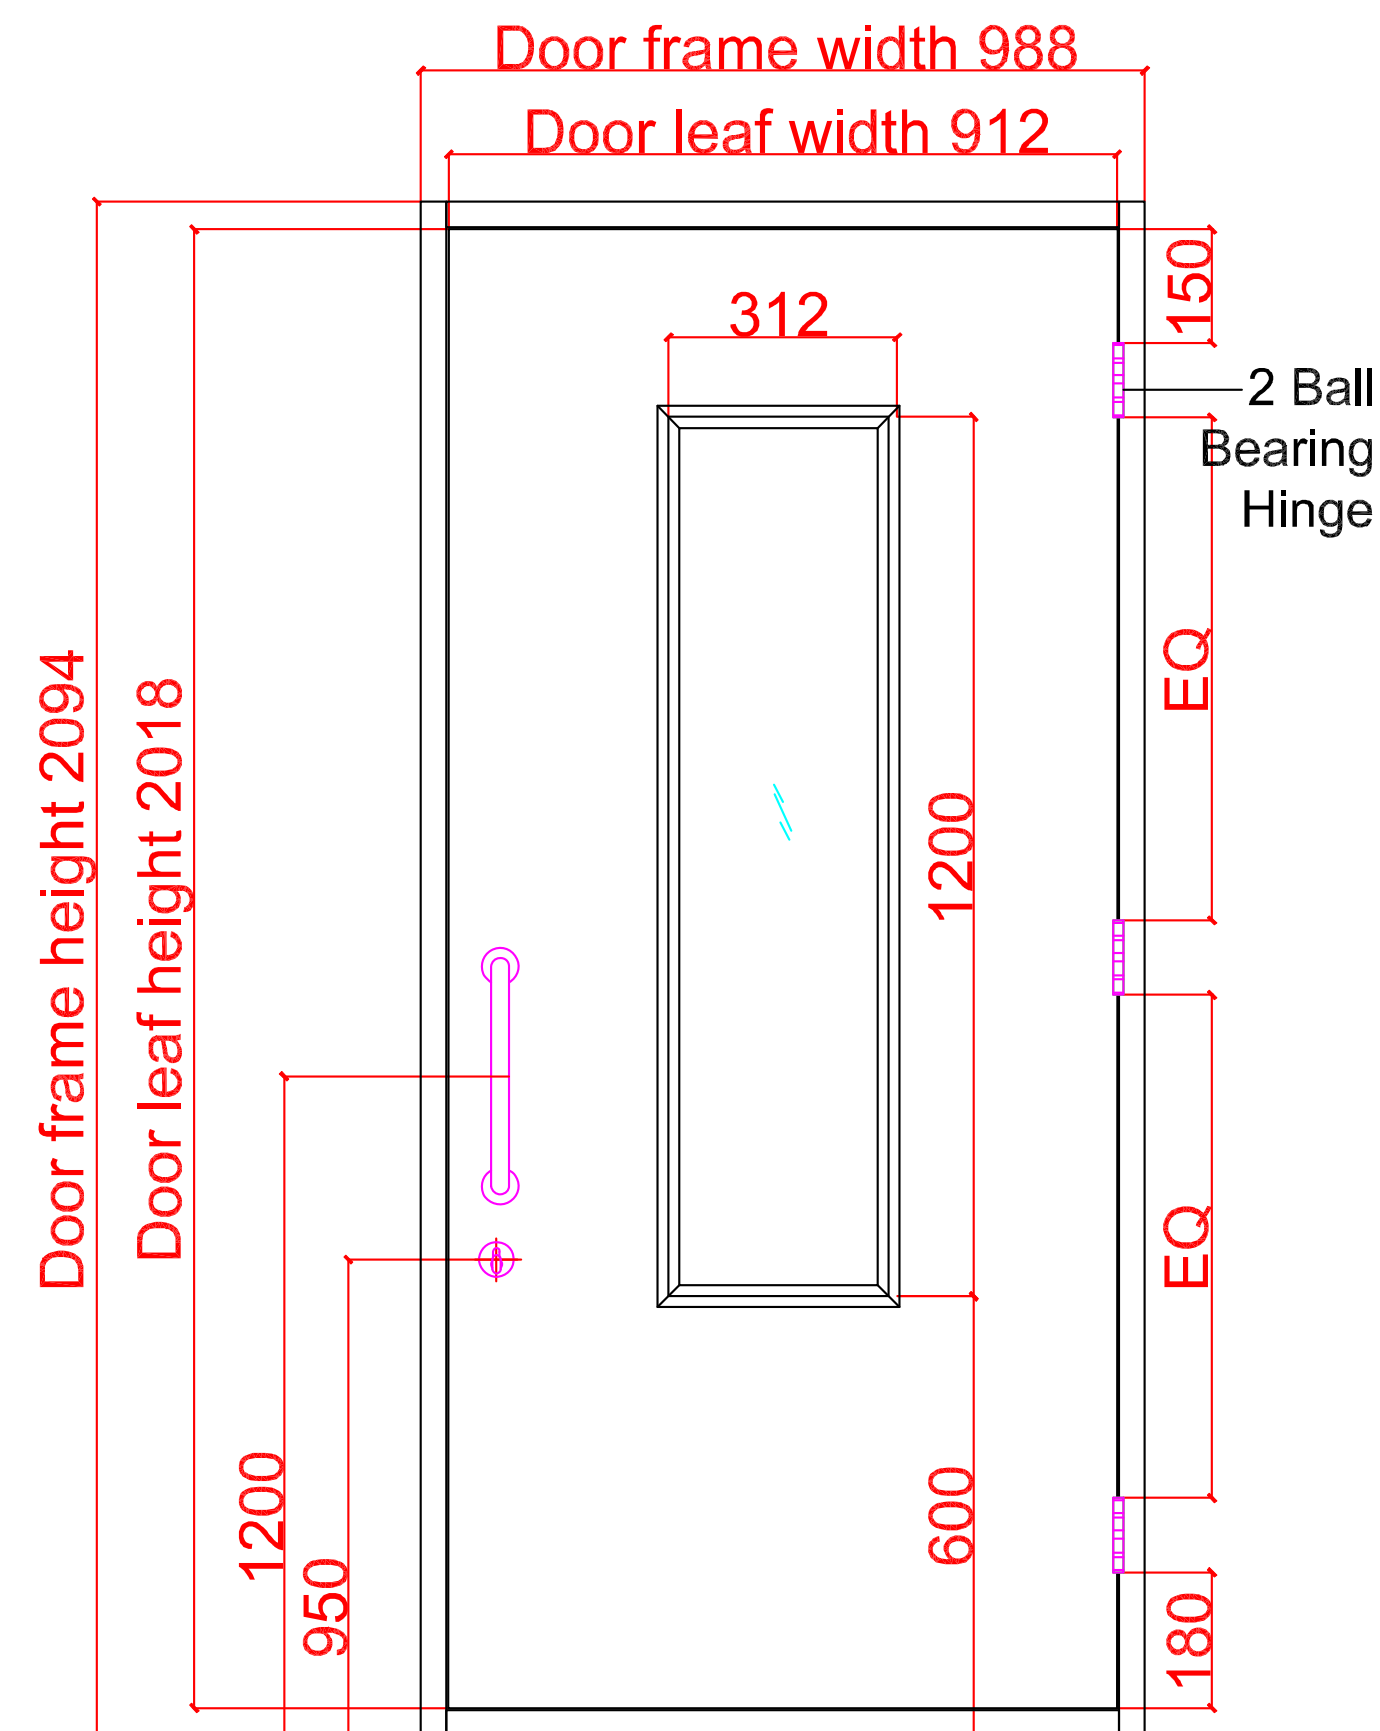

Inside elevation

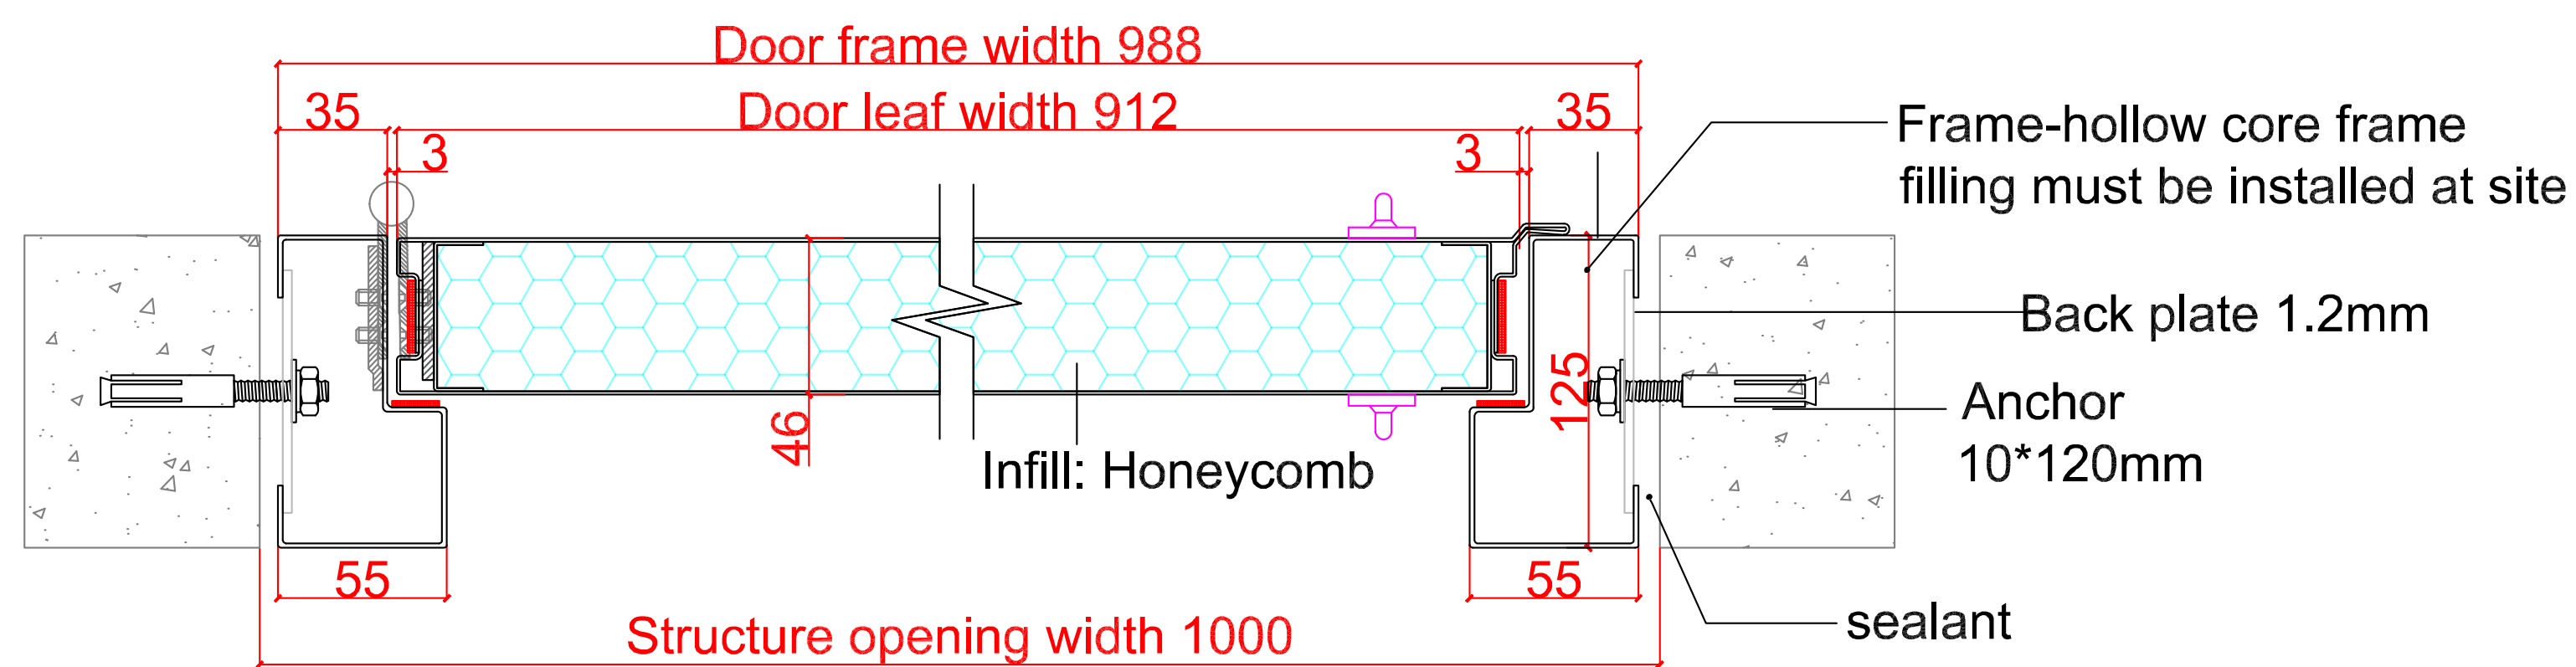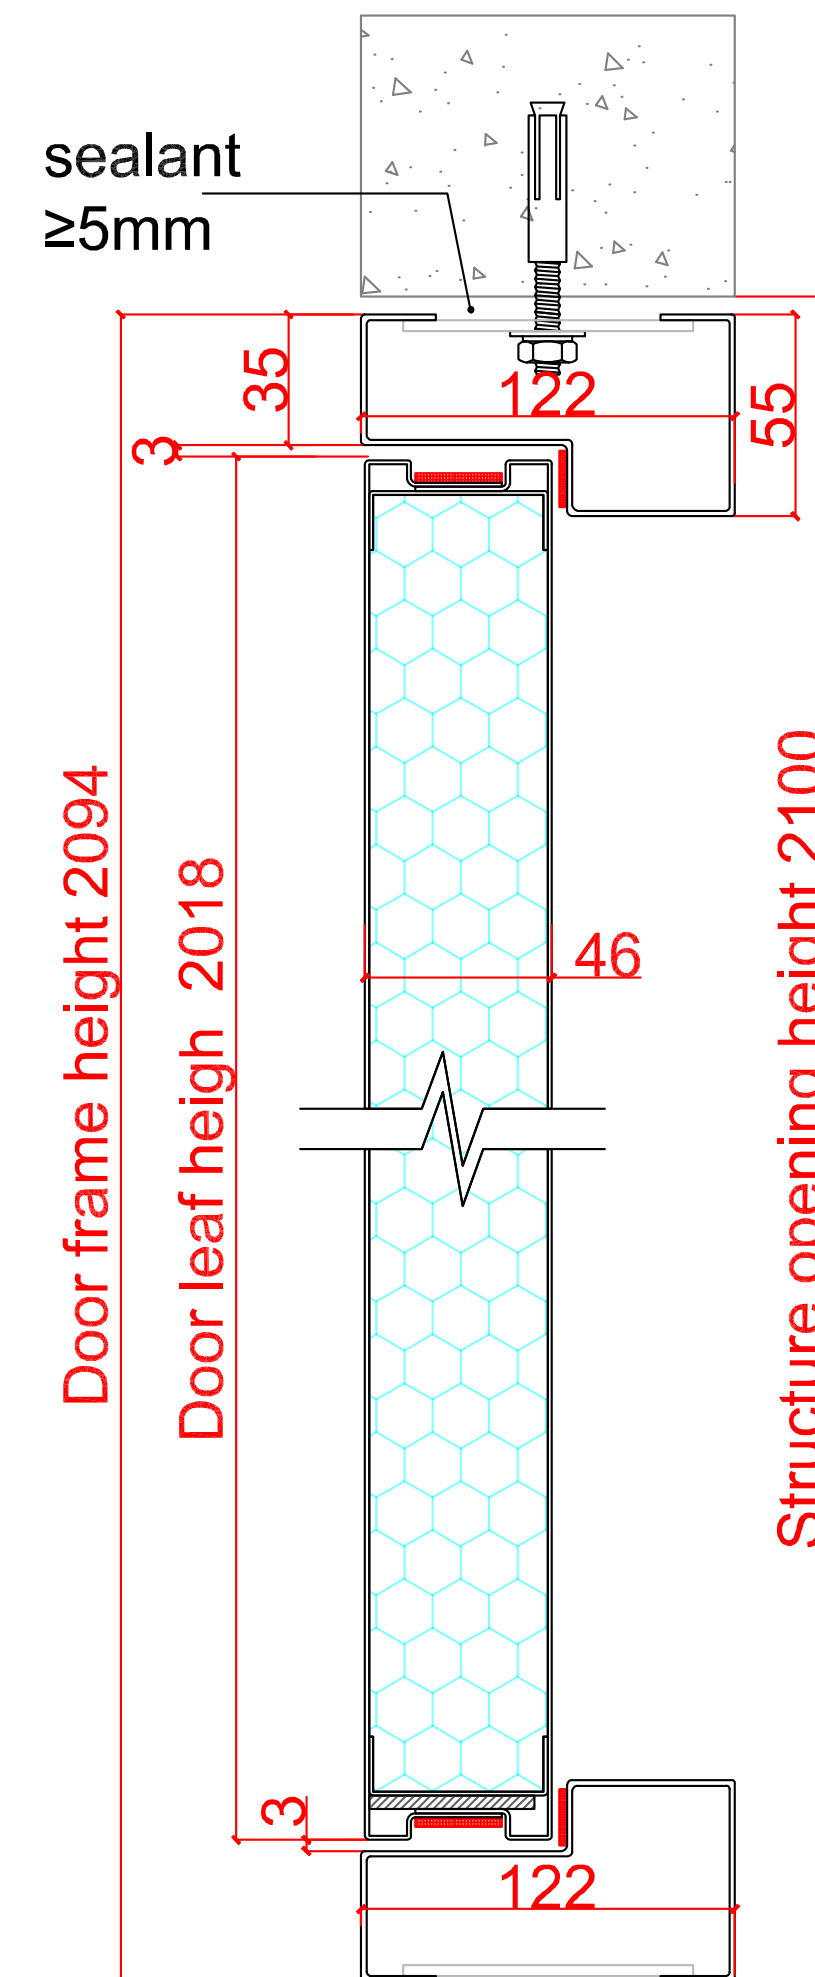

Hinge




sealing trip




Deadlock

Mortise deadlock +euro profile, cylinder with one side key+ (no thumbturn)

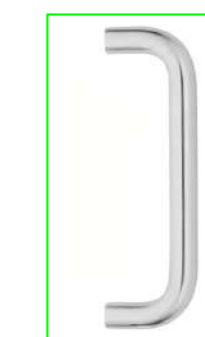

D type handle

Hardware			
Name	Description	Qty	Remarks
Lock type	Deadlock+Handle	1	
Hinge	4*4*3	3	
Glass	300*1200mm	1	
Smoke seal			
Door frame	1.2mm Galvanized steel sheet		
Door leaf	0.8mm Galvanized steel sheet		
Threshold			
Filling	Honeycomb		
Colour			

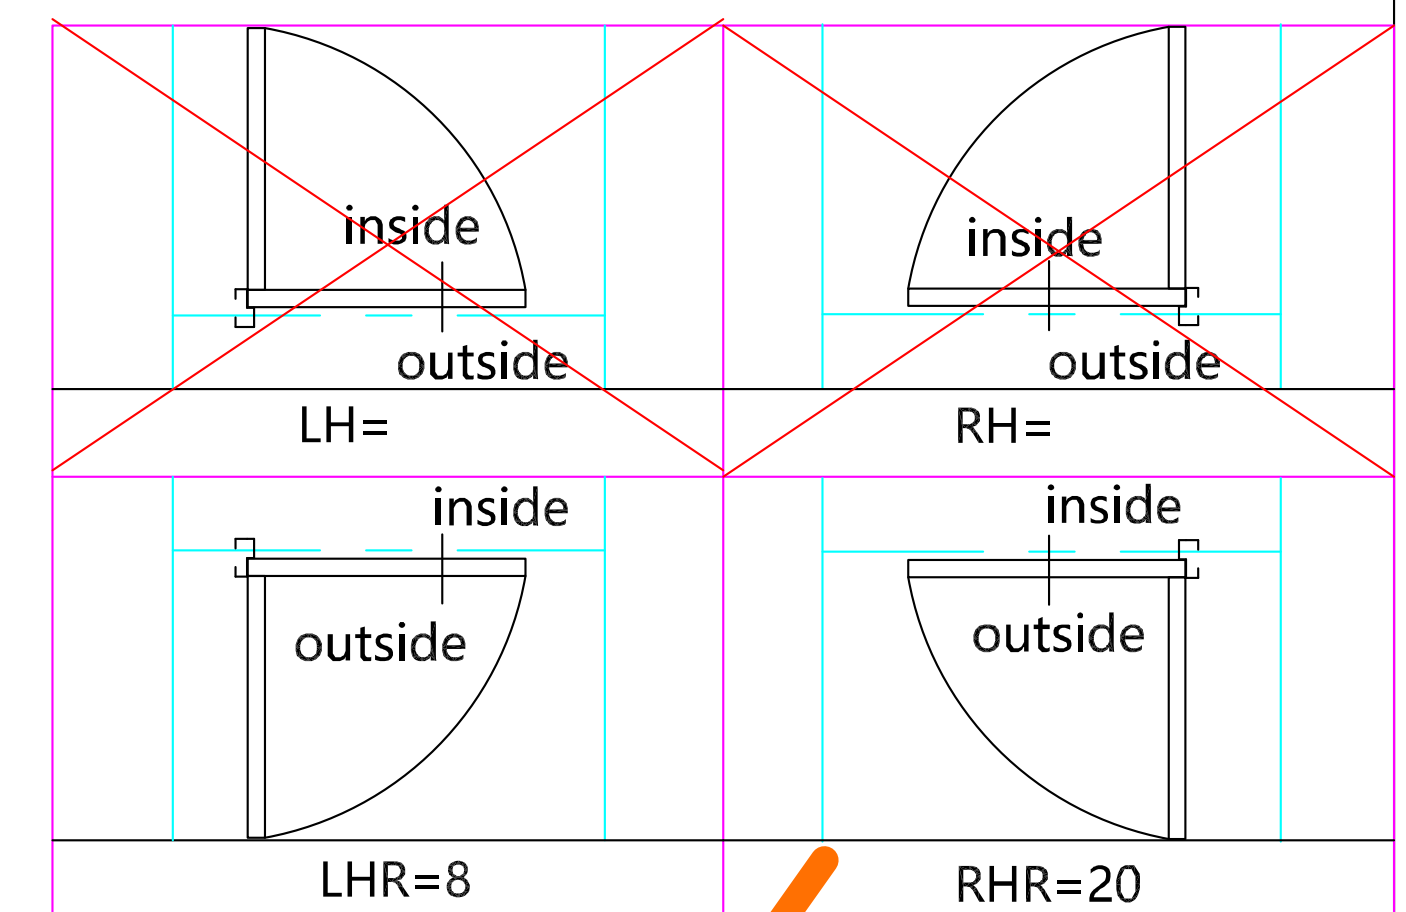


Shanghai Xunzhong Industry Co., Ltd


Project name

By		Drawing title	
Design		Size	
Check		Qty	28
Review		Opening direction	
Approval		Date	2026.05.18
		Page No	24
Total Page	34	Diagram number	



SD3a

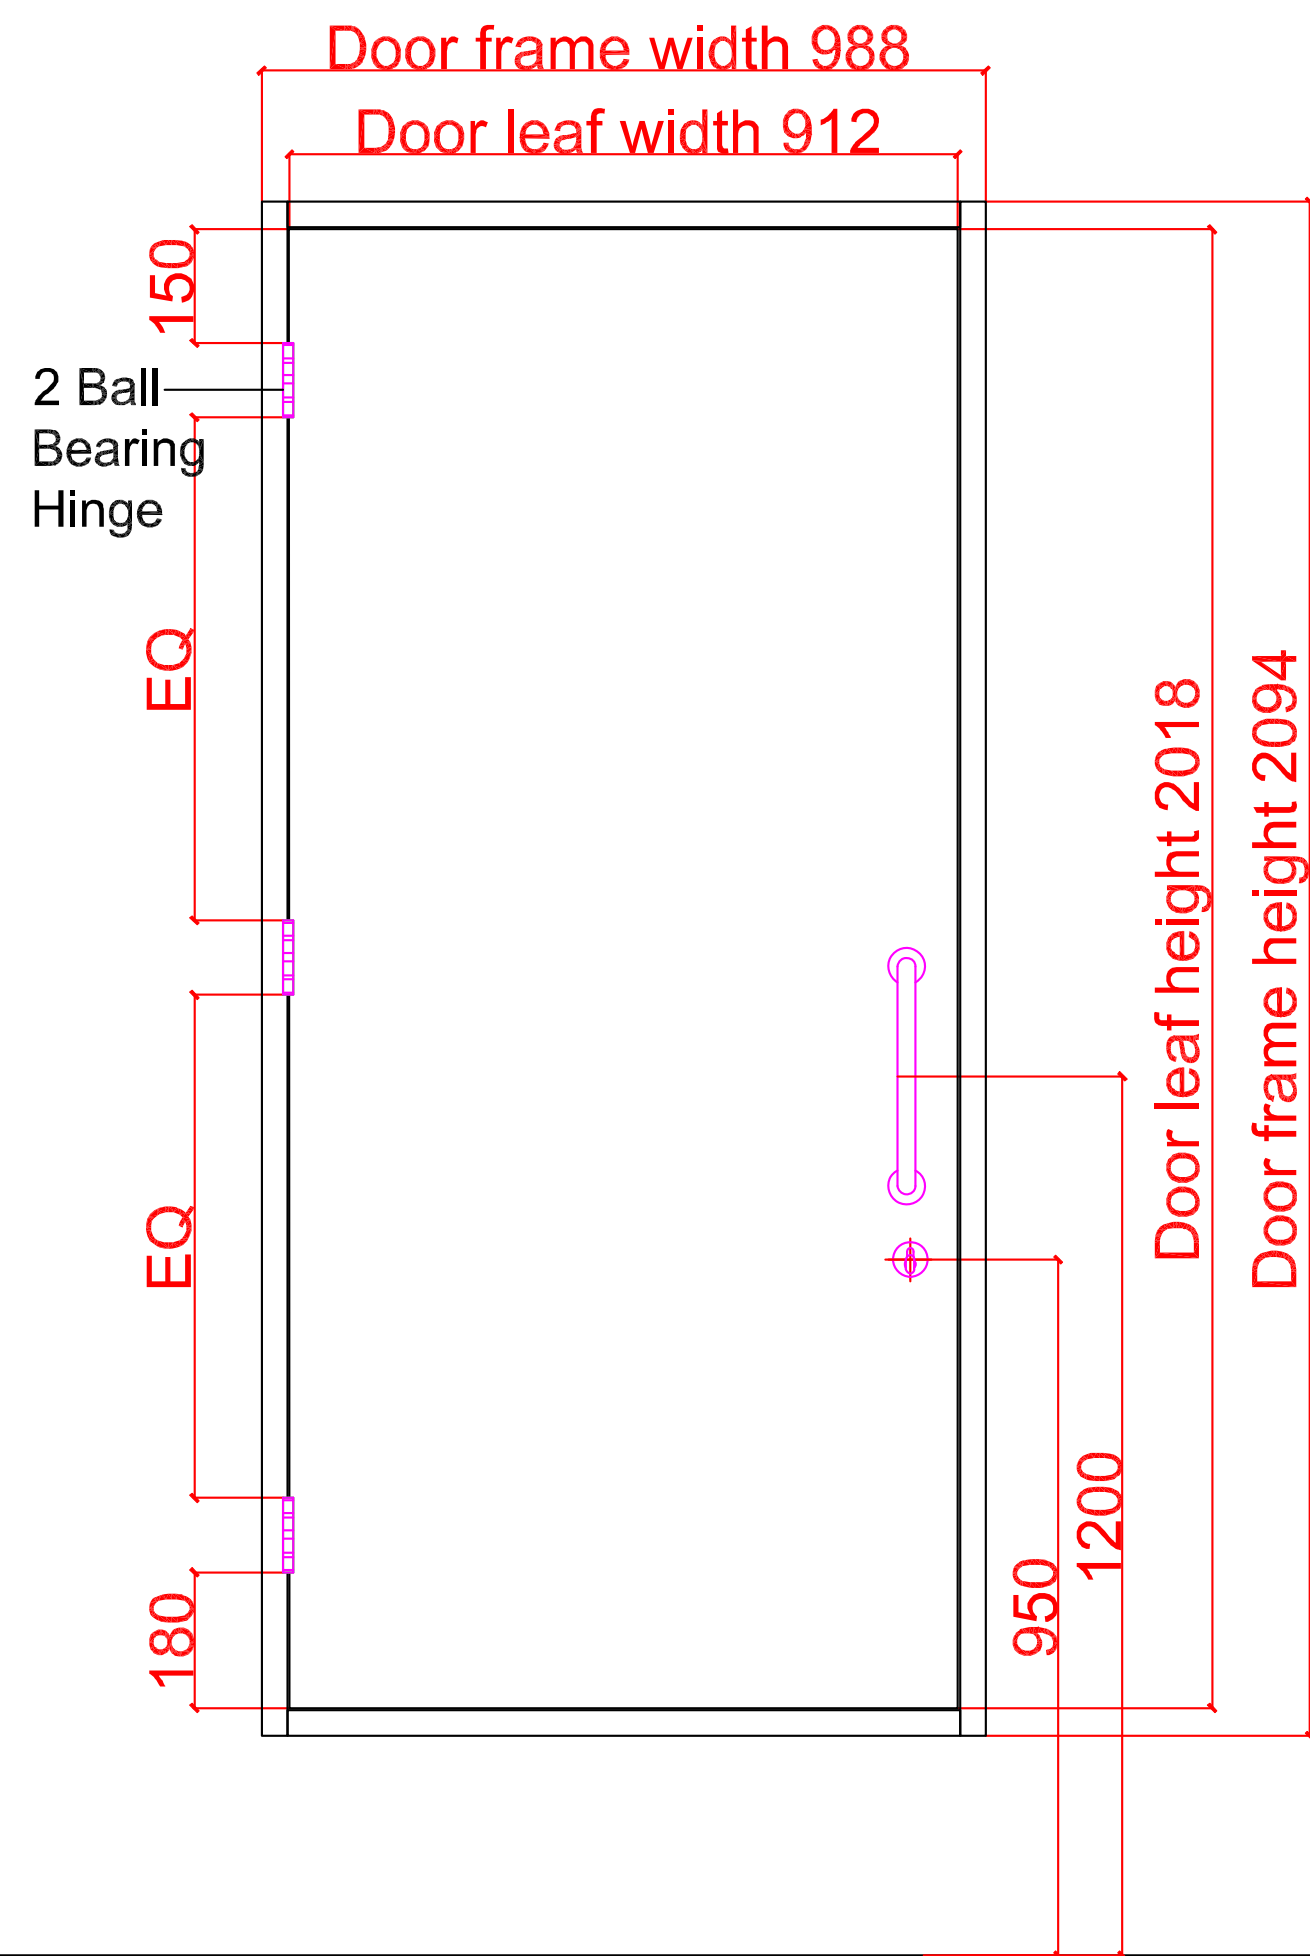

Outside elevation

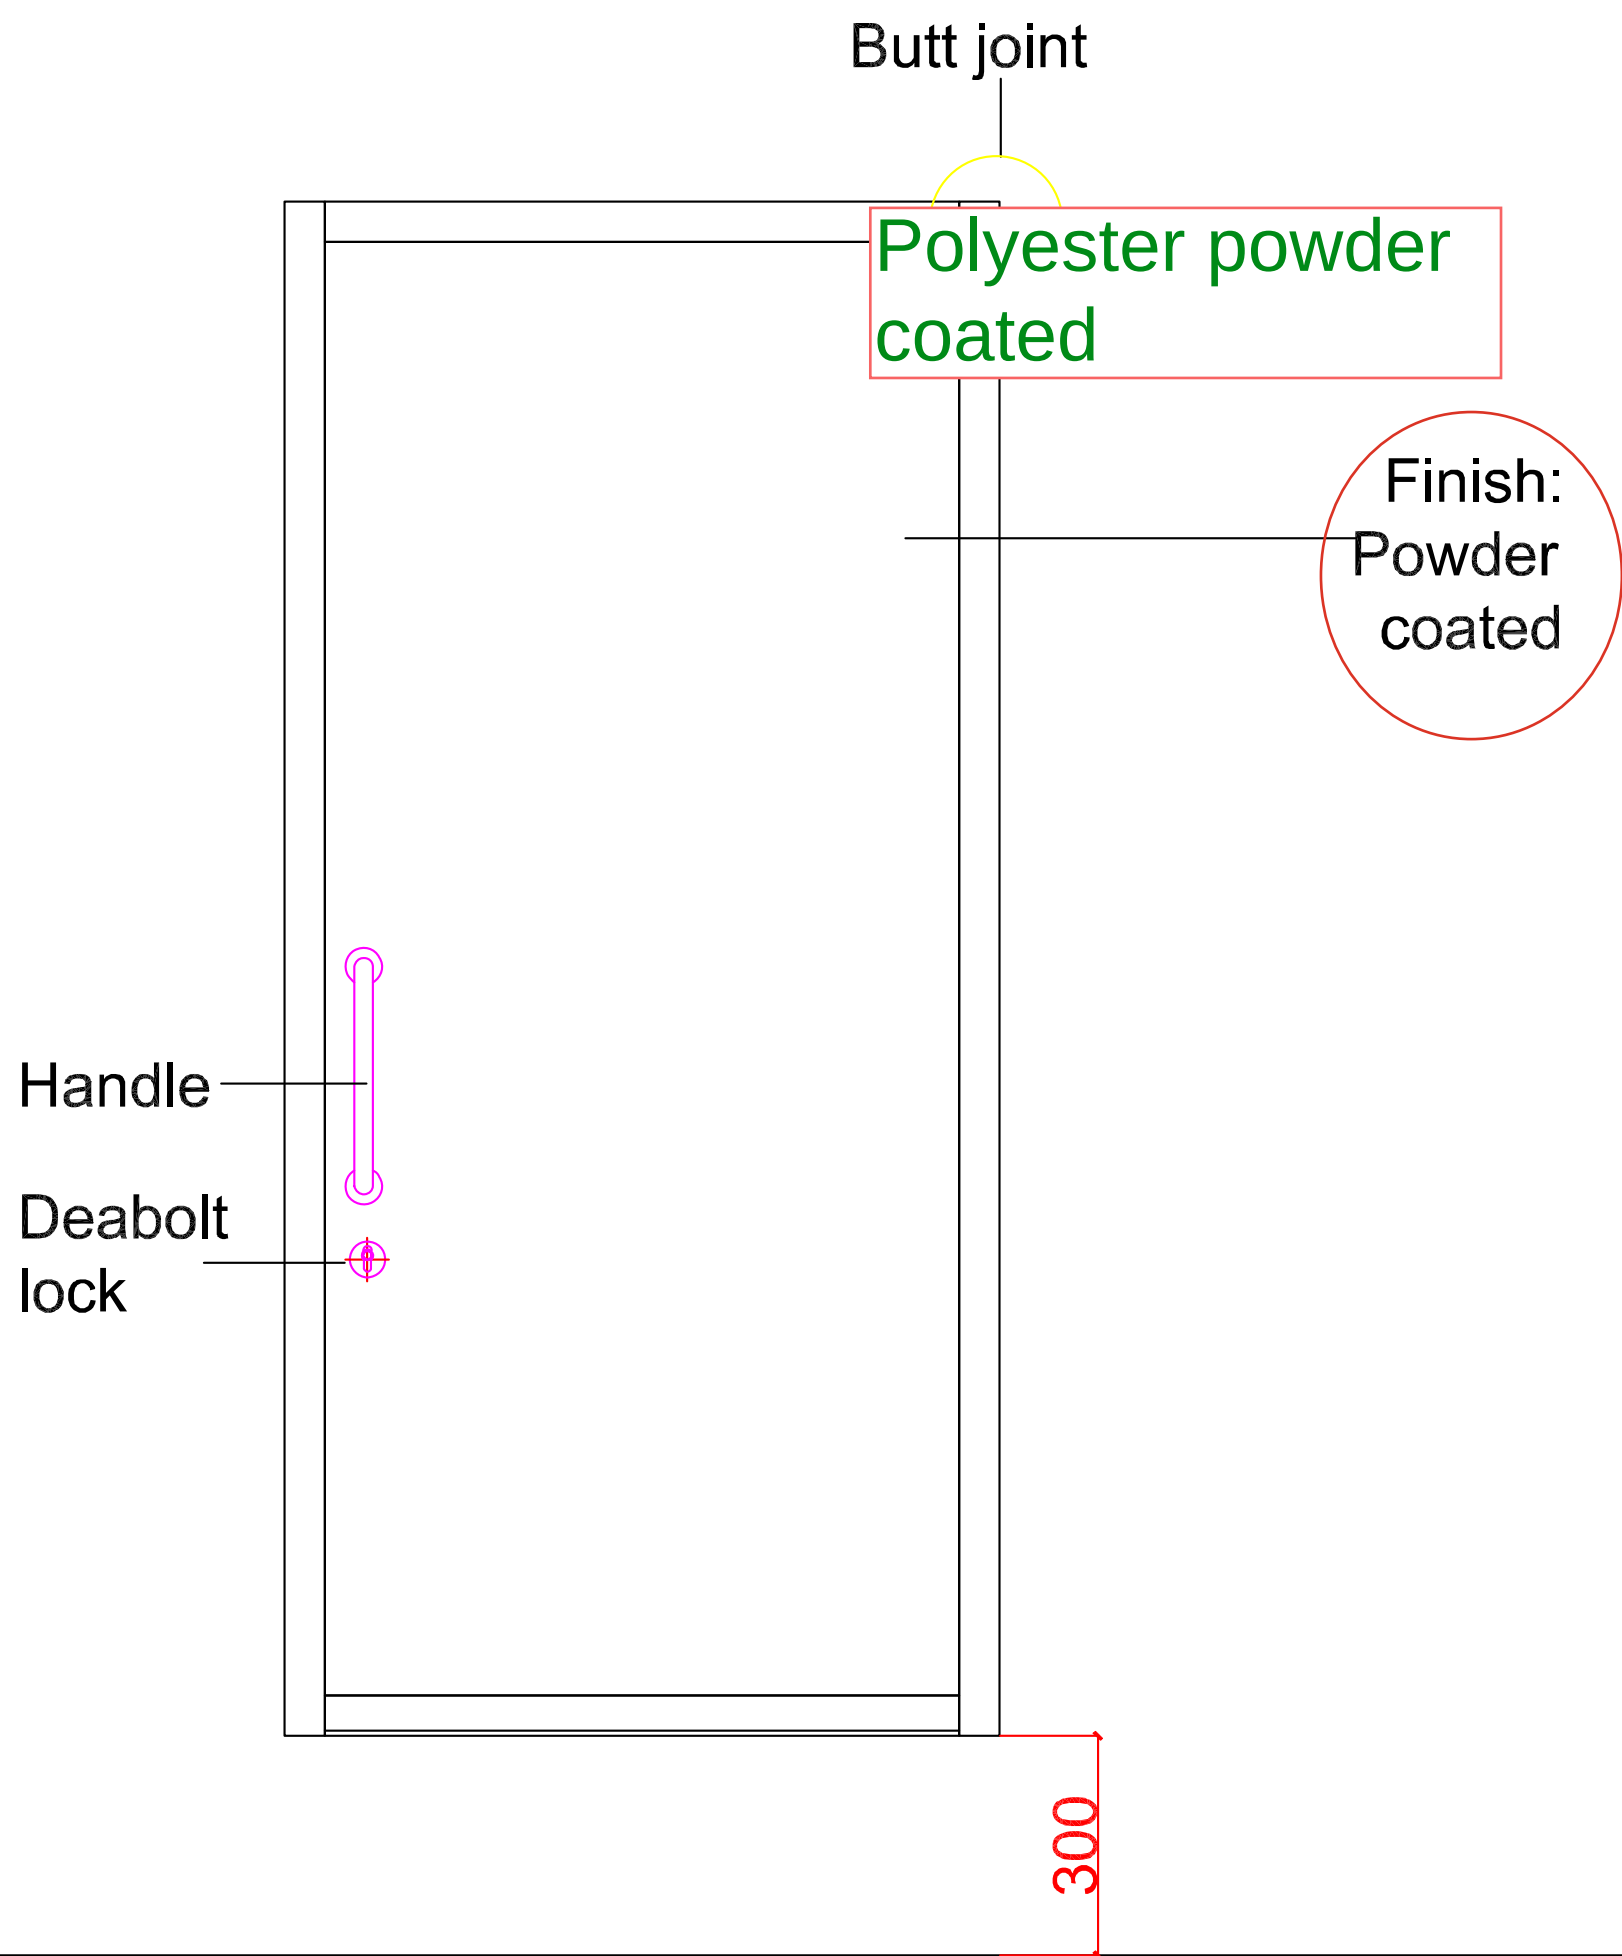

Inside elevation

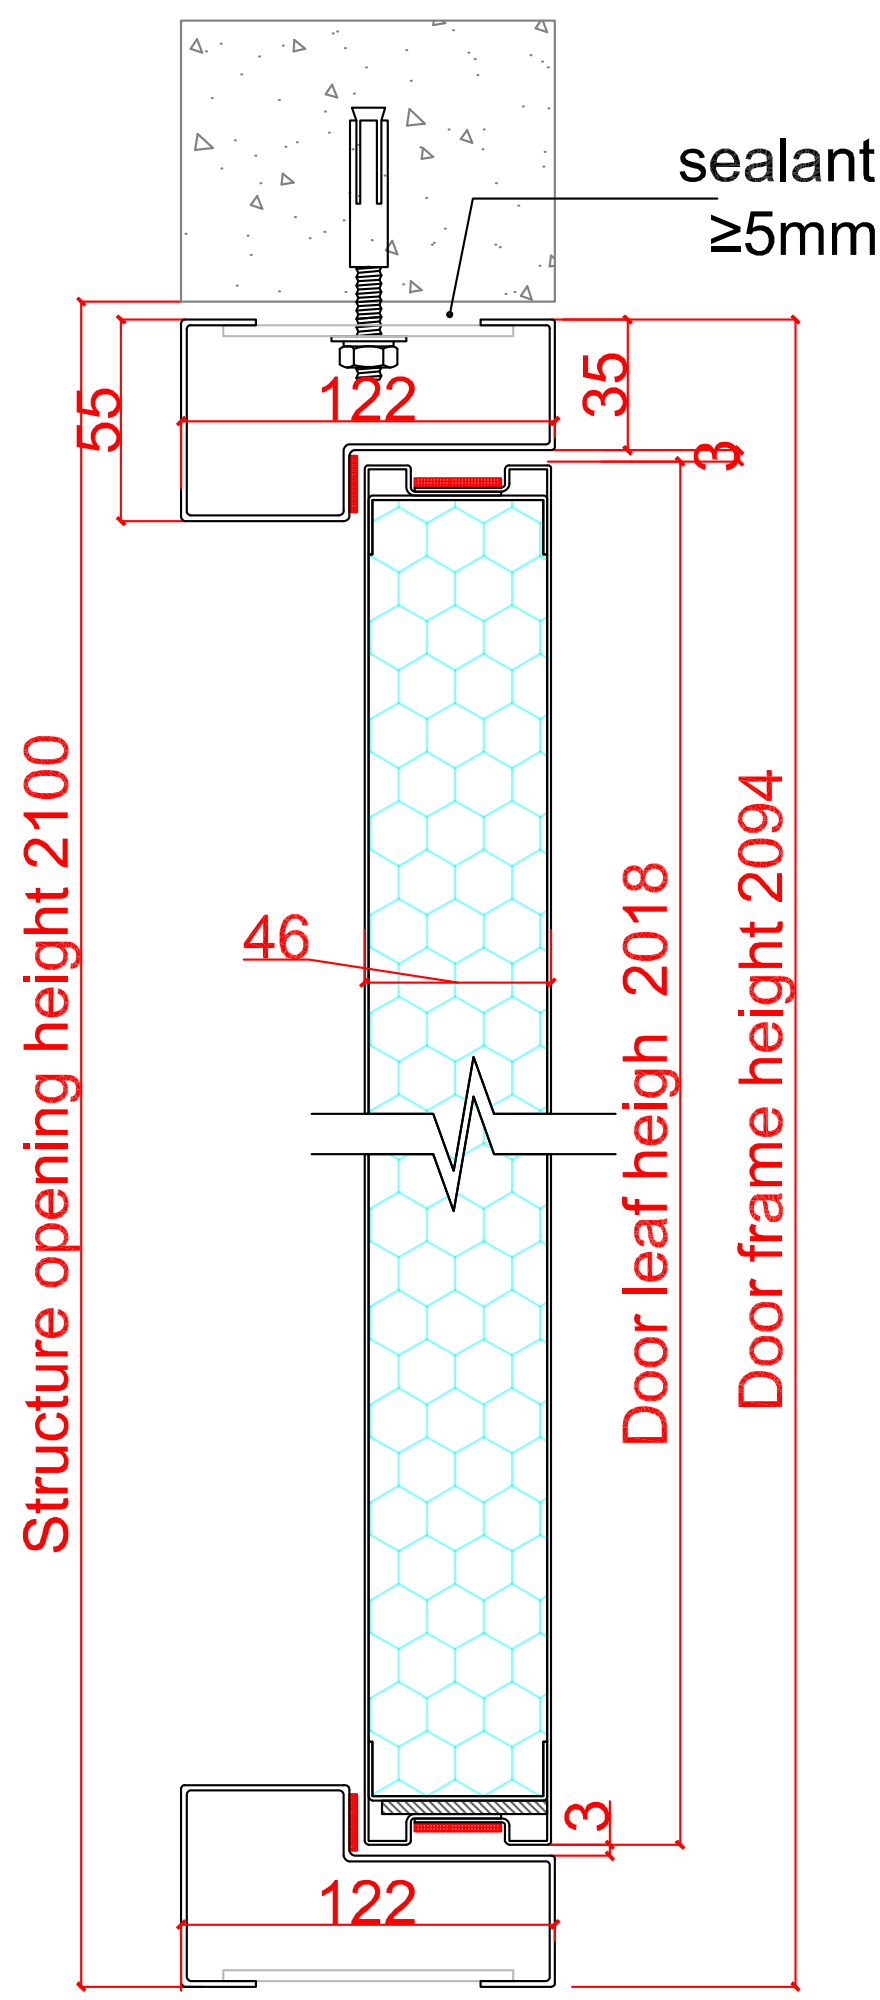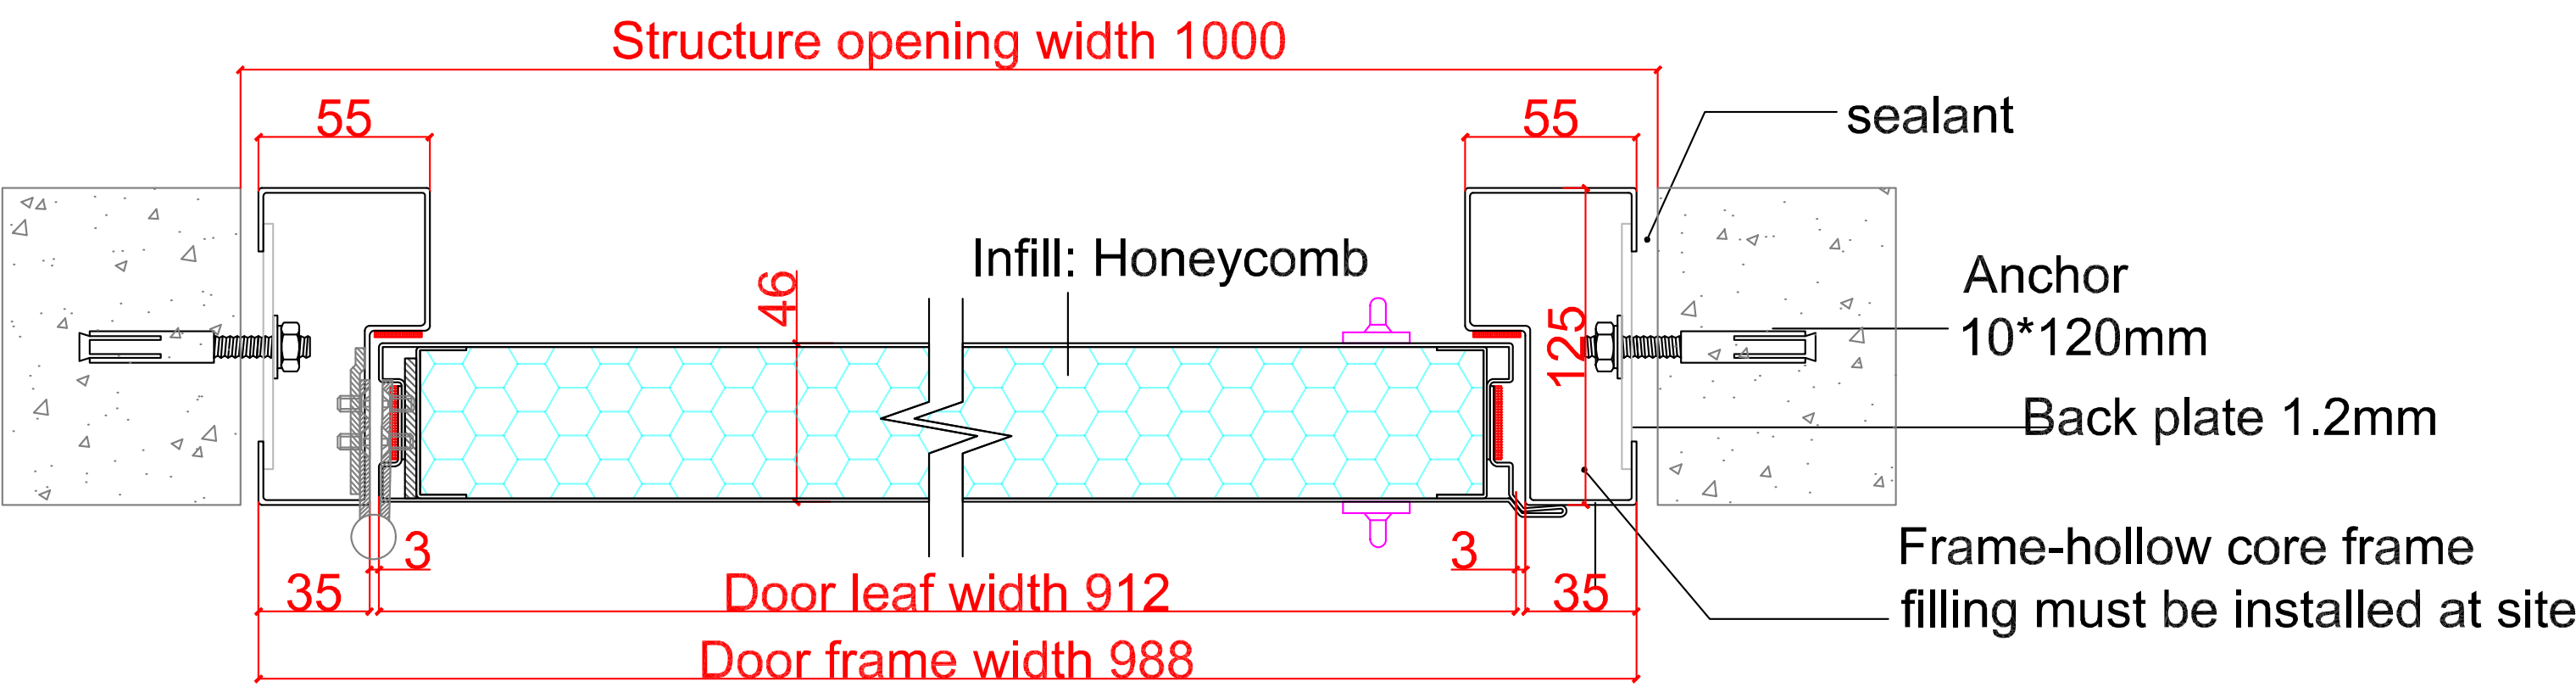

Hinge




sealing trip




Deadlock

Mortise deadlock +euro profile, cylinder with one side key+ (no thumbturn)

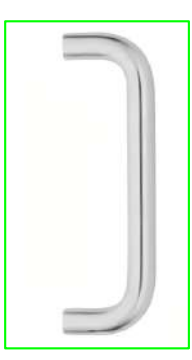

D type handle


Hardware			
Name	Description	Qty	Remarks
Lock type	Deadlock+Handle	1	
Hinge	4*4*3	3	
Smoke seal			
Door frame	1.2mm Galvanized steel sheet		
Door leaf	0.8mm Galvanized steel sheet		
Threshold			
Filling	Honeycomb		
Colour			

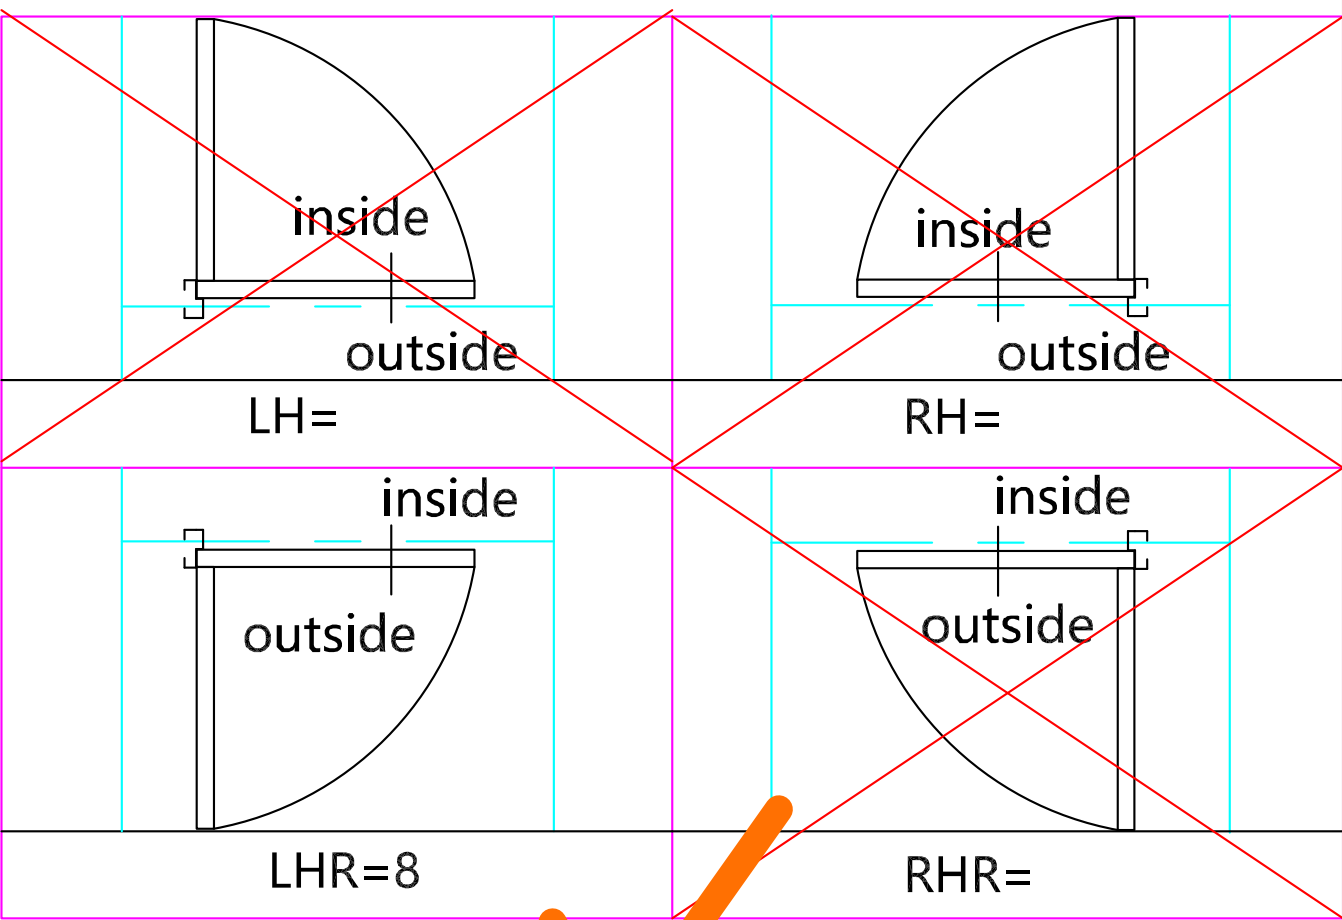


Project name

By		Drawing title	
Design		Size	
Check		Qty	8
Review		Opening direction	
Approval		Date	2026.05.18
		Page No	25
Total Page	34	Diagram number	



SD4

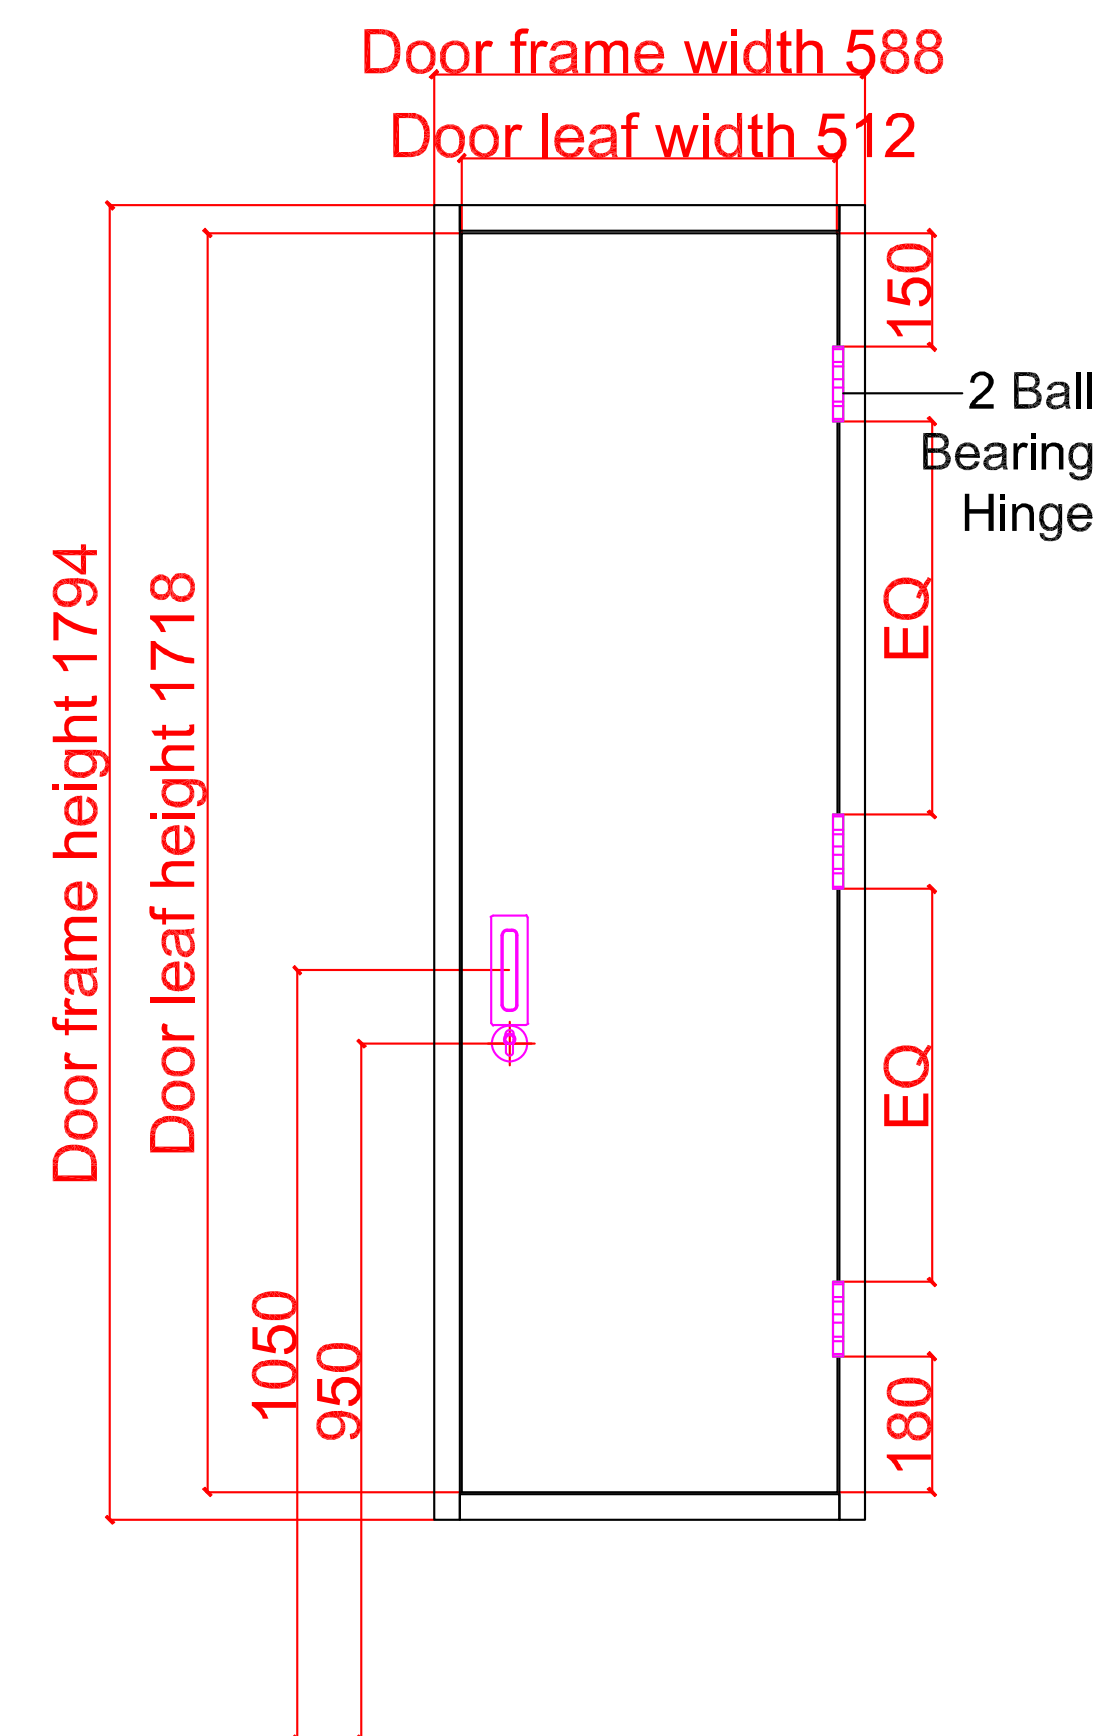

Outside elevation

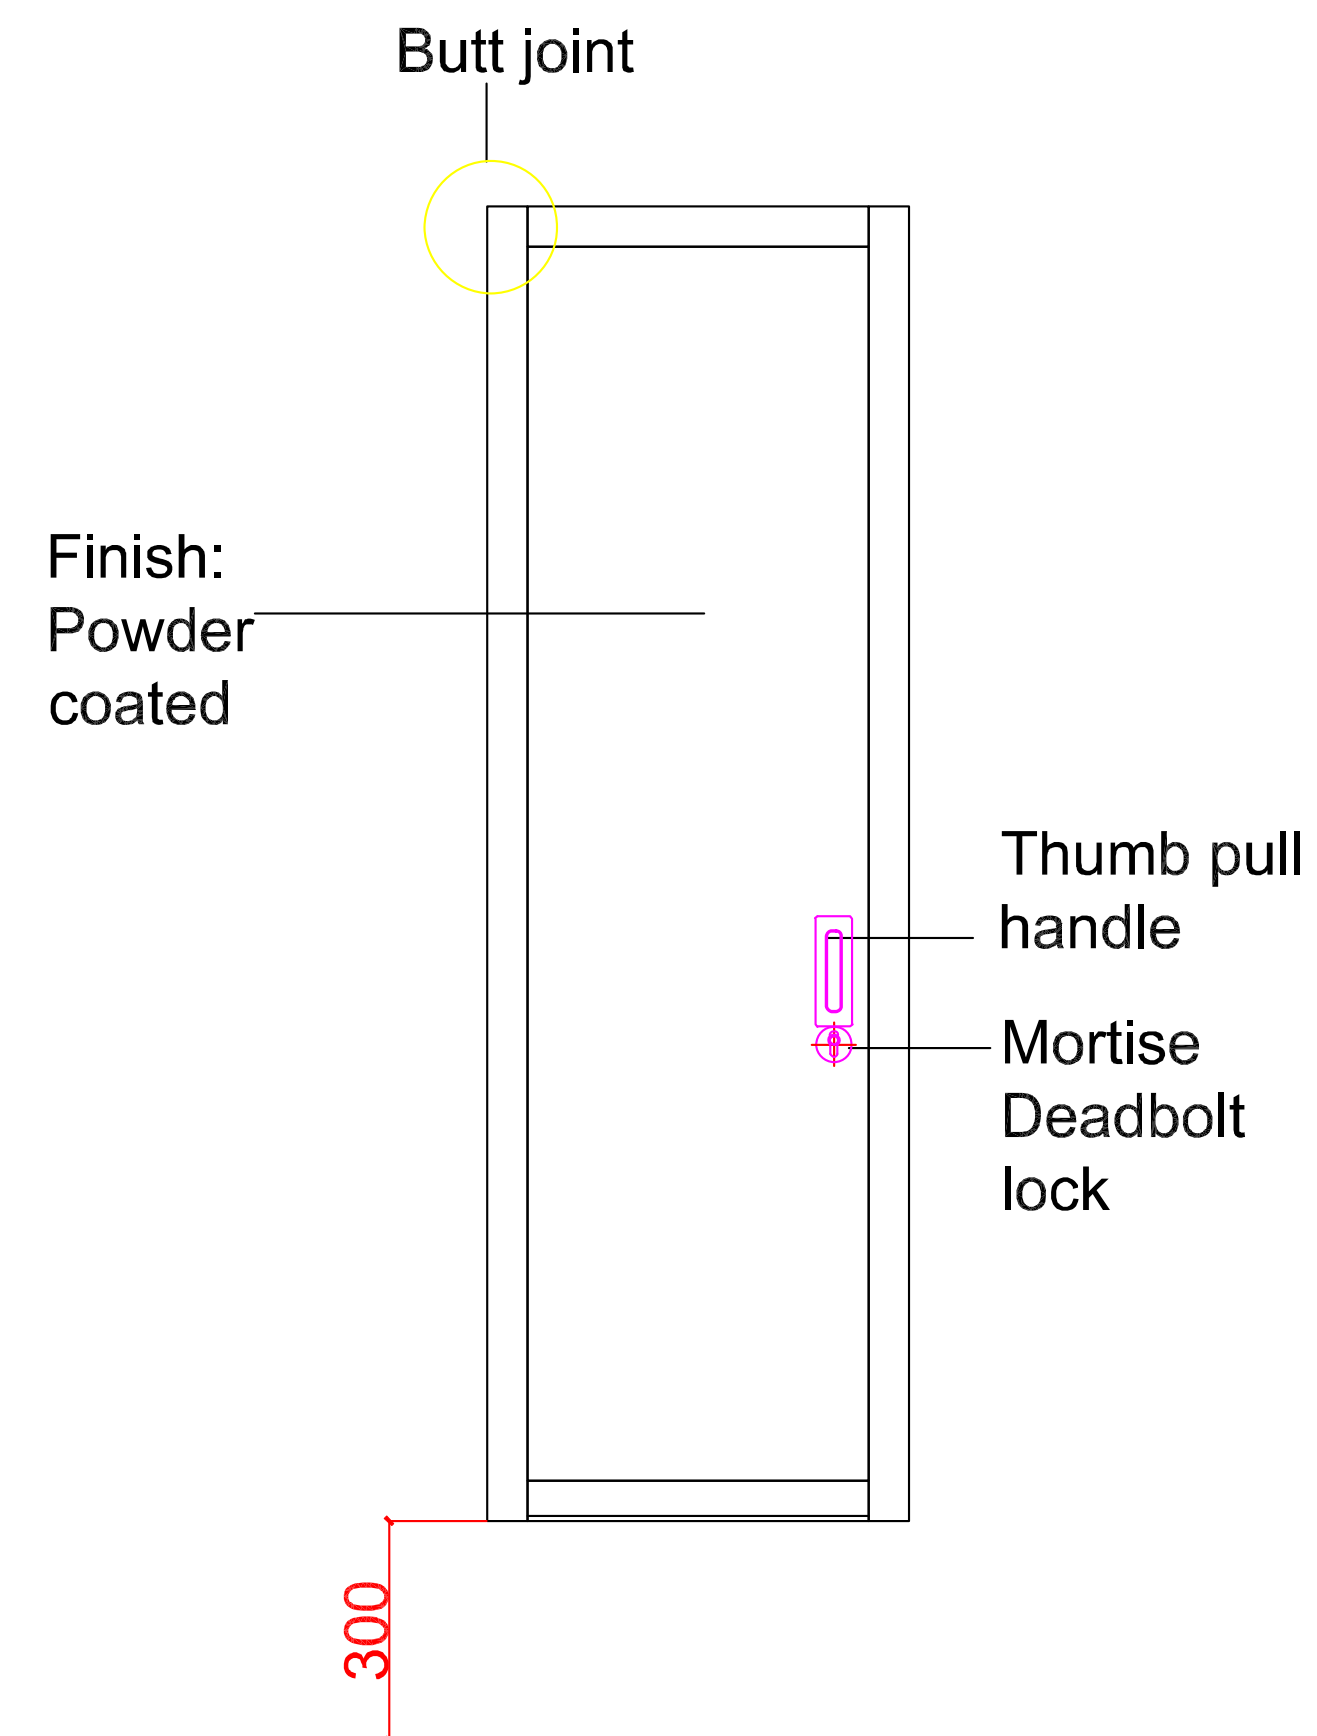

Inside elevation

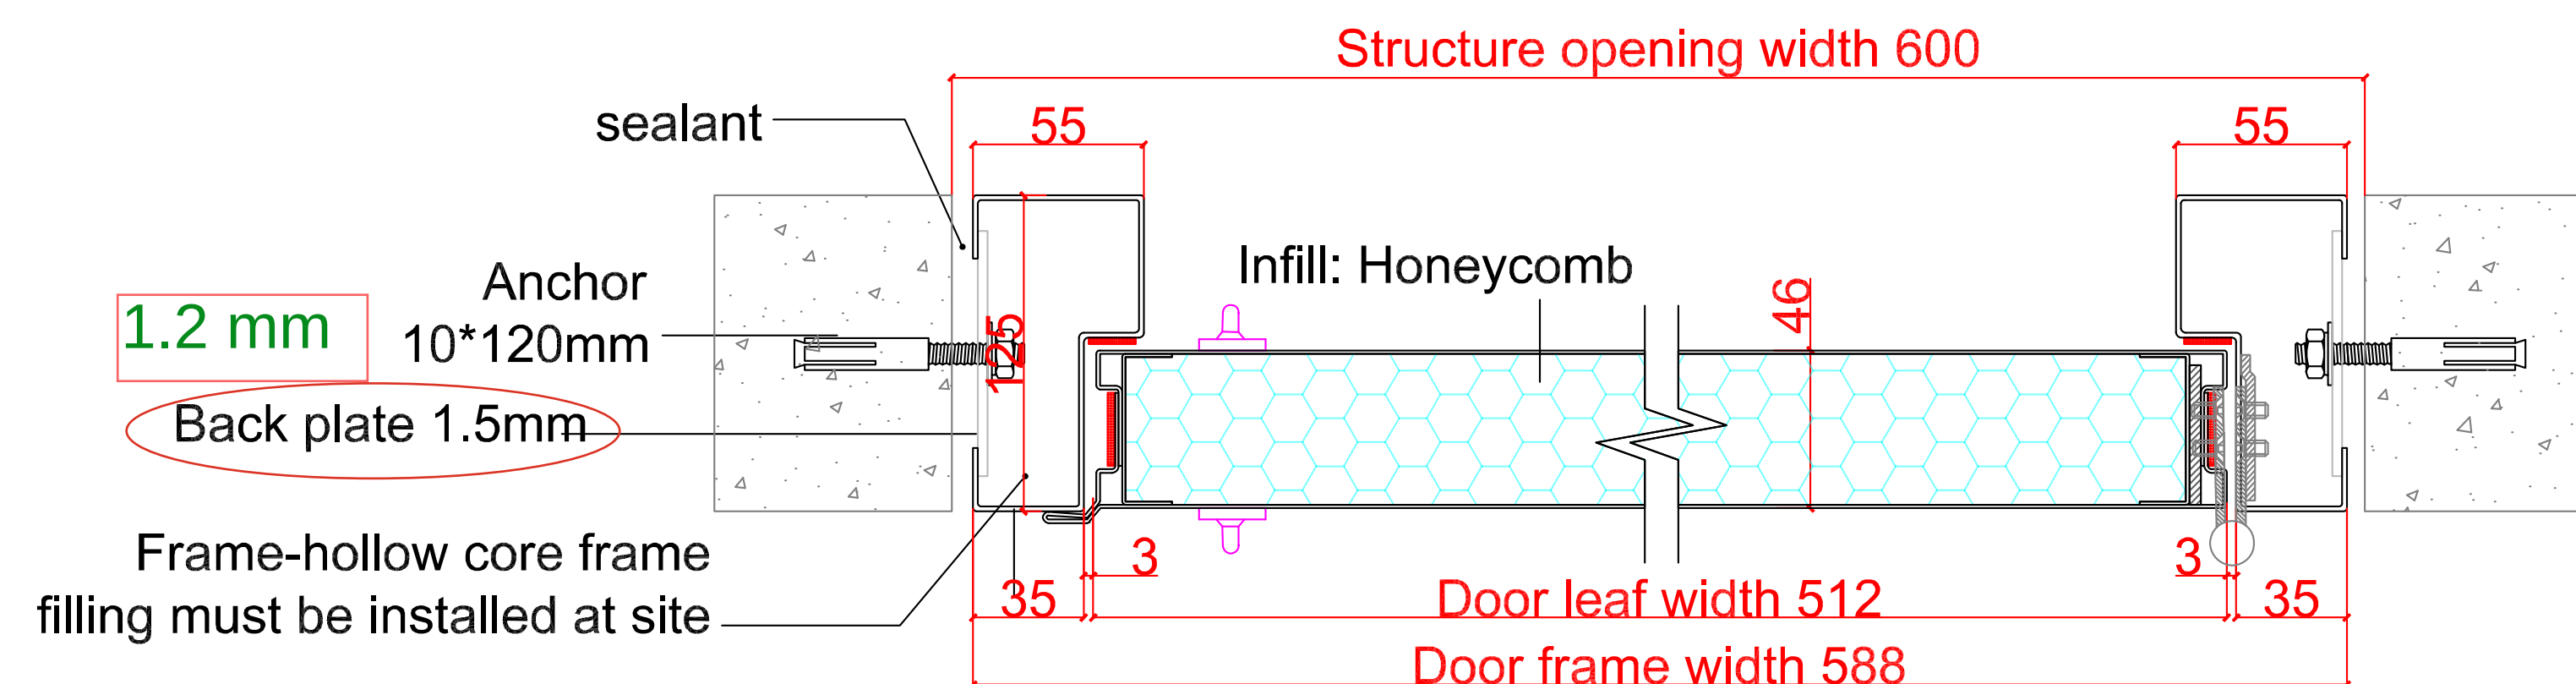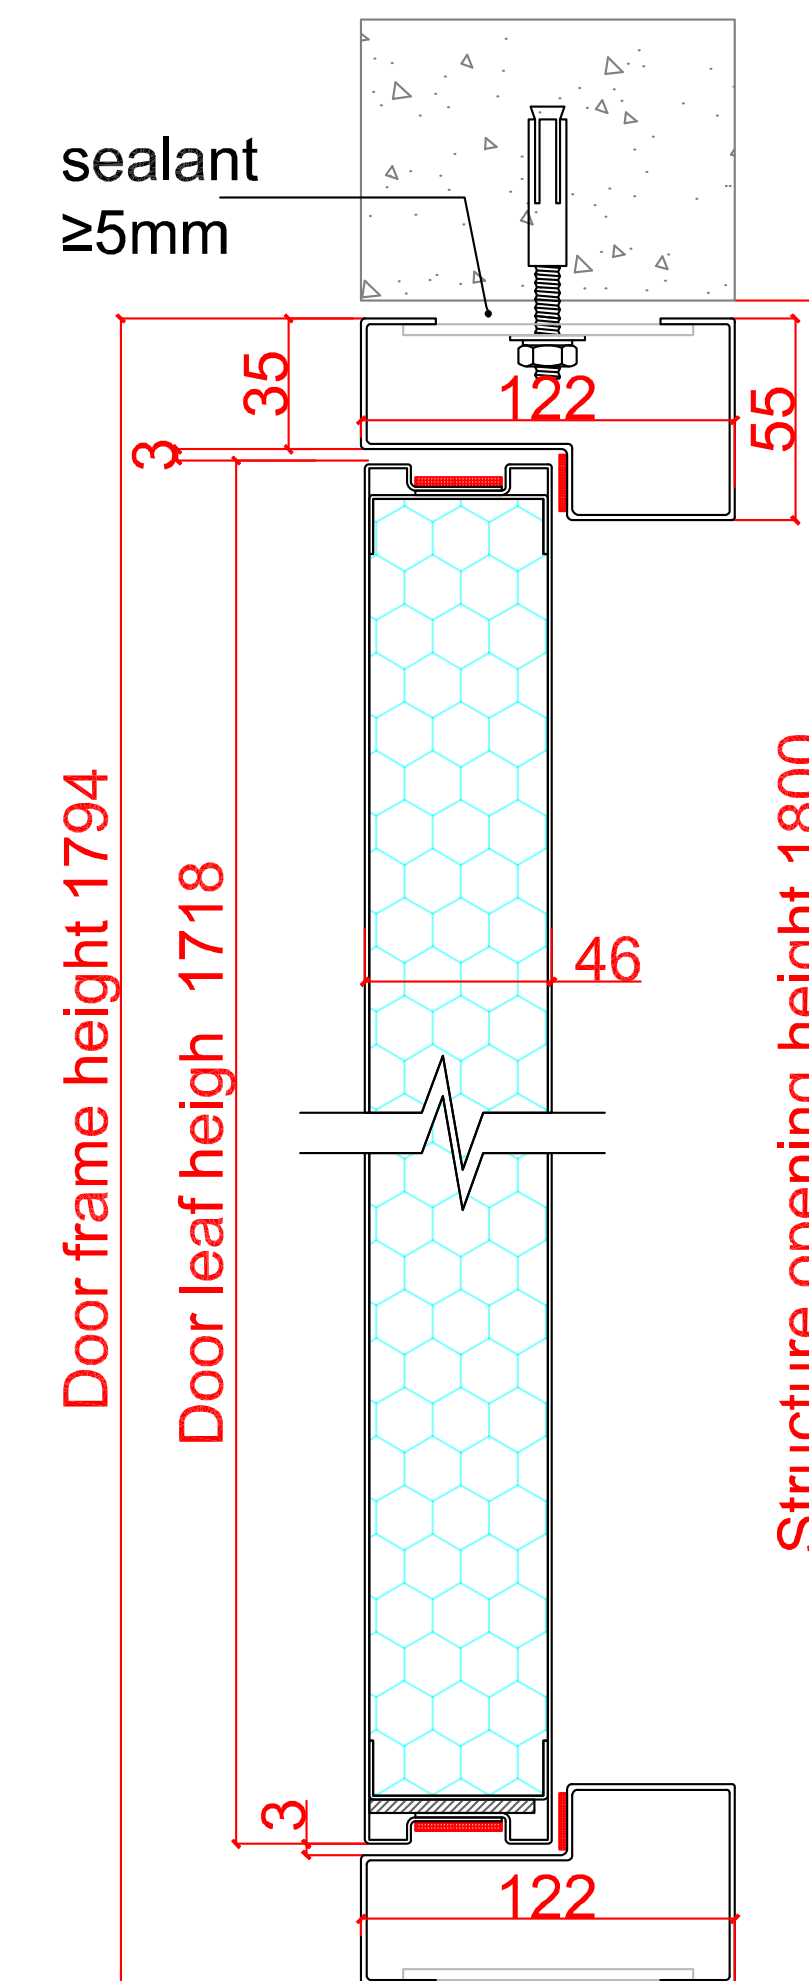


Hinge



sealing trip




Deadlock

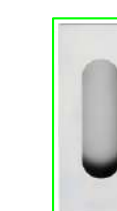

Thumb pull handle

Hardware			
Name	Description	Qty	Remarks
Lock type	Deadlock+Flush pull	1	
Hinge	4*4*3	3	
Smoke seal			
Door frame	1.2mm Galvanized steel sheet		
Door leaf	0.8mm Galvanized steel sheet		
Threshold			
Filling	Honeycomb		
Colour			



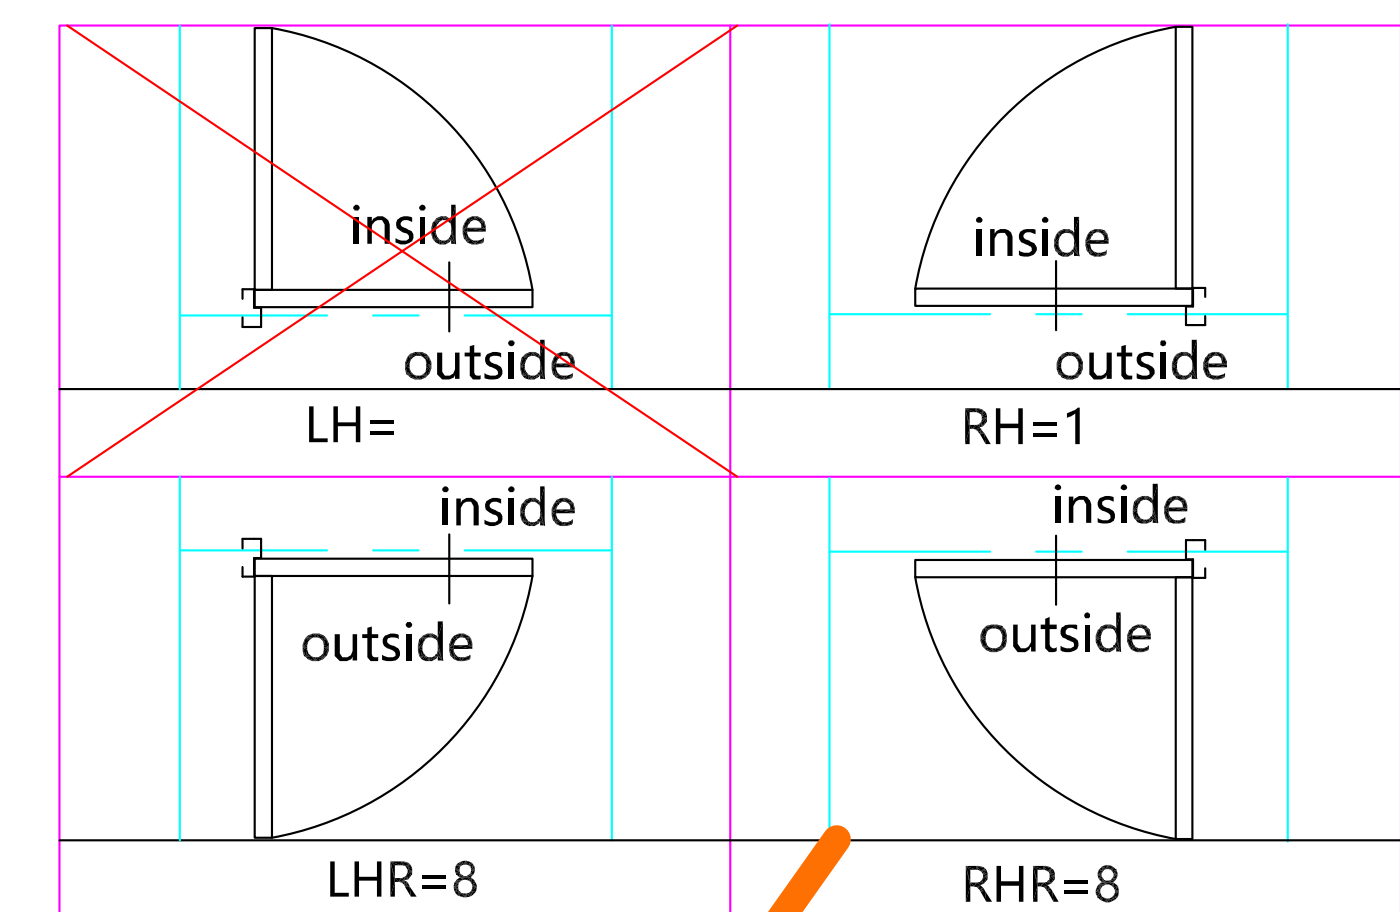


Shanghai Xunzhong Industry Co., Ltd


Project name

By		Drawing title	
Design		Size	
Check		Qty	17
Review		Opening direction	
Approval		Date	2026.05.18
		Page No	26
Total Page	34	Diagram number	

SD5

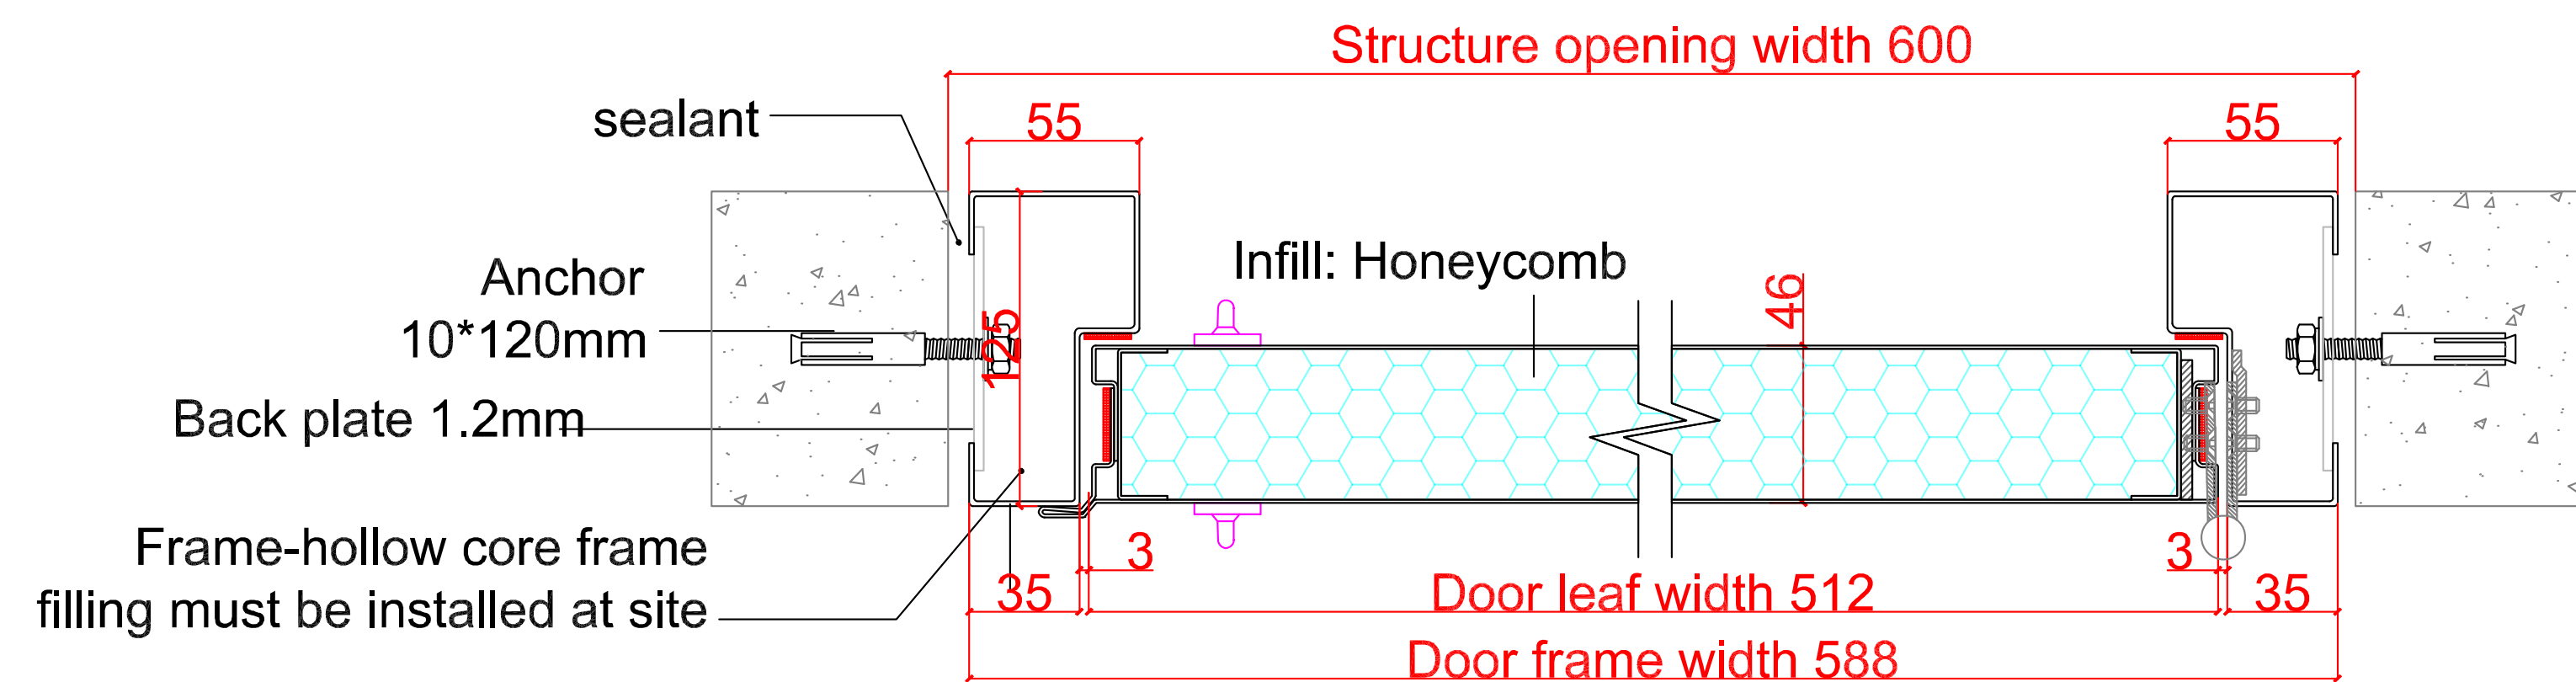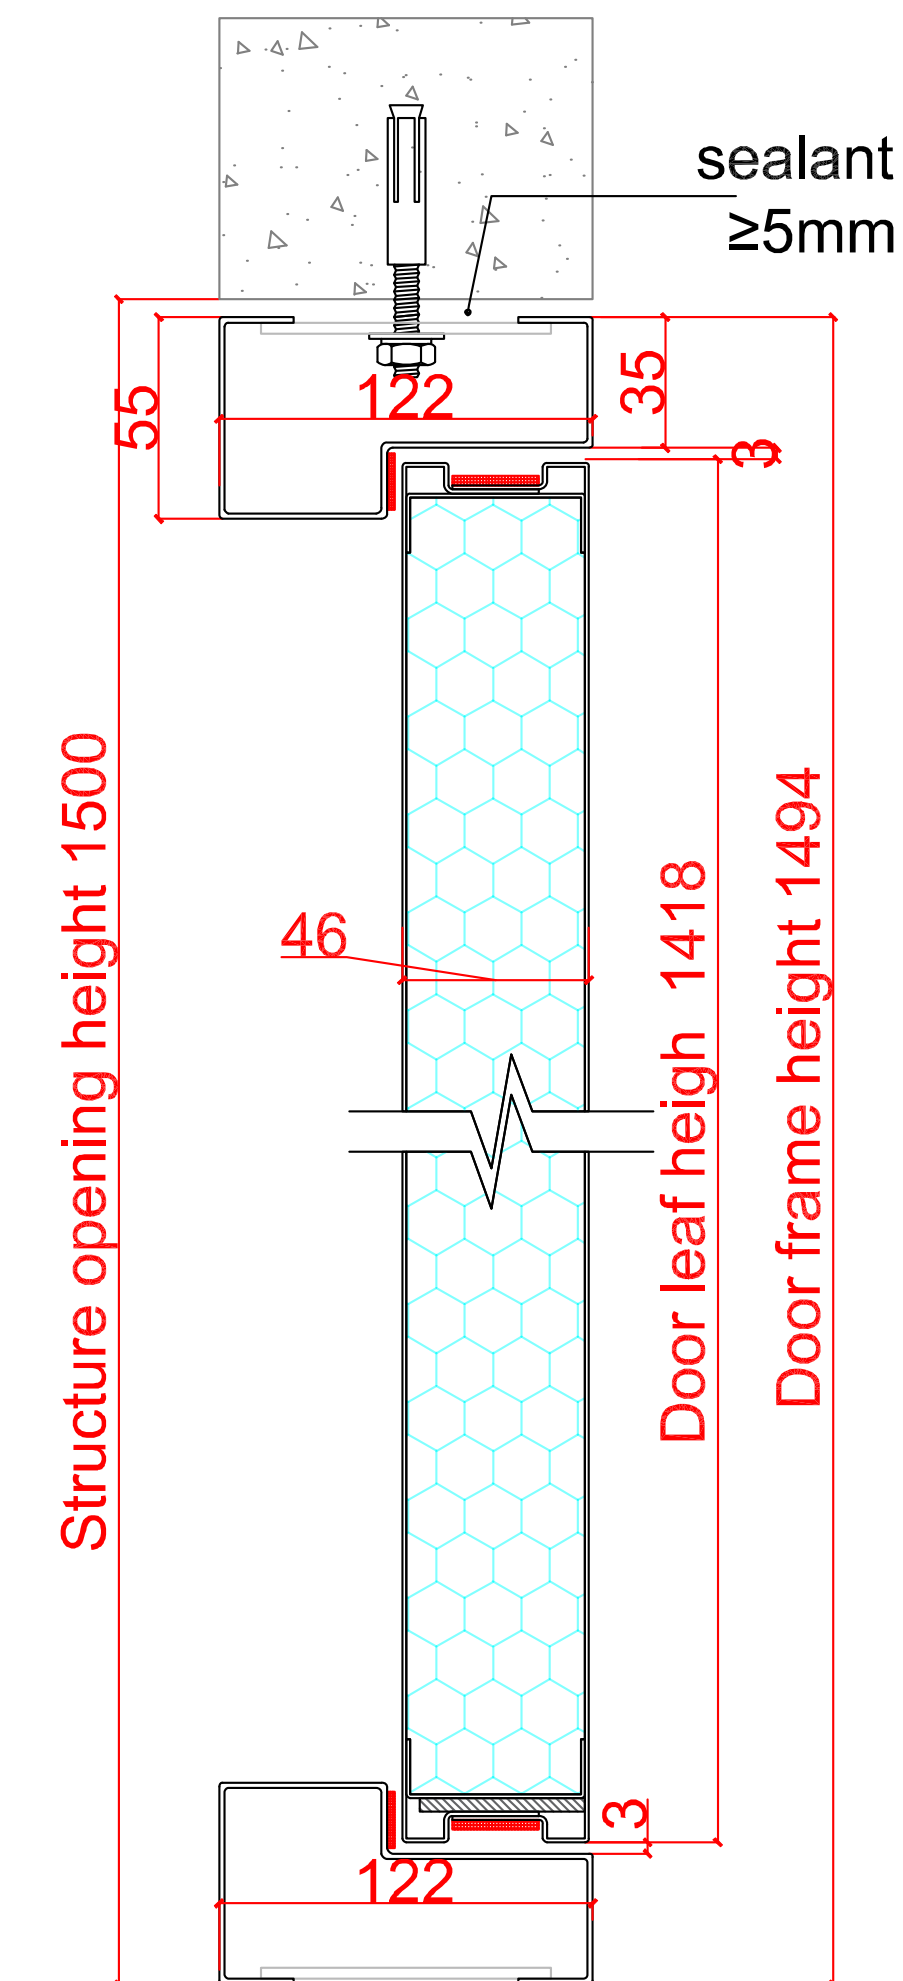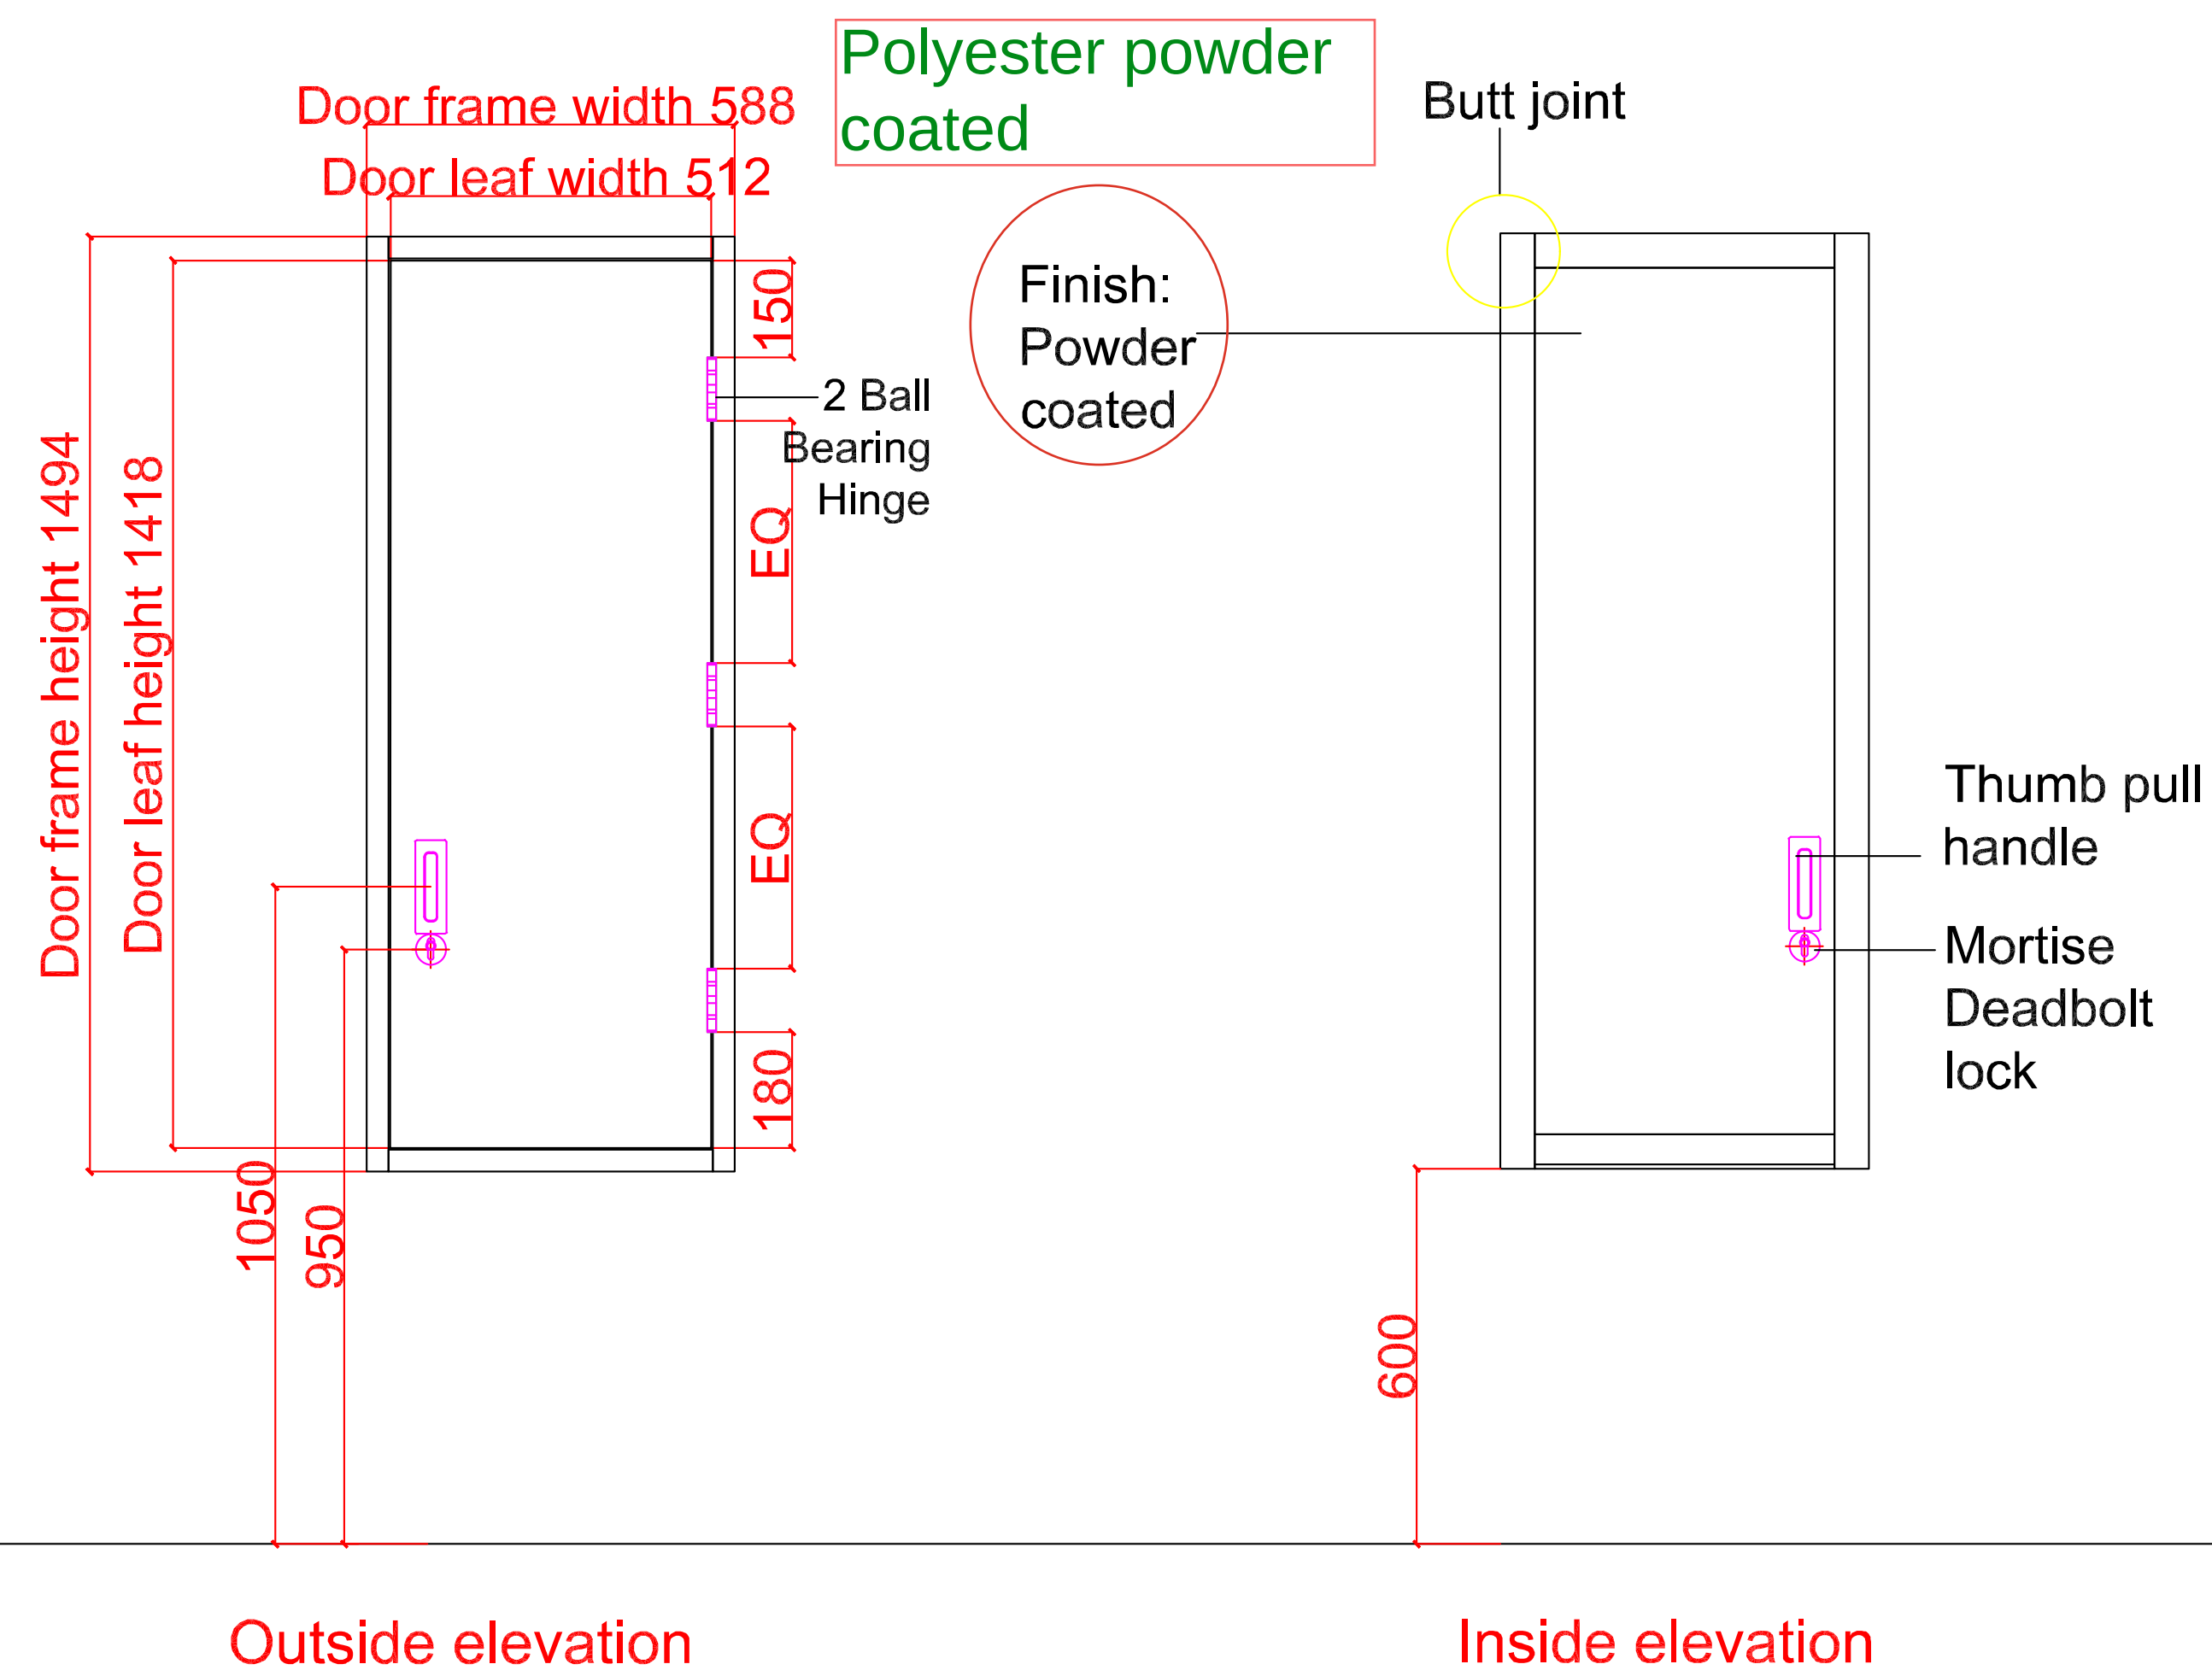



Hardware			
Name	Description	Qty	Remarks
Lock type	Deadlock+Flush pull	1	
Hinge	4*4*3	3	
Smoke seal			
Door frame	1.2mm Galvanized steel sheet		
Door leaf	0.8mm Galvanized steel sheet		
Threshold			
Filling	Honeycomb		
Colour			

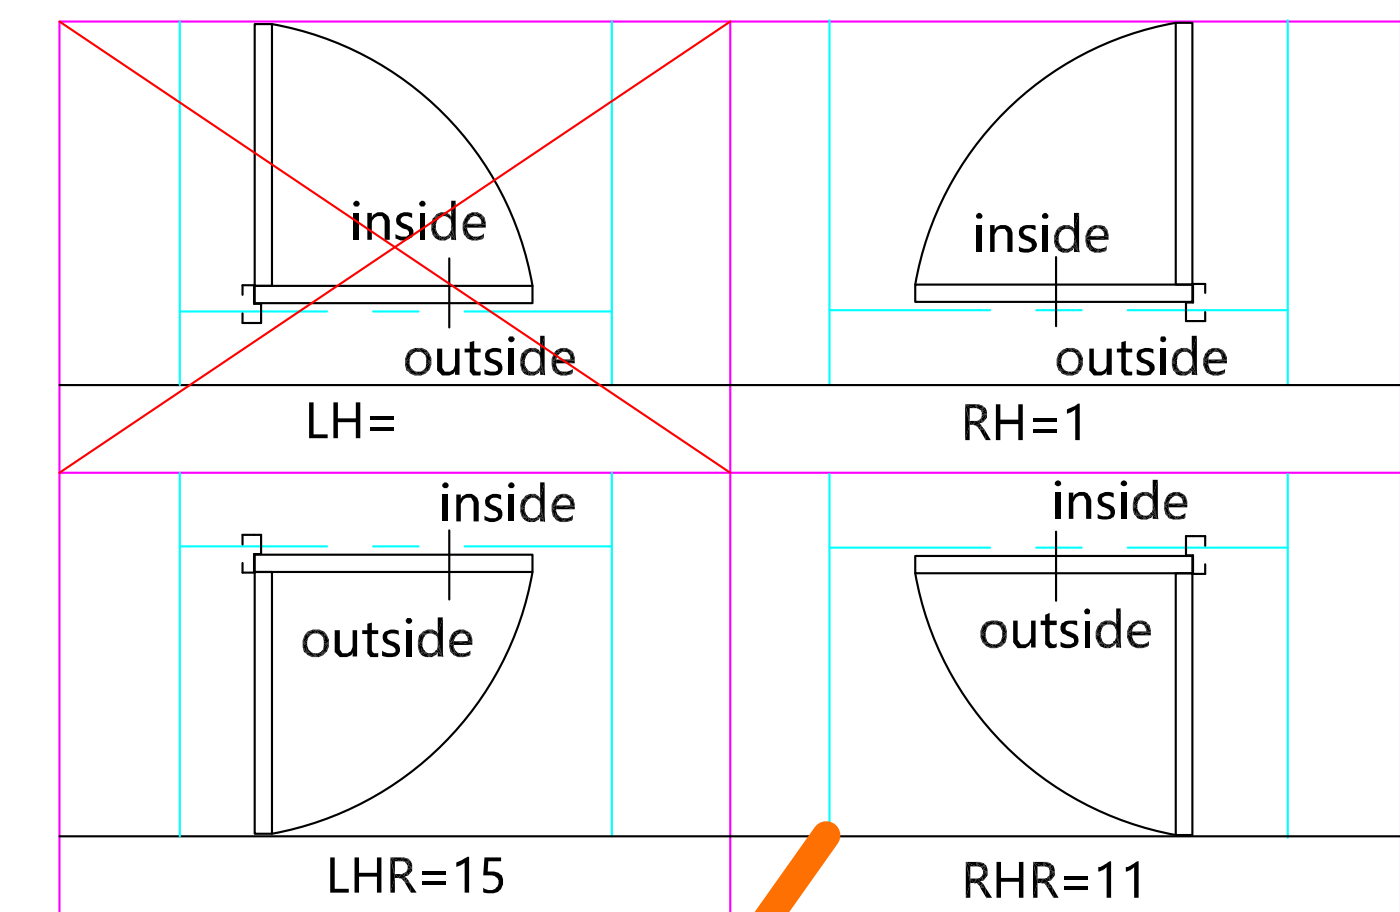




Project name

By		Drawing title	
Design		Size	
Check		Qty	27
Review		Opening direction	
Approval		Date	2026.05.18
		Page No	27
Total Page	34	Diagram number	

SD6

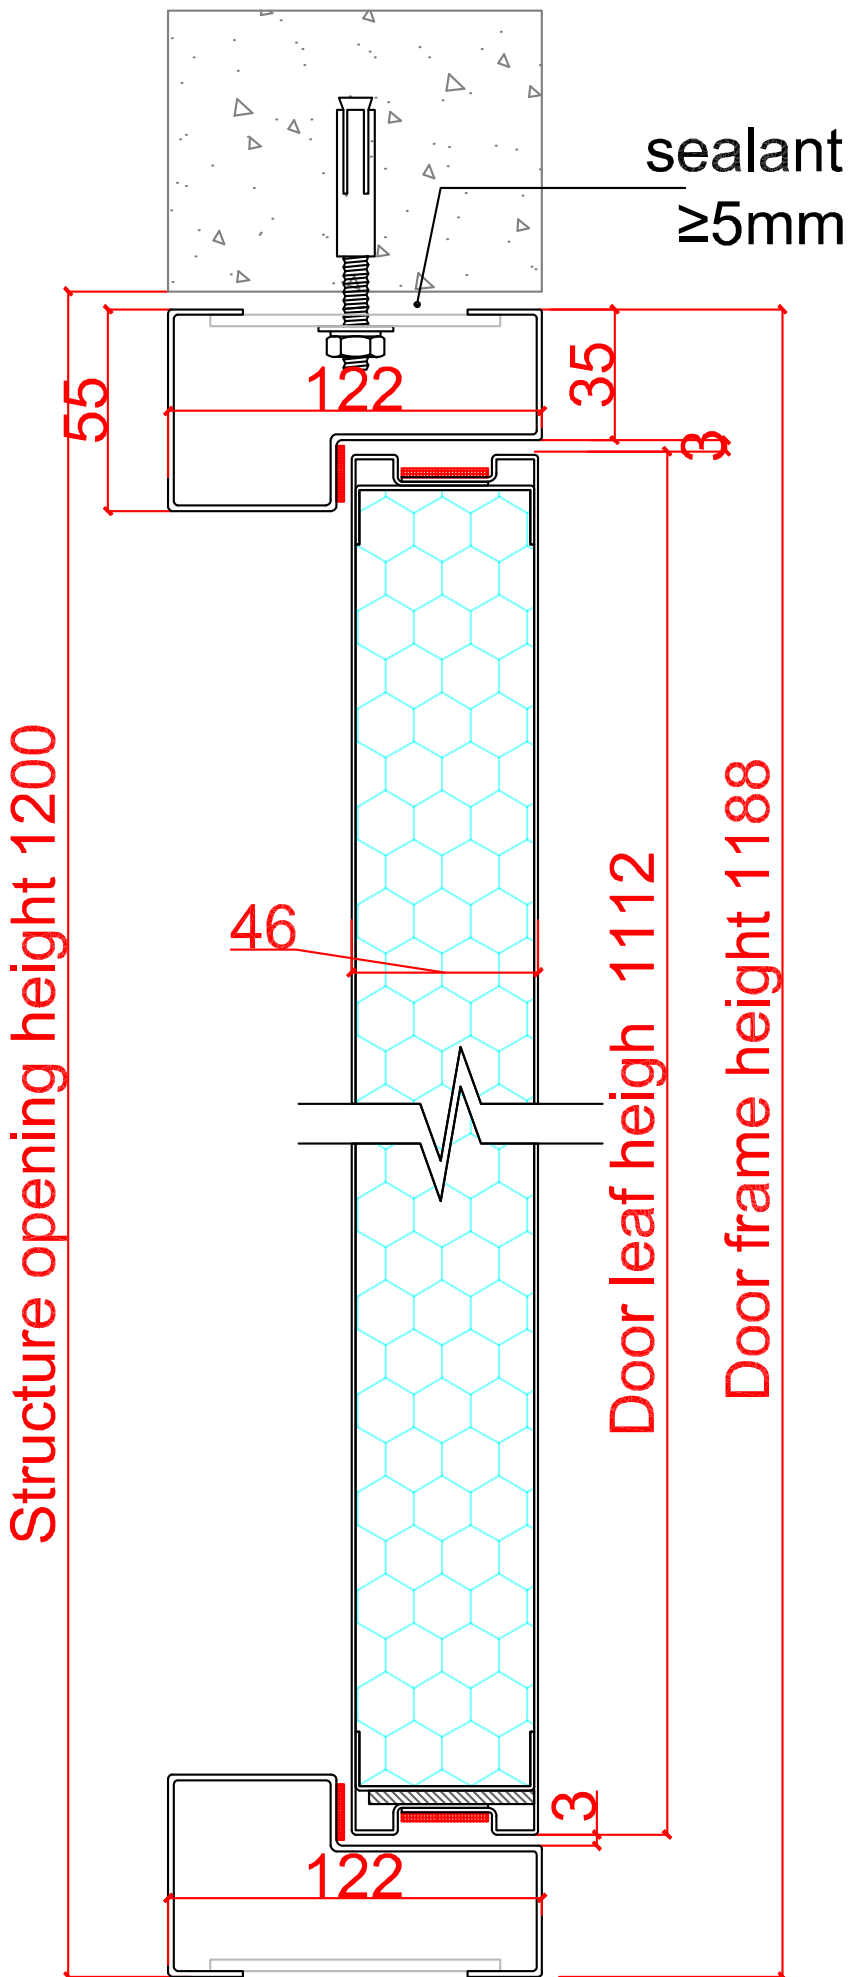
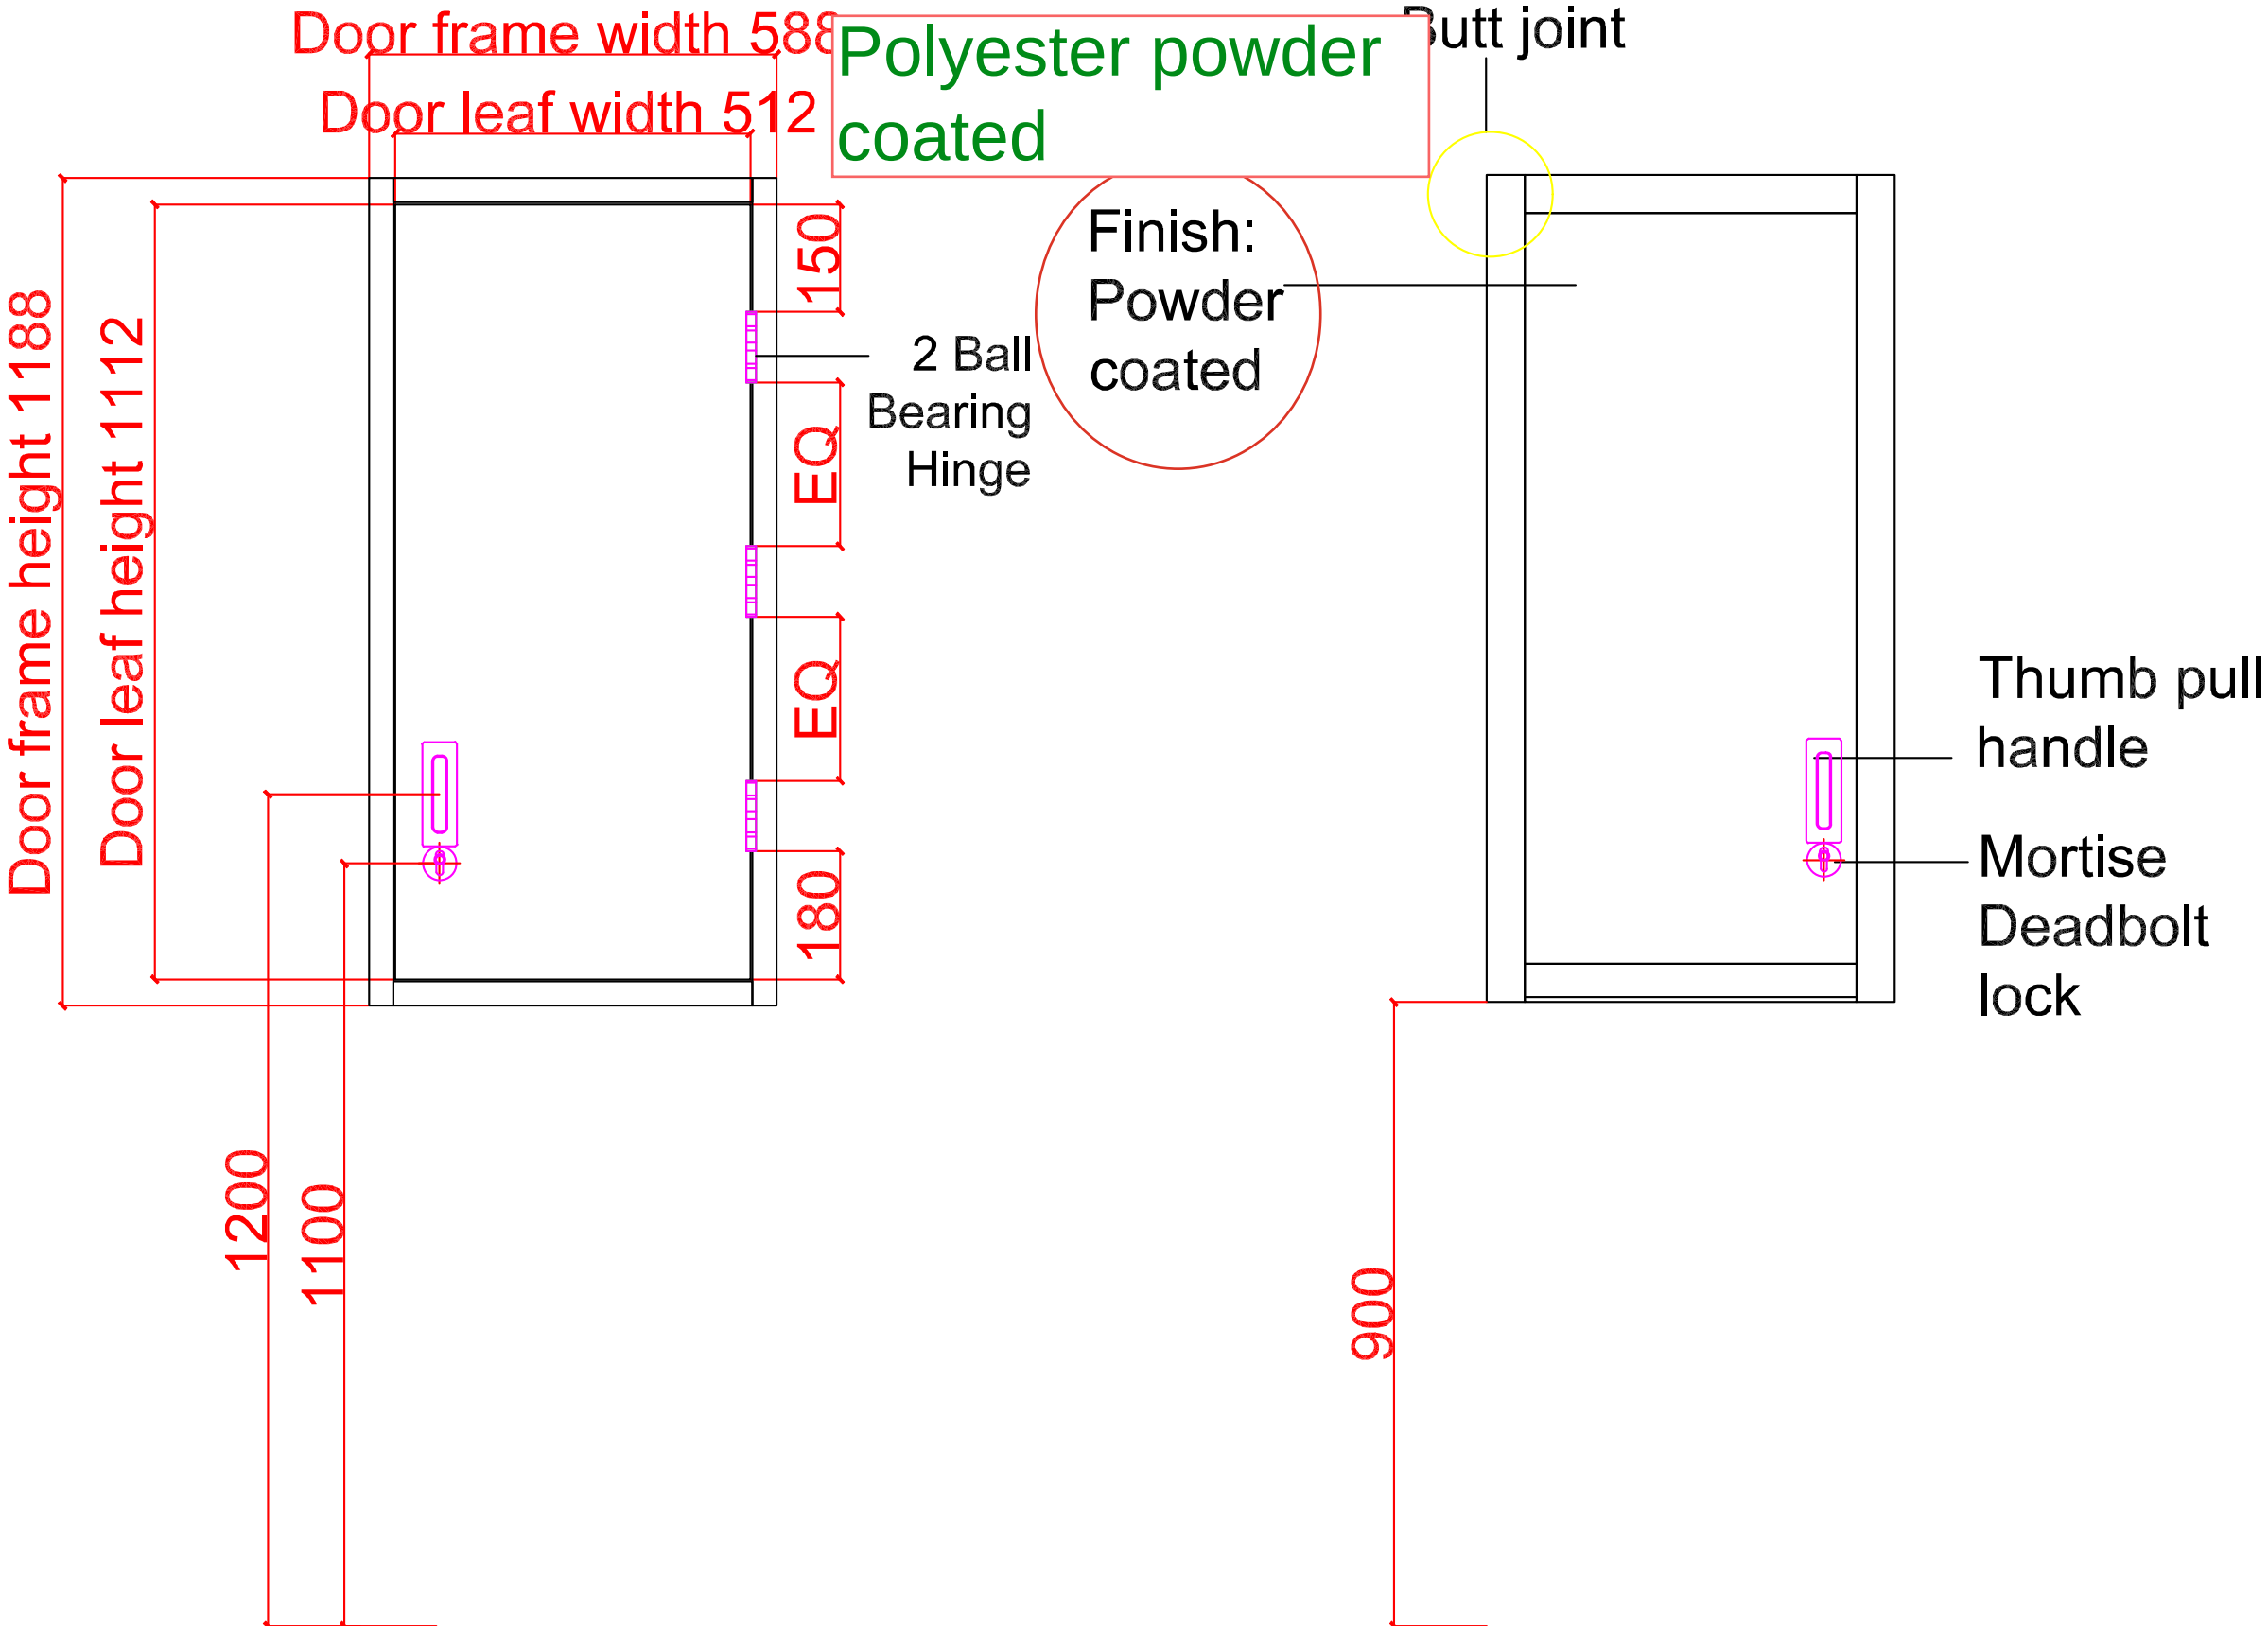


Hardware			
Name	Description	Qty	Remarks
Lock type	Deadlock+Flush pull	1	
Hinge	4*4*3	3	
Smoke seal			
Door frame	1.2mm Galvanized steel sheet		
Door leaf	0.8mm Galvanized steel sheet		
Threshold			
Filling	Honeycomb		
Colour			

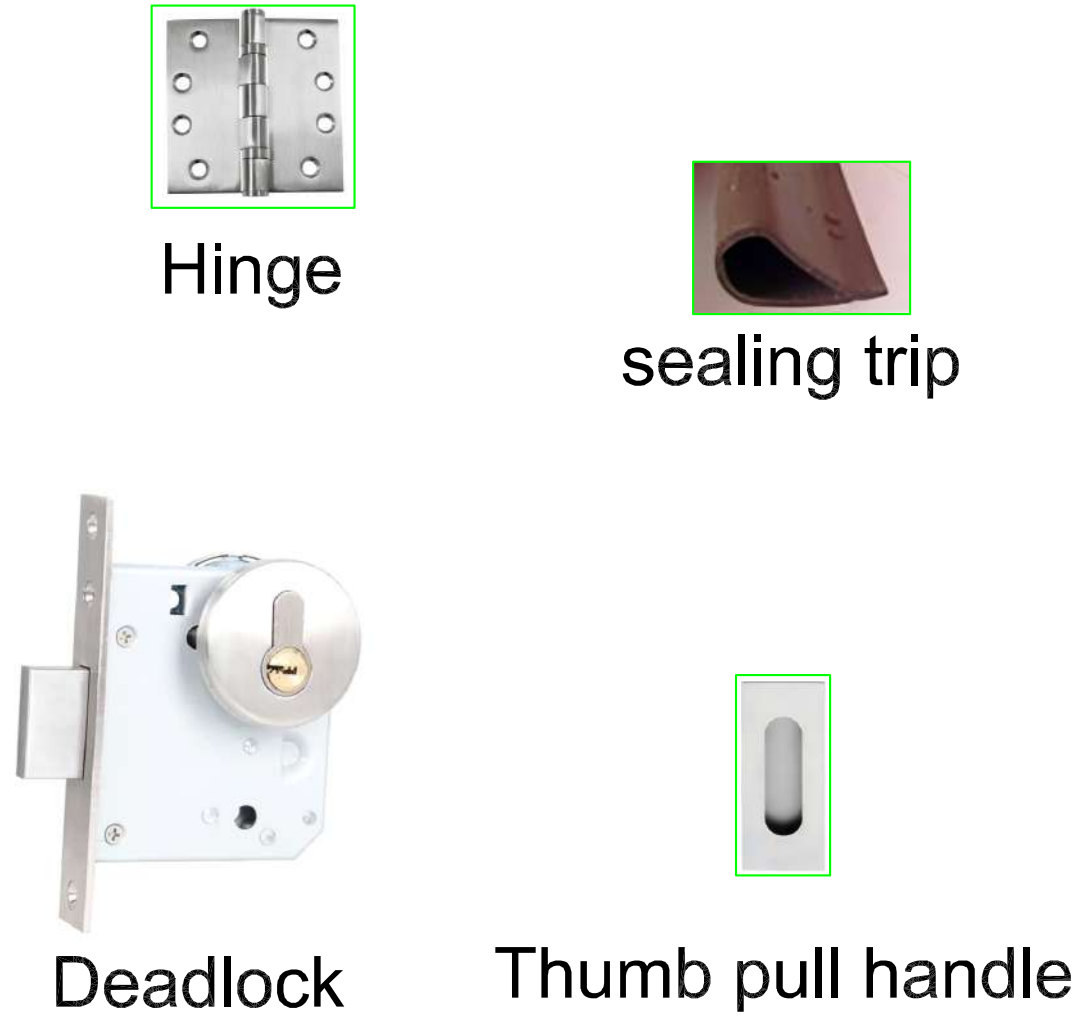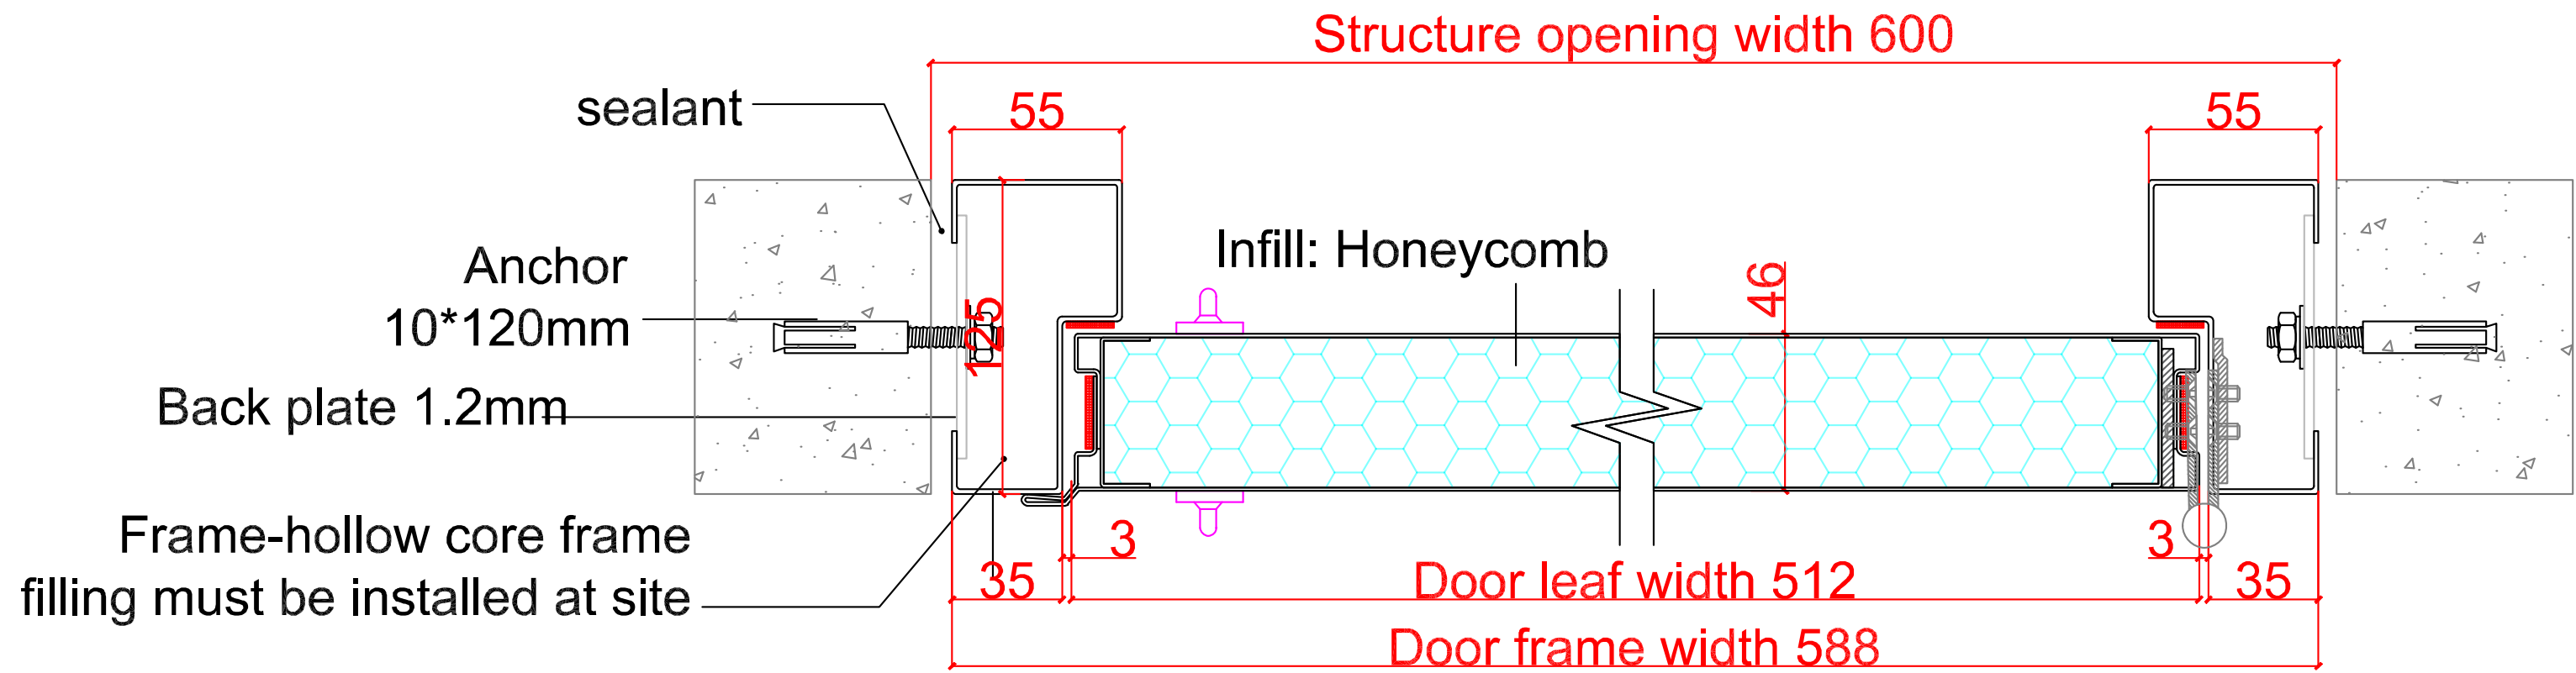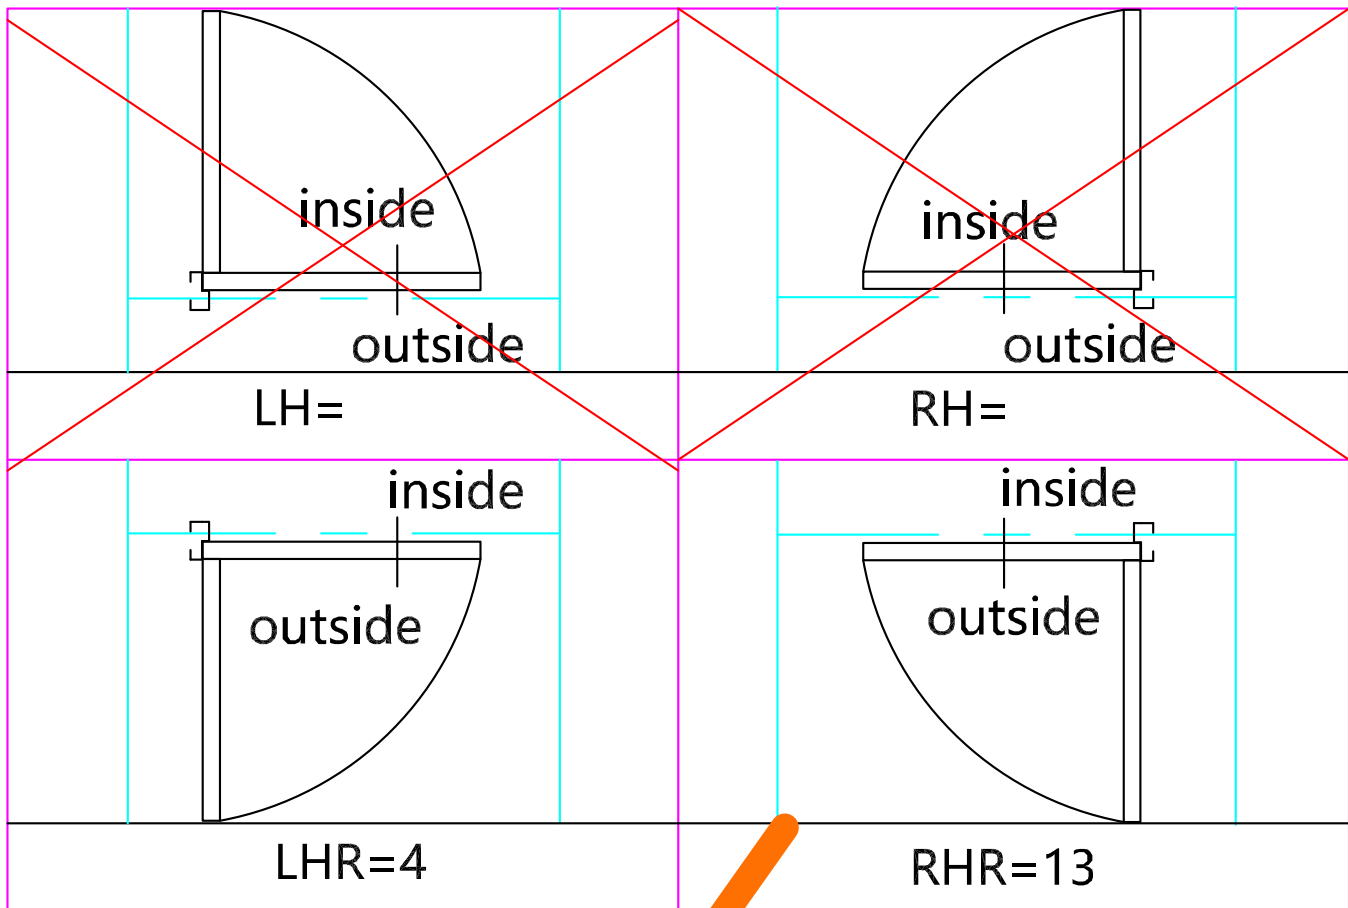


 Shanghai Xunzhong Industry Co., Ltd			
Project name			
By		Drawing title	
Design		Size	
Check		Qty	17
Review		Opening direction	
Approval		Date	2026.05.18
Total Page	34	Page No	28
		Diagram number	

SD7

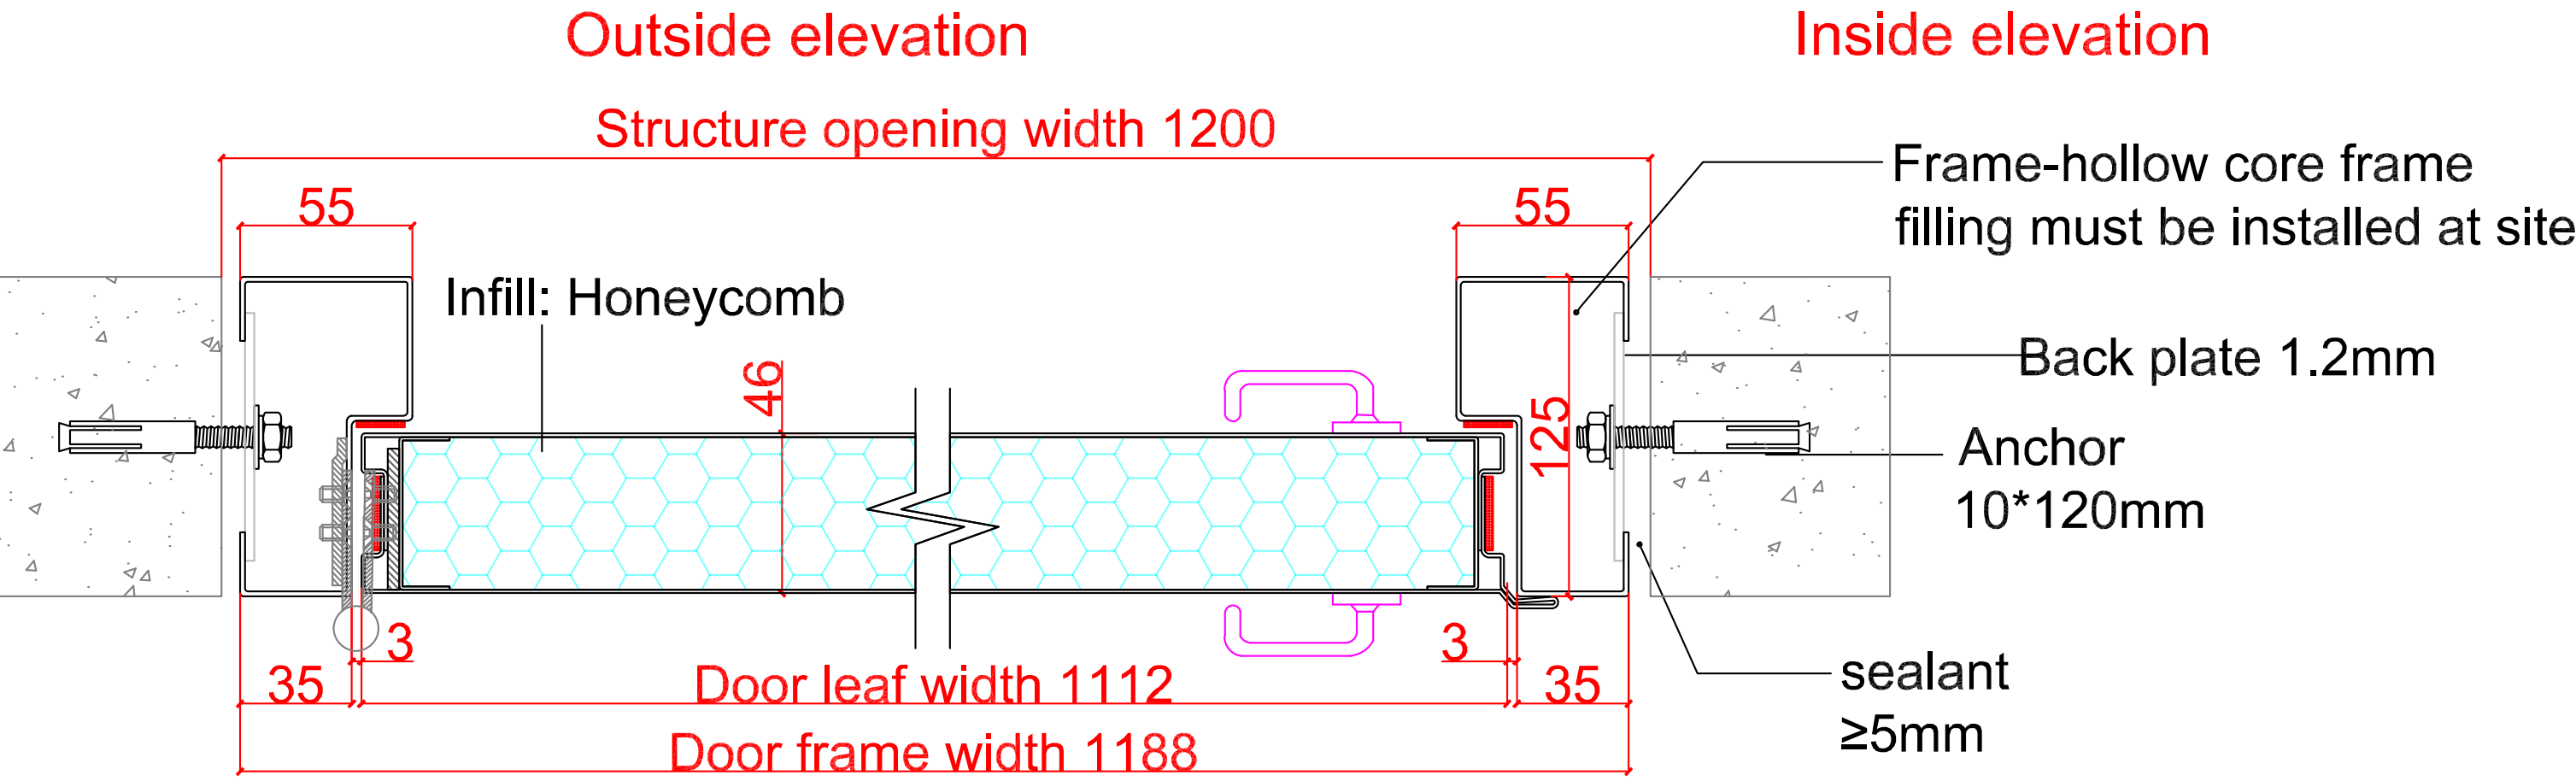
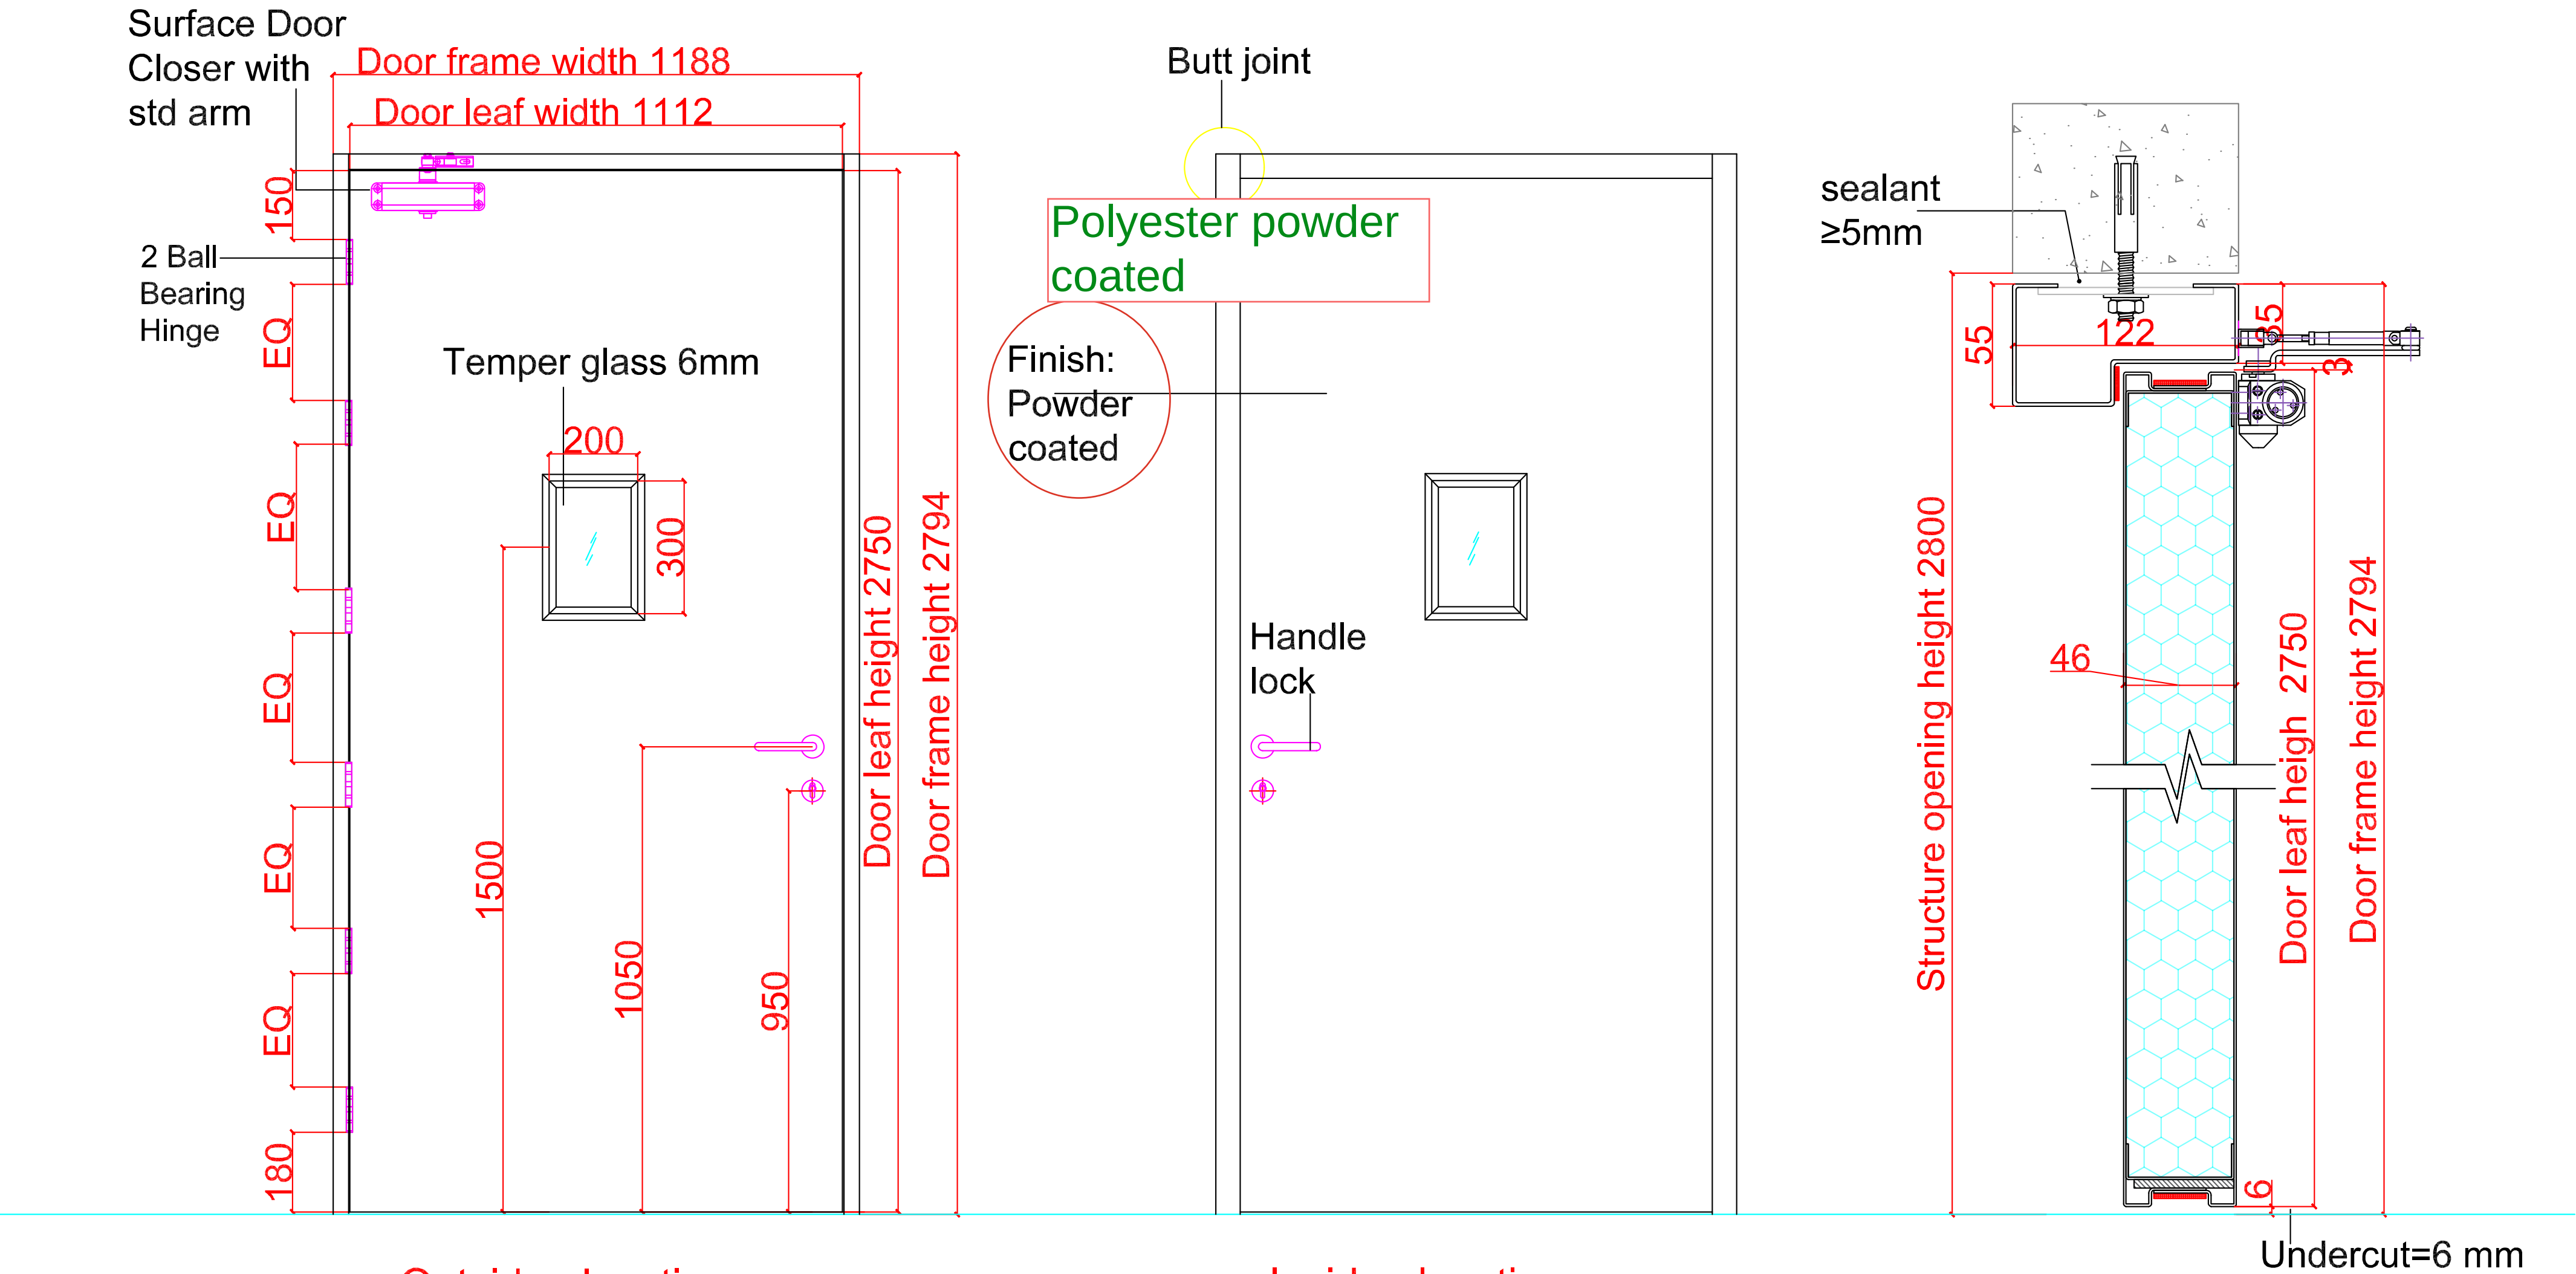


Hardware			
Name	Description	Qty	Remarks
Lock type	Mortise lock	1	
Hinge	4*4*3	6	
Door closer	184	1	
Door stop			
Glass	200*300mm	1	
Smoke seal			
Door frame	1.2mm Galvanized steel sheet		
Door leaf	0.8mm Galvanized steel sheet		
Threshold			
Filling	Honeycomb		
Colour			

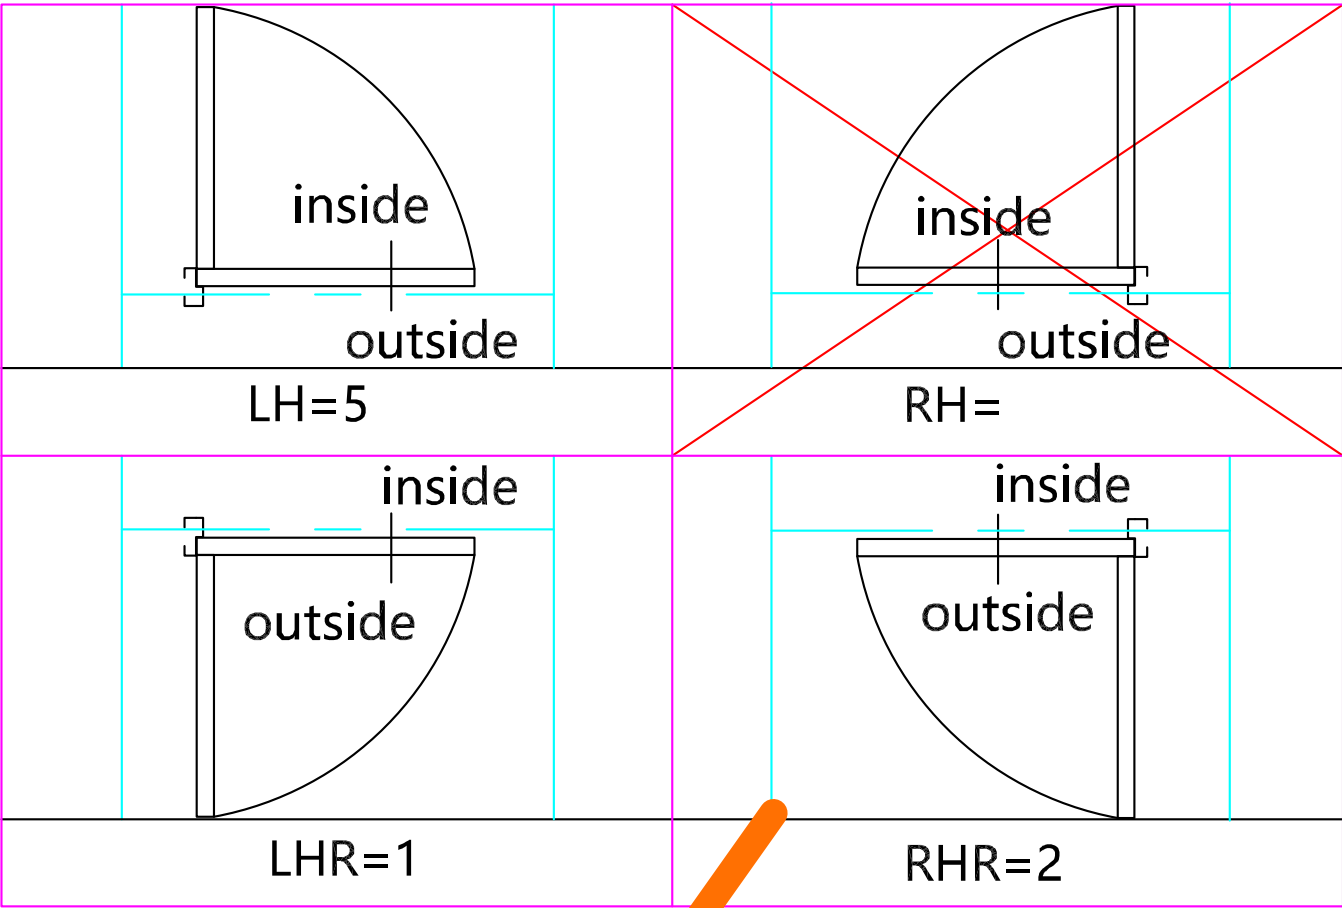

 Shanghai Xunzhong Industry Co., Ltd			
Project name			
By		Drawing title	
Design		Size	
Check		Qty	8
Review		Opening direction	
Approval		Date	2026.05.18
		Page No	20
Total Page	34	Diagram number	



GSLD1

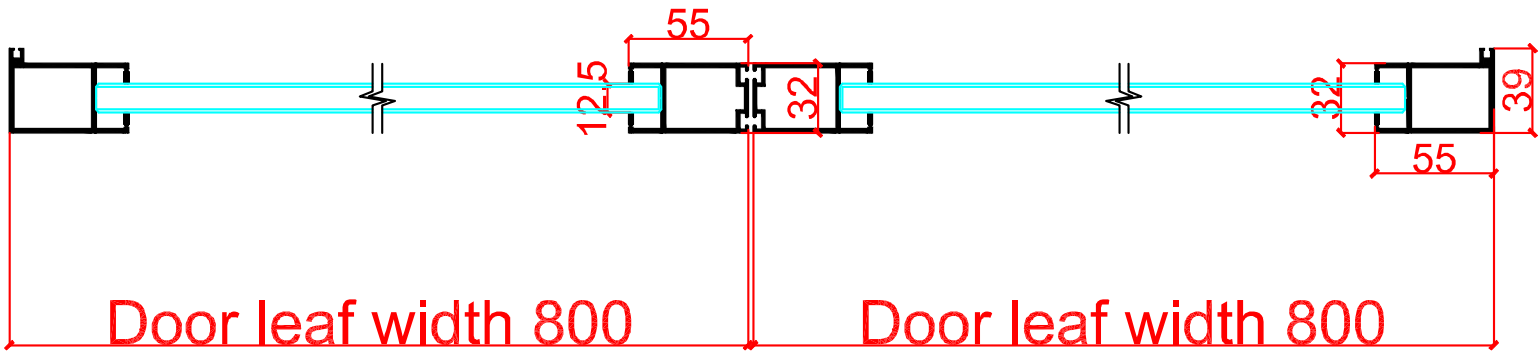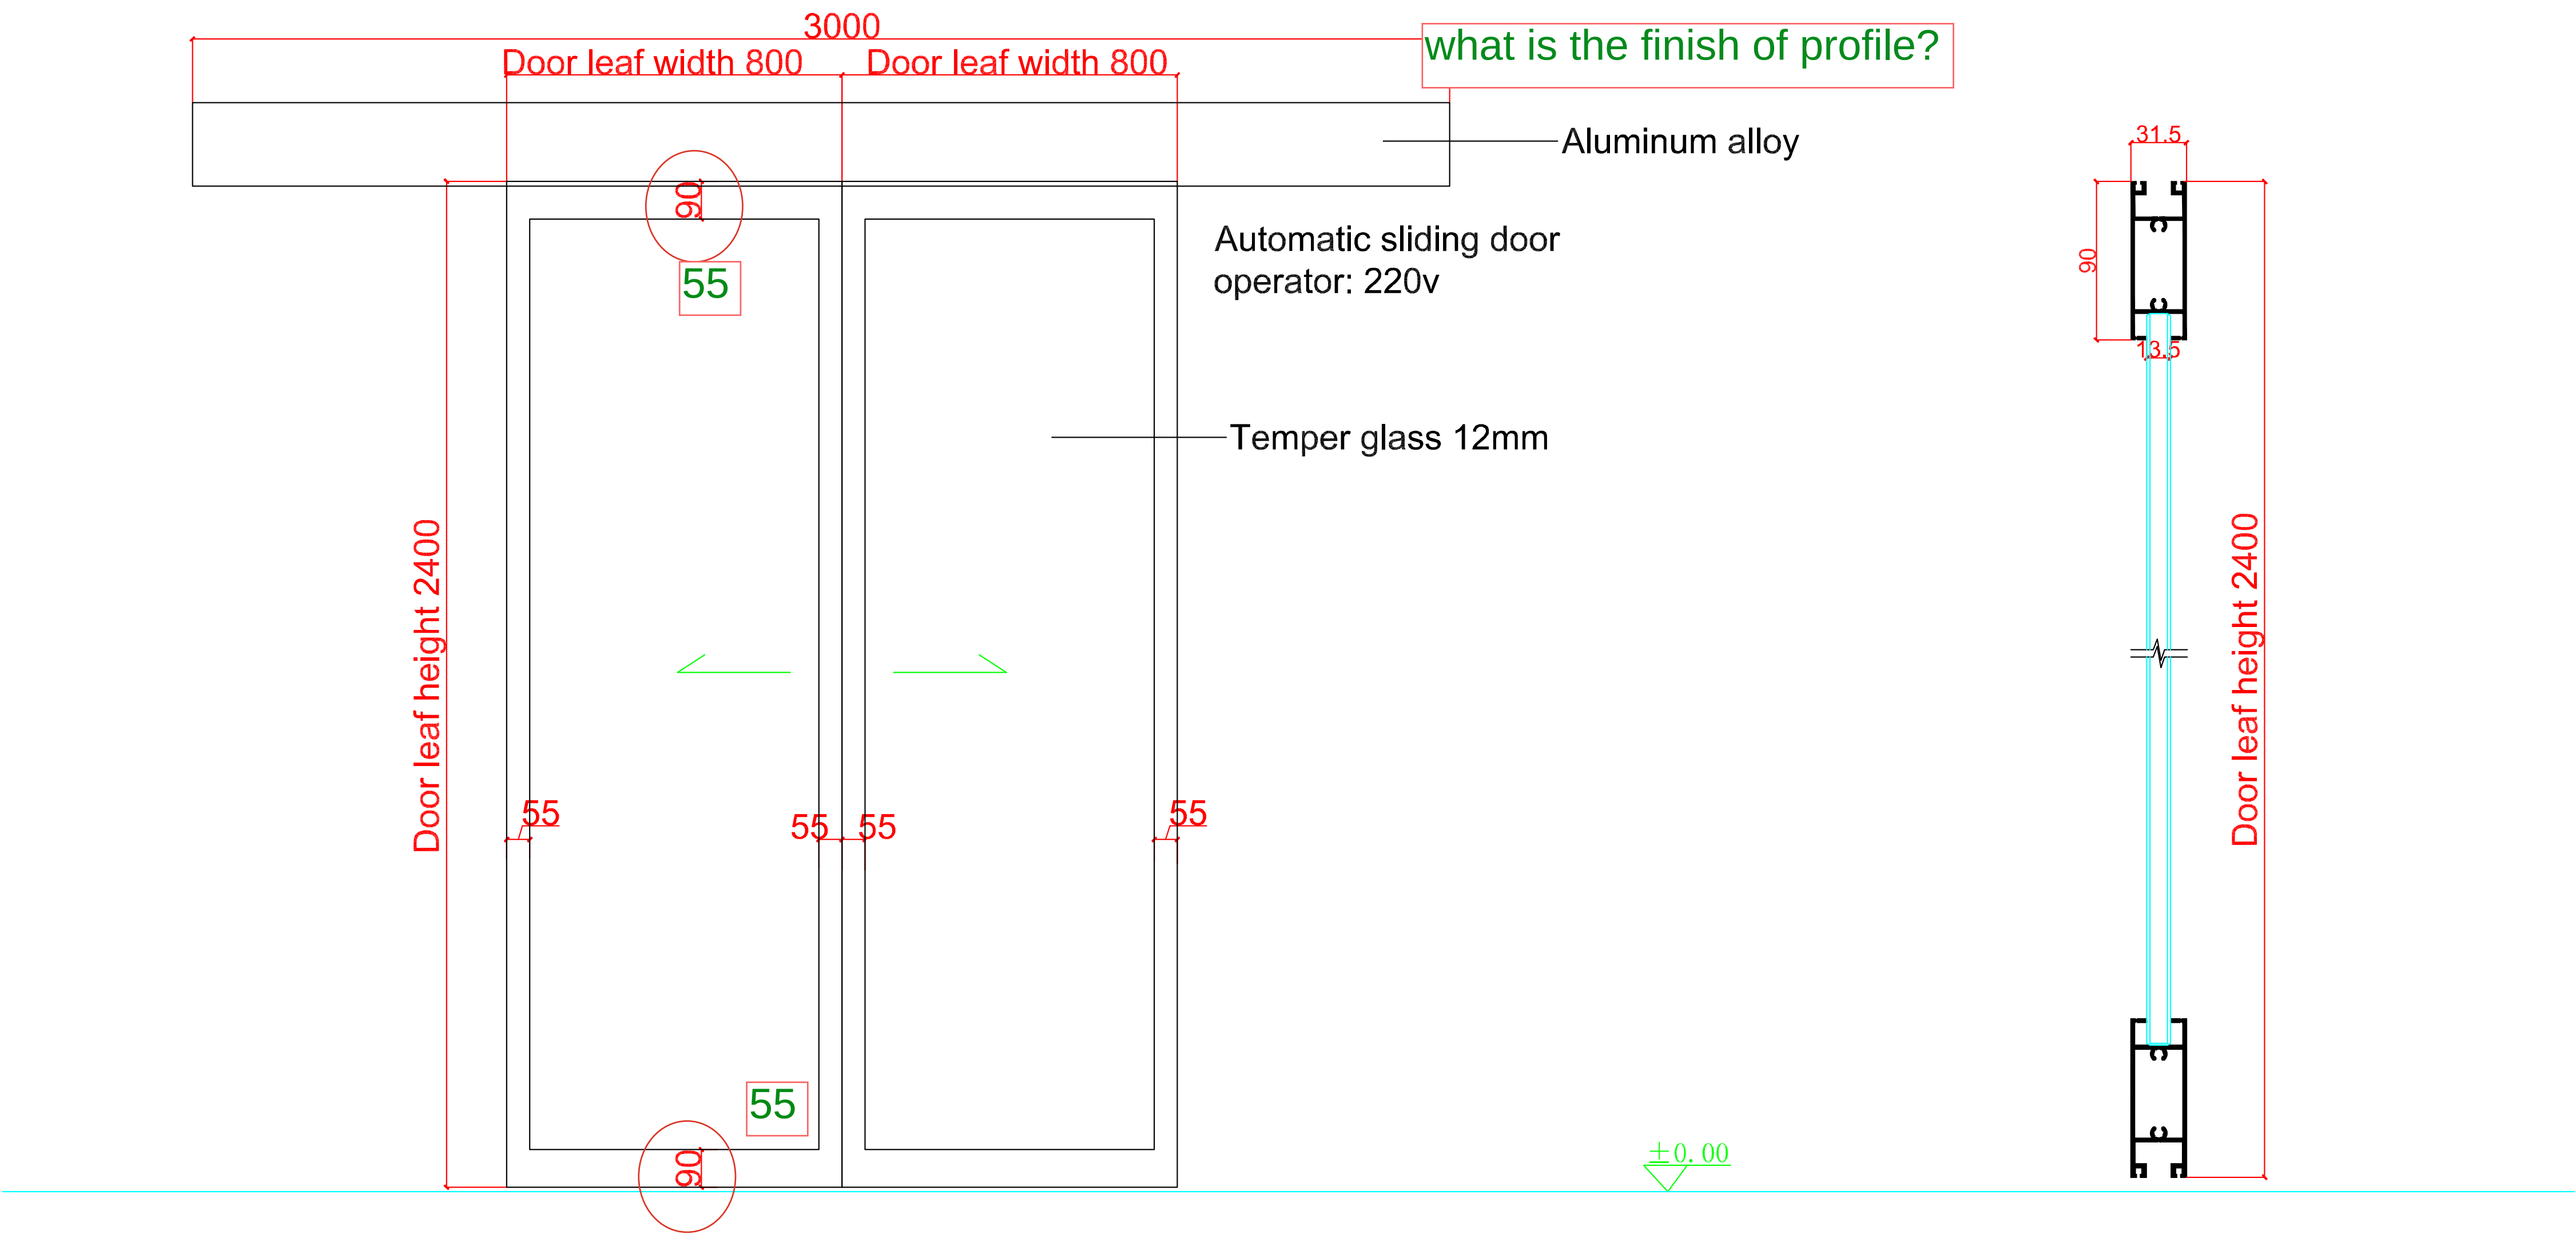

Hardware	
Name	Qty
Wall mounted fascia track	1
Balance wheel hanger	2
Floor guide	1
Solid door stopper	2
Radar sensor	1
Infrared and microwave combination sensor	1

 Shanghai Xunzhong Industry Co., Ltd			
Project name			
By		Drawing title	
Design		Size	
Check		Qty	1
Review		Opening direction	
Approval		Date	2026.05.18
		Page No	29
Total Page	34	Diagram number	

GD1

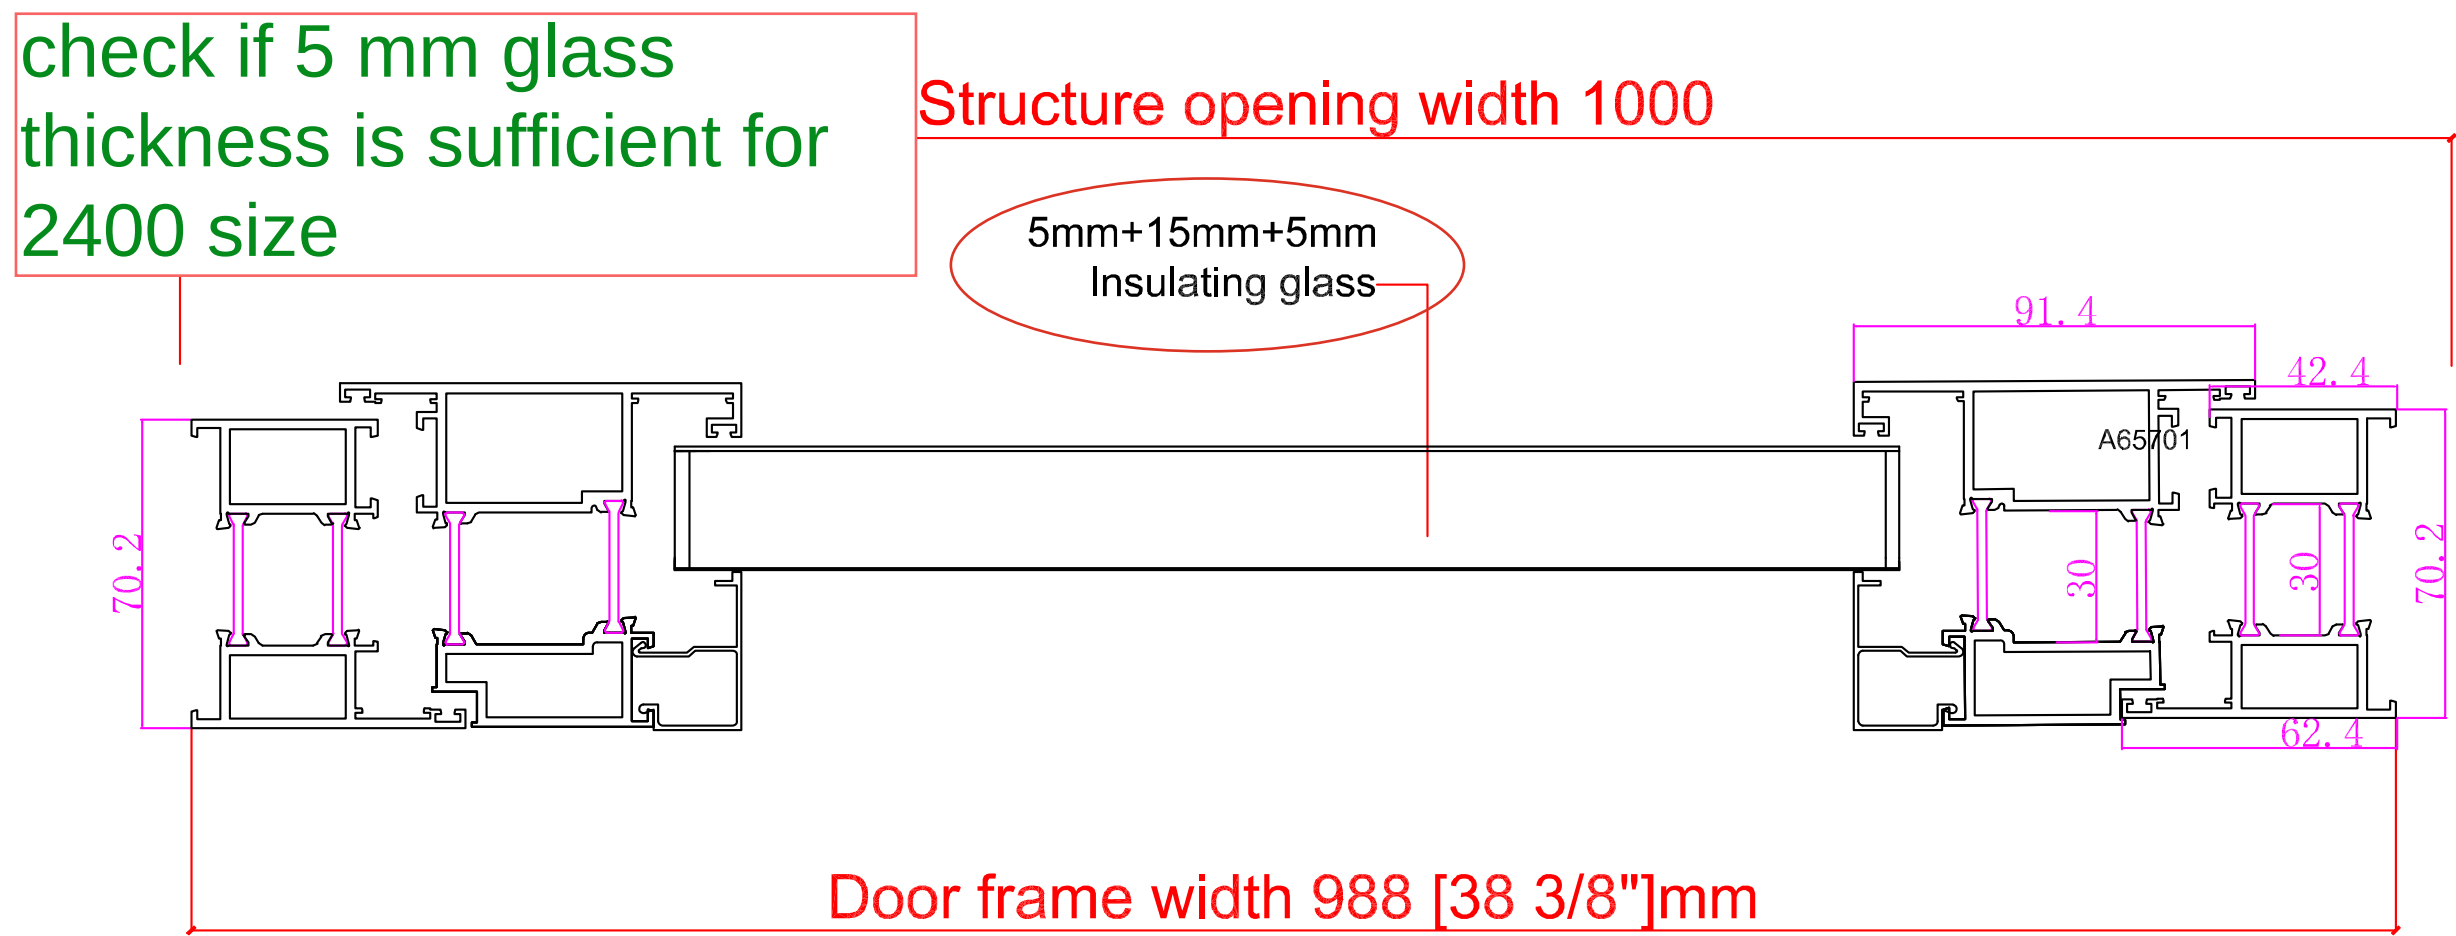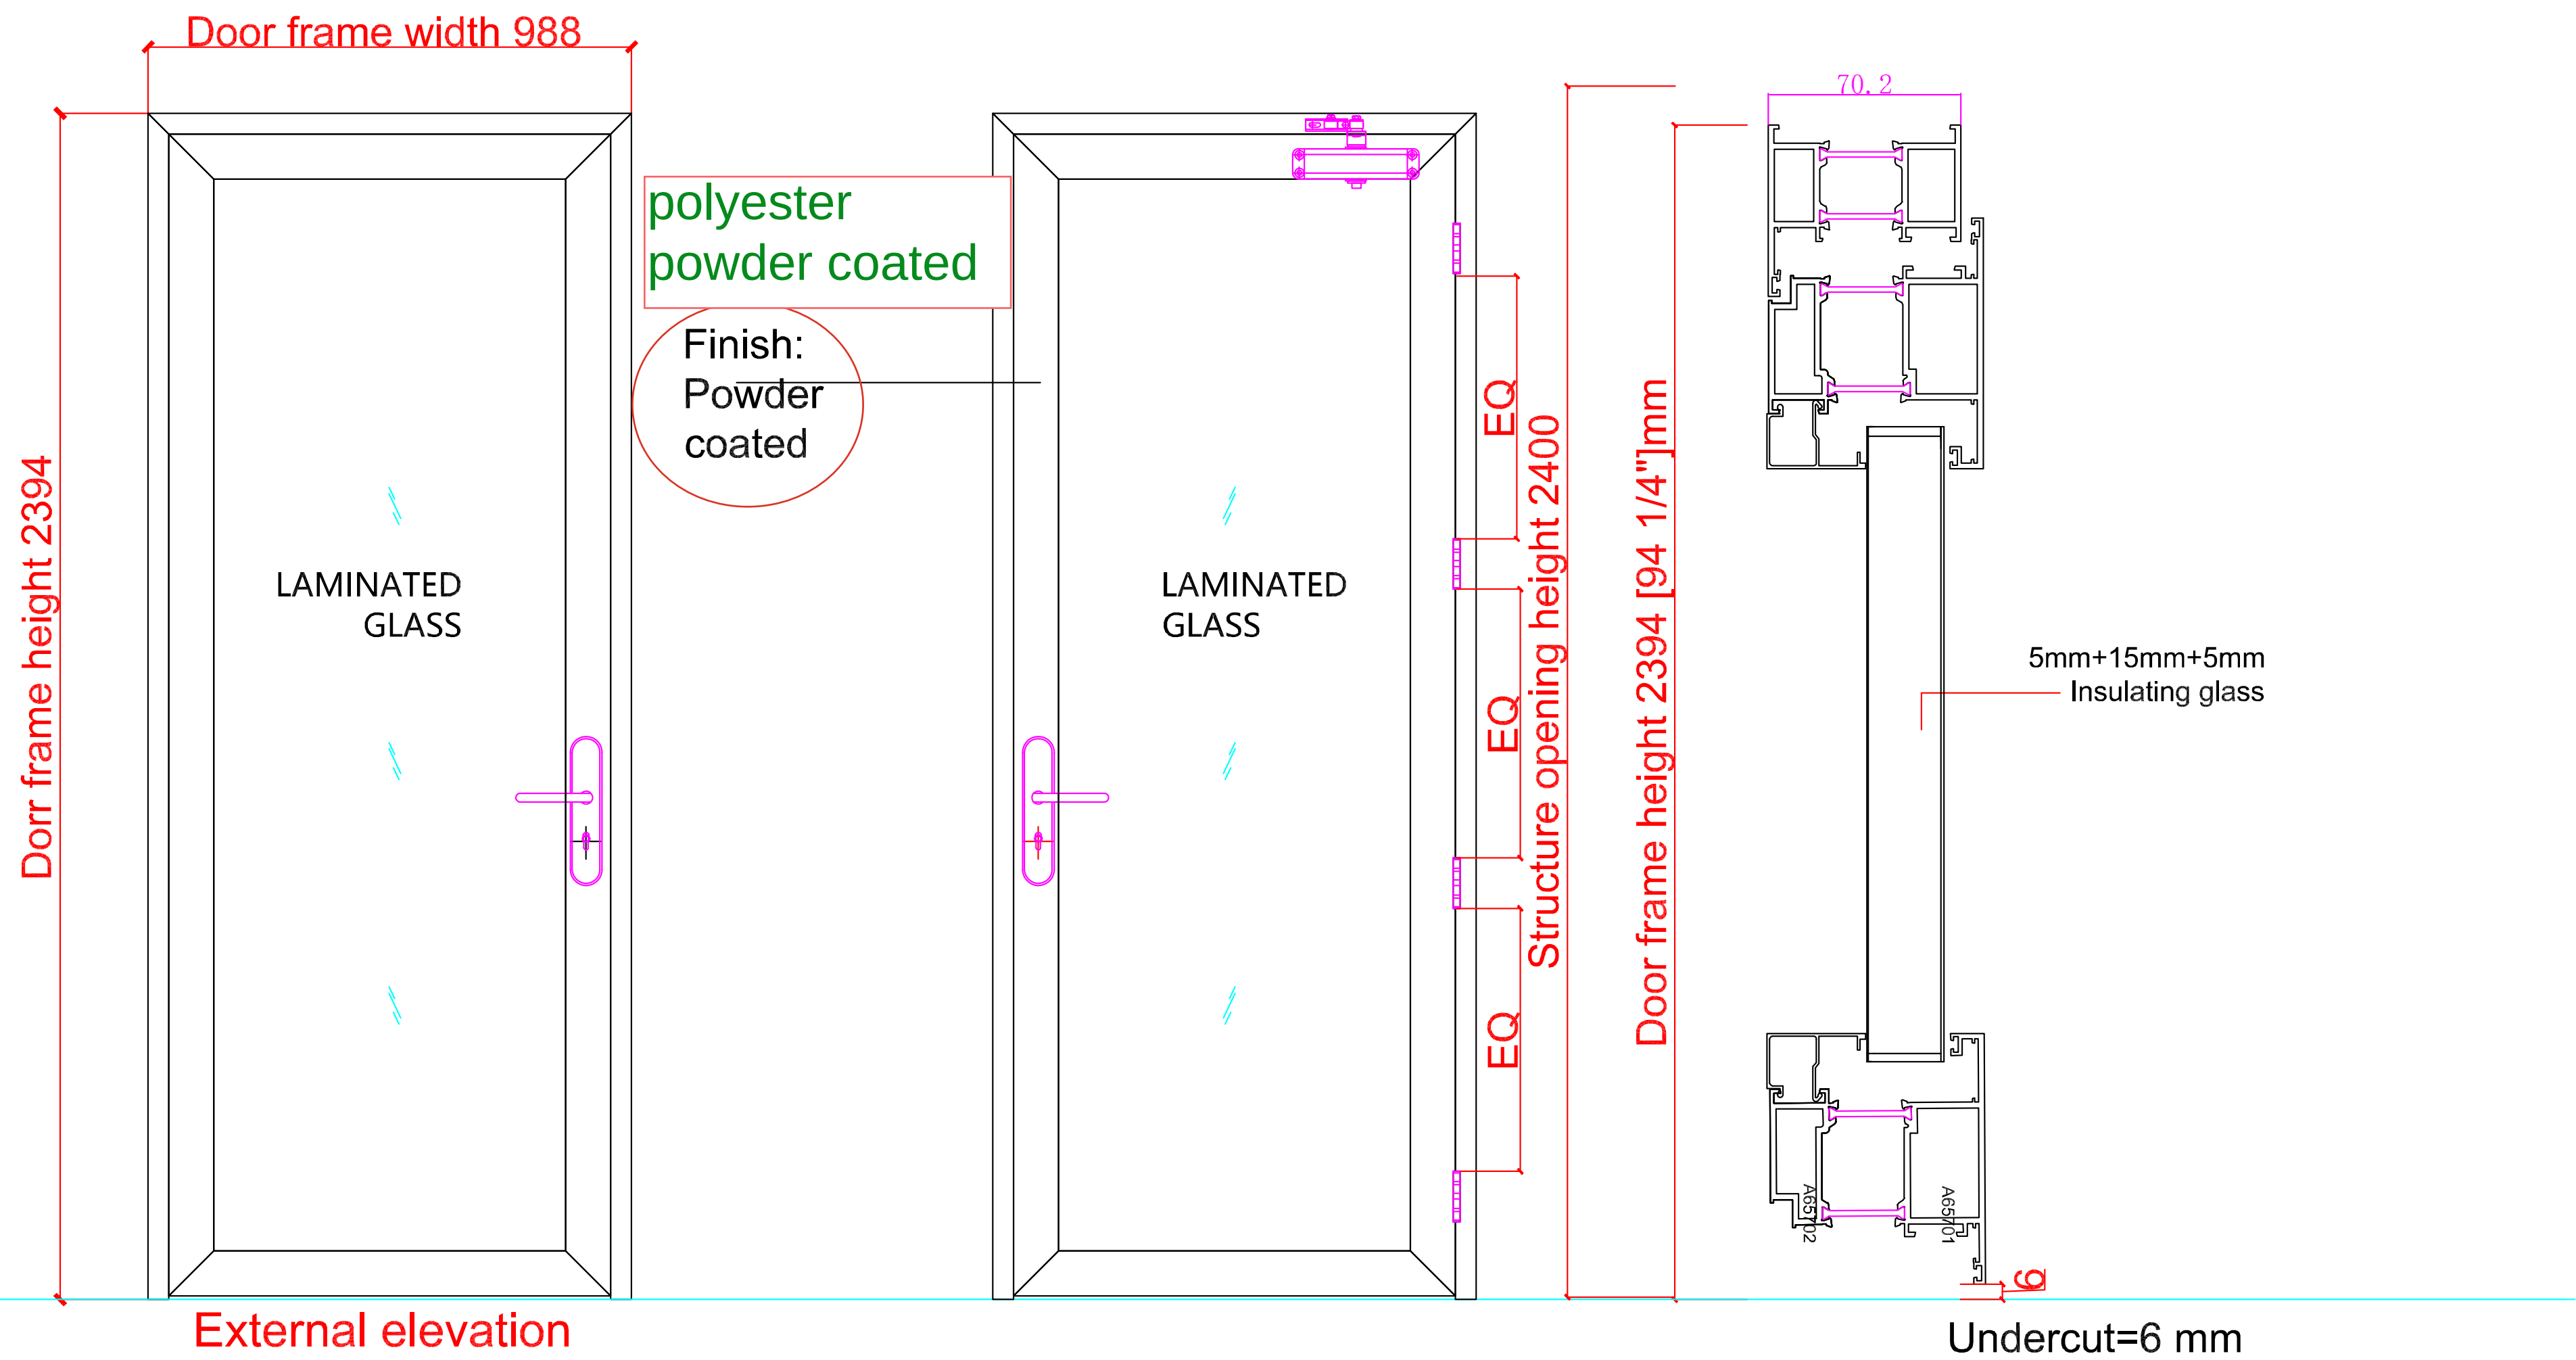

Hinge




Door closer




euro profile cylinder with both side key

Hardware			
Name	Description	Qty	Remarks
Lock type	Mortise lock	1	
Hinge	4.5*4*3	4	
Door closer		1	
Peephole			
Flush bolt			
Glass			
"Push&Pull Plate"			
Door sweep			
Smoke seal			
Door frame	2.0 mm aluminum alloy		
Door leaf	1.4 mm aluminum alloy		
Threshold			
Filling	Hollow		
Colour			

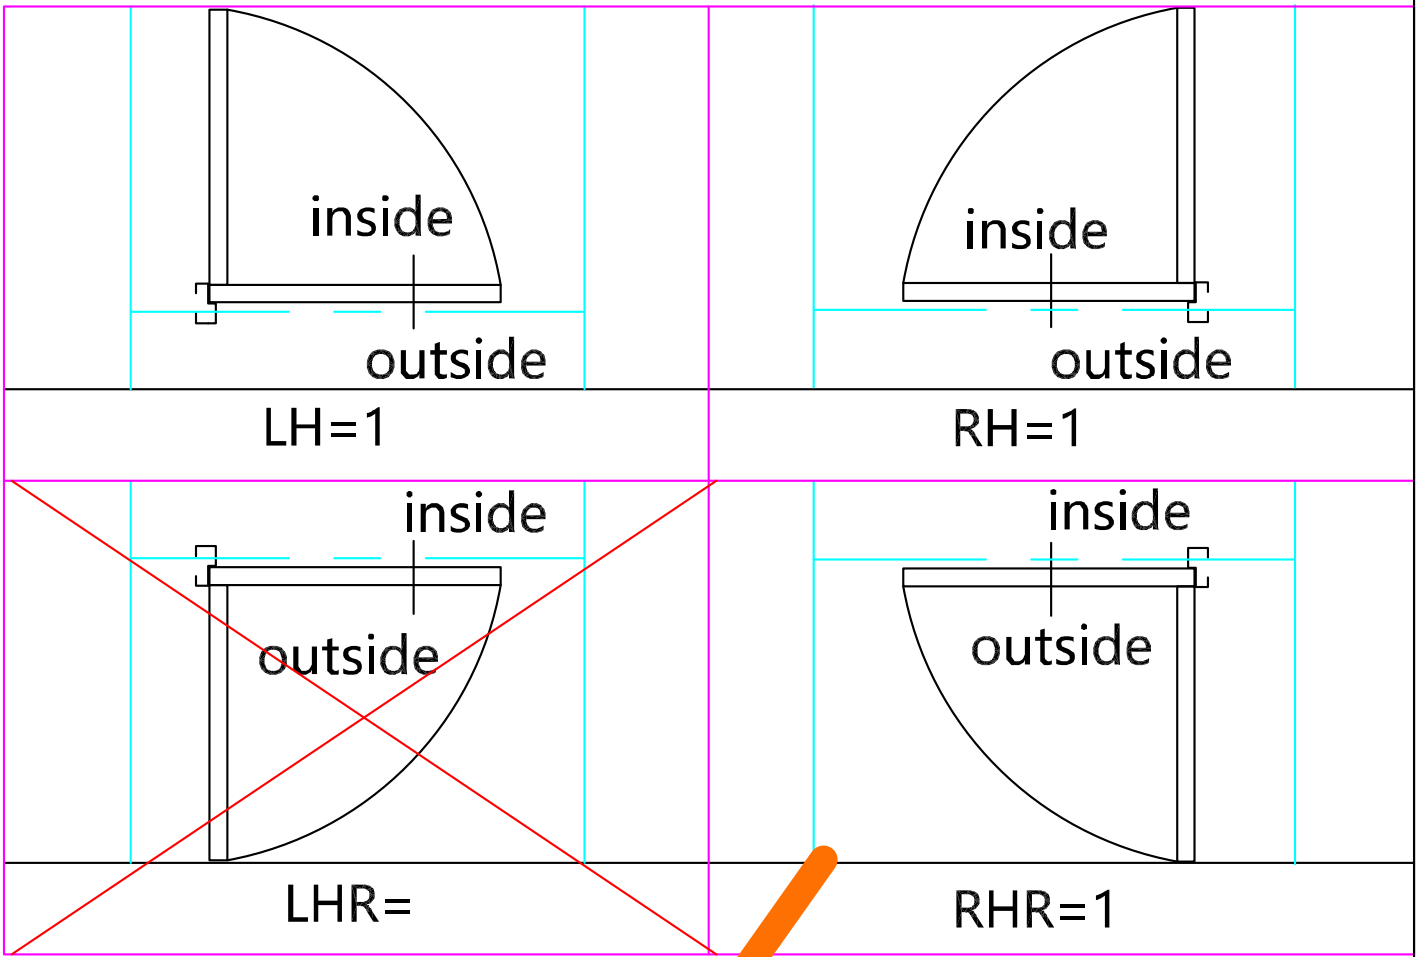


 Shanghai Xunzhong Industry Co., Ltd			
Project name			
By		Drawing title	
Design		Size	
Check		Qty	3
Review		Opening direction	
Approval		Date	2026.05.18
		Page No	1
Total Page	1	Diagram number	

GD2

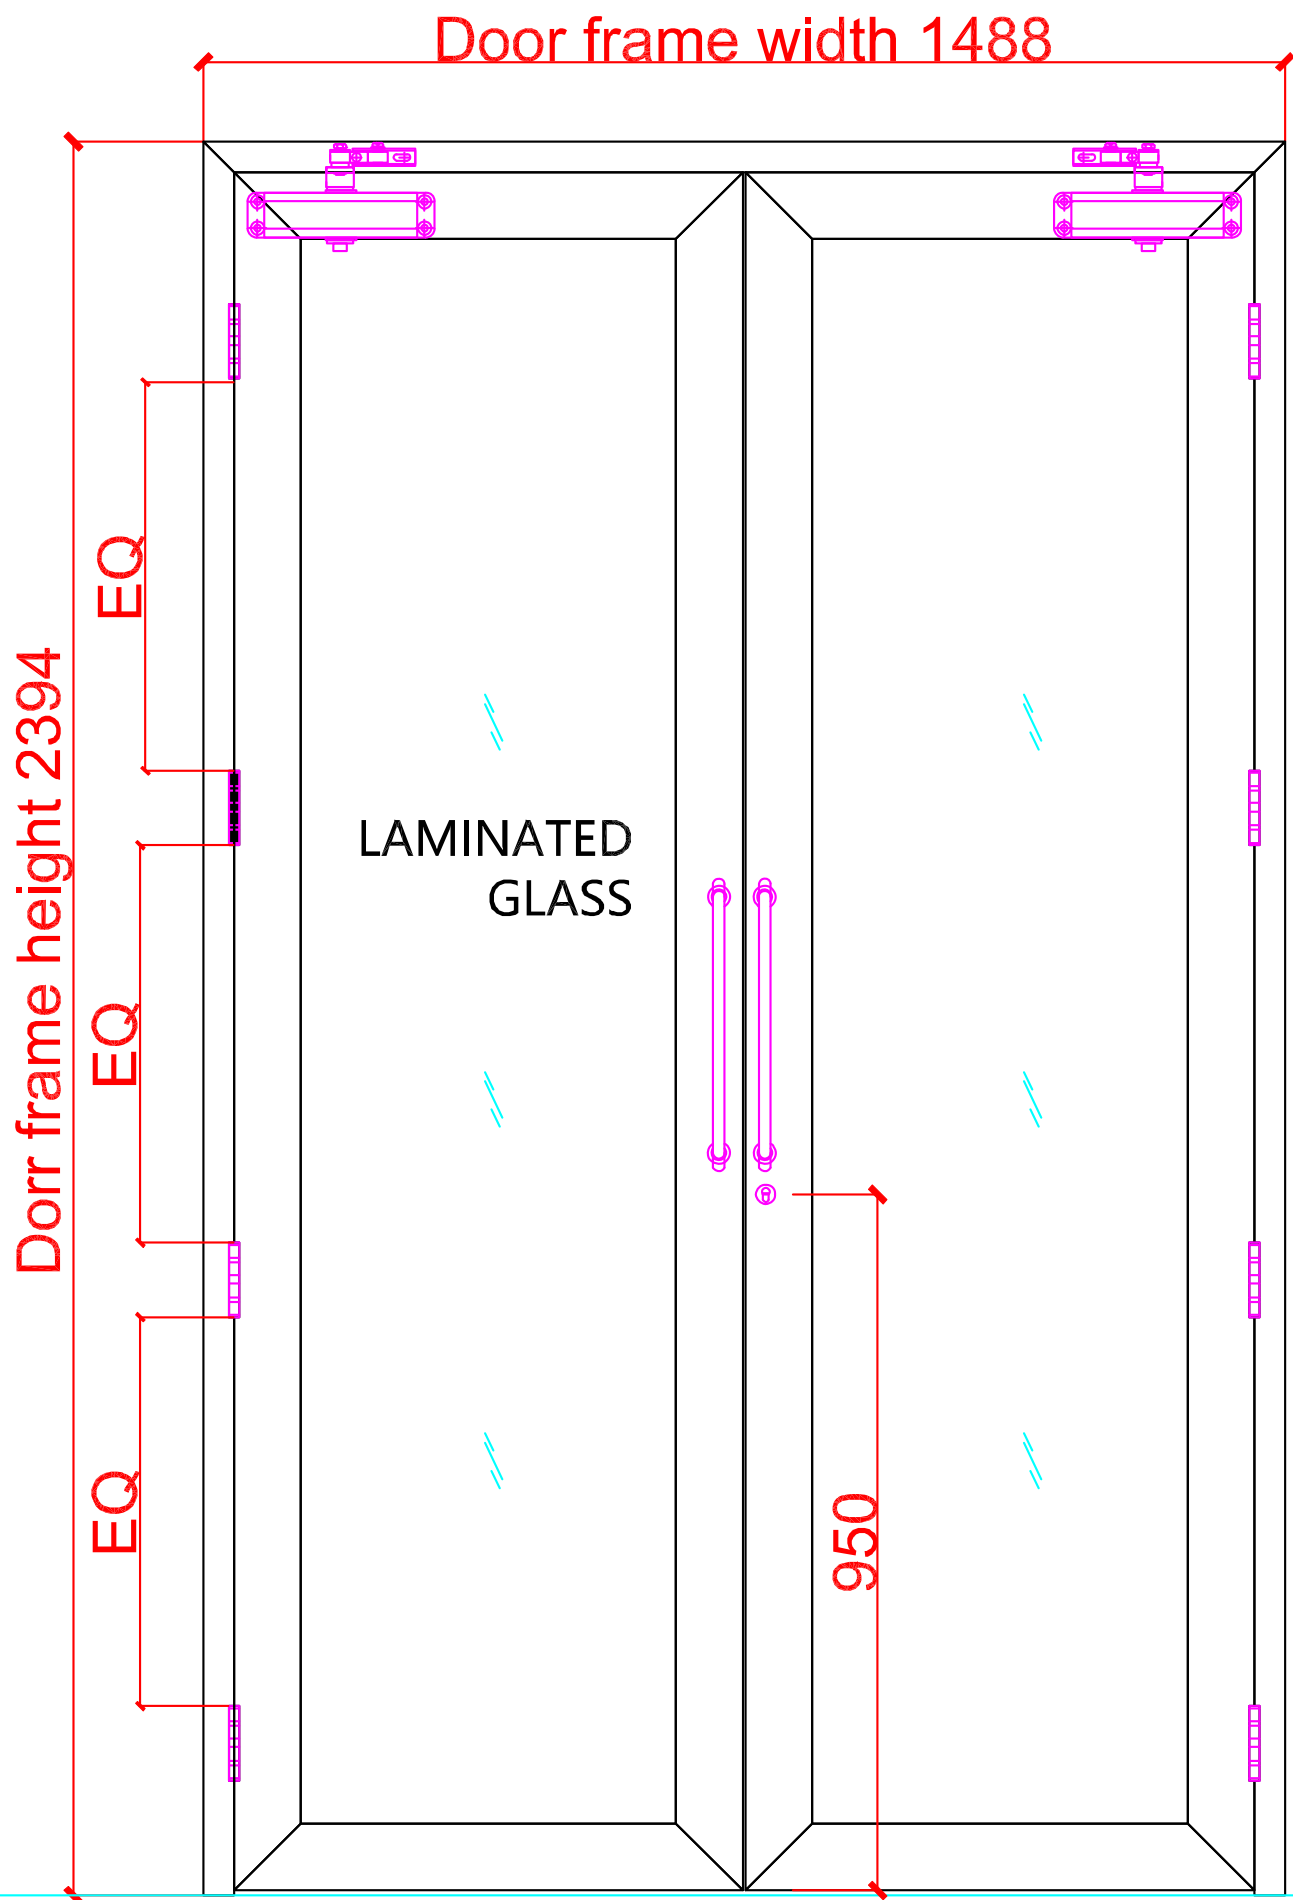


External elevation

Finish:
Powder
coated

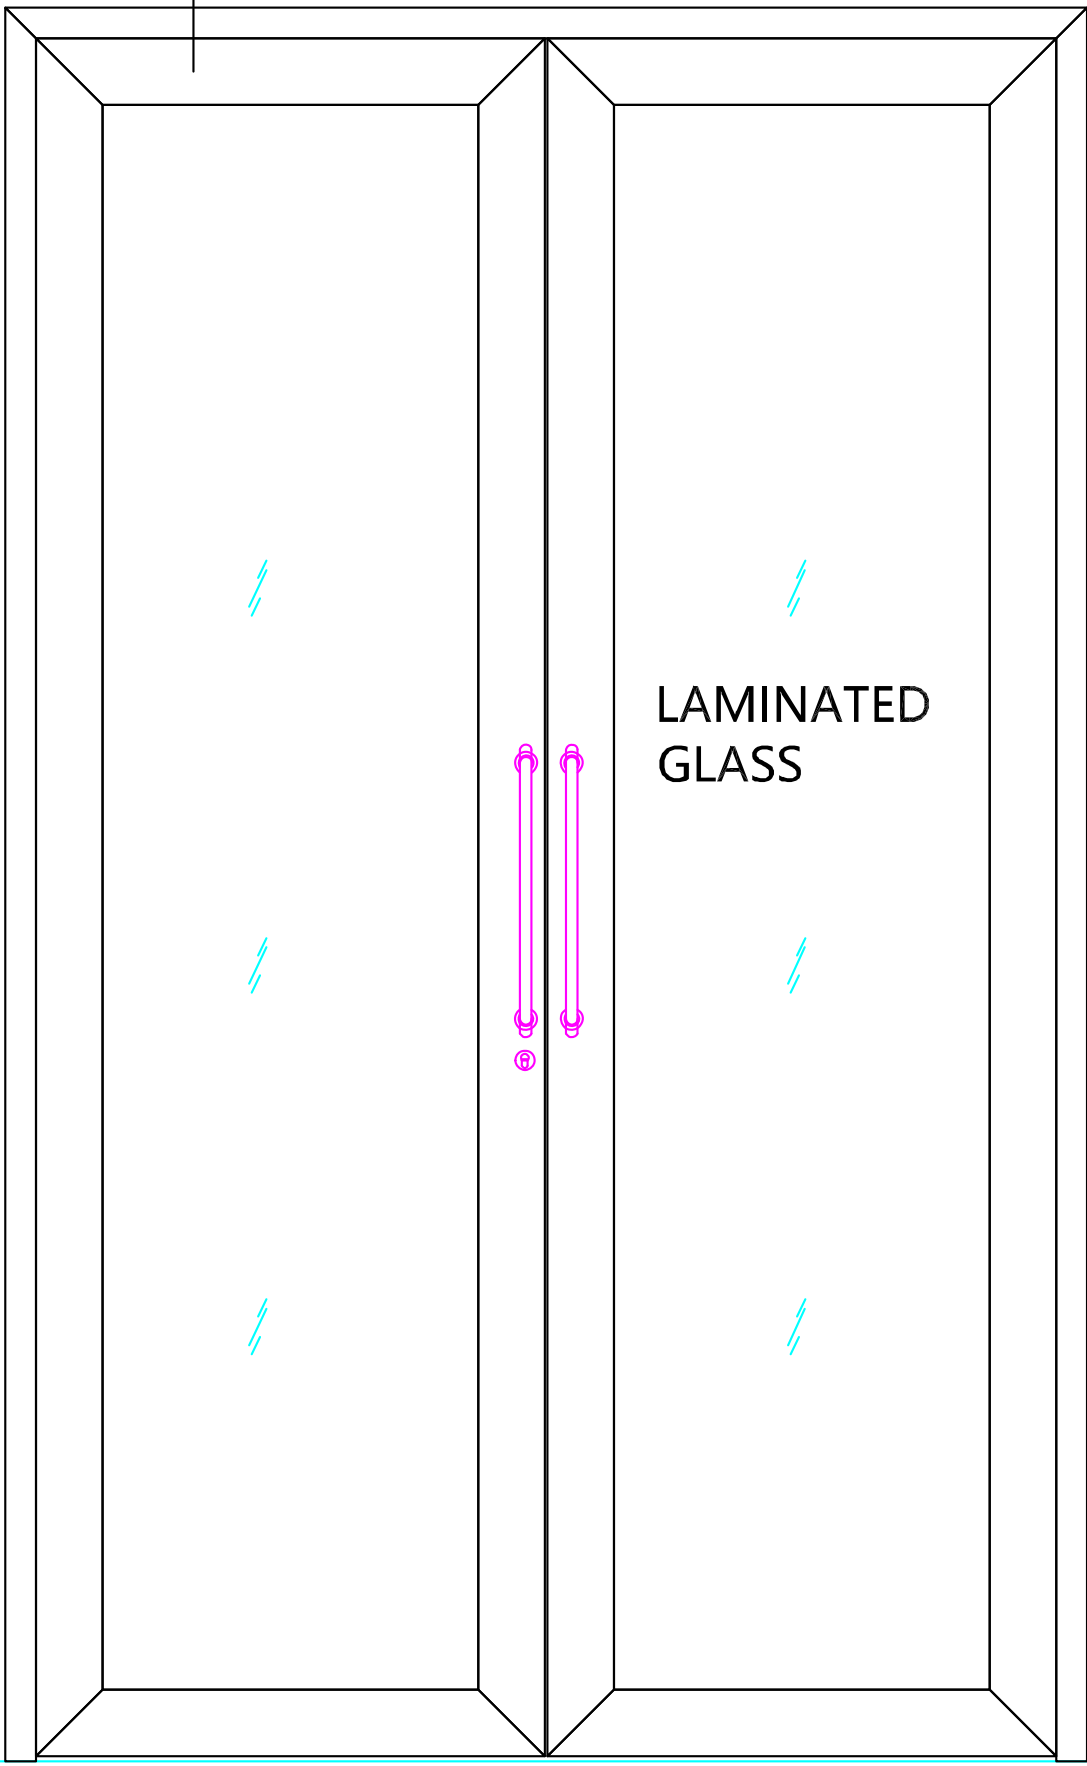

Structure opening height 2400


Door frame height 2394 [94 1/4"]mm

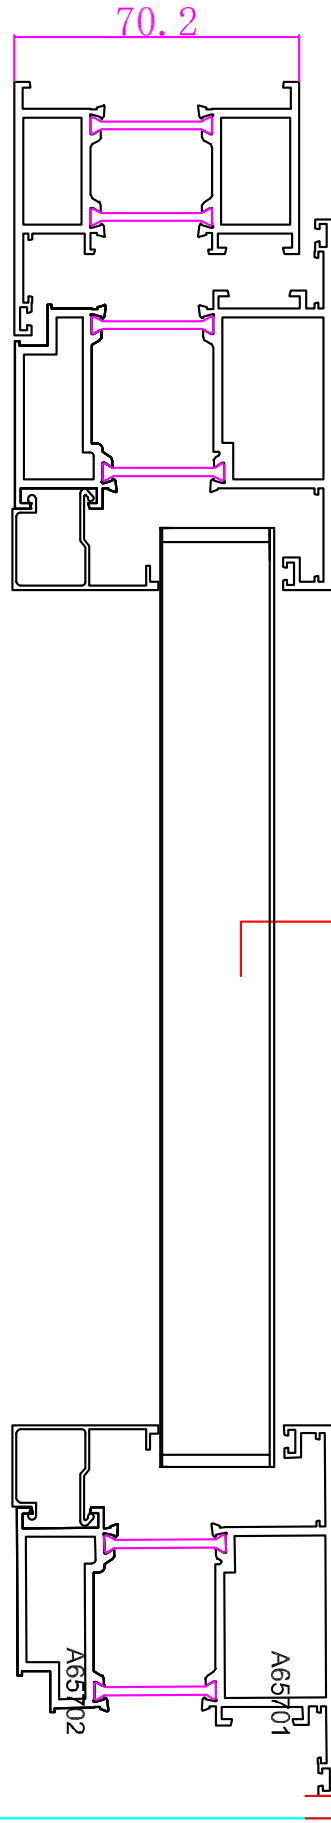

Mortise deadlock +euro profile, cylinder
with one side key+ (no thumbturn)

5mm+15mm+5mm
Insulating glass


Undercut=6 mm

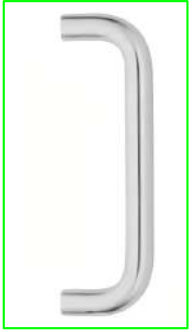

D type handle



Mortise deadlock +euro profile, cylinder
with one side key+ (no thumbturn)

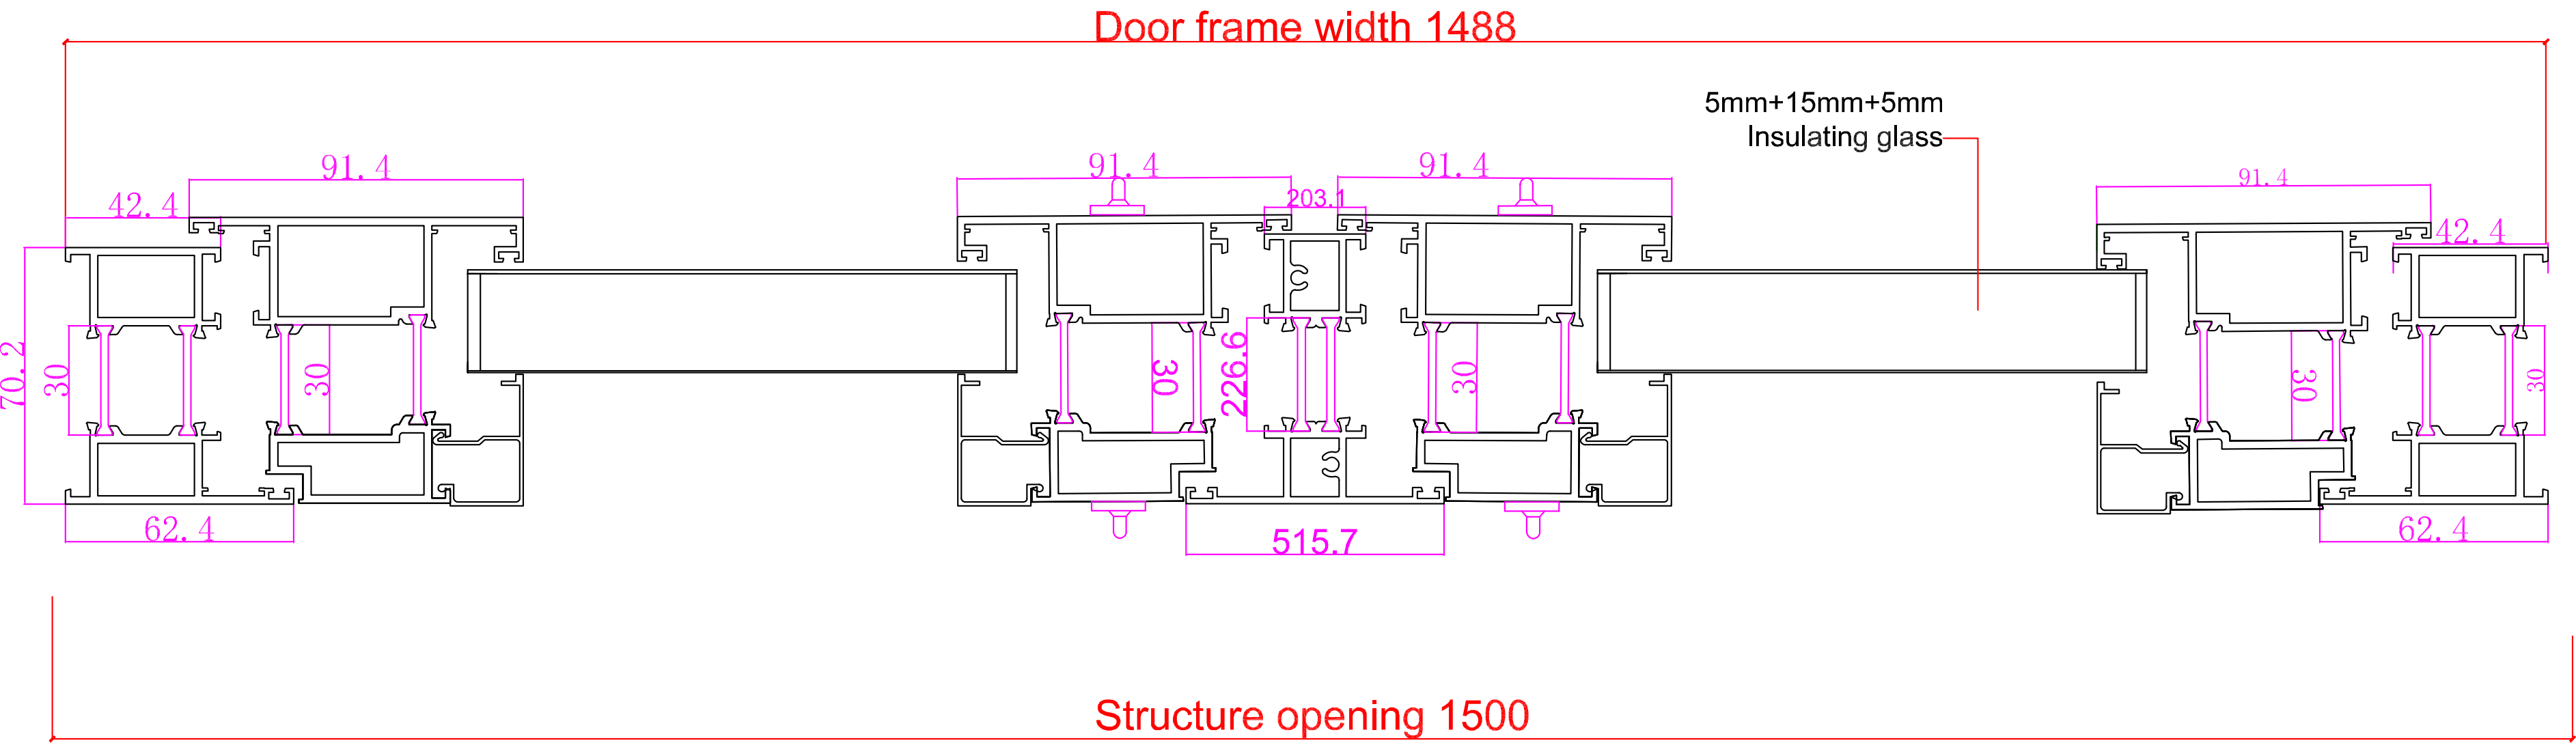

Structure opening 1500



Hinge




Door closer

Hardware

Name	Description	Qty	Remarks
Lock type	Mortise lock	1	
Hinge	4.5*4*3	8	
Door closer		2	
Peephole			
Flush bolt			
Glass "Push&Pull Plate"			
Door sweep			
Smoke seal			
Door frame			
Door leaf			
Threshold			
Filling			
Colour			

hardware Items are missing.
mention all the hardware used in door.
Refer Drawing nos. 97& 98

SET 10 DOUBLE LEAF ALUMINIUM FRAMED GLASS DOOR (1500 X 2400) - ENTRANCE LOBBY					
THUMBNAIL	PRODUCT DESCRIPTION	FINISH	QUANTITY	UNIT	DOOR TAG
	Ball bearing hinge 102x89x3mm with Metal screws.	SSS	8		GD2
	Dust proof strike for flush bolts.	SSS	1		
	Automatic flush bolt.	SSS	1	Pair	
	6 pin euro profile cylinder with both side key.	SSS	1		
	Euro mortise narrow stile lock 30mm back set.	SSS	1		
	Surface mounted door closer.	SIL	2		
	D-type pull handle, back to back mount, size 300x25mm.	SSS	2	Pair	

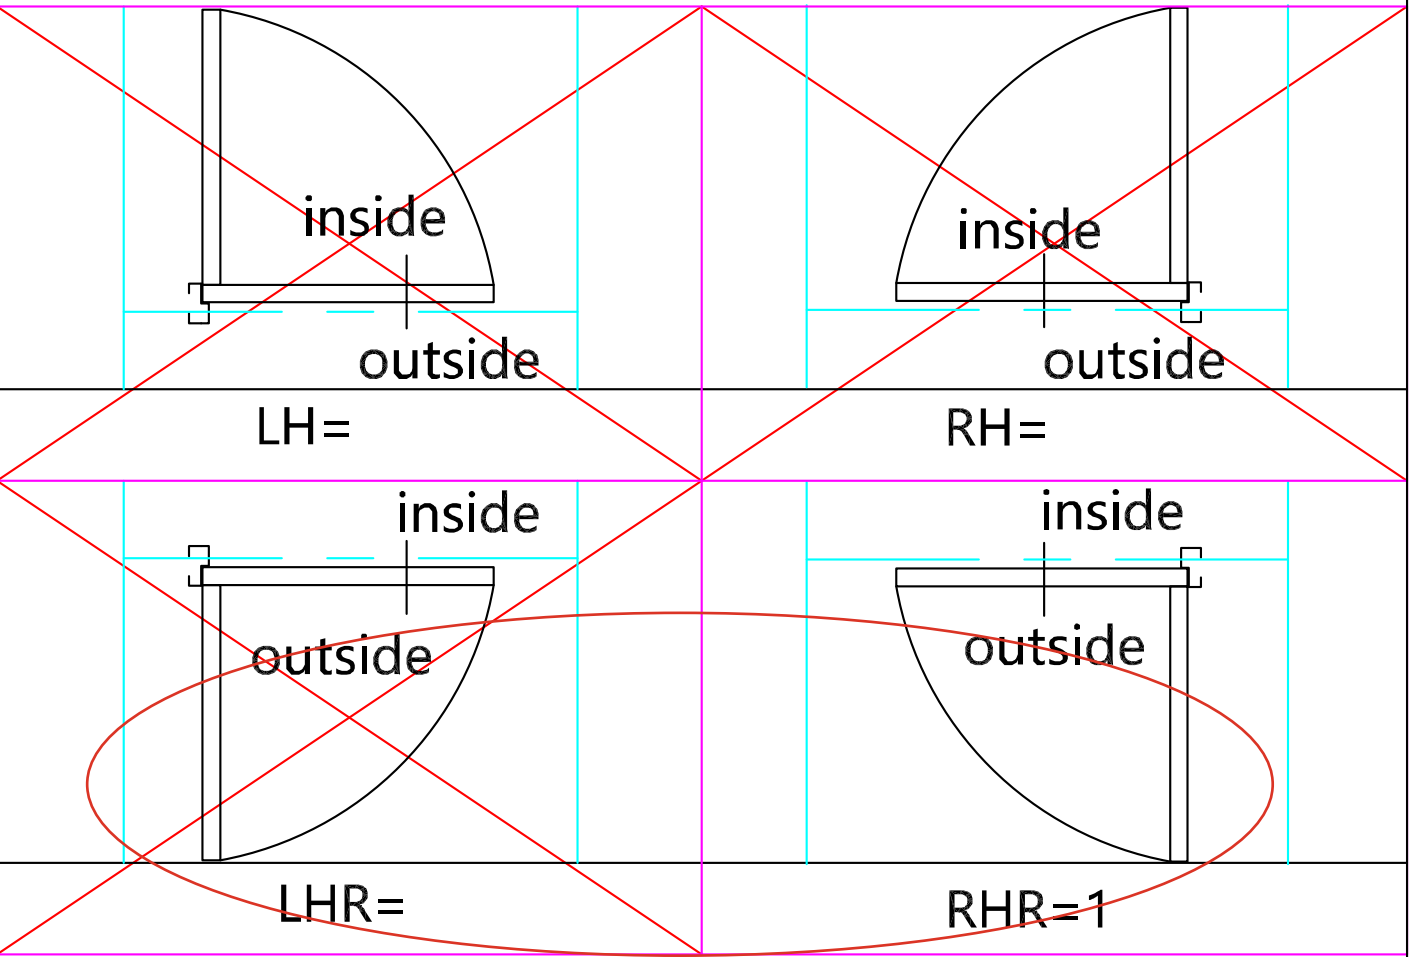

GD2 - LHA + RHA






Shanghai Xunzhong Industry Co., Ltd


Project name

By		Drawing title	
Design		Size	
Check		Qty	1
Review		Opening direction	
Approval		Date	2026.05.18
		Page No	1
Total Page	1	Diagram number	

FRS1

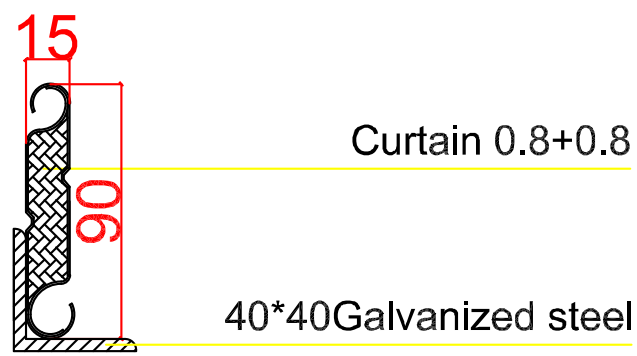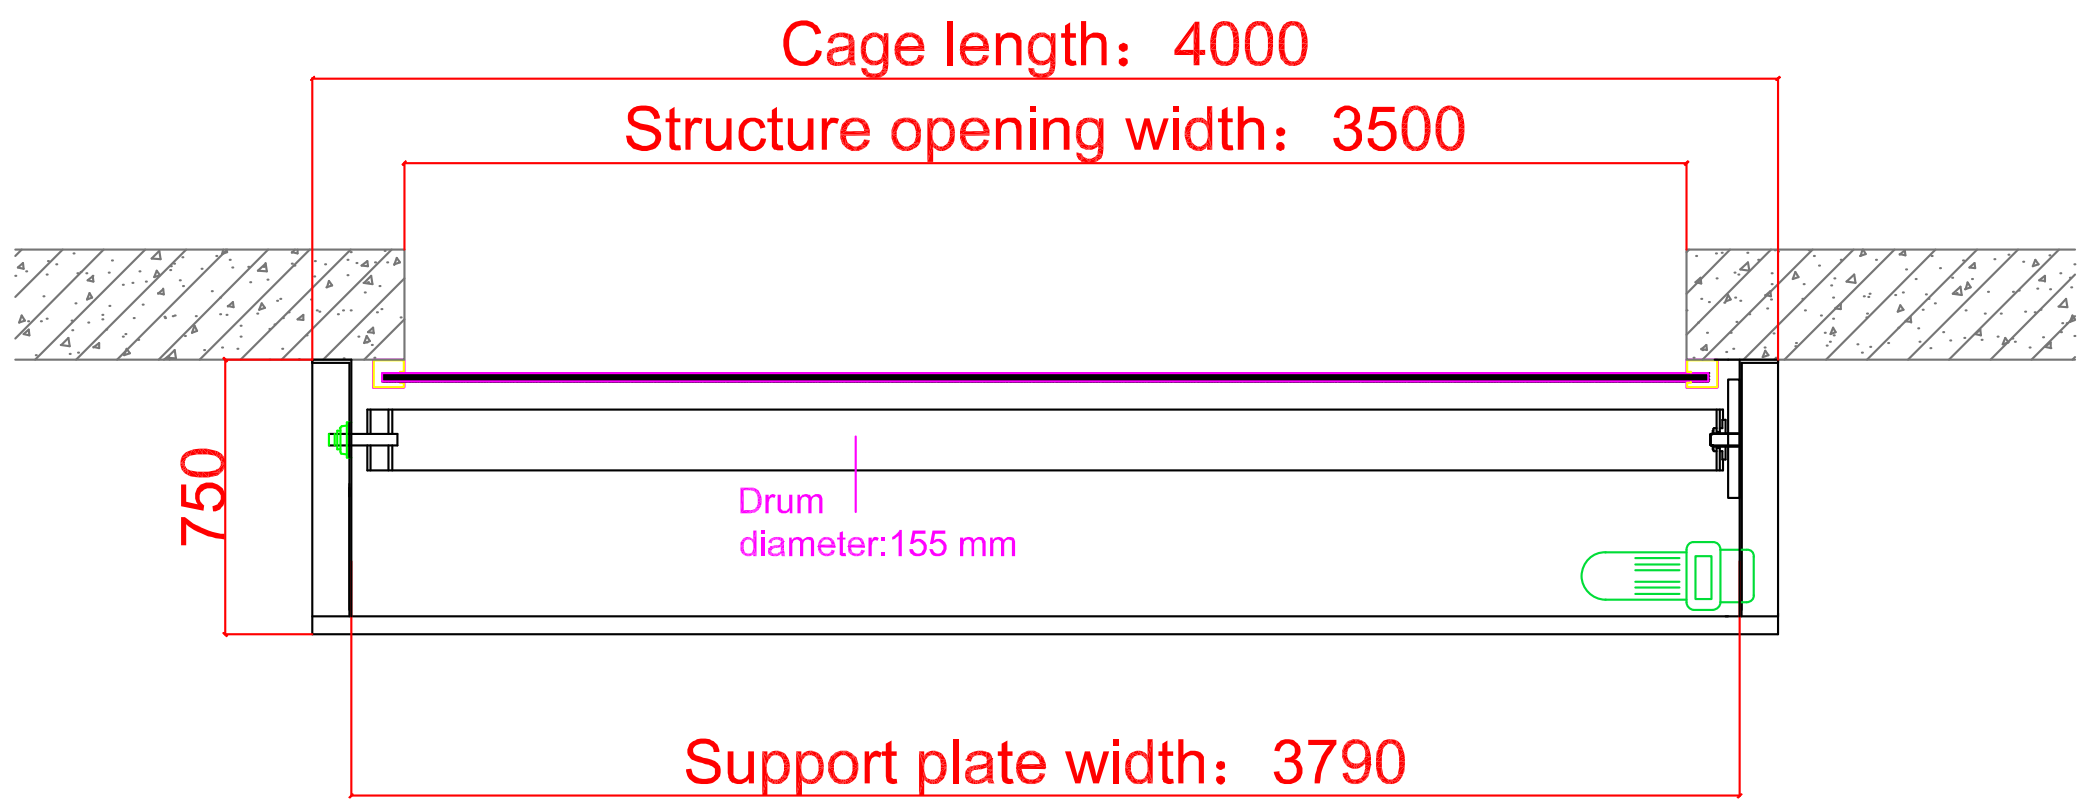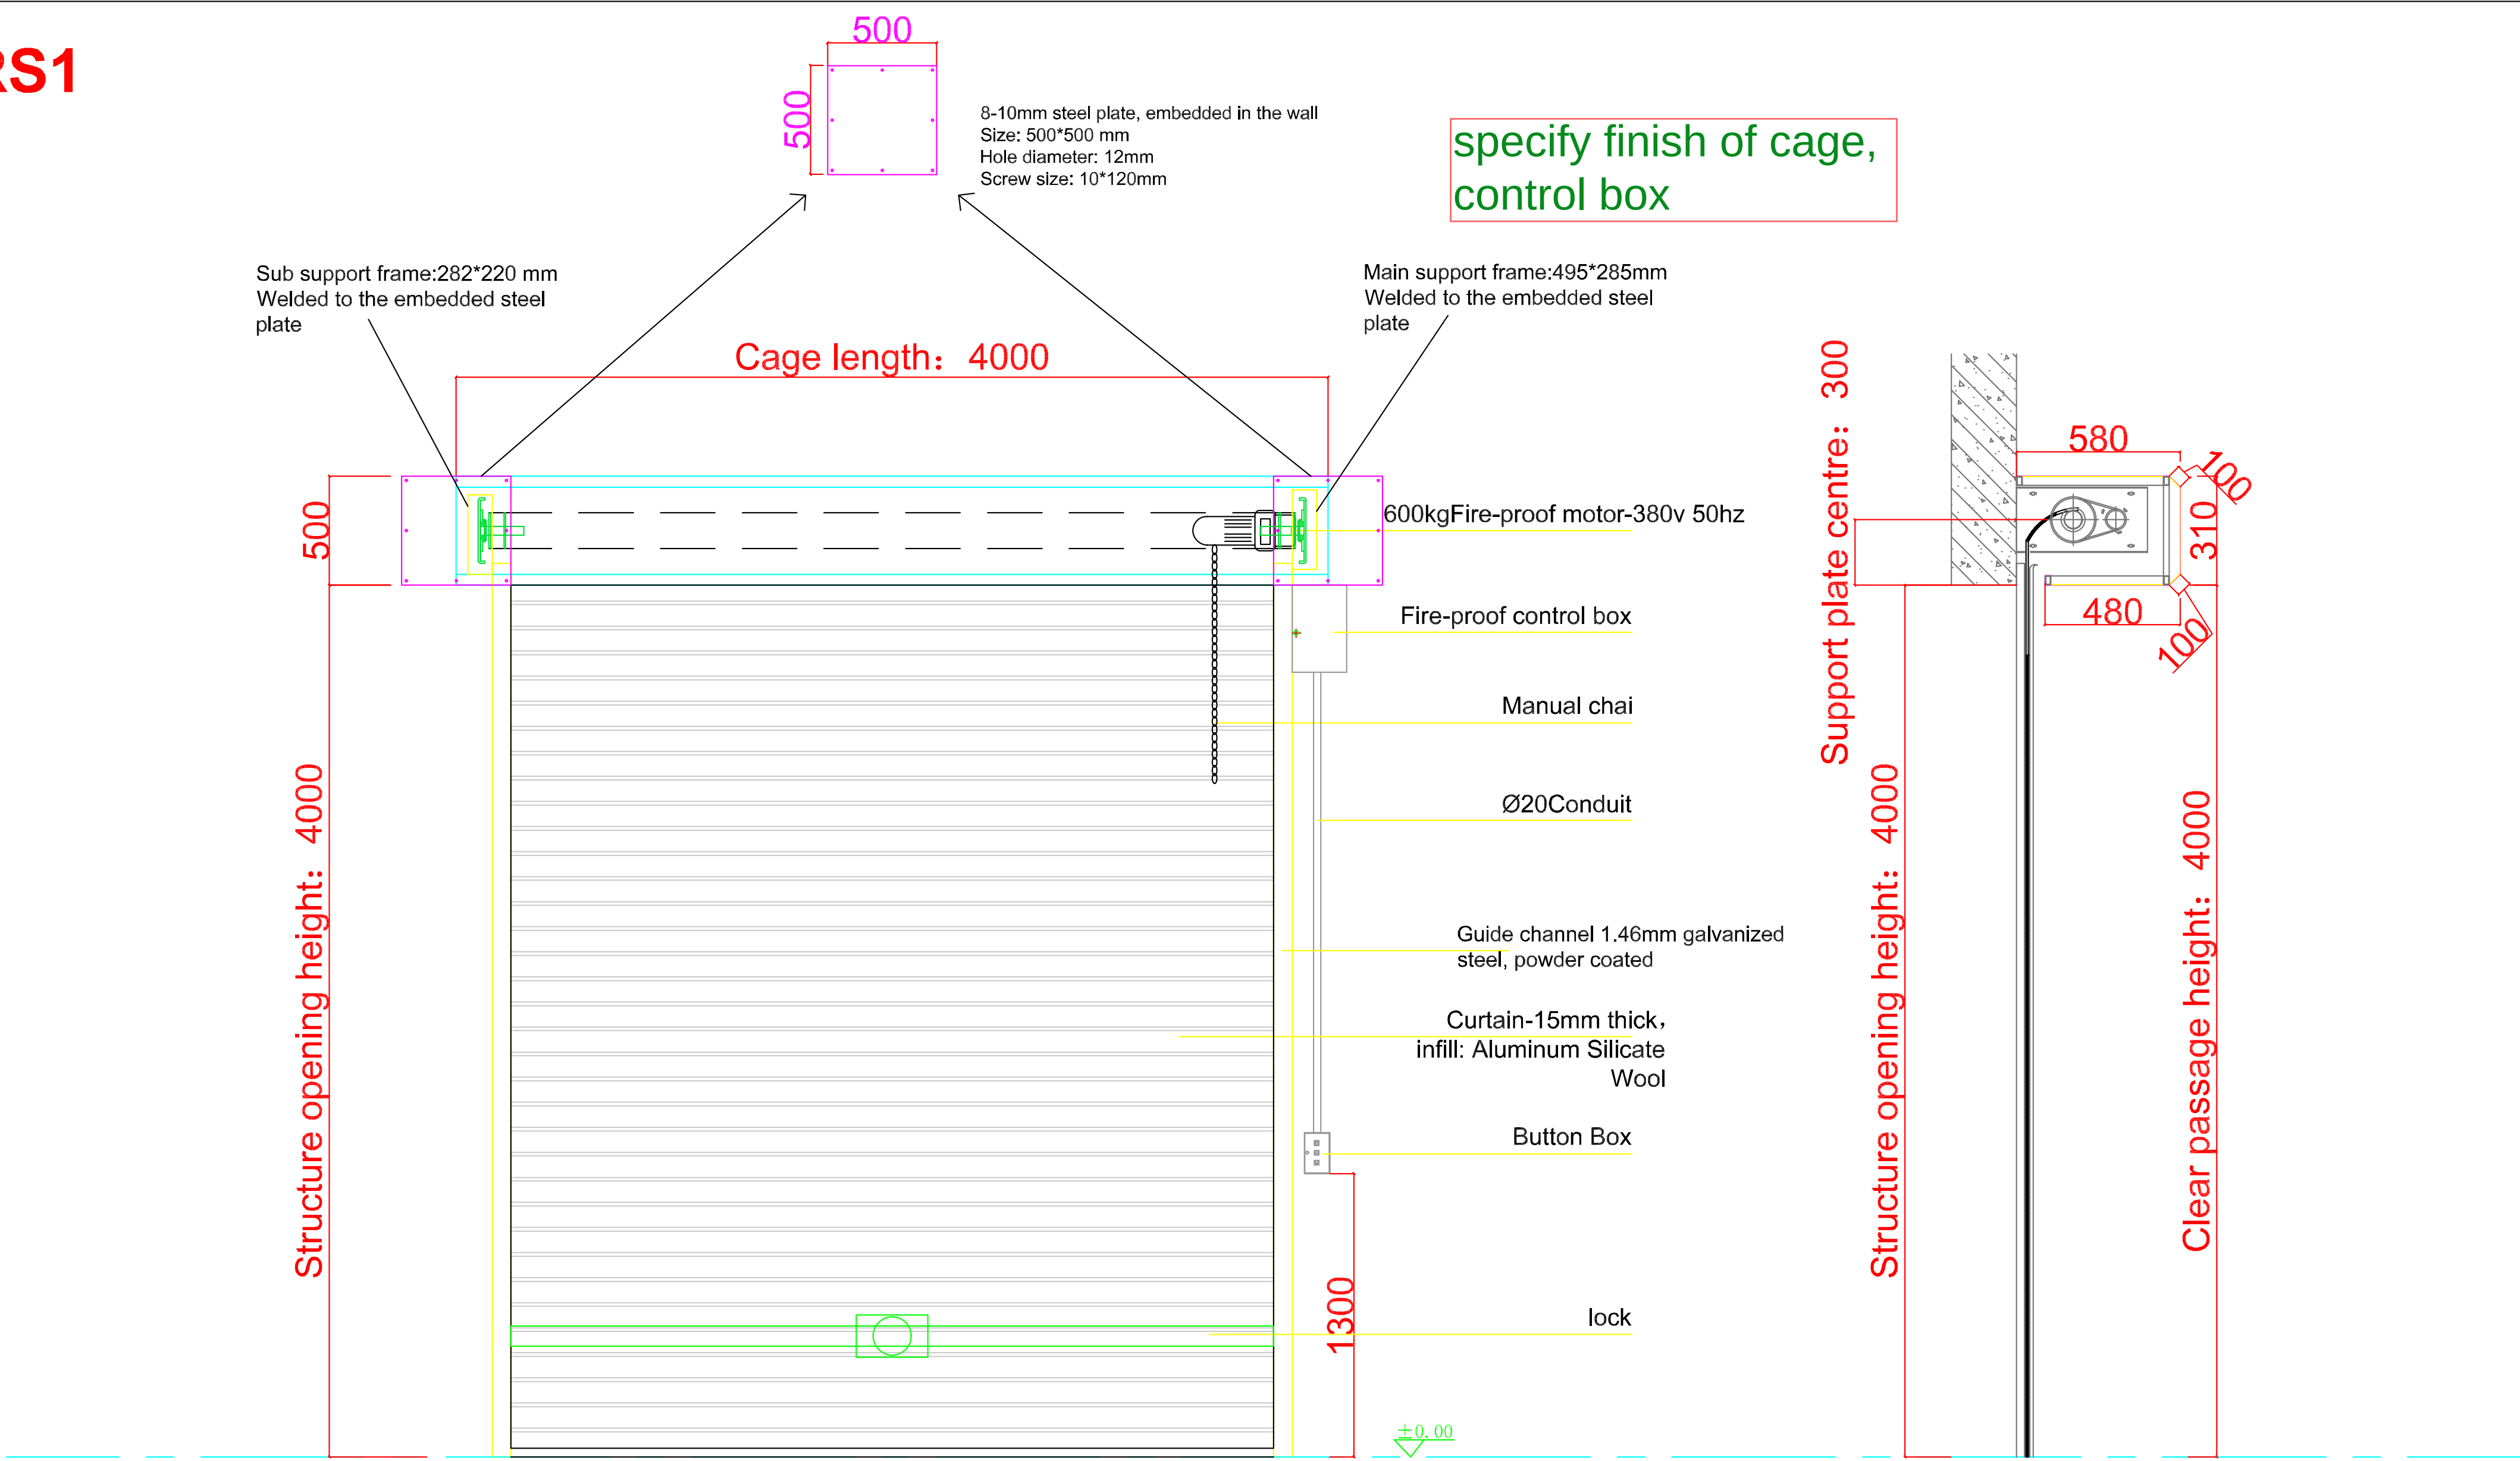

Bottom beam

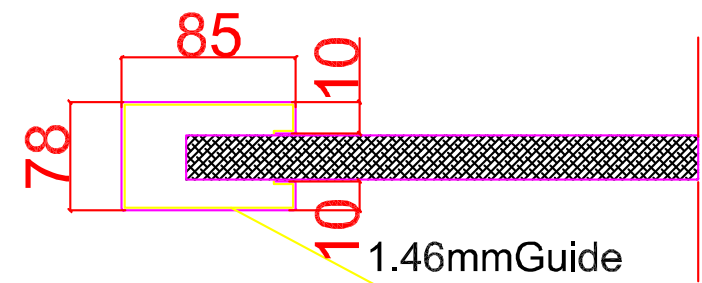


Guide

Hardware

Name	Description	Qty	Remarks
Motor	Fire-proof motor	1	
Control box	Fire-proof control box	1	
Support plate		1	
Button Box		1	
Access opening		1	
Guide	1.46mm Galvanized steel		
Cage	0.8mm Galvanized steel sheet		
Side Panel	0.8mm Galvanized steel sheet		
Baseplate	0.8mm Galvanized steel sheet		
Colour	RAL		



Heat resistant-open in high temperature: available
Fire alarm system: available
Fail safe: available

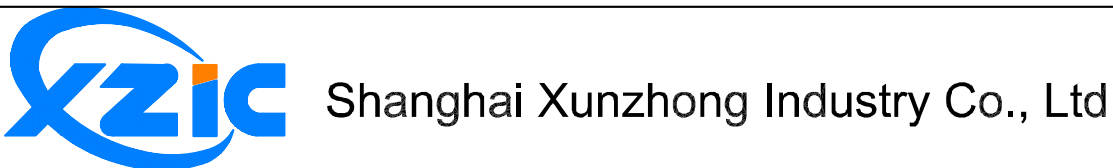

Project name

By		Drawing title	
Design		Size	
Check		Qty	3
Review		Opening direction	
Approval		Date	2026.05.18
		Page No	31
Total Page	34	Diagram number	

RS1

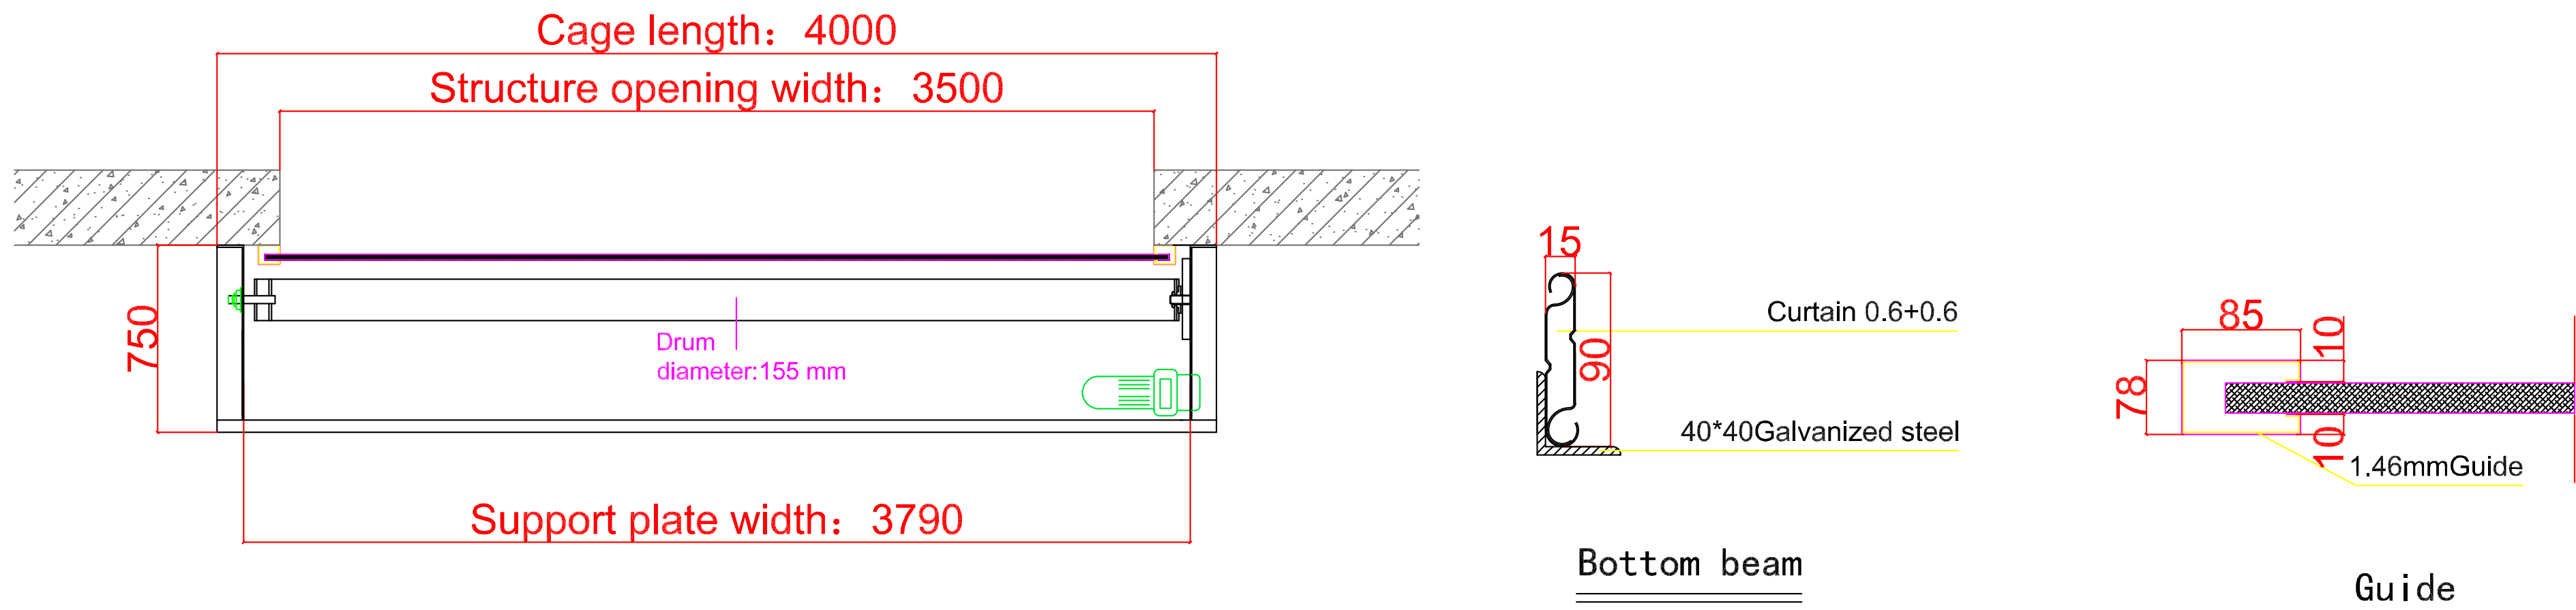
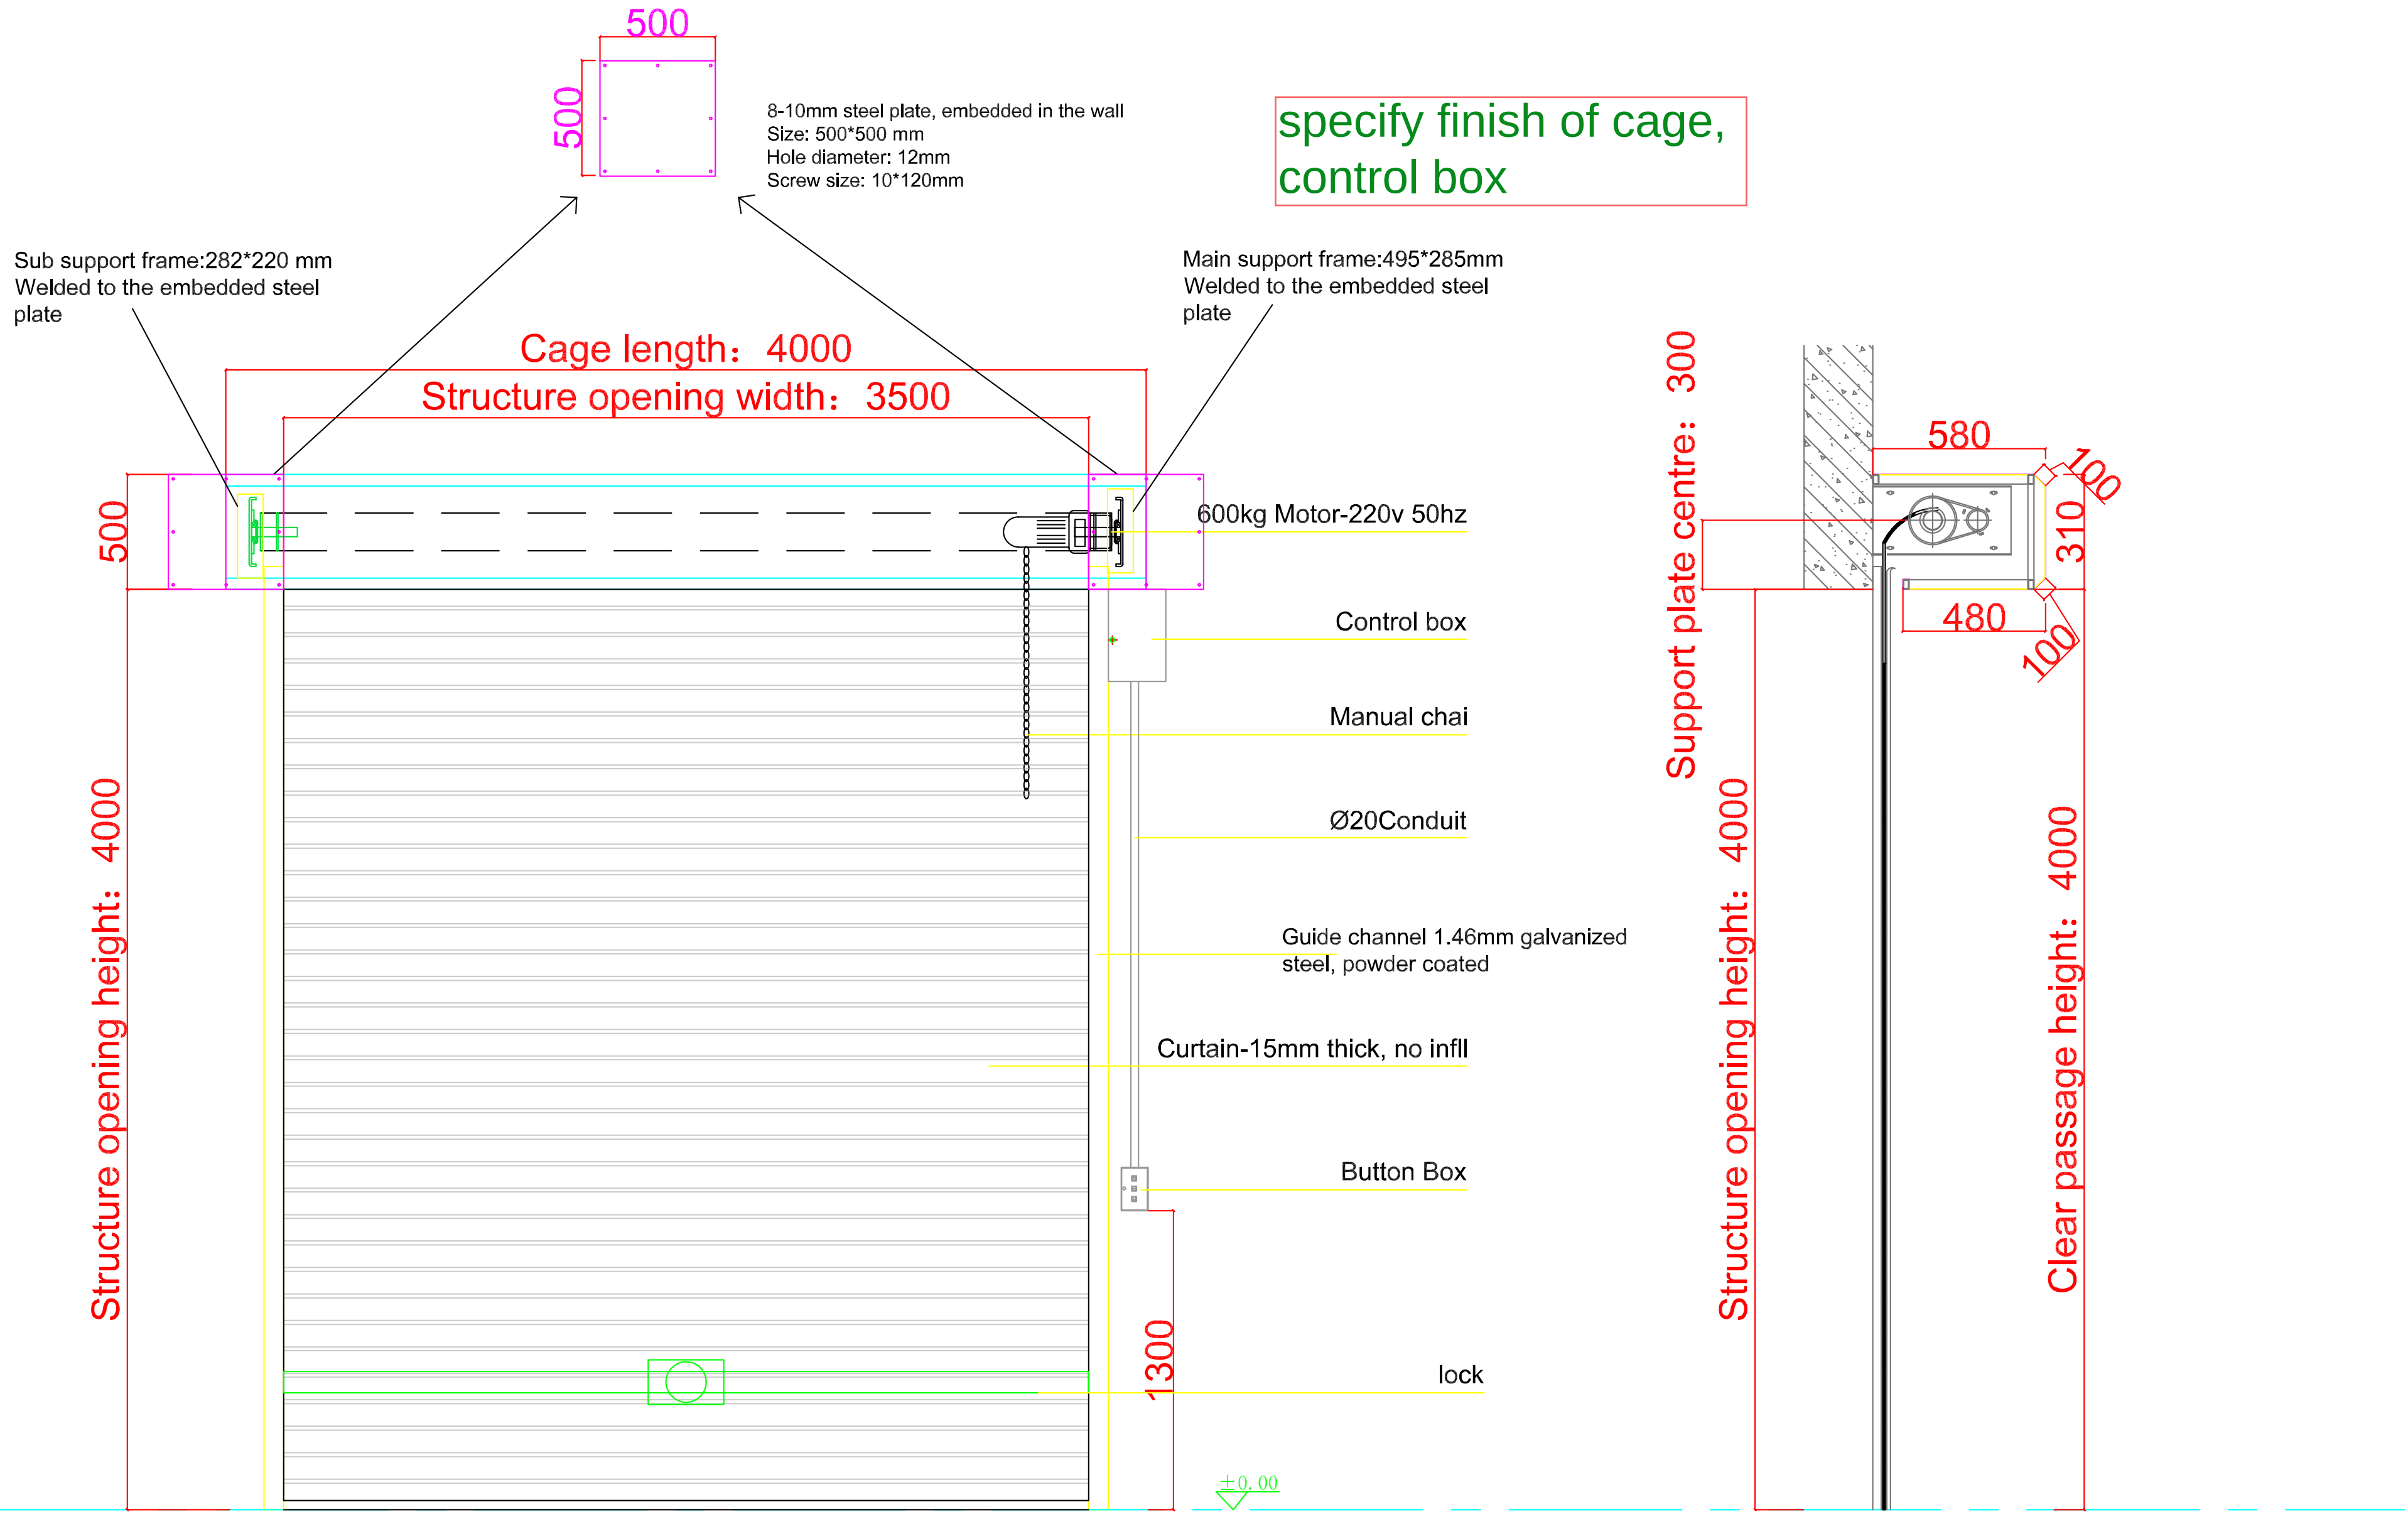


Hardware			
Name	Description	Qty	Remarks
Motor		1	
Control box		1	
Support plate		1	
Button Box		1	
Access opening		1	
Guide	1.46mm Galvanized steel		
Cage	0.8mm Galvanized steel sheet		
Side Panel	0.8mm Galvanized steel sheet		
Baseplate	0.8mm Galvanized steel sheet		
Colour	RAL		

Heat resistant-open in high temperature: available
Fire alarm system: available
Fail safe: available

 Shanghai Xunzhong Industry Co., Ltd			
Project name			
By		Drawing title	
Design		Size	
Check		Qty	11
Review		Opening direction	
Approval		Date	2026.05.18
		Page No	32
Total Page	34	Diagram number	

RS2



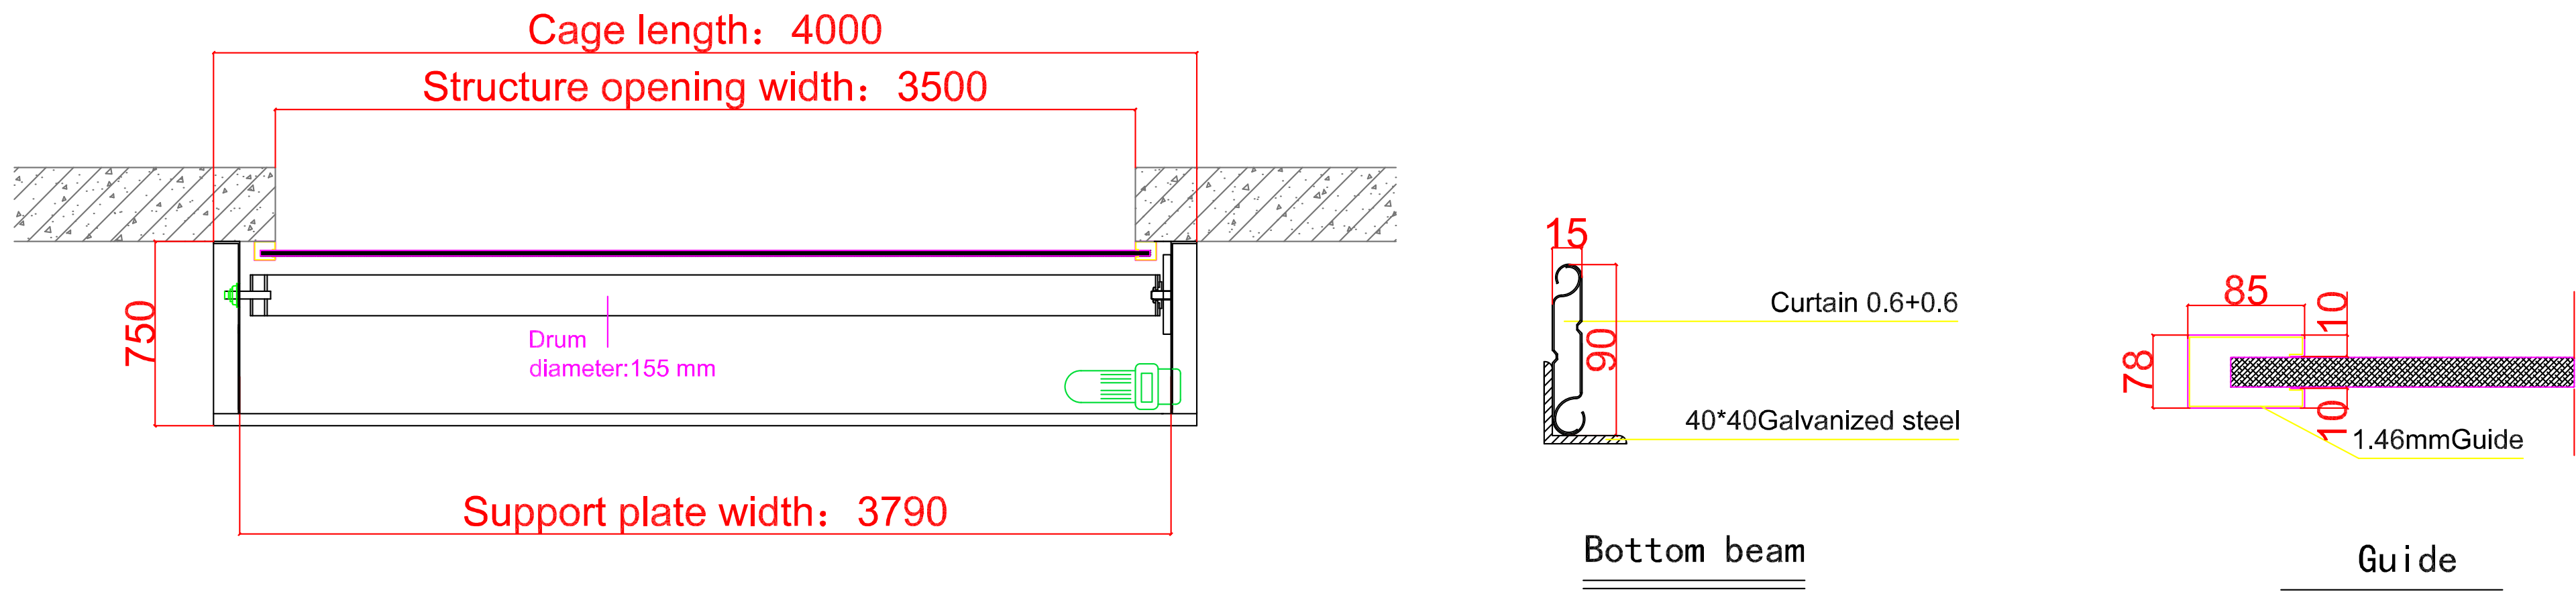
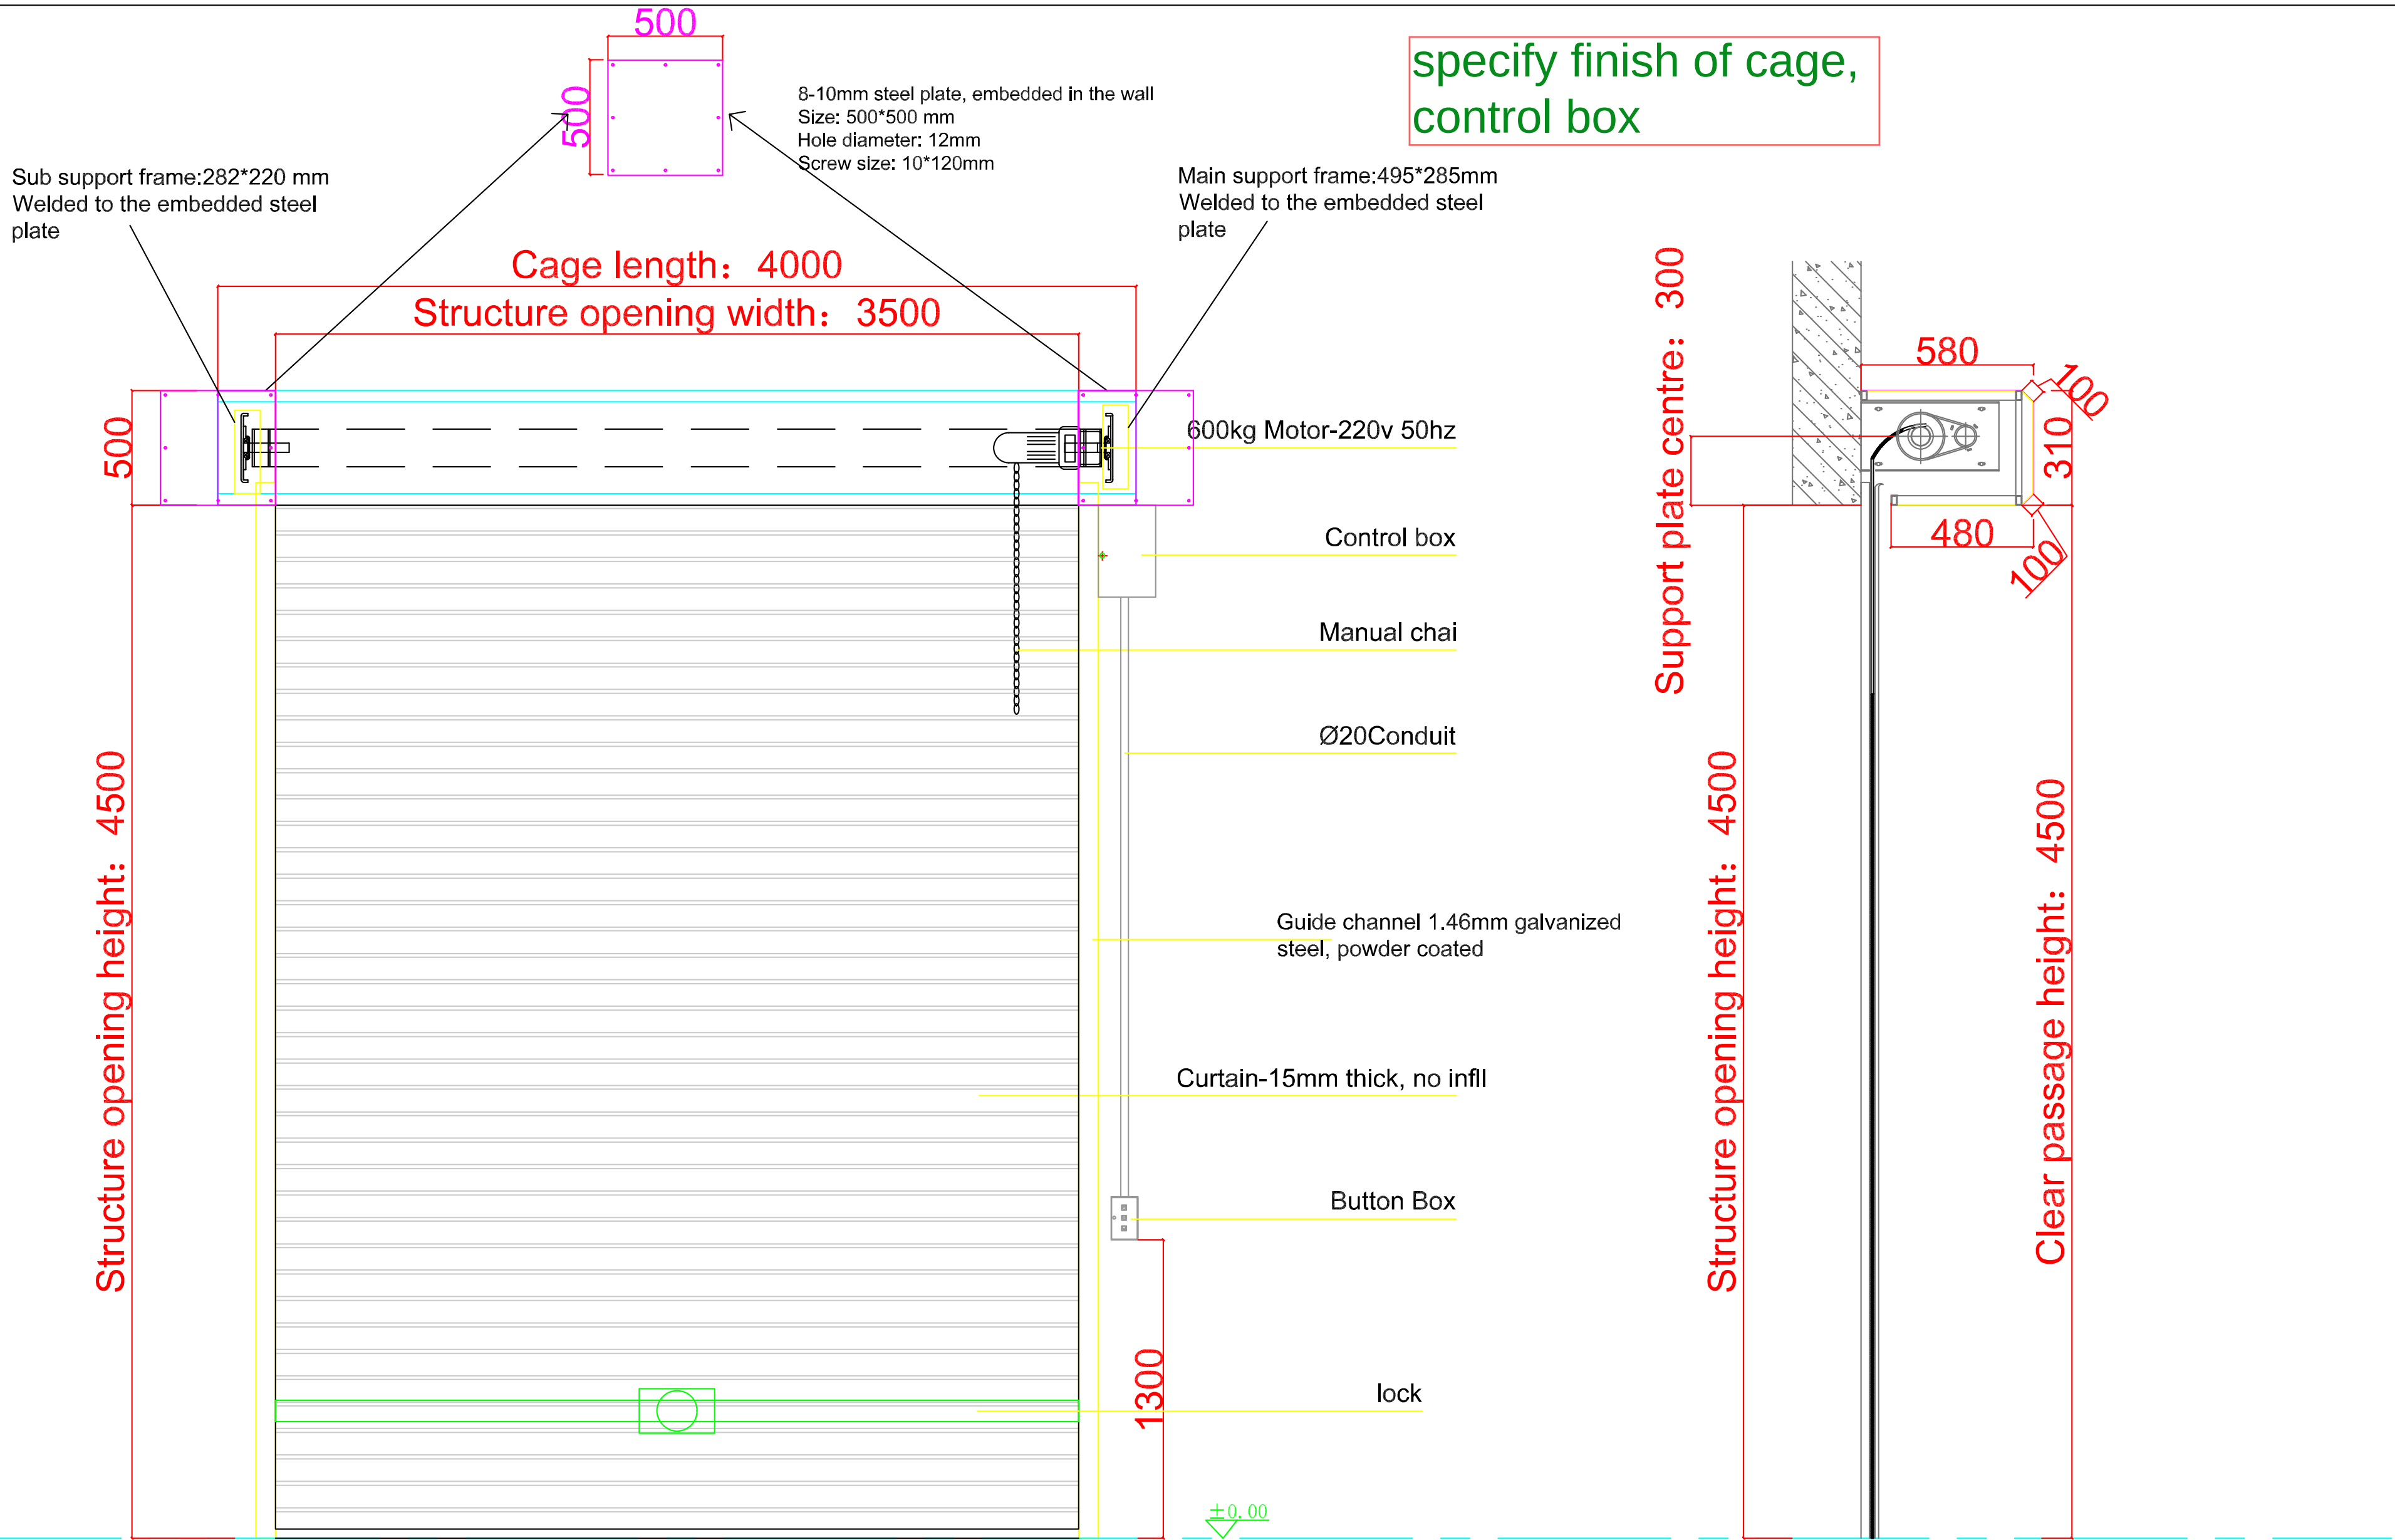


Hardware			
Name	Description	Qty	Remarks
Motor		1	
Control box		1	
Support plate		1	
Button Box		1	
Access opening		1	
Guide	1.46mm Galvanized steel		
Cage	0.8mm Galvanized steel sheet		
Side Panel	0.8mm Galvanized steel sheet		
Baseplate	0.8mm Galvanized steel sheet		
Colour	RAL		

Heat resistant-open in high temperature: available
Fire alarm system: available
Fail safe: available

 Shanghai Xunzhong Industry Co., Ltd			
Project name			
By		Drawing title	
Design		Size	
Check		Qty	9
Review		Opening direction	
Approval		Date	2026.05.18
		Page No	33
Total Page	34	Diagram number	

RS3

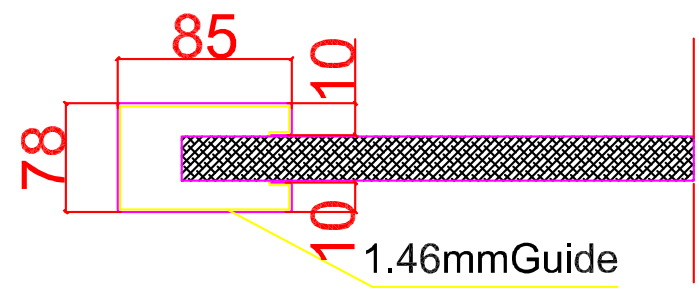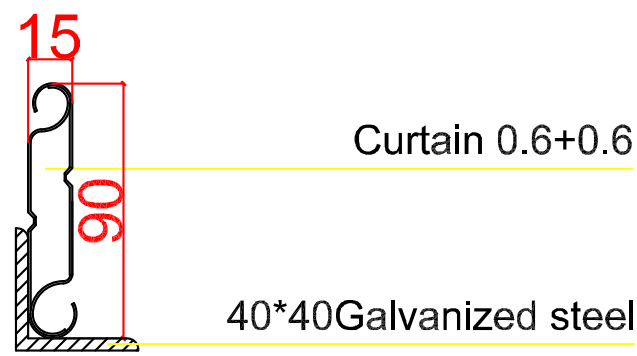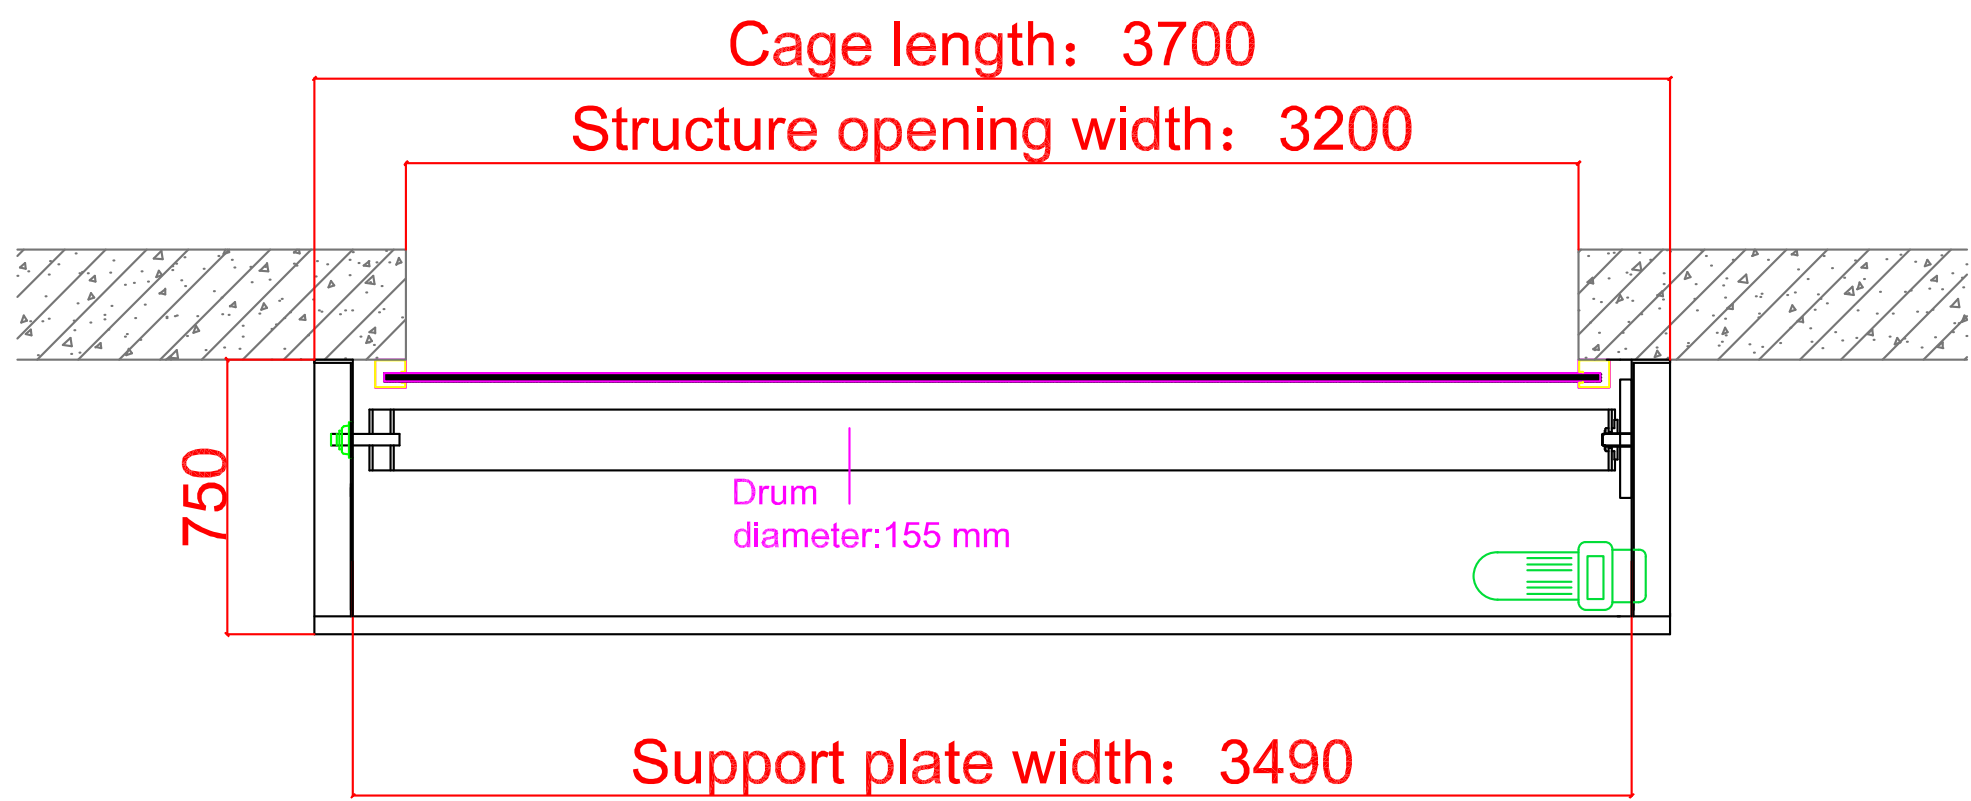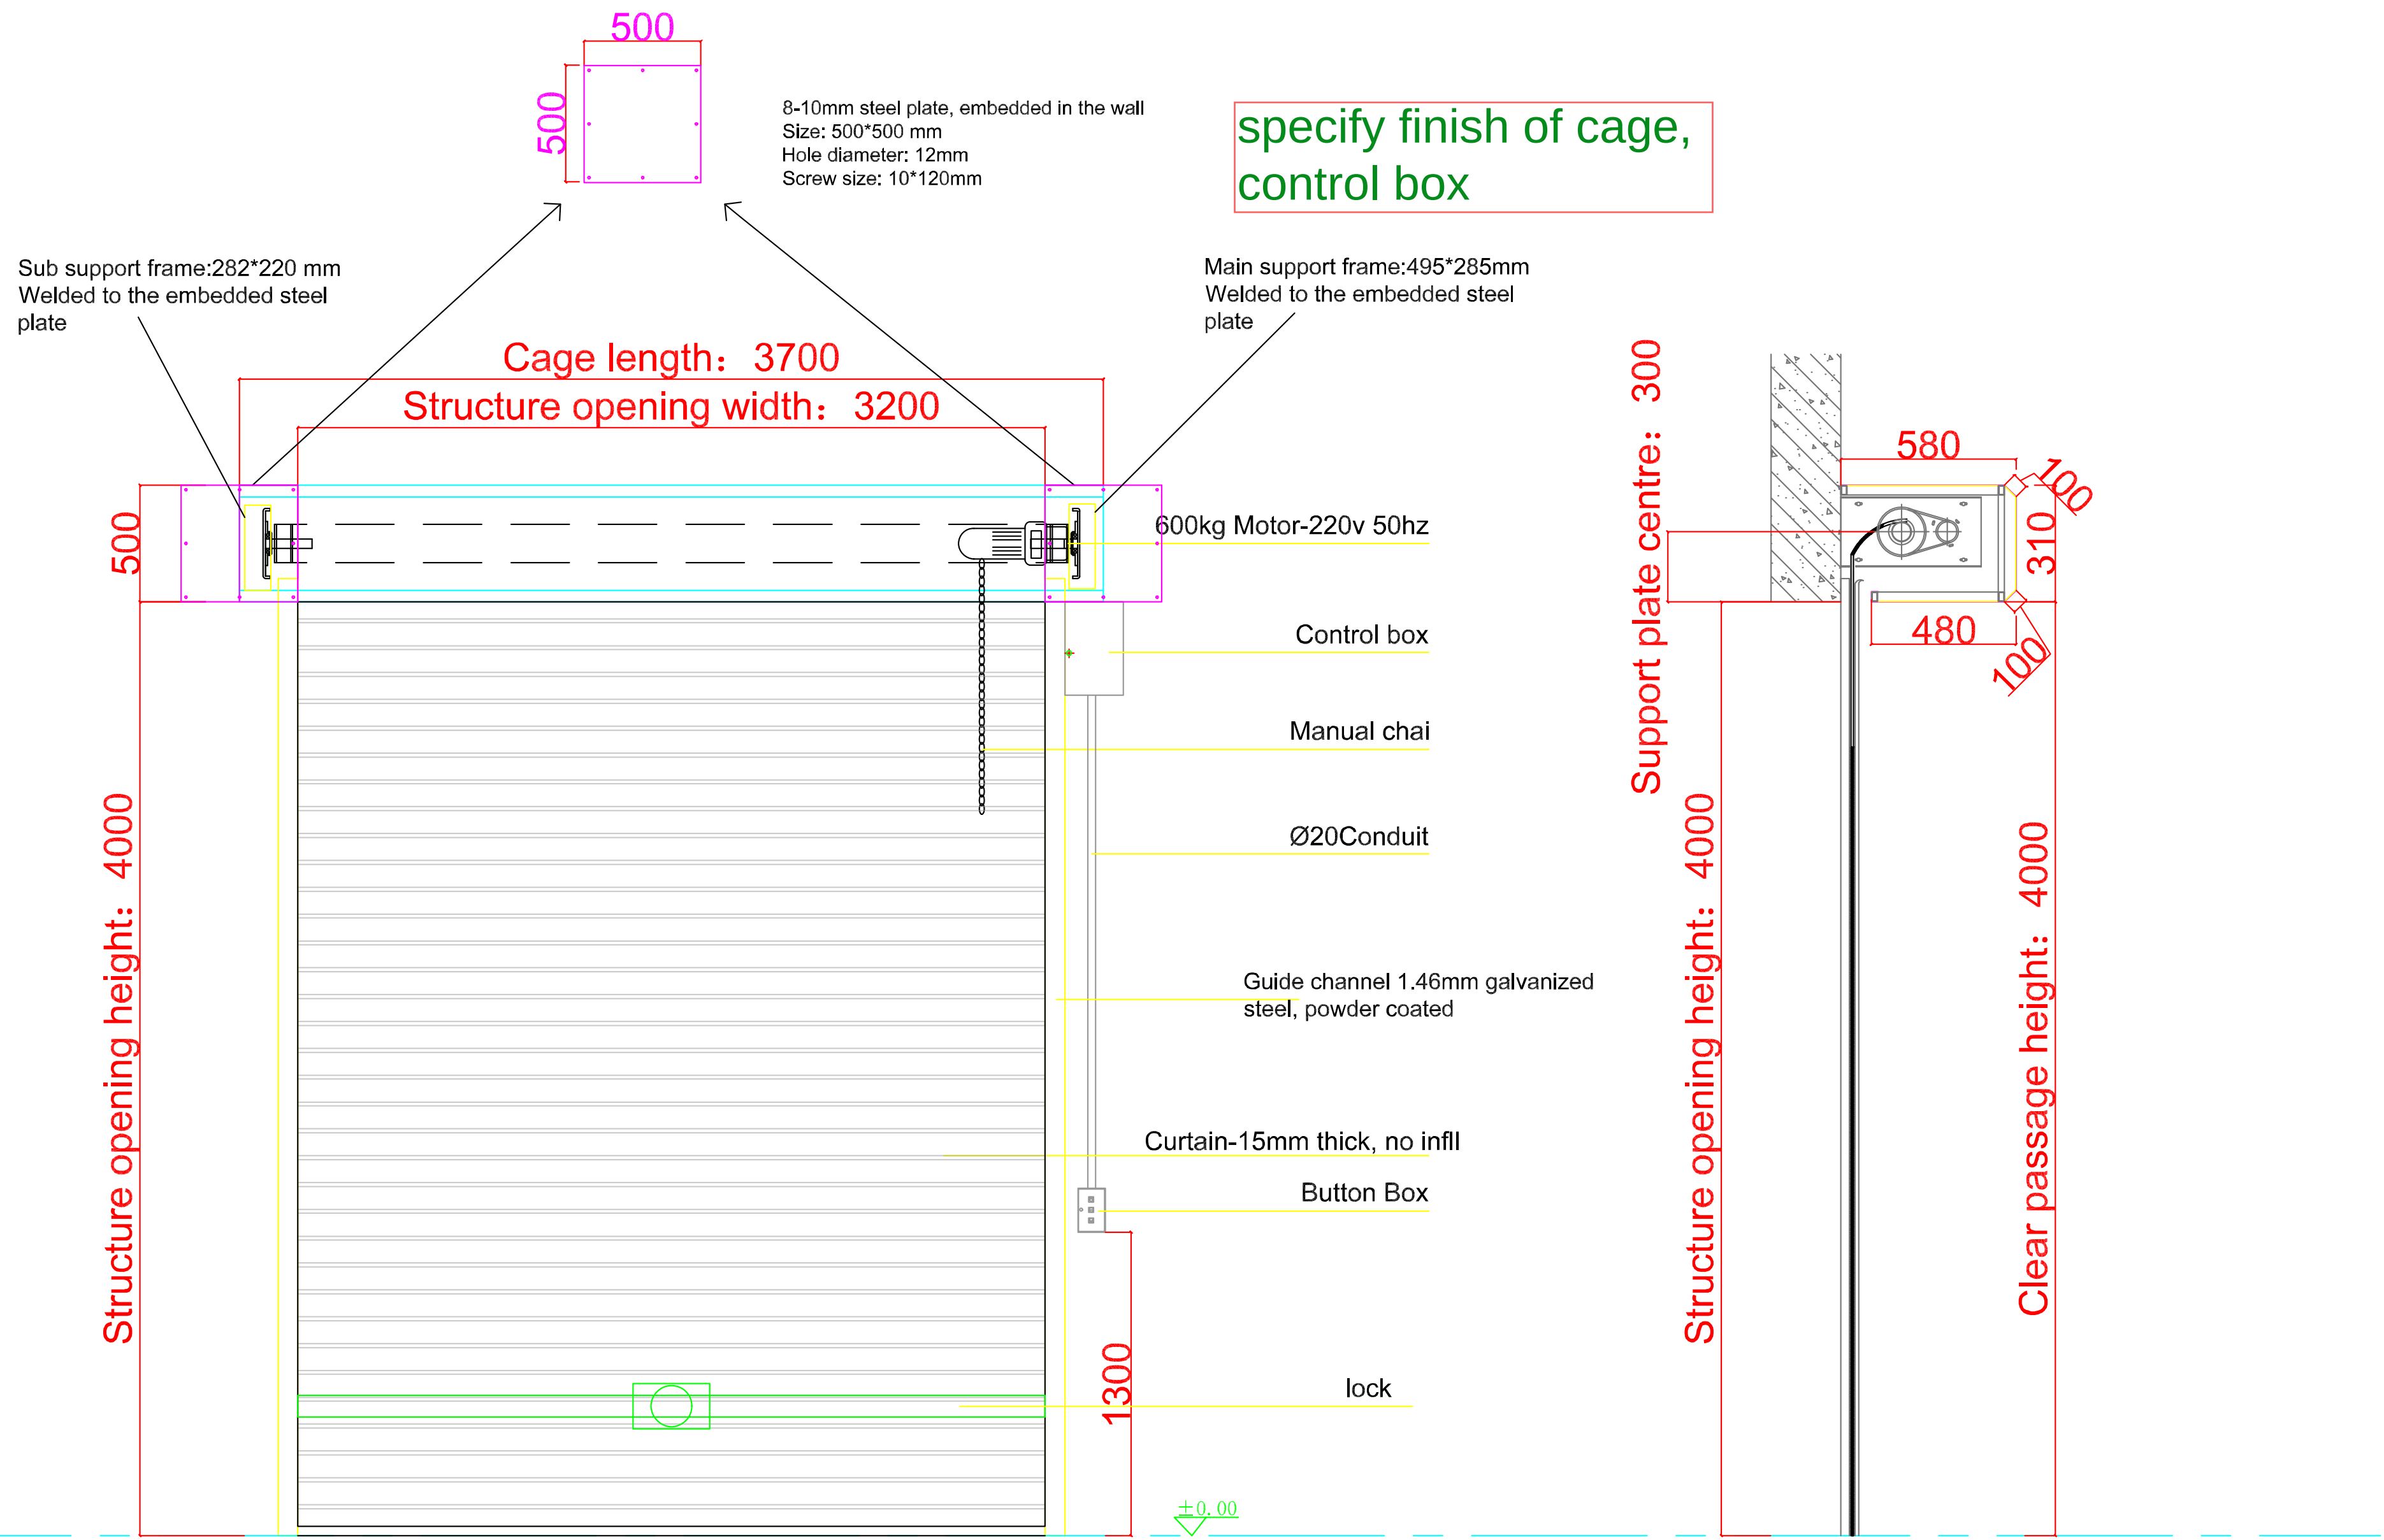

Bottom beam





Guide

Hardware			
Name	Description	Qty	Remarks
Motor		1	
Control box		1	
Support plate		1	
Button Box		1	
Access opening		1	
Guide	1.46mm Galvanized steel		
Cage	0.8mm Galvanized steel sheet		
Side Panel	0.8mm Galvanized steel sheet		
Baseplate	0.8mm Galvanized steel sheet		
Colour	RAL		

Heat resistant-open in high temperature: available
Fire alarm system: available
Fail safe: available

 Shanghai Xunzhong Industry Co., Ltd			
Project name			
By		Drawing title	
Design		Size	
Check		Qty	3
Review		Opening direction	
Approval		Date	2026.05.18
		Page No	34
Total Page	34	Diagram number	

RS4

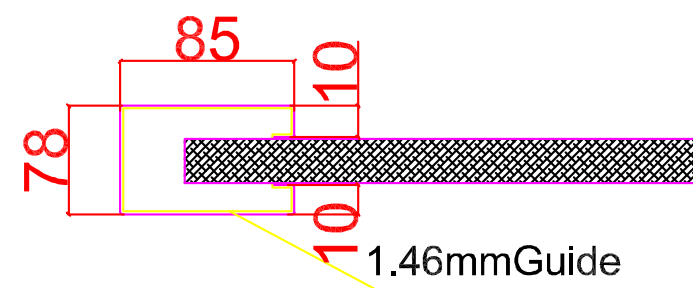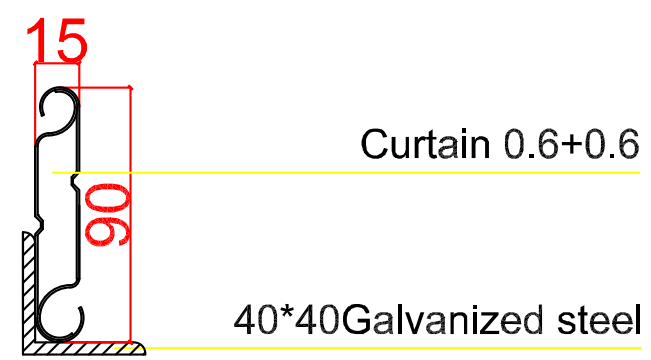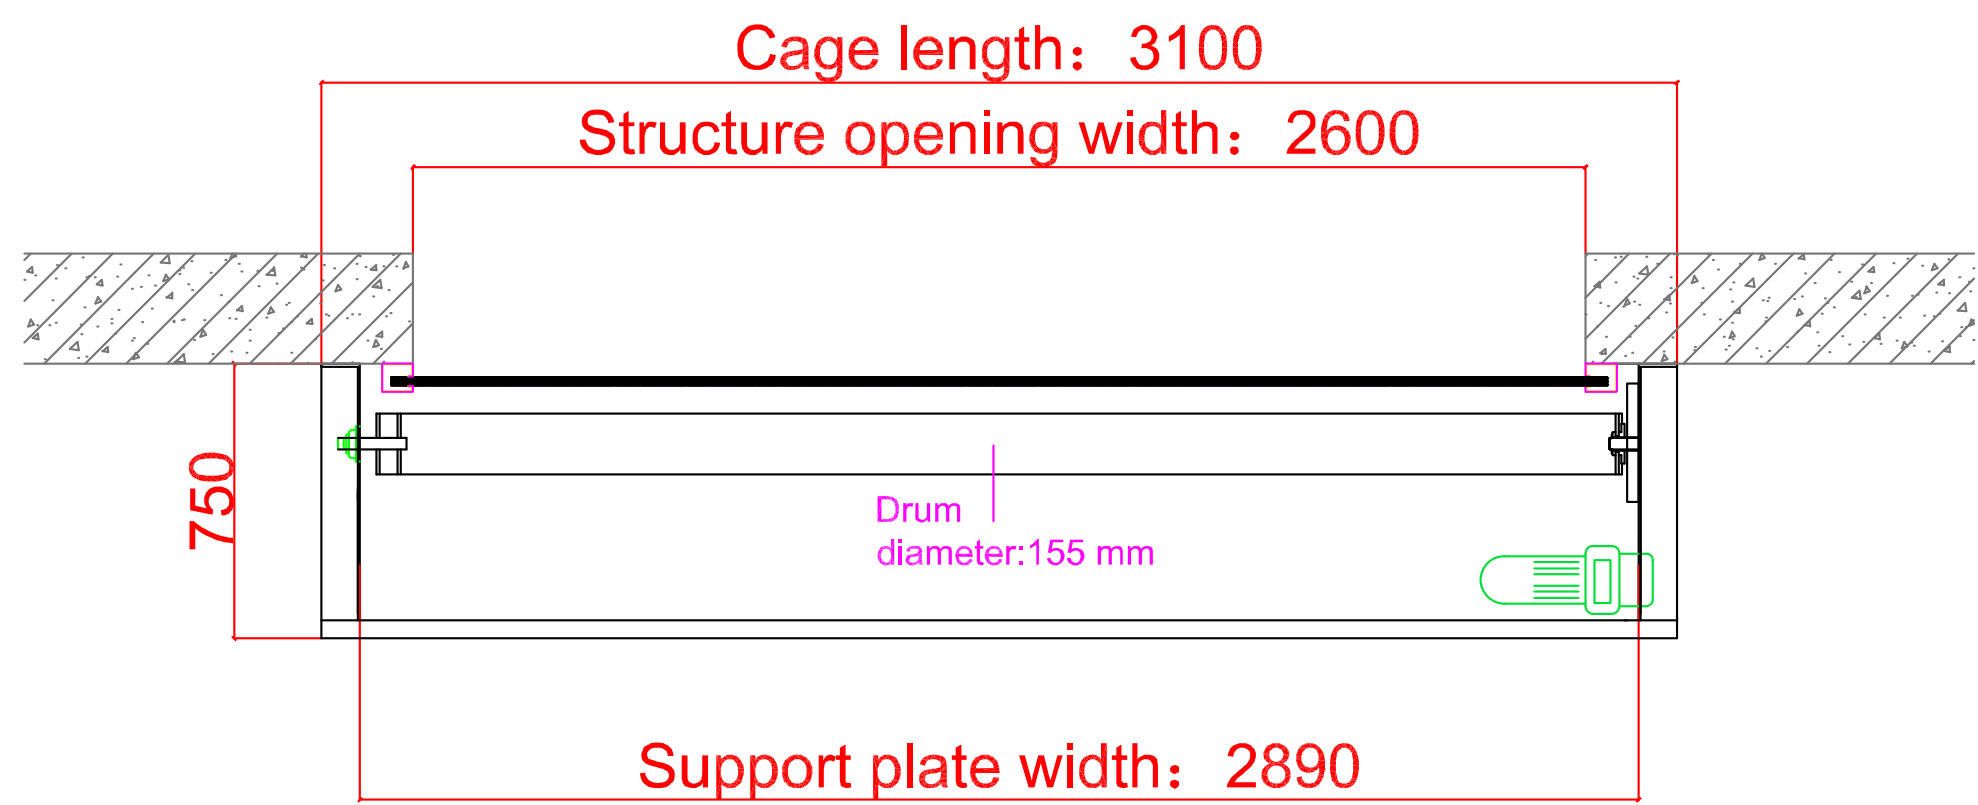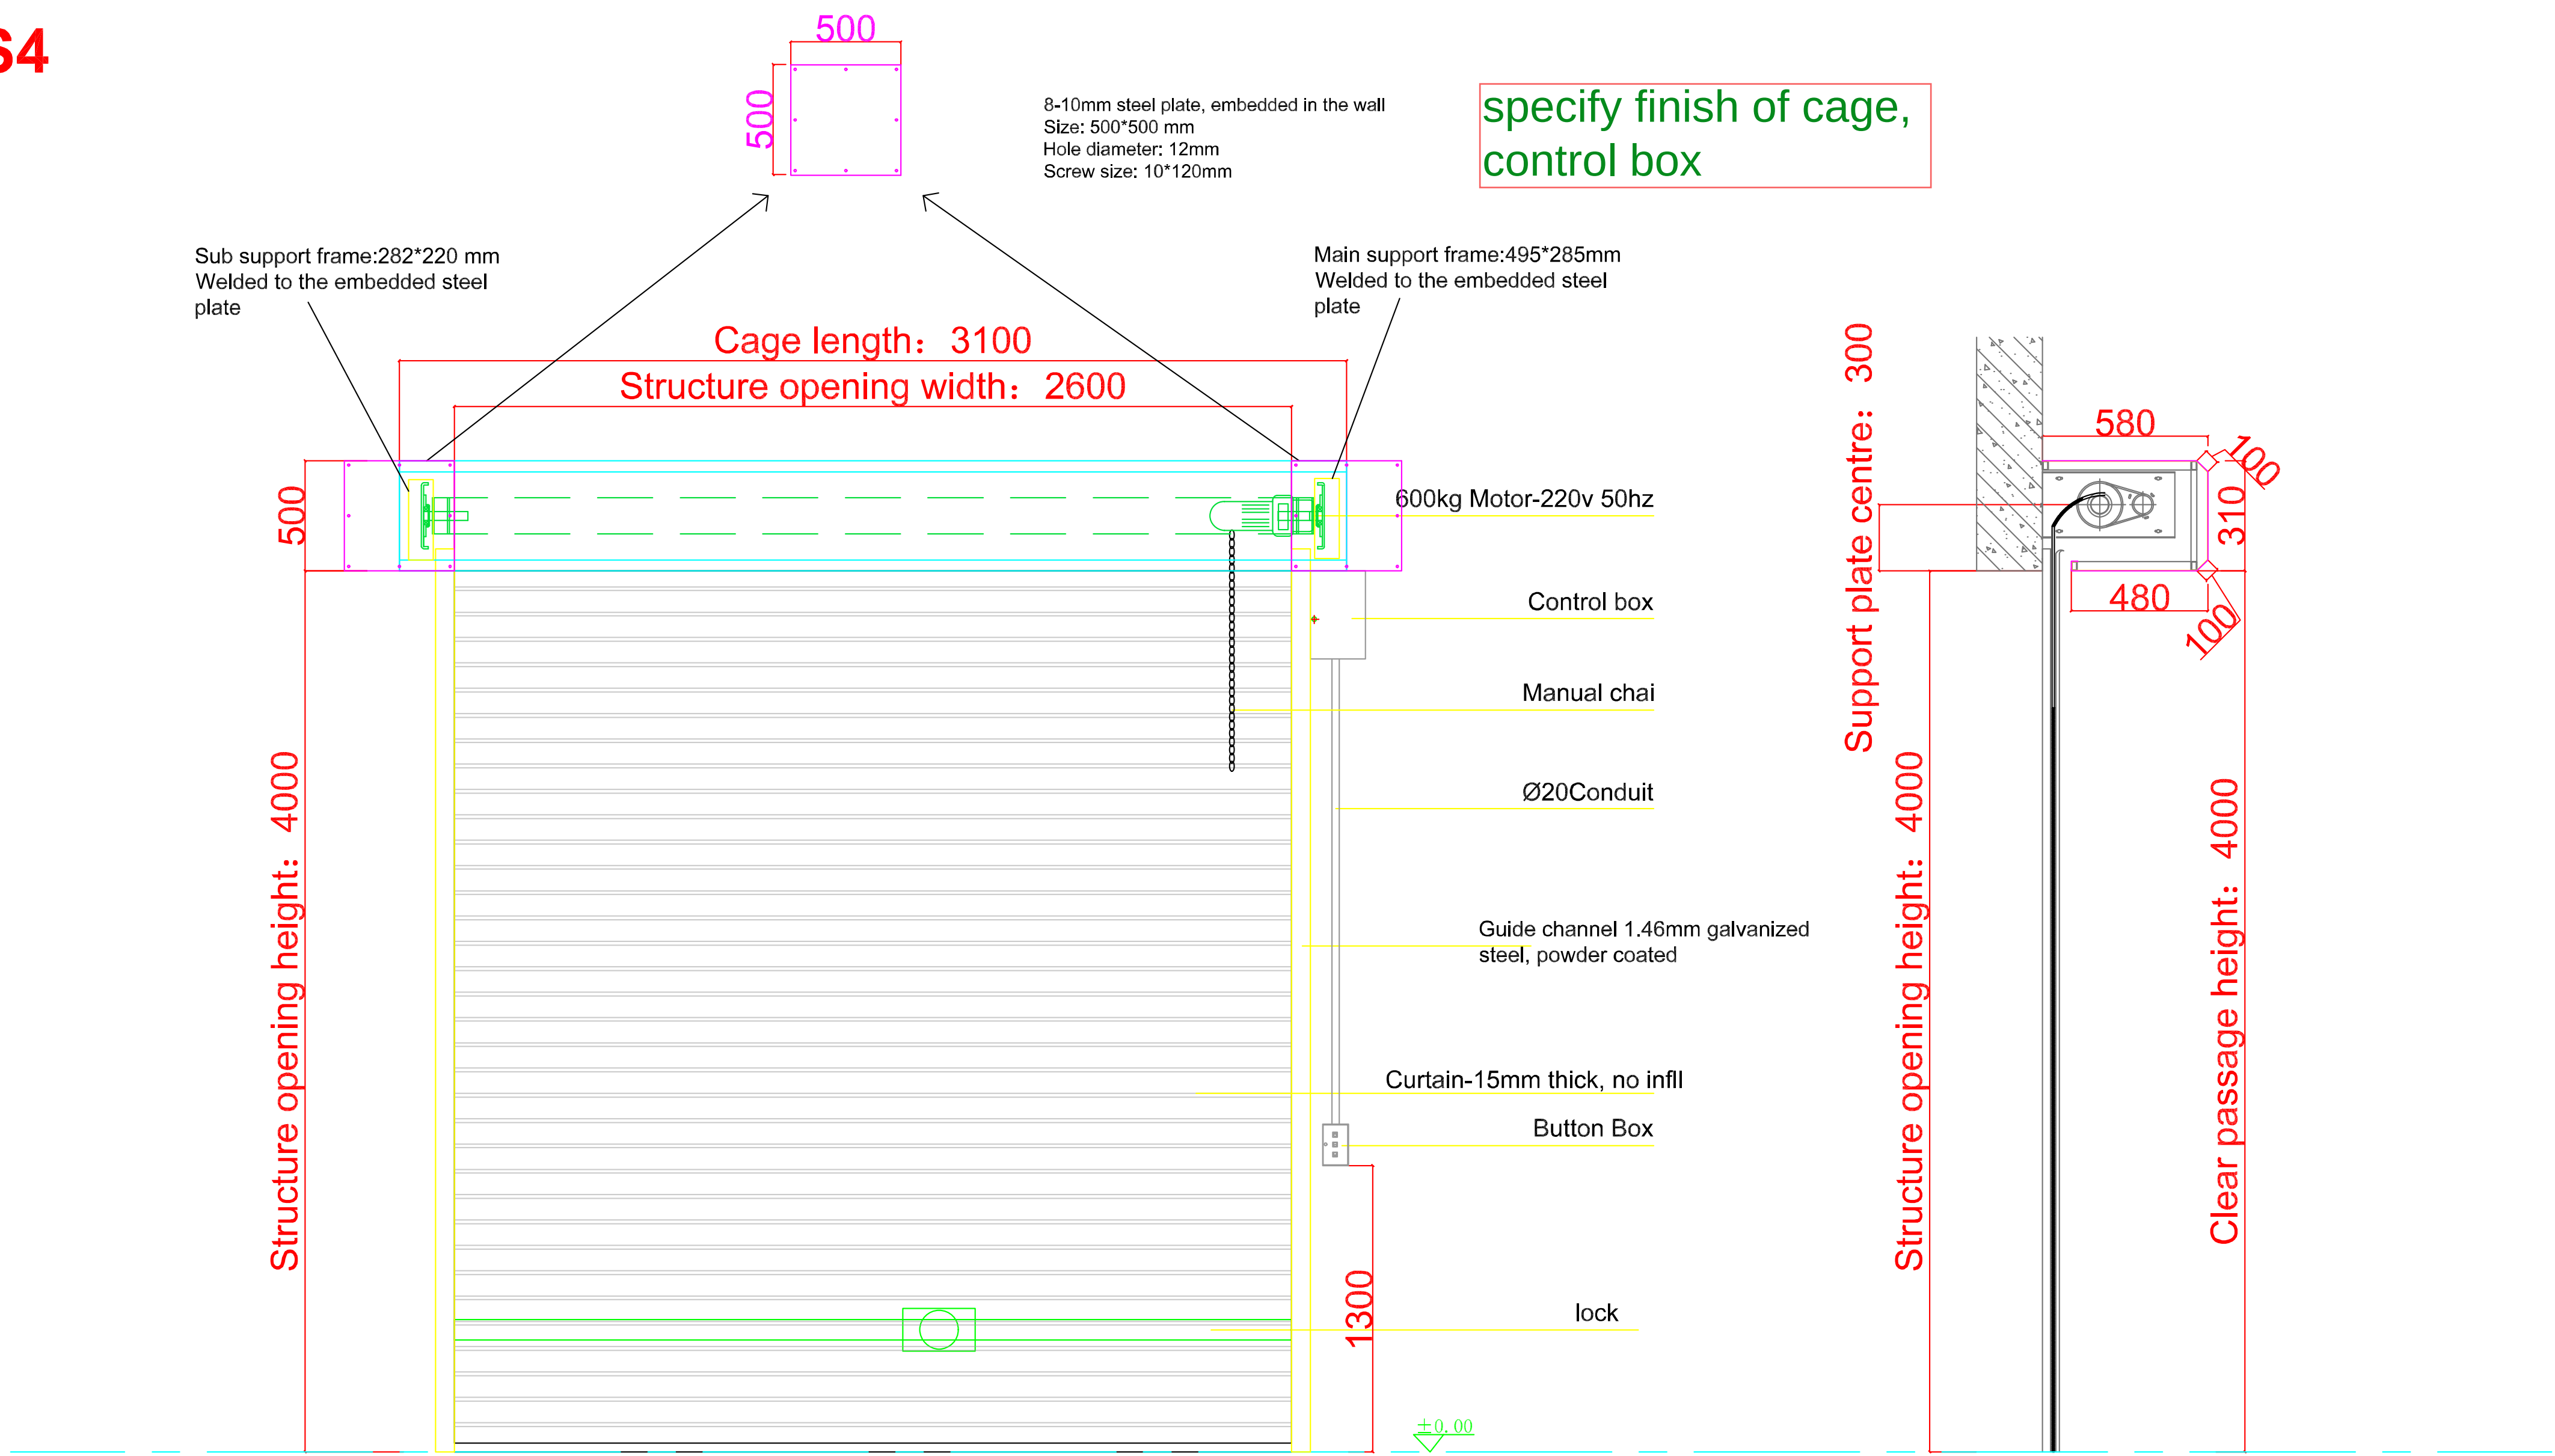

Hardware			
Name	Description	Qty	Remarks
Motor		1	
Control box		1	
Support plate		1	
Button Box		1	
Access opening		1	
Guide	1.46mm Galvanized steel		
Cage	0.8mm Galvanized steel sheet		
Side Panel	0.8mm Galvanized steel sheet		
Baseplate	0.8mm Galvanized steel sheet		
Colour	RAL		

Heat resistent-open in high temperature: available
Fire alarm system: available
Fail safe: available

 Shanghai Xunzhong Industry Co., Ltd			
Project name			
By		Drawing title	
Design		Size	
Check		Qty	2
Review		Opening direction	
Approval		Date	2026.05.18
		Page No	34
Total Page	34	Diagram number	